



NN — 18×42 cm, L = 2,90 m, C25/30

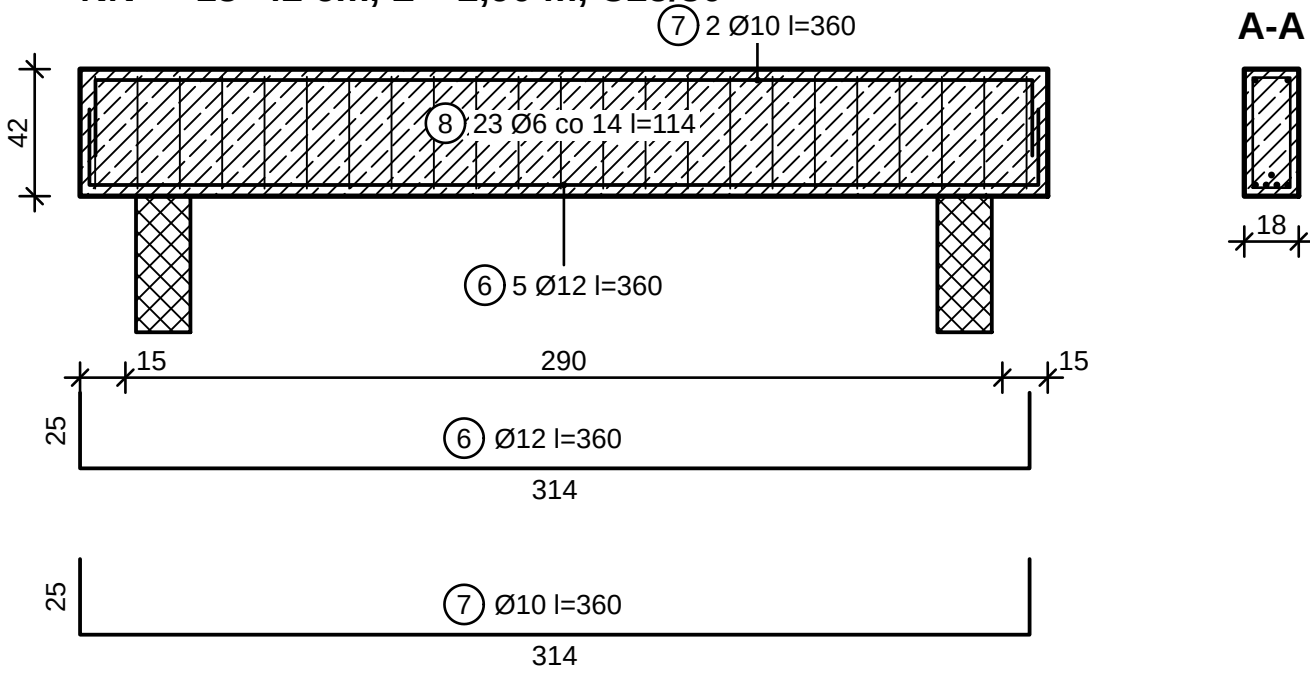


OBJAŚNIENIA I UWAGI

- Wymiary w cm (mm w indeksie górnym, np. 24^s = 24,5 cm), rzędne w m względem ±0,000 = 101.650 m n.p.m. (PL-EVRF2007-NH).
- Belki: pręty dolne i górne z odgięciami 90° w strefach podporowych (zakotwienie ≥ l_{bd} od lica podpory — PN-EN 1992-1-1 9.2.1.4), strzemiona zamknięte z hakami 135° (8.5, rys. 8.5), pierwsze strzemie 5 cm od lica podpory; rozstaw wg obliczeń (6.2.3), s ≤ min(0,75·d; 400 mm) (9.6N).
- Przekrój A-A — w środku rozpiętości; długości prętów l — długości rozwinięcia (wymiarzy zewnętrzne, odliczenie gięcia wg PN-EN ISO 3766).
- Betonowanie: beton wg PN-EN 206+A2 i PN-B-06265 (klasa, ekspozycja, D_{max} 16 mm, konsystencja S3); pielęgnacja ≥ 7 dni (klasa pielęgnacji 2 — PN-EN 13670 p. 8.5); przerwy robocze wyłącznie w miejscach uzgodnionych z projektantem.
- Rozszalowanie i usunięcie podpór: płyty i belki po uzyskaniu ≥ 70 % f_{ck} (PN-EN 13670 p. 5.6 i 8.5), wsporniki — nie wcześniej niż po 28 dniach i po wykonaniu elementów dociążających zaplecze; podpory wtórne do 28 dni.
- Nadproża pogrupowano w typy (jednakowy przekrój, długość i zbrojenie z obliczeń); liczby sztuk w zestawieniu — łącznie dla wszystkich nadproży typu.
- Rysunek wygenerowany automatycznie z modelu model/budynek.yaml (wersja 1.0, 2026-09-25) — generatory lamela.views.


NK — 18×25 cm, L = 1,90 m, C25/30

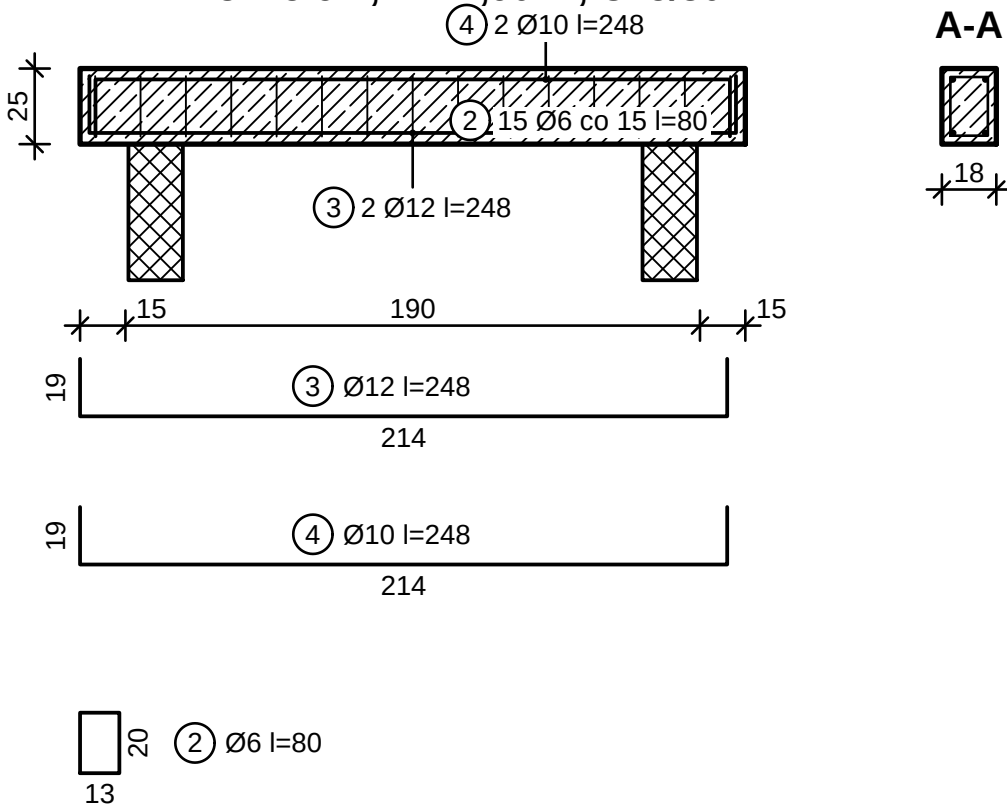


NM — 18×25 cm, L = 2,30 m, C25/30

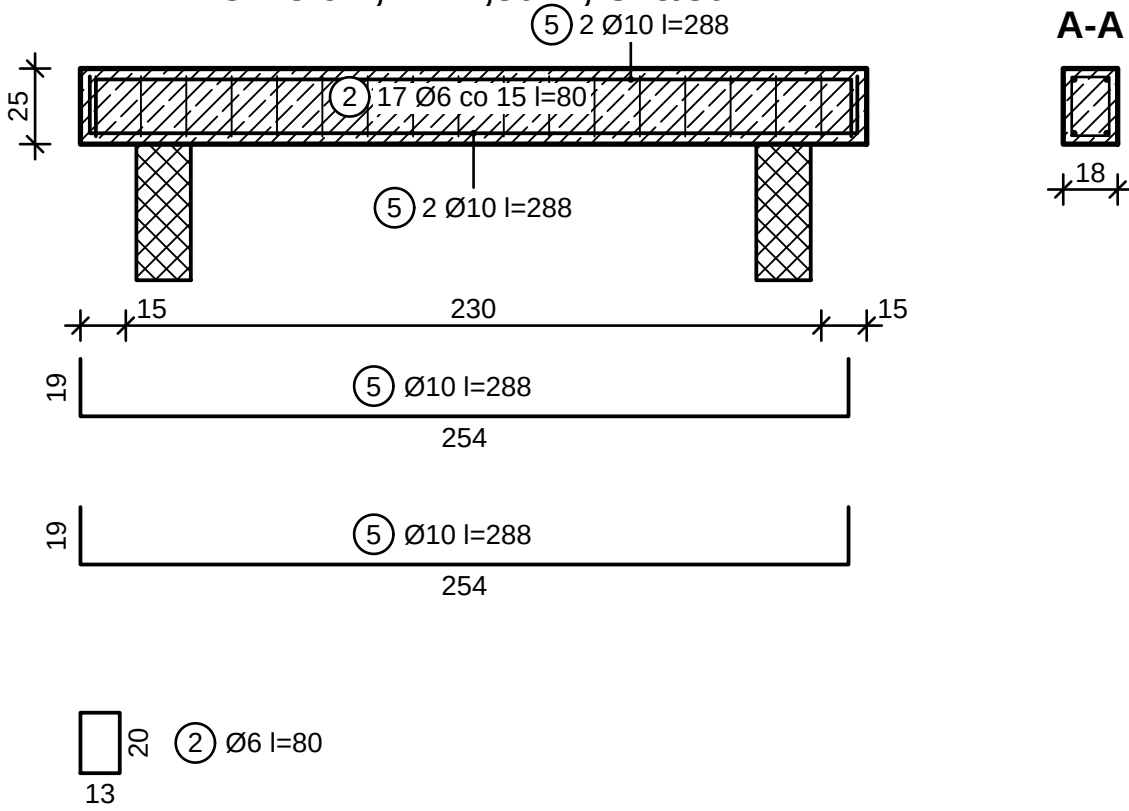

NJ — 18×25 cm, L = 1,60 m, C25/30

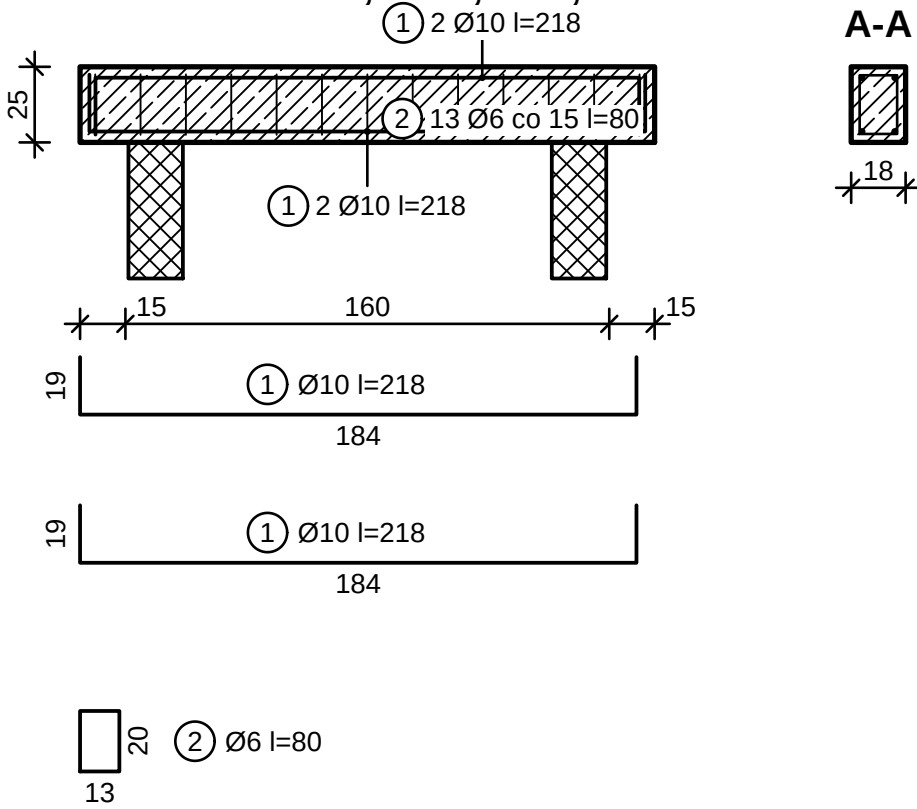

NL — 18×25 cm, L = 1,90 m, C25/30

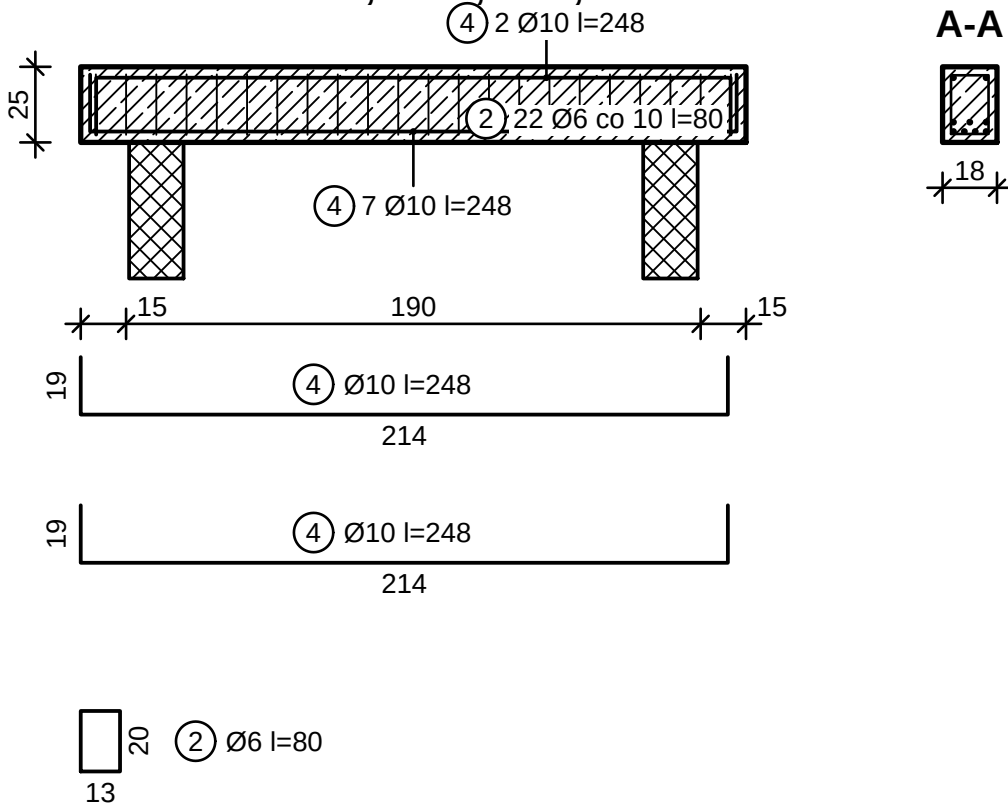

ZBROJENIE NADPROŻY NJ, NK, NL, NM, NN 1:25


TYPY NADPROŻY — OTWORY I POZYCJE OBLICZEŃ

Typ	Otwory	Poz. obl.	Szt.
NJ	O1-04	6.17	1
NK	O1-02	6.15	1
NL	O0-18	6.11	1
NM	O0-12	6.6	1
NN	O0-11	6.5	1

ZESTAWIENIE STALI

Poz.	Ø [mm]	Kształt ISO 3766, wymiary [cm]	Dług. [cm]	Liczba [szt.]	Elem.	Ø6 [m]	Ø10 [m]	Ø12 [m]
1	10	21: a=19 b=184 c=19	218	4	N-O1-0		8,72	
2	6	51: a=13 b=20	80	70	N-O1-0	56,00		
3	12	21: a=19 b=214 c=19	248	2	N-O1-0			4,96
4	10	21: a=19 b=214 c=19	248	11	N-O1-0		27,28	
5	10	21: a=19 b=254 c=19	288	4	N-O0-1		11,52	
6	12	21: a=25 b=314 c=25	360	5	N-O0-1			18,00
7	10	21: a=25 b=314 c=25	360	2	N-O0-1		7,20	
8	6	51: a=13 b=37	114	24	N-O0-1	27,36		
		Długość całkowita [m]				83,4	54,7	23,0
		Masa jednostkowa [kg/m]				0,222	0,617	0,888
		Masa [kg]				18,5	33,7	20,4
		RAZEM stal B500SP [kg]						72,6

O1-04, O1-02, O0-18, O0-12, O0-11: beton C25/30, XC1, otulina strzemion c_{nom} = 25 mm (tabl. 4.4N + NA).

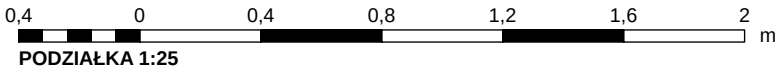

REW.	OPIS ZMIANY	DATA				
0	Wydanie — rysunek wygenerowany z modelu	2026-09-25				
PRACOWNIA PROJEKTOWA PRACOWNIA PROJEKTOWA — nazwa do uzupełnienia adres pracowni do uzupełnienia		STADIUM PT	BRANŻA KONSTRUKCJA (BO)			
INWESTOR (do uzupełnienia)						
OBIEKT / NAZWA ZAMIERZENIA BUDOWLANEGO Budynek mieszkalny jednorodzinny wolnostojący „Dom LAMELA”						
ADRES / LOKALIZACJA (NR DZIAŁKI, OBRĘB, JEDN. EWIDENCYJNA) ul. Lipowa (fikcyjna), dz. nr ewid. 123/4, obręb 0005 Przykładowo, gm. Przykładowo (fikcyjna)			KAT. OBIEKTU I			
FUNKCJA	IMIĘ I NAZWISKO	SPECJALNOŚĆ, NR UPRAWNIENI	DATA	PODPIS		
Projektant	[DO UZUPEŁNIENIA]	[DO UZUPEŁNIENIA]				
Projektant (wsp.)	[DO UZUPEŁNIENIA]	[DO UZUPEŁNIENIA]				
Sprawdzający	nie dotyczy (art. 20 ust. 3 pkt 2 PB)	—				
Opracował	[DO UZUPEŁNIENIA]	[DO UZUPEŁNIENIA]				
TYTUŁ RYSUNKU ZBROJENIE NADPROŻY (3)						
SKALA 1:25	FORMAT 400×594	DATA WYDANIA 2026-09-25	RODZAJ DOK. rysunek zbrojenia	NR RYSUNKU PT-BO-25	ARKUSZ 25/27	REW. 0