


odcinek kontroli 100 mm (wydruk 1:1)

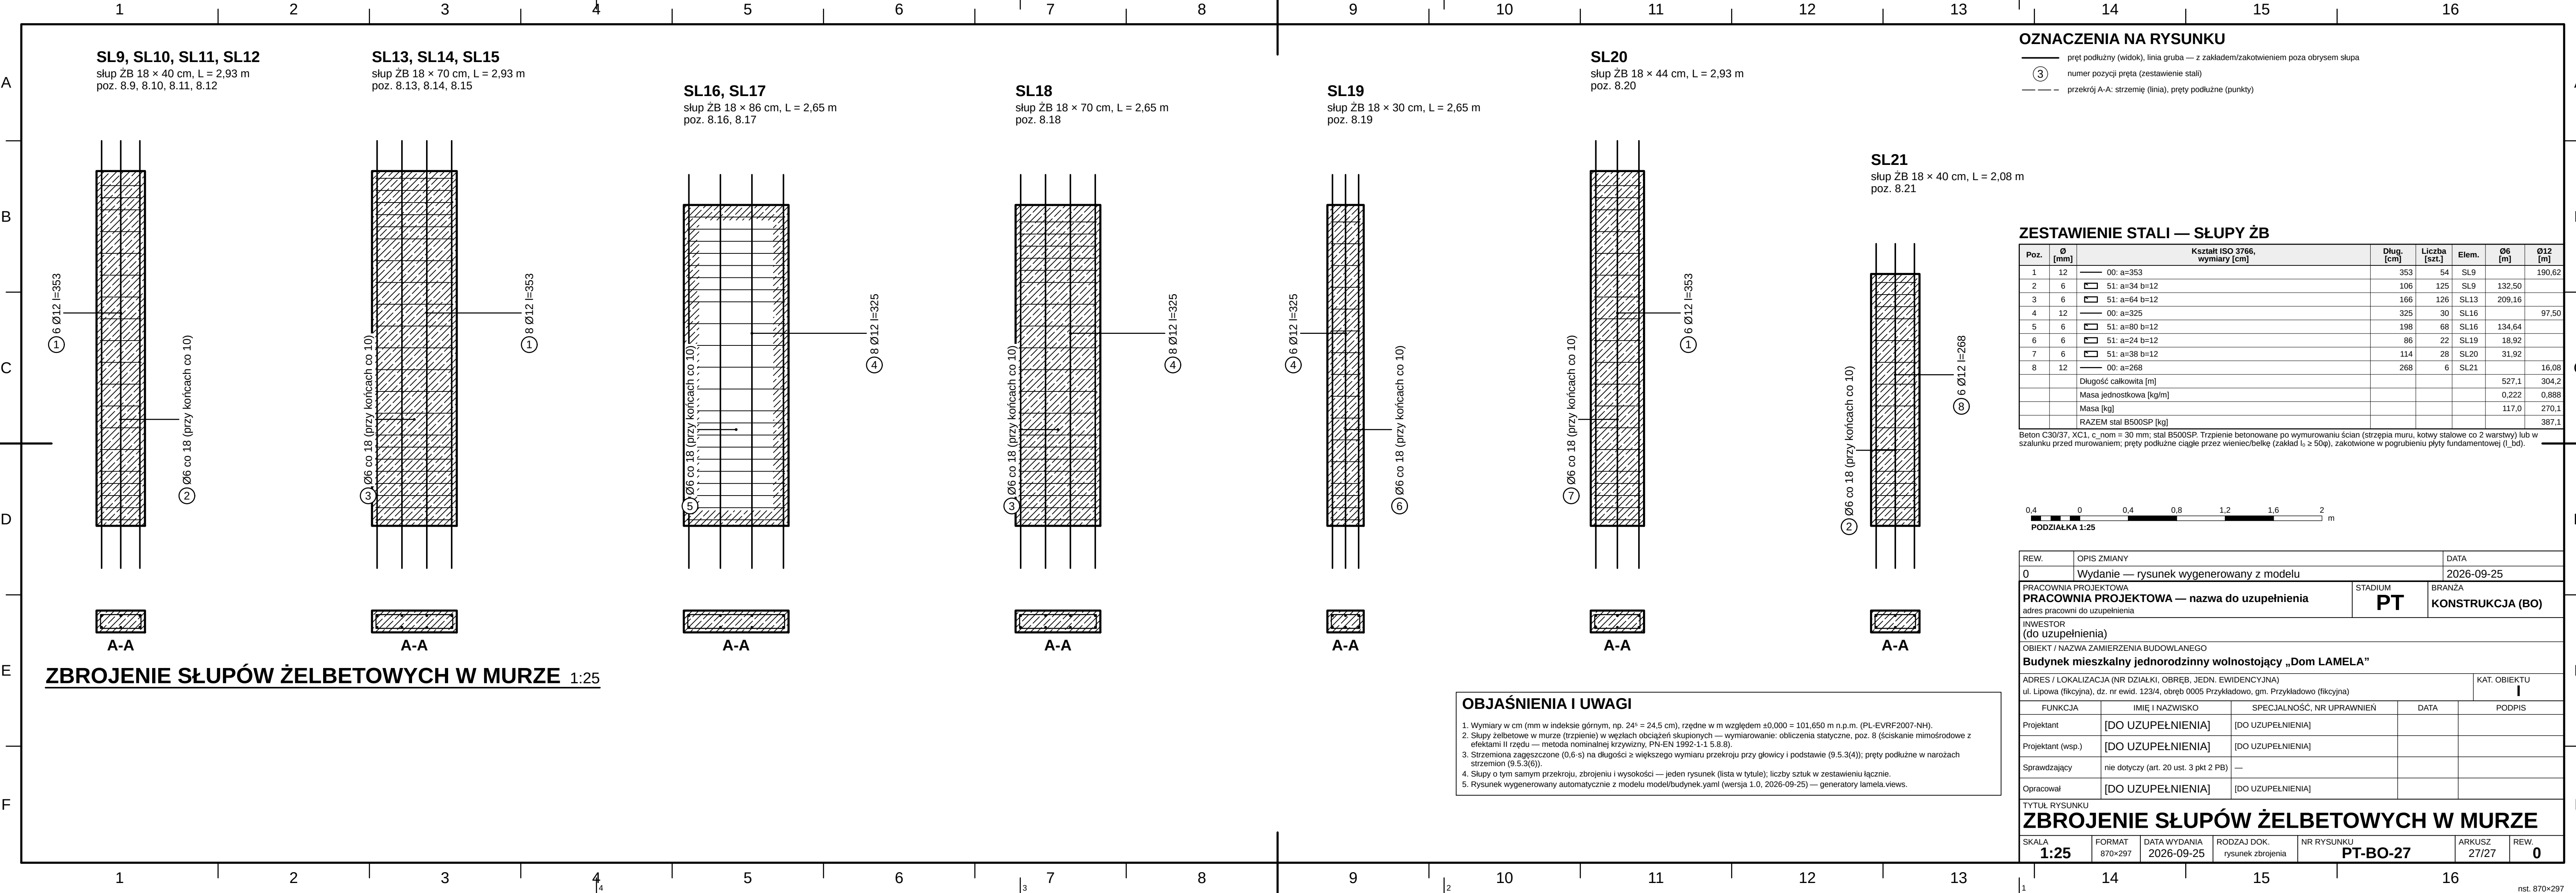

OBJAŚNIENIA I UWAGI

- Wymiary w cm (mm w indeksie górnym, np. 24⁵ = 24,5 cm), rzędne w m względem ±0,000 = 101,650 m n.p.m. (PL-EVRF2007-NH).
- Słupy żelbetowe w murze (trzpienie) w węzłach obciążeń skupionych — wymiarowanie: obliczenia statyczne, poz. 8 (ściskanie mimośrodowe z efektami II rzędu — metoda nominalnej krzywizny, PN-EN 1992-1-1 5.8.8).
- Strzemia zageszczone (0,6-s) na długości z większego wymiaru przekroju przy głowicy i podstawie (9.5.3(4)); pręty podłużne w narożach strzemion (9.5.3(6)).
- Słupy o tym samym przekroju, zbrojeniu i wysokości — jeden rysunek (lista w tytule); liczby sztuk w zestawieniu łącznie.
- Rysunek wygenerowany automatycznie z modelu model/budynek.yaml (wersja 1.0, 2026-09-25) — generatory lamela.views.