



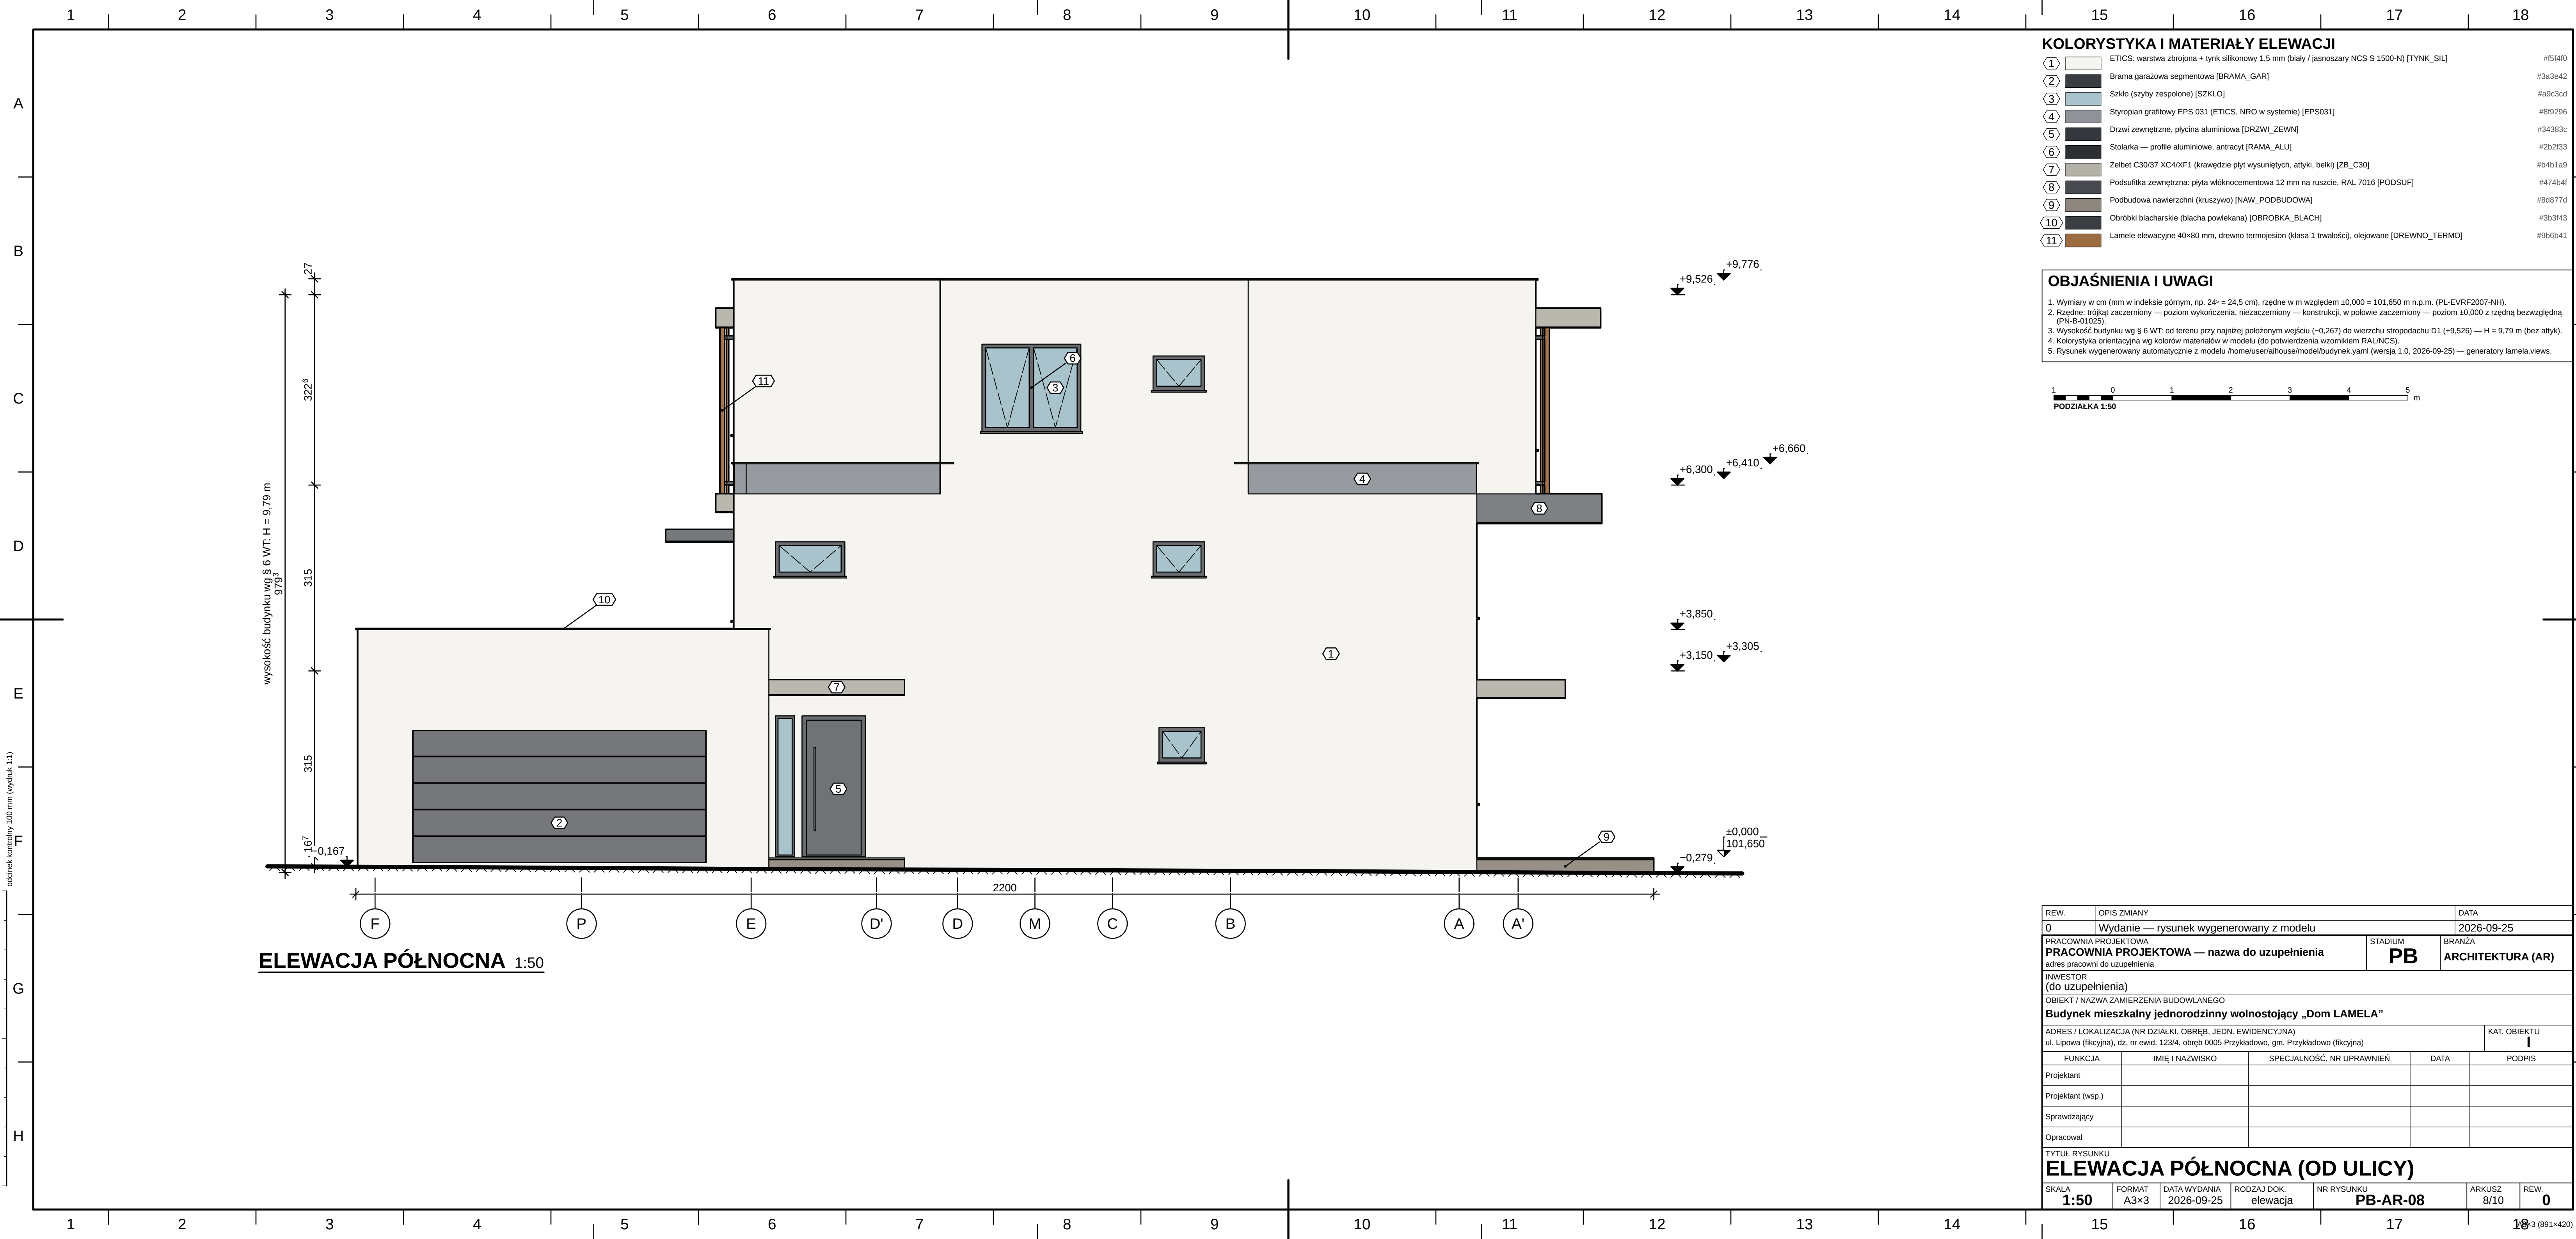

KOLORYSTYKA I MATERIAŁY ELEWACJI			
1		ETICS: warstwa zbrojona + tynk silikonowy 1,5 mm (biały / jasnoszary NCS S 1500-N) [TYNK_SIL]	#f5f4f0
2		Brama garażowa segmentowa [BRAMA_GAR]	#3a3c42
3		Szkło (szyby zespolone) [SZKLO]	#a9c3cd
4		Styropian grafitowy EPS 031 [ETICS, NRO w systemie] [EPS031]	#8f9296
5		Drzwi zewnętrzne, płycina aluminiowa [DRZWI_ZEWN]	#34383c
6		Stolarka — profile aluminiowe, antrycyt [RAMA_ALU]	#2b2f33
7		Żelbet C30/37 XC4/XF1 (krawędzie płyt wysuniętych, attyki, belki) [ZB_C30]	#4b41a9
8		Podsufita zewnętrzna: płyta włóknocementowa 12 mm na ruszcie, RAL 7016 [PODSUF]	#474b4f
9		Podbudowa nawierzchni (kruszywo) [NAW_PODBUDOWA]	#80877d
10		Obróbki blacharskie (blacha powlekana) [OBRÓBKA_BLACH]	#3b3f43
11		Lamele elewacyjne 40x80 mm, drewno termojesion (klasa 1 trwałości), olejowane [DREWNO_TERMJO]	#9b6b41

OBJAŚNIENIA I UWAGI

1. Wymiary w cm (mm w indeksie górnym, np. 24" = 24,5 cm), rzędne w m względem $\pm 0,000 \pm 0,165$ m n.p.m. (PL-EVRF2007-NH).
2. Rzędne: trójką znaczącą – poziom wykończenia, niezaczerpnięty – konstrukcji, w połowie zaczerpnięty – poziom $\pm 0,000$ z rzędną bezwzględną (PN-B-01025).
3. Wysokość budynku wg § 6 WT: od terenu przy najniższej położonym wejściu ($-0,267$) do wierzchu stropodachu D1 (+9,526) – $H = 9,79$ m (bez attyki).
4. Kolorystyka orientacyjna wg kolorów materiałów w modelu (od potwierdzenia wzornikiem RAL/NC).
5. Rysunek wygenerowany automatycznie z modelu `/home/user/arkadiusz/models/budynek_yam` (wersja 1.0, 2026-09-25) – generatory lamela.views.

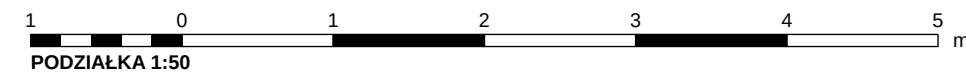

REW.		OPIS ZMIANY		DATA	
0		Wydanie — rysunek wygenerowany z modelu		2026-09-25	
PRACOWNIA PROJEKTOWA PRACOWNIA PROJEKTOWA — nazwa do uzupełnienia adres pracowni do uzupełnienia			STADIUM PB	BRANŻA ARCHITEKTURA (AR)	
INWESTOR (do uzupełnienia)					
OBJEKT / NAZWA ZAMIERZENIA BUDOWLANEGO Budynek mieszkalny jednorodzinny wolnostojący „Dom LAMELA”					
ADRES / LOKALIZACJA, NR DZIAŁKI, OBRĘB, JEDN. EWIDENCYJNA ul. Lipowa (fakcyjna), dz. nr ewid. 123/4, obręb 0005 Przykładowo, gm. Przykładowo (fikcyjna)				KAT. OBIEKTU I	
FUNKCJA	IMIĘ I NAZWISKO	SPECJALNOŚĆ, NR UPRAWNIIEŃ		DATA	PODPIS
Projektant					
Projektant (wsp.)					
Sprawdzający					
Opracował					
TYTUŁ RYSUNKU ELEWACJA PÓŁNOCNA (OD ULICY)					
SKALA 1:50	FORMAT A3×3	DATA WYDANIA 2026-09-25	RODZAJ DOK. elewacja	NR RYSUNKU PB-AR-08	ARKUSZ 8/10
					REW. 0