



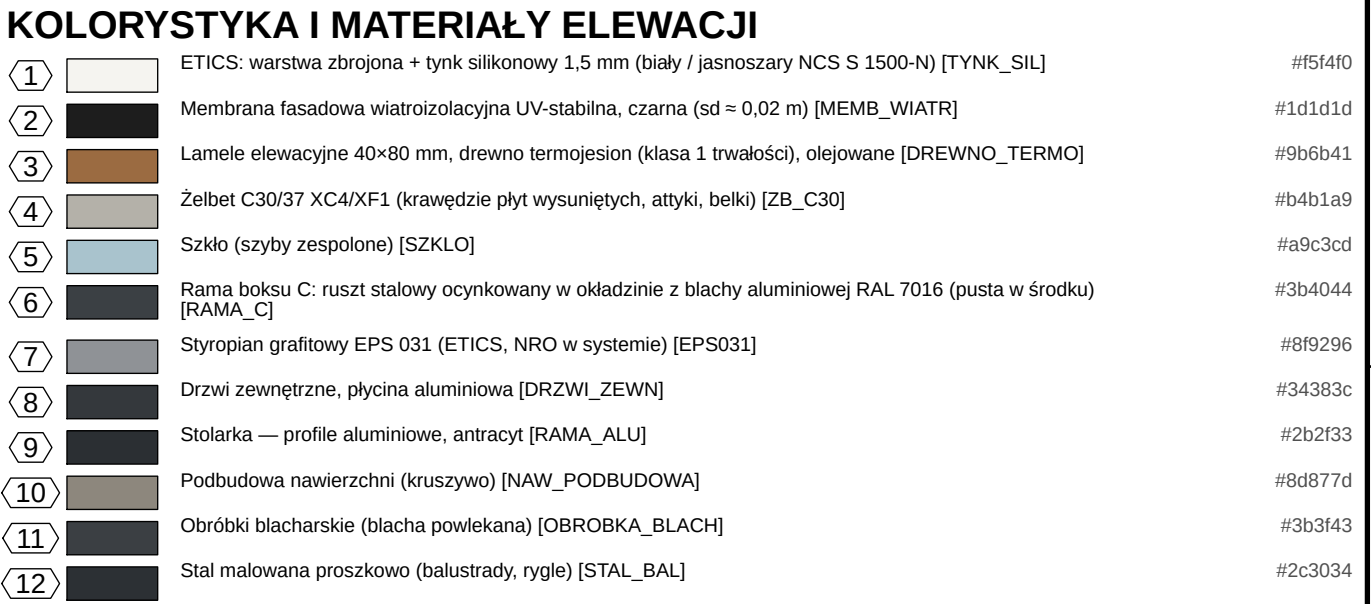

1. Wymiary w cm (mm w indeksie górnym, np. 24" = 24,5 cm), rzędne w m względem $\pm 0,000 = 101,650$ m n.p.m. (PL-EVRF2007-NH).
2. Rzędne: trójką zaczerpiony — poziom wykończenia, niezaczerpiony — konstrukcji, w połowie zaczerpiony — poziom $\pm 0,000$ z rzędną bezwzględną (PN-B-01025).
3. Wykośnienie budynku wg § 6 WT: od terenu przy najniżej położonym wejściu ($-0,267$) do wierzchu stropodachu D1 (+9,526) — $H = 9,79$ m (bez attyki).
4. Kolorystyka orientacyjna wg kolorów materiałów w modelu (do potwierdzenia wzornikiem RAL/NC).
5. Rysunek wygenerowany automatycznie z modelu /home/user/aihouse/model/budynek.yaml (wersja 1.0, 2026-09-25) — generatory lamela.views.

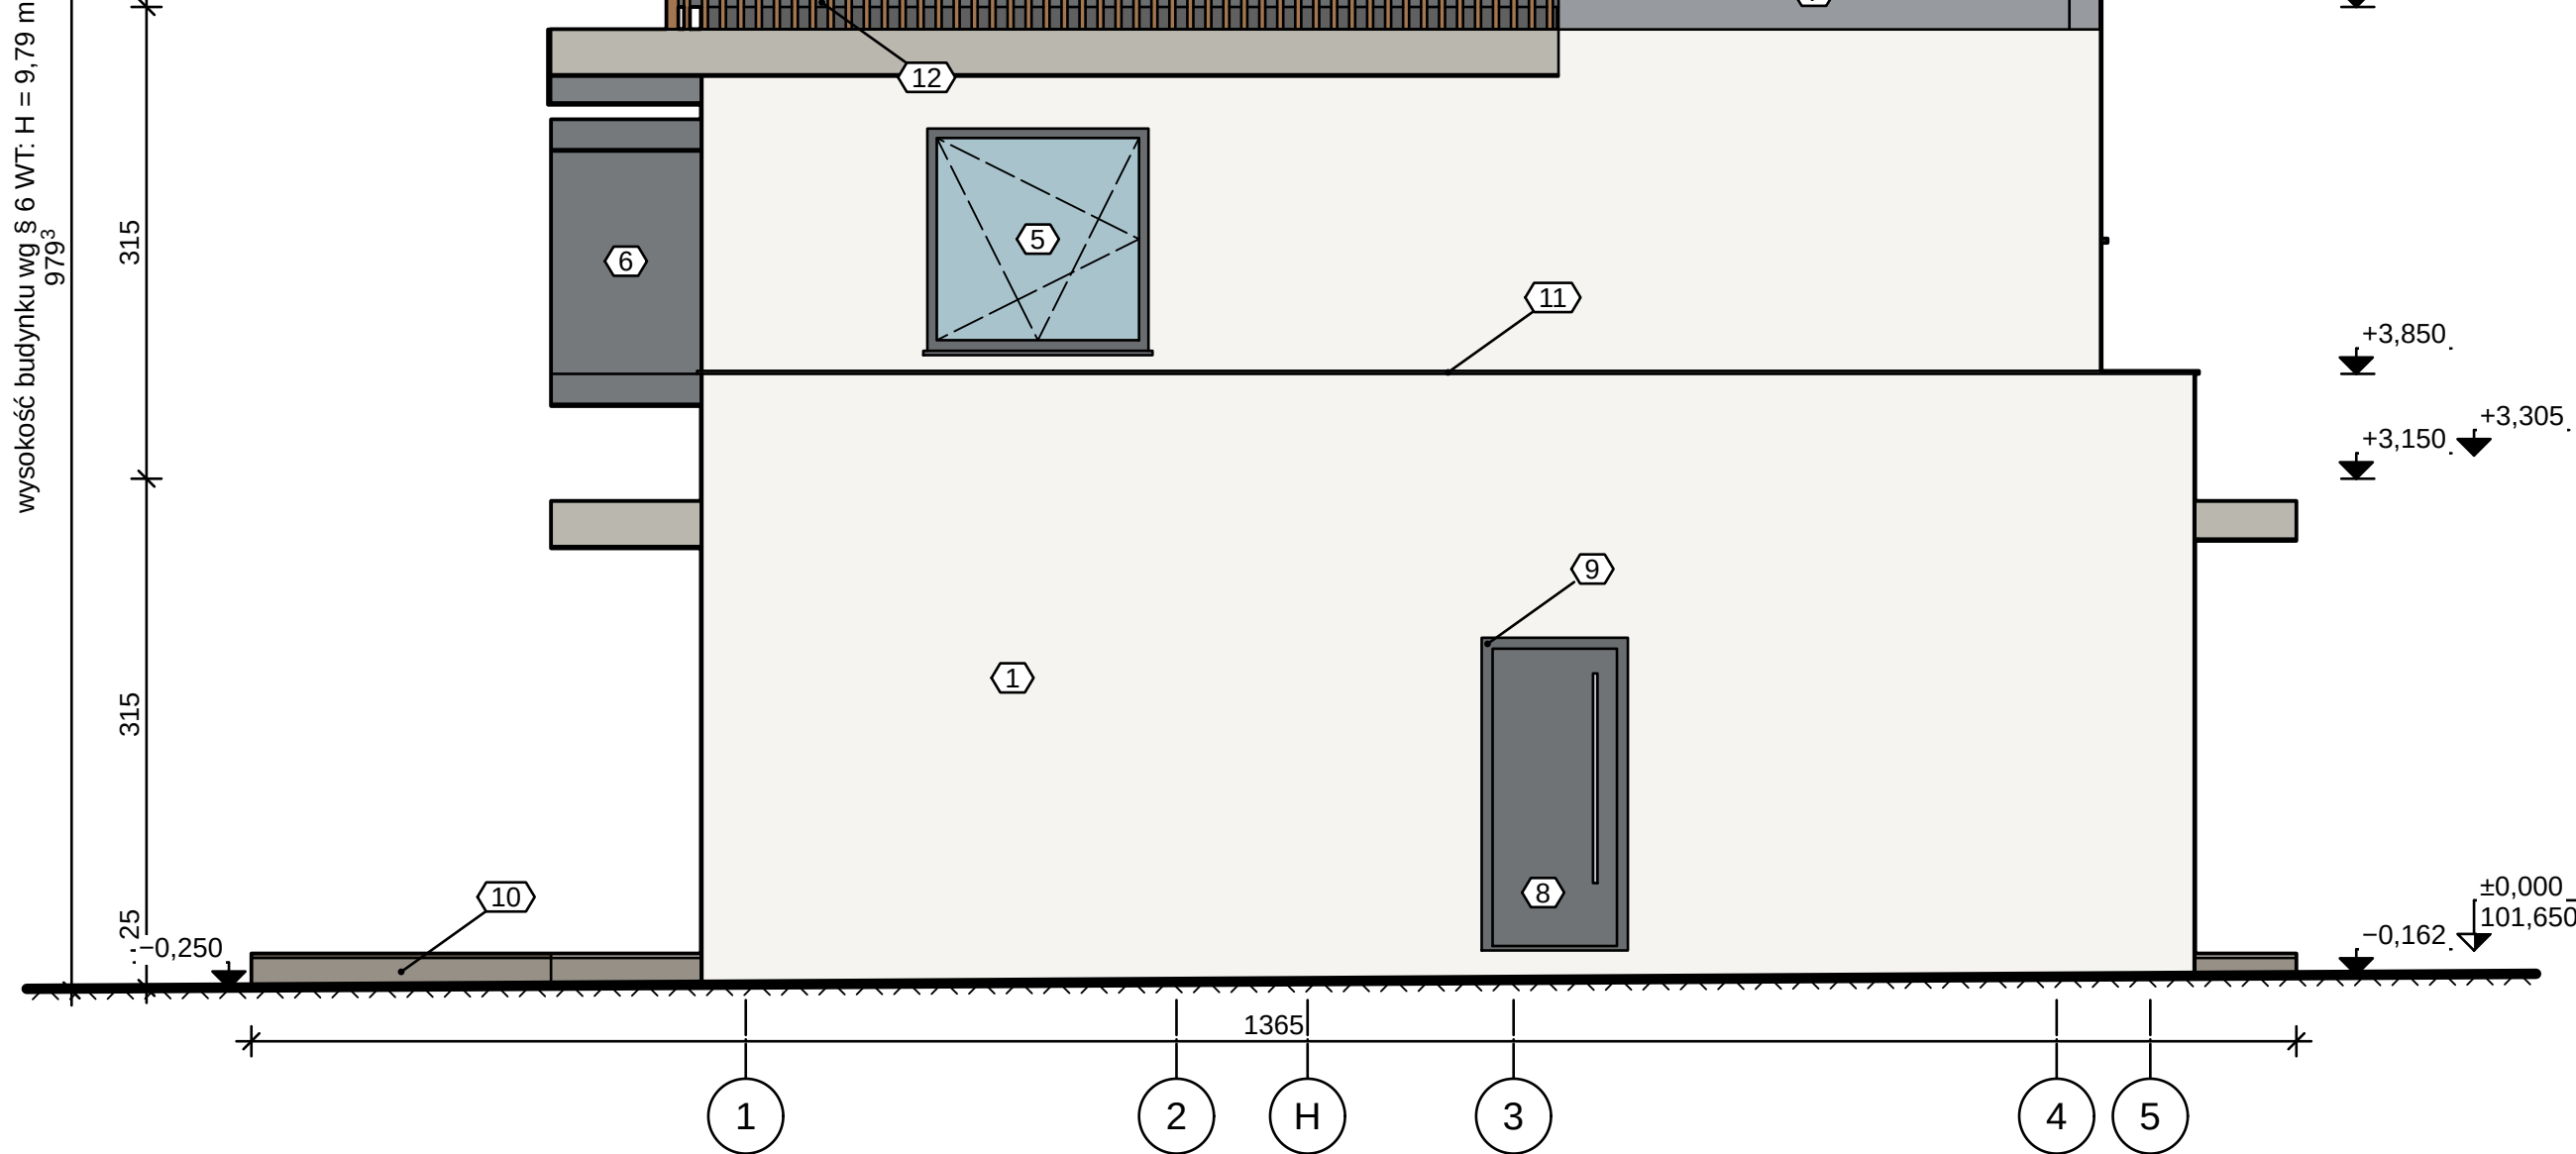

ELEWACJA WSCHODNIA 1:50

odcinek kontrolny 100 mm (wydruk 1:1)