


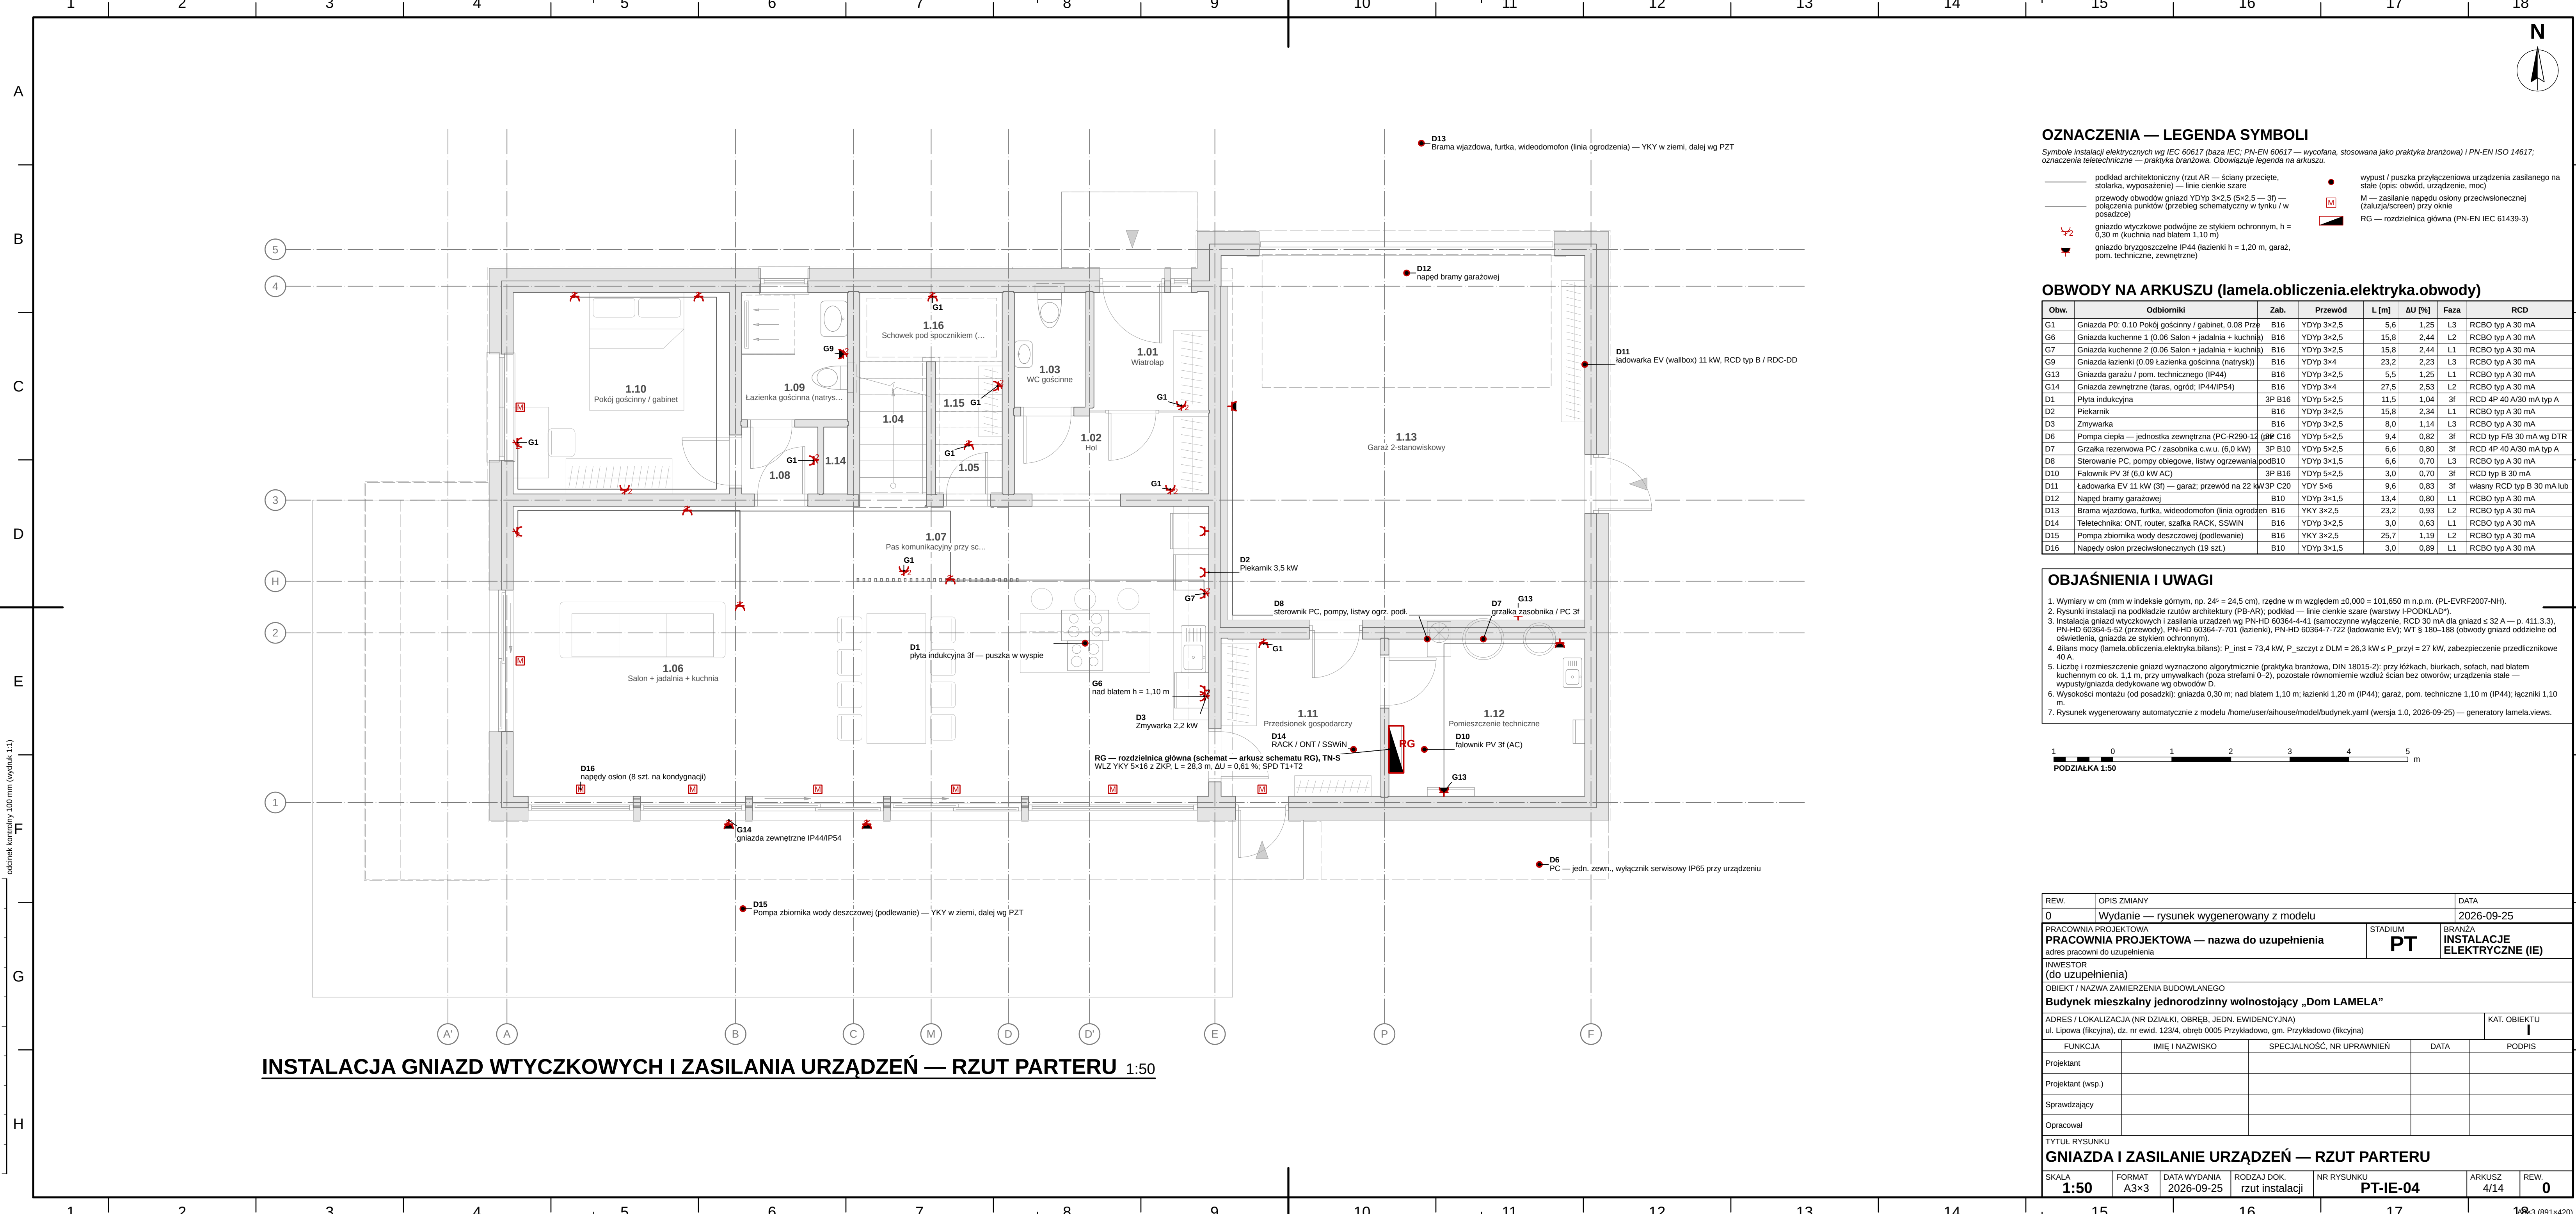

INSTALACJA GNIAZD WTYCZKOWYCH I ZASILANIA URZĄDZEŃ — RZUT PARTERU 1:50

OZNACZENIA — LEGENDA SYMBOLI

Symboly instalacji elektrycznych wg IEC 60617 (baza IEC; PN-EN 60617 — wycofana, stosowana jako praktyka branżowa) i PN-EN ISO 14617; oznaczenia teletechniczne — praktyka branżowa. Obowiązuje legenda na arkuszu.


	podkład architektoniczny (rzut AR) — ściany przecięte, stolarka, wyposażenie		wypust / puszka przyłączeniowa urządzenia zasilanego na stałe (opis: obwód, urządzenie, moc)
	przewody obwodów gniazd YDYp 3×2,5 (5×2,5 — 3f) — połączenia punktów (przebieg schematyczny w tynku / w posadzce)		M — zasilanie napędu osłony przeciwsłonecznej (zaluza/screen) przy oknie
	gniazdo wtyczkowe podwójne ze stykiem ochronnym, h = 0,30 m (kuchnia nad blatem 1,10 m)		RG — rozdzielnica główna (PN-EN IEC 61439-3)
	gniazdo bryzgoczelne IP44 (łazienki h = 1,20 m, garaż, pom. techniczne, zewnętrzne)		

OBWODY NA ARKUSZU (lamela.obliczenia.elektryka.obwody)

Obw.	Odbiorniki	Zab.	Przewód	L [m]	ΔU [%]	Faza	RCD
G1	Gniazda PD: 0.10 Pokój gościnny / gabinet, 0.08 Przp	B16	YDYp 3×2,5	5,6	1,25	L3	RCBO typ A 30 mA
G6	Gniazda kuchenne 1 (0.06 Salon + jadalnia + kuchnia)	B16	YDYp 3×2,5	15,8	2,44	L2	RCBO typ A 30 mA
G7	Gniazda kuchenne 2 (0.06 Salon + jadalnia + kuchnia)	B16	YDYp 3×2,5	15,8	2,44	L1	RCBO typ A 30 mA
G9	Gniazda łazienki (0.09 Łazienka gościnna (natrys))	B16	YDYp 3×4	23,2	2,23	L3	RCBO typ A 30 mA
G13	Gniazda garażu / pom. technicznego (IP44)	B16	YDYp 3×2,5	5,5	1,25	L1	RCBO typ A 30 mA
G14	Gniazda zewnętrzne (taras, ogród, IP44/IP54)	B16	YDYp 3×4	27,5	2,53	L2	RCBO typ A 30 mA
D1	Płyta indukcyjna	3P B16	YDYp 5×2,5	11,5	1,04	3f	RCD 4P 40 A/30 mA typ A
D2	Piekarnik	B16	YDYp 3×2,5	15,8	2,34	L1	RCBO typ A 30 mA
D3	Zmywarka	B16	YDYp 3×2,5	8,0	1,14	L3	RCBO typ A 30 mA
D6	Pompa ciepła — jednostka zewnętrzna (PC-R290-12)	C16	YDYp 5×2,5	9,4	0,82	3f	RCD typ F/B 30 mA wg DTR
D7	Grzałka rezerwowa PC / zasobnika c.w.u. (6,0 kW)	3P B10	YDYp 5×2,5	6,6	0,80	3f	RCD 4P 40 A/30 mA typ A
D8	Sterowanie PC, pompy obiegowe, listwy ogrzewania	podB10	YDYp 3×1,5	6,6	0,70	L3	RCBO typ A 30 mA
D10	Falownik PV 3f (6,0 kW AC)	3P B16	YDYp 5×2,5	3,0	0,70	3f	RCD typ B 30 mA
D11	Ładowarka EV 11 kW (3f) — garaż; przewód na 22 kV	3P C20	YDY 5×6	9,6	0,83	3f	własny RCD typ B 30 mA lub
D12	Napęd bramy garażowej	B10	YDYp 3×1,5	13,4	0,80	L1	RCBO typ A 30 mA
D13	Brama wjazdowa, furtka, wideodomofon (linia ogrodzen	B16	YKY 3×2,5	23,2	0,93	L2	RCBO typ A 30 mA
D14	Teletechnika: ONT, router, szafka RACK, SSWIN	B16	YDYp 3×2,5	3,0	0,63	L1	RCBO typ A 30 mA
D15	Pompa zbiornika wody deszczowej (podlewanie)	B16	YKY 3×2,5	25,7	1,19	L2	RCBO typ A 30 mA
D16	Napędy osłon przeciwsłonecznych (19 szt.)	B10	YDYp 3×1,5	3,0	0,89	L1	RCBO typ A 30 mA

OBJAŚNIENIA I UWAGI

- Wymiary w cm (mm w indeksie górnym, np. 24^o = 24,5 cm), rzędne w m względem ±0.000 = 101,650 m n.p.m. (PL-EVRF2007-NH).
- Rysunki instalacji na podkładzie rzutów architektury (PB-AR); podkład — linie cienie szare (warstwy I-PODKLADY).
- Instalacja gniazd wtyczkowych i zasilania urządzeń wg PN-HD 60364-4-41 (samoczynne wyłączenie, RCD 30 mA dla gniazd ≤ 32 A — p. 411.3.3); PN-HD 60364-5-52 (przewody); PN-HD 60384-7-701 (łazienki); PN-HD 60364-7-722 (ładowanie EV); WT § 180–188 (obwody gniazd oddzielne od oświetlenia, gniazda ze stykiem ochronnym).
- Bilans mocy (lamela.obliczenia.elektryka.bilans): P_{inst} = 73,4 kW, P_{szzczyt} z DLM = 26,3 kW ≤ P_{przyl} = 27 kW, zabezpieczenie przedlicznikowe 40 A.
- Liczbe i rozmieszczenie gniazd wyznaczono algorytmicznie (praktyka branżowa, DIN 18015-2); przy kółkach, biurkach, sofach, nad blatem kuchennym co ok. 1,1 m, przy umywalkach (poza strefami 0–2), pozostałe równomiernie wzdłuż ścian bez otworów; urządzenia stałe — wypusty/gniazda dedykowane wg obwodów D.
- Wysokości montażu (od posadzki): gniazda 0,30 m; nad blatem 1,10 m; łazienki 1,20 m (IP44); garaż, pom. techniczne 1,10 m (IP44); łączniki 1,10 m.
- Rysunek wygenerowany automatycznie z modelu /home/user/aihouse/model/budynek.yaml (wersja 1.0, 2026-09-25) — generatory lamela.views.

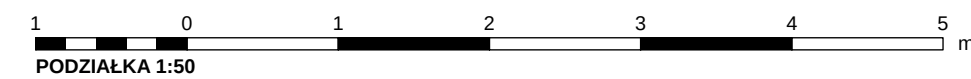

REW.	OPIS ZMIANY	DATA
0	Wydanie — rysunek wygenerowany z modelu	2026-09-25
PRACOWNIA PROJEKTOWA	PRACOWNIA PROJEKTOWA — nazwa do uzupełnienia	STADIUM PT
adres pracowni do uzupełnienia	BRANŻA INSTALACJE ELEKTRYCZNE (IE)	
INWESTOR	(do uzupełnienia)	
OBIEKT / NAZWA ZAMIERZENIA BUDOWLANEGO	Budynek mieszkalny jednorodzinny wolnostojący „Dom LAMELA”	
ADRES / LOKALIZACJA (NR DZIAŁKI, OBRĘB, JEDN. EWIDENCYJNA)	KAT. OBIEKTU I	
ul. Lipowa (fikcyjna), dz. nr ewid. 123/4, obręb 0005 Przykładowo, gm. Przykładowo (fikcyjna)		
FUNKCJA	IMIĘ I NAZWISKO	SPECJALNOŚĆ, NR UPRAWNIEN
Projektant		DATA
Projektant (wsp.)		PODPIS
Sprawdzający		
Opracował		
TYTUŁ RYSUNKU	Gniazda i zasilanie urządzeń — Rzut Parteru	
SKALA 1:50	FORMAT A3×3	DATA WYDANIA 2026-09-25
RODZAJ DOK. rzut instalacji	NR RYSUNKU PT-IE-04	ARKUSZ 4/14
		REW. 0