

RZUT KONSTRUKCJI — PŁYTY ST1, D4, PL-E, PL-DA 1:50

OZNACZENIA MATERIAŁÓW (PN-B-01030 + przyjęte)

☒ Błoczek wapienno-piaskowy (silikat) 18 cm, kl. 20, gr. 1, na zaprawie cienkowarstwowej — kratka ukośna 45°/135°

OZNACZENIA NA RYSUNKU


- słup stalowy (przekrój) — pod płytą
▨ słup żelbetowy w murze (trzcina) — przekrój kreskowany; zbrojenie PT-BO-27
--- belka / podciąg pod płytą (widok zasłonięty); linia ciągła — belka odwrócona (nad płytą)
▬ łącznik termoizolacyjny płyty wspornikowej (ETA)
↔ kierunek pracy pola (krzyż — płyta krzyżowo zbrojona); P1... — pola obliczeniowe MES
NA, NB... — typ nadproża (tabela); ściany pod płytą kreskowane wg materiału

NADPROŻA ŻELBETOWE W ŚCIANACH POD PŁYTĄ (z obliczeń; zbrojenie — arkusz nadproży)

Typ	b×h [cm]	L [m]	dół/góra	strzemiona	otwory	poz. obl.
NC	18×24	1,30	2Ø10 / 2Ø10	Ø6 co 15	00-06	6.1
ND	18×25	1,30	2Ø10 / 2Ø10	Ø6 co 15	00-22	6.13
NG	18×25	1,40	2Ø10 / 2Ø10	Ø6 co 15	00-08	6.2

OBJAŚNIENIA I UWAGI

- Wymiary w cm (mm w indeksie górnym, np. 24⁵ = 24,5 cm), rzędne w m względem ±0,000 = 101,650 m n.p.m. (PL-EVRF2007-NH).
- PL-E: łączniki termoizolacyjne ciągłe na całej linii zamocowania — wyrób z Europejską Oceną Techniczną (EAD 050001-00-0301) „lub równoważny” (np. typ z prętami ze stali nierdzewnej przez izolację gr. 80–120 mm); dobór wg dokumentacji producenta na m_{Ed} i v_{Ed} z obliczeń, z uwzględnieniem uskoju wierzchu płyt; sprawdzenie ugięcia wspornika z podatnością łącznika (W-268, W-272).
- PL-DA: łączniki termoizolacyjne ciągłe na całej linii zamocowania — wyrób z Europejską Oceną Techniczną (EAD 050001-00-0301) „lub równoważny” (np. typ z prętami ze stali nierdzewnej przez izolację gr. 90–120 mm); dobór wg dokumentacji producenta na m_{Ed} i v_{Ed} z obliczeń, z uwzględnieniem uskoju wierzchu płyt; sprawdzenie ugięcia wspornika z podatnością łącznika (W-268, W-272).
- Płyty monolityczne: ST1 h = 22 cm (C25/30, XC1, c_{nom} = 25 mm), D4 h = 24 cm (C25/30, XC1, c_{nom} = 25 mm), PL-E h = 30 cm (C30/37, XC3, c_{nom} = 35 mm), PL-DA h = 25 cm (C30/37, XC4, c_{nom} = 40 mm); wierzch konstrukcji +3,000 (średnio), rzędne elementów wg przekrojów i modelu.
- Wierce (W-ST1_D4_PL-E_PL-DA, poz. 7.3): na wszystkich ścianach nośnych pod płytą, szerokość = grubość muru, wysokość = grubość płyty, 4Ø12 + strzemiona Ø6 co 25 cm, C25/30; zakład l₀ = 638 mm (PN-EN 1992-1-1 9.10.2.2, 8.7).
- Kierunek pracy pól wg modelu MES płyty (biblioteka — Wood-Armer); pola P... — numeracja komórek siatki podpór obliczeń (zbrojenie — arkusze zbrojenia dolnego i górnego).
- Ściany-tarcze: analiza nie wykryła ścian-tarcz na tym poziomie (moduł tarcze — ściana ŻB podparta na < 95 % długości lub pole "tarcza: true").
- Rysunek wygenerowany automatycznie z modelu model/budynek.yaml (wersja 1.0, 2026-09-25) — generatory lamela.views.

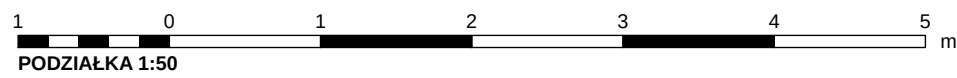

REW.	OPIS ZMIANY			DATA		
0	Wydanie — rysunek wygenerowany z modelu			2026-09-25		
PRACOWNIA PROJEKTOWA PRACOWNIA PROJEKTOWA — nazwa do uzupełnienia adres pracowni do uzupełnienia			STADIUM PT	BRANŻA KONSTRUKCJA (BO)		
INWESTOR (do uzupełnienia)						
OBIEKT / NAZWA ZAMIERZENIA BUDOWLANEGO Budynek mieszkalny jednorodzinny wolnostojący „Dom LAMELA”						
ADRES / LOKALIZACJA (NR DZIAŁKI, OBRĘB, JEDN. EWIDENCYJNA) ul. Lipowa (fikcyjna), dz. nr ewid. 123/4, obręb 0005 Przykładowo, gm. Przykładowo (fikcyjna)				KAT. OBIEKTU I		
FUNKCJA	IMIĘ I NAZWISKO	SPECJALNOŚĆ, NR UPRAWNIENI	DATA	PODPIS		
Projektant	[DO UZUPEŁNIENIA]	[DO UZUPEŁNIENIA]				
Projektant (wsp.)	[DO UZUPEŁNIENIA]	[DO UZUPEŁNIENIA]				
Sprawdzający	nie dotyczy (art. 20 ust. 3 pkt 2 PB)	—				
Opracował	[DO UZUPEŁNIENIA]	[DO UZUPEŁNIENIA]				
TYTUŁ RYSUNKU RZUT KONSTRUKCJI STROPU NAD PARTEREM						
SKALA 1:50	FORMAT 594x460	DATA WYDANIA 2026-09-25	RODZAJ DOK. rzut konstrukcji	NR RYSUNKU PT-BO-06	ARKUSZ 6/27	REW. 0