



B1 — 18×107 cm, C30/37 (poz. 5.15)

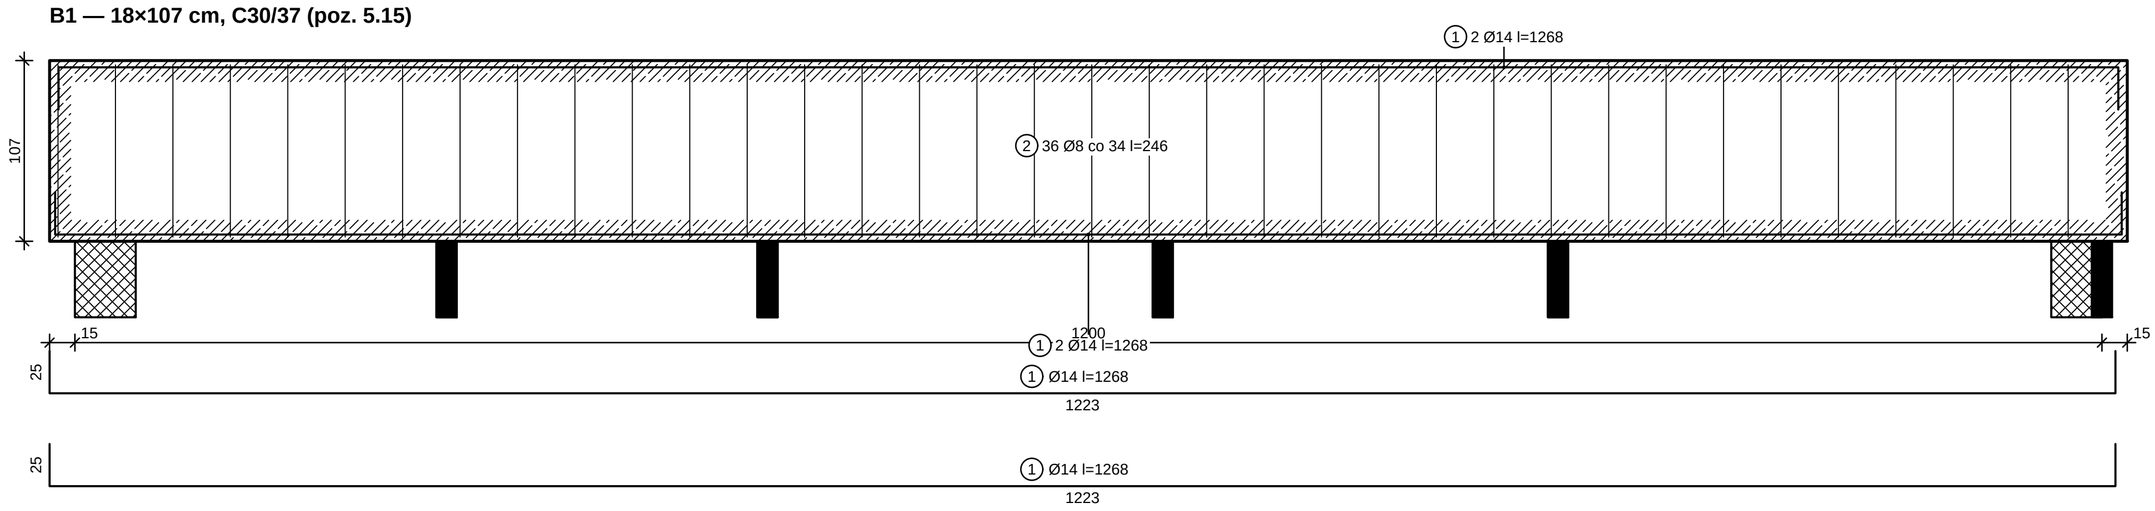

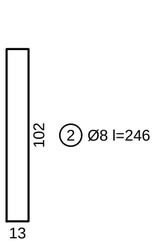



B2 — 18×80 cm, C30/37 (poz. 5.11)

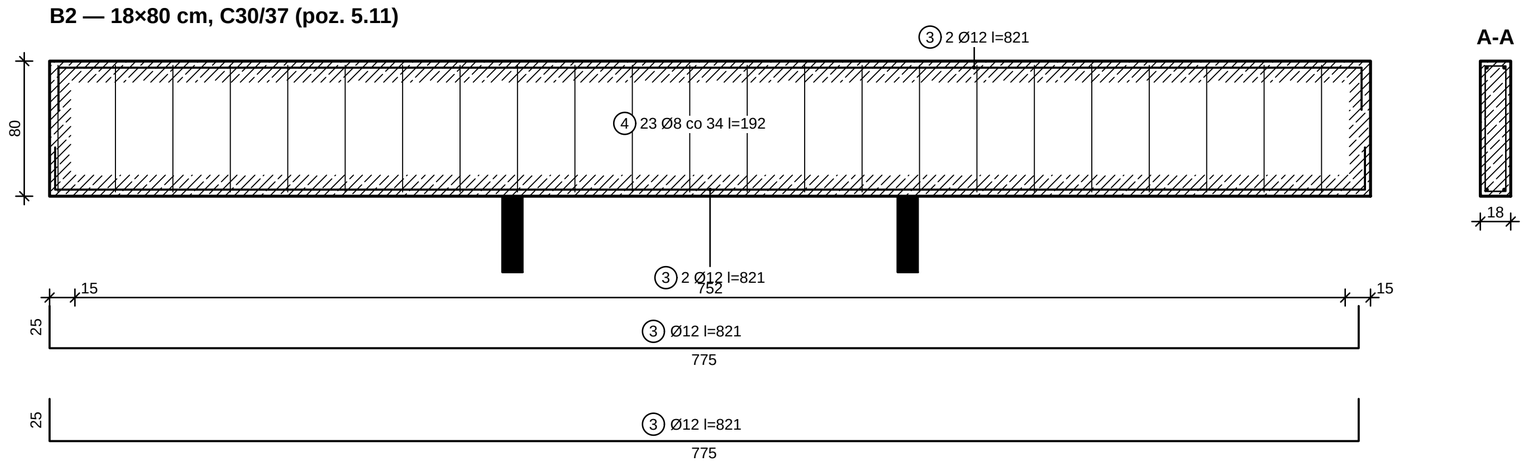

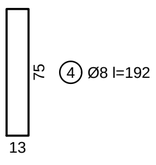



B3 — 20×60 cm, C30/37 (poz. 5.8)

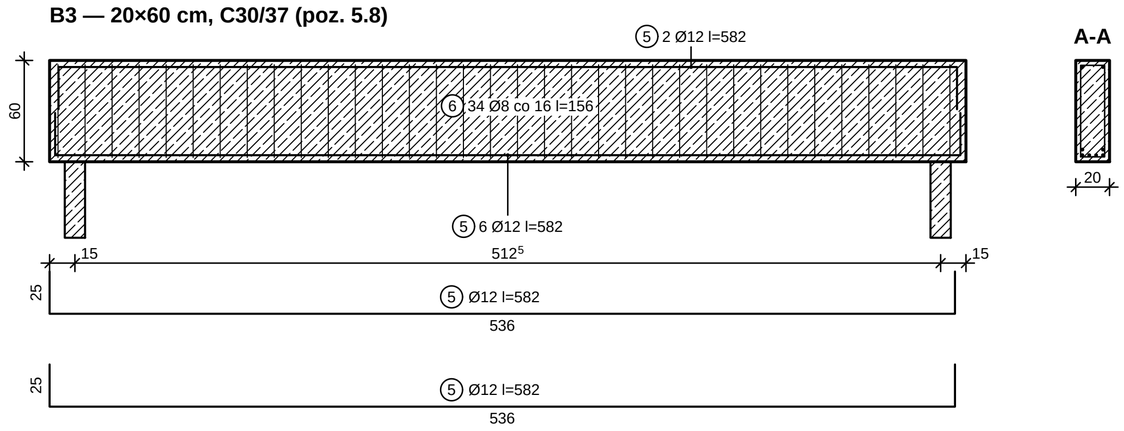

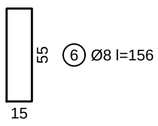



B4 — 18×80 cm, C30/37 (poz. 5.9)

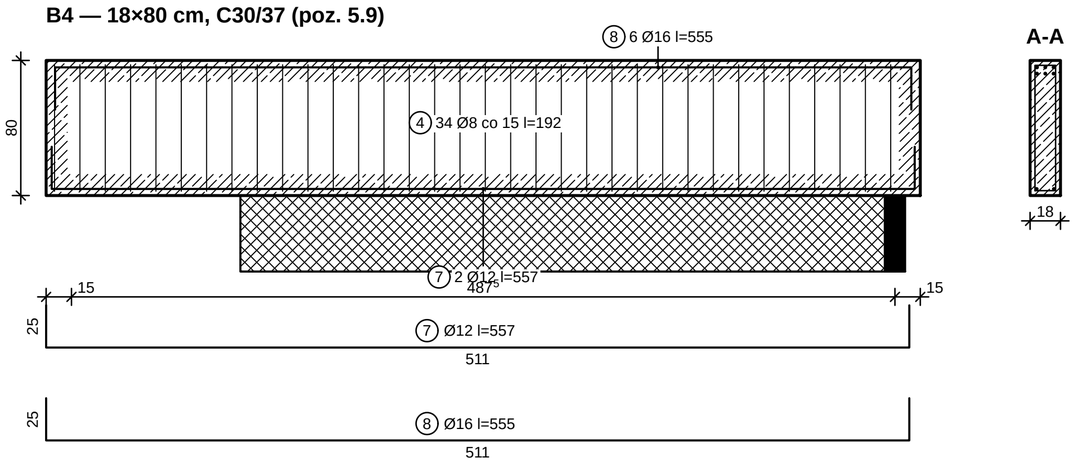

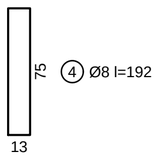

B5 — 18×80 cm, C30/37 (poz. 5.10)

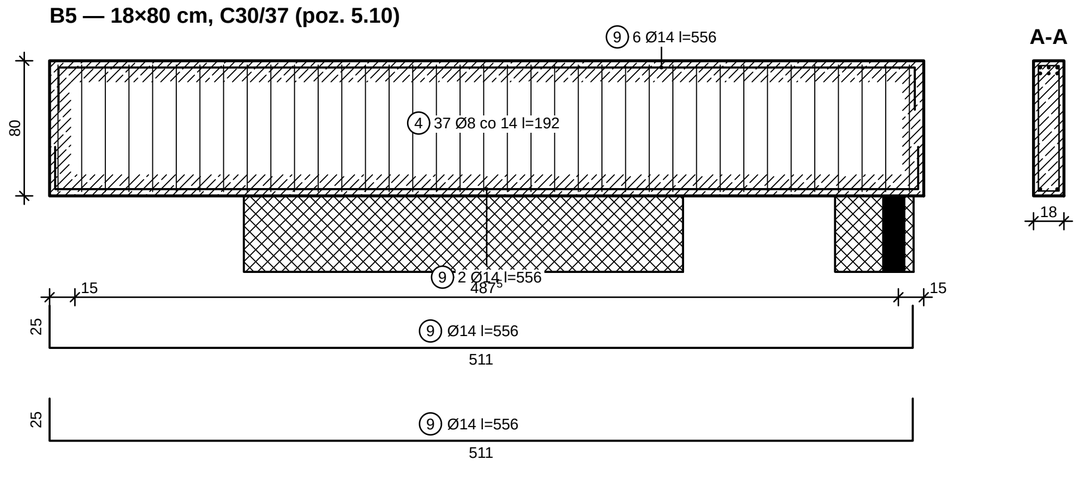

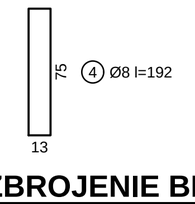

ZESTAWIENIE STALI

Poz.	Ø [mm]	Kształt ISO 3766, wymiary [cm]	Dług. [cm]	Liczba [szt.]	Elem.	Ø8 [m]	Ø12 [m]	Ø14 [m]	Ø16 [m]
1	14	21: a=25 b=1223 c=25	1268	4	B1			50,72	
2	8	51: a=13 b=102	246	37	B1	91,02			
3	12	21: a=25 b=775 c=25	821	4	B2		32,84		
4	8	51: a=13 b=75	192	97	B2	186,24			
5	12	21: a=25 b=536 c=25	582	8	B3		46,56		
6	8	51: a=15 b=55	156	35	B3	54,60			
7	12	21: a=25 b=511 c=25	557	2	B4		11,14		
8	16	21: a=25 b=511 c=25	555	6	B4				33,30
9	14	21: a=25 b=511 c=25	556	8	B5			44,48	
		Długość całkowita [m]				331,9	90,5	95,2	33,3
		Masa jednostkowa [kg/m]				0,395	0,888	1,208	1,578
		Masa [kg]				130,9	80,4	115,0	52,6
		RAZEM stal B500SP [kg]							378,9

B1, B2, B3, B4, B5: beton C30/37, XC1, otulina strzemion c_nom = 25 mm (tabl. 4.4N + NA).

OBJAŚNIENIA I UWAGI

1. Wymiary w cm (mm w indeksie górnym, np. 24⁵ = 24,5 cm), rzędne w m względem ±0,000 = 101,650 m n.p.m. (PL-EVRF2007-NH).
2. Belki: pręty dolne i górne z odgięciami 90° w strefach podporowych (zakotwienie ≥ l_bd od lica podpory — PN-EN 1992-1-1 9.2.1.4), strzemiona zamknięte z hakami 135° (8.5, rys. 8.5), pierwsze strzemię 5 cm od lica podpory; rozstaw wg obliczeń (6.2.3), s ≤ min(0,75·d; 400 mm) (9.6N).
3. Przekrój A-A — w środku rozpiętości; długości prętów l — długości rozwinięcia (wymiary zewnętrzne, odliczenie gięcia wg PN-EN ISO 3766).
4. Betonowanie: beton wg PN-EN 206+A2 i PN-B-06265 (normy wycofane — stosowane jako wiedza techniczna, rejestr D-09; deklarację betonu wg PN-EN 206-1:2026-09 potwierdzić z wytwórnią) (klasa, ekspozycja, D_max 16 mm, konsystencja S3); pielęgnacja ≥ 7 dni (klasa pielęgnacji 2 — PN-EN 13670 p. 8.5); przerwy robocze wyłącznie w miejscach uzgodnionych z projektantem.
5. Rozszalowanie i usunięcie podpór: płyty i belki po uzyskaniu ≥ 70 % f_ck (PN-EN 13670 p. 5.6 i 8.5), wsporniki — nie wcześniej niż po 28 dniach i po wykonaniu elementów dociążających zaplecze; podpory wtórne do 28 dni.
6. Rysunek wygenerowany automatycznie z modelu model/budynek.yaml (wersja 1.0, 2026-09-25) — generatory lamela.views.

ZBROJENIE BELEK B1, B2, B3, B4, B5 1:25

0,4 0 0,4 0,8 1,2 1,6 2 m

PODZIAŁKA 1:25

odcinek kontrolny 100 mm (wydruk 1:1)

REW.	OPIS ZMIANY	DATA
0	Wydanie — rysunek wygenerowany z modelu	2026-09-25

PRACOWNIA PROJEKTOWA
PRACOWNIA PROJEKTOWA — nazwa do uzupełnienia
adres pracowni do uzupełnienia

STADIUM: **PT**

BRANŻA: **KONSTRUKCJA (BO)**

INWESTOR
(do uzupełnienia)

OBIEKT / NAZWA ZAMIERZENIA BUDOWLANEGO
Budynek mieszkalny jednorodzinny wolnostojący „Dom LAMELA”

ADRES / LOKALIZACJA (NR DZIAŁKI, OBRĘB, JEDN. EWIDENCYJNA)
ul. Lipowa (fikcyjna), dz. nr ewid. 123/4, obręb 0005 Przykładowo, gm. Przykładowo (fikcyjna)

KAT. OBIEKTU: I

FUNKCJA	IMIĘ I NAZWISKO	SPECJALNOŚĆ, NR UPRAWNIEŃ	DATA	PODPIS
Projektant	[DO UZUPEŁNIENIA]	[DO UZUPEŁNIENIA]		
Projektant (wsp.)	[DO UZUPEŁNIENIA]	[DO UZUPEŁNIENIA]		
Sprawdzający	nie dotyczy (art. 20 ust. 3 pkt 2 PB)	—		
Opracował	[DO UZUPEŁNIENIA]	[DO UZUPEŁNIENIA]		

TYTUŁ RYSUNKU
ZBROJENIE BELEK (1)

SKALA	FORMAT	DATA WYDANIA	RODZAJ DOK.	NR RYSUNKU	ARKUSZ	REW.
1:25	610×810	2026-09-25	rysunek zbrojenia	PT-BO-20	20/27	0

nst. 610×810