


odcinek kontajniowy 100 mm (wydruk 1:1)

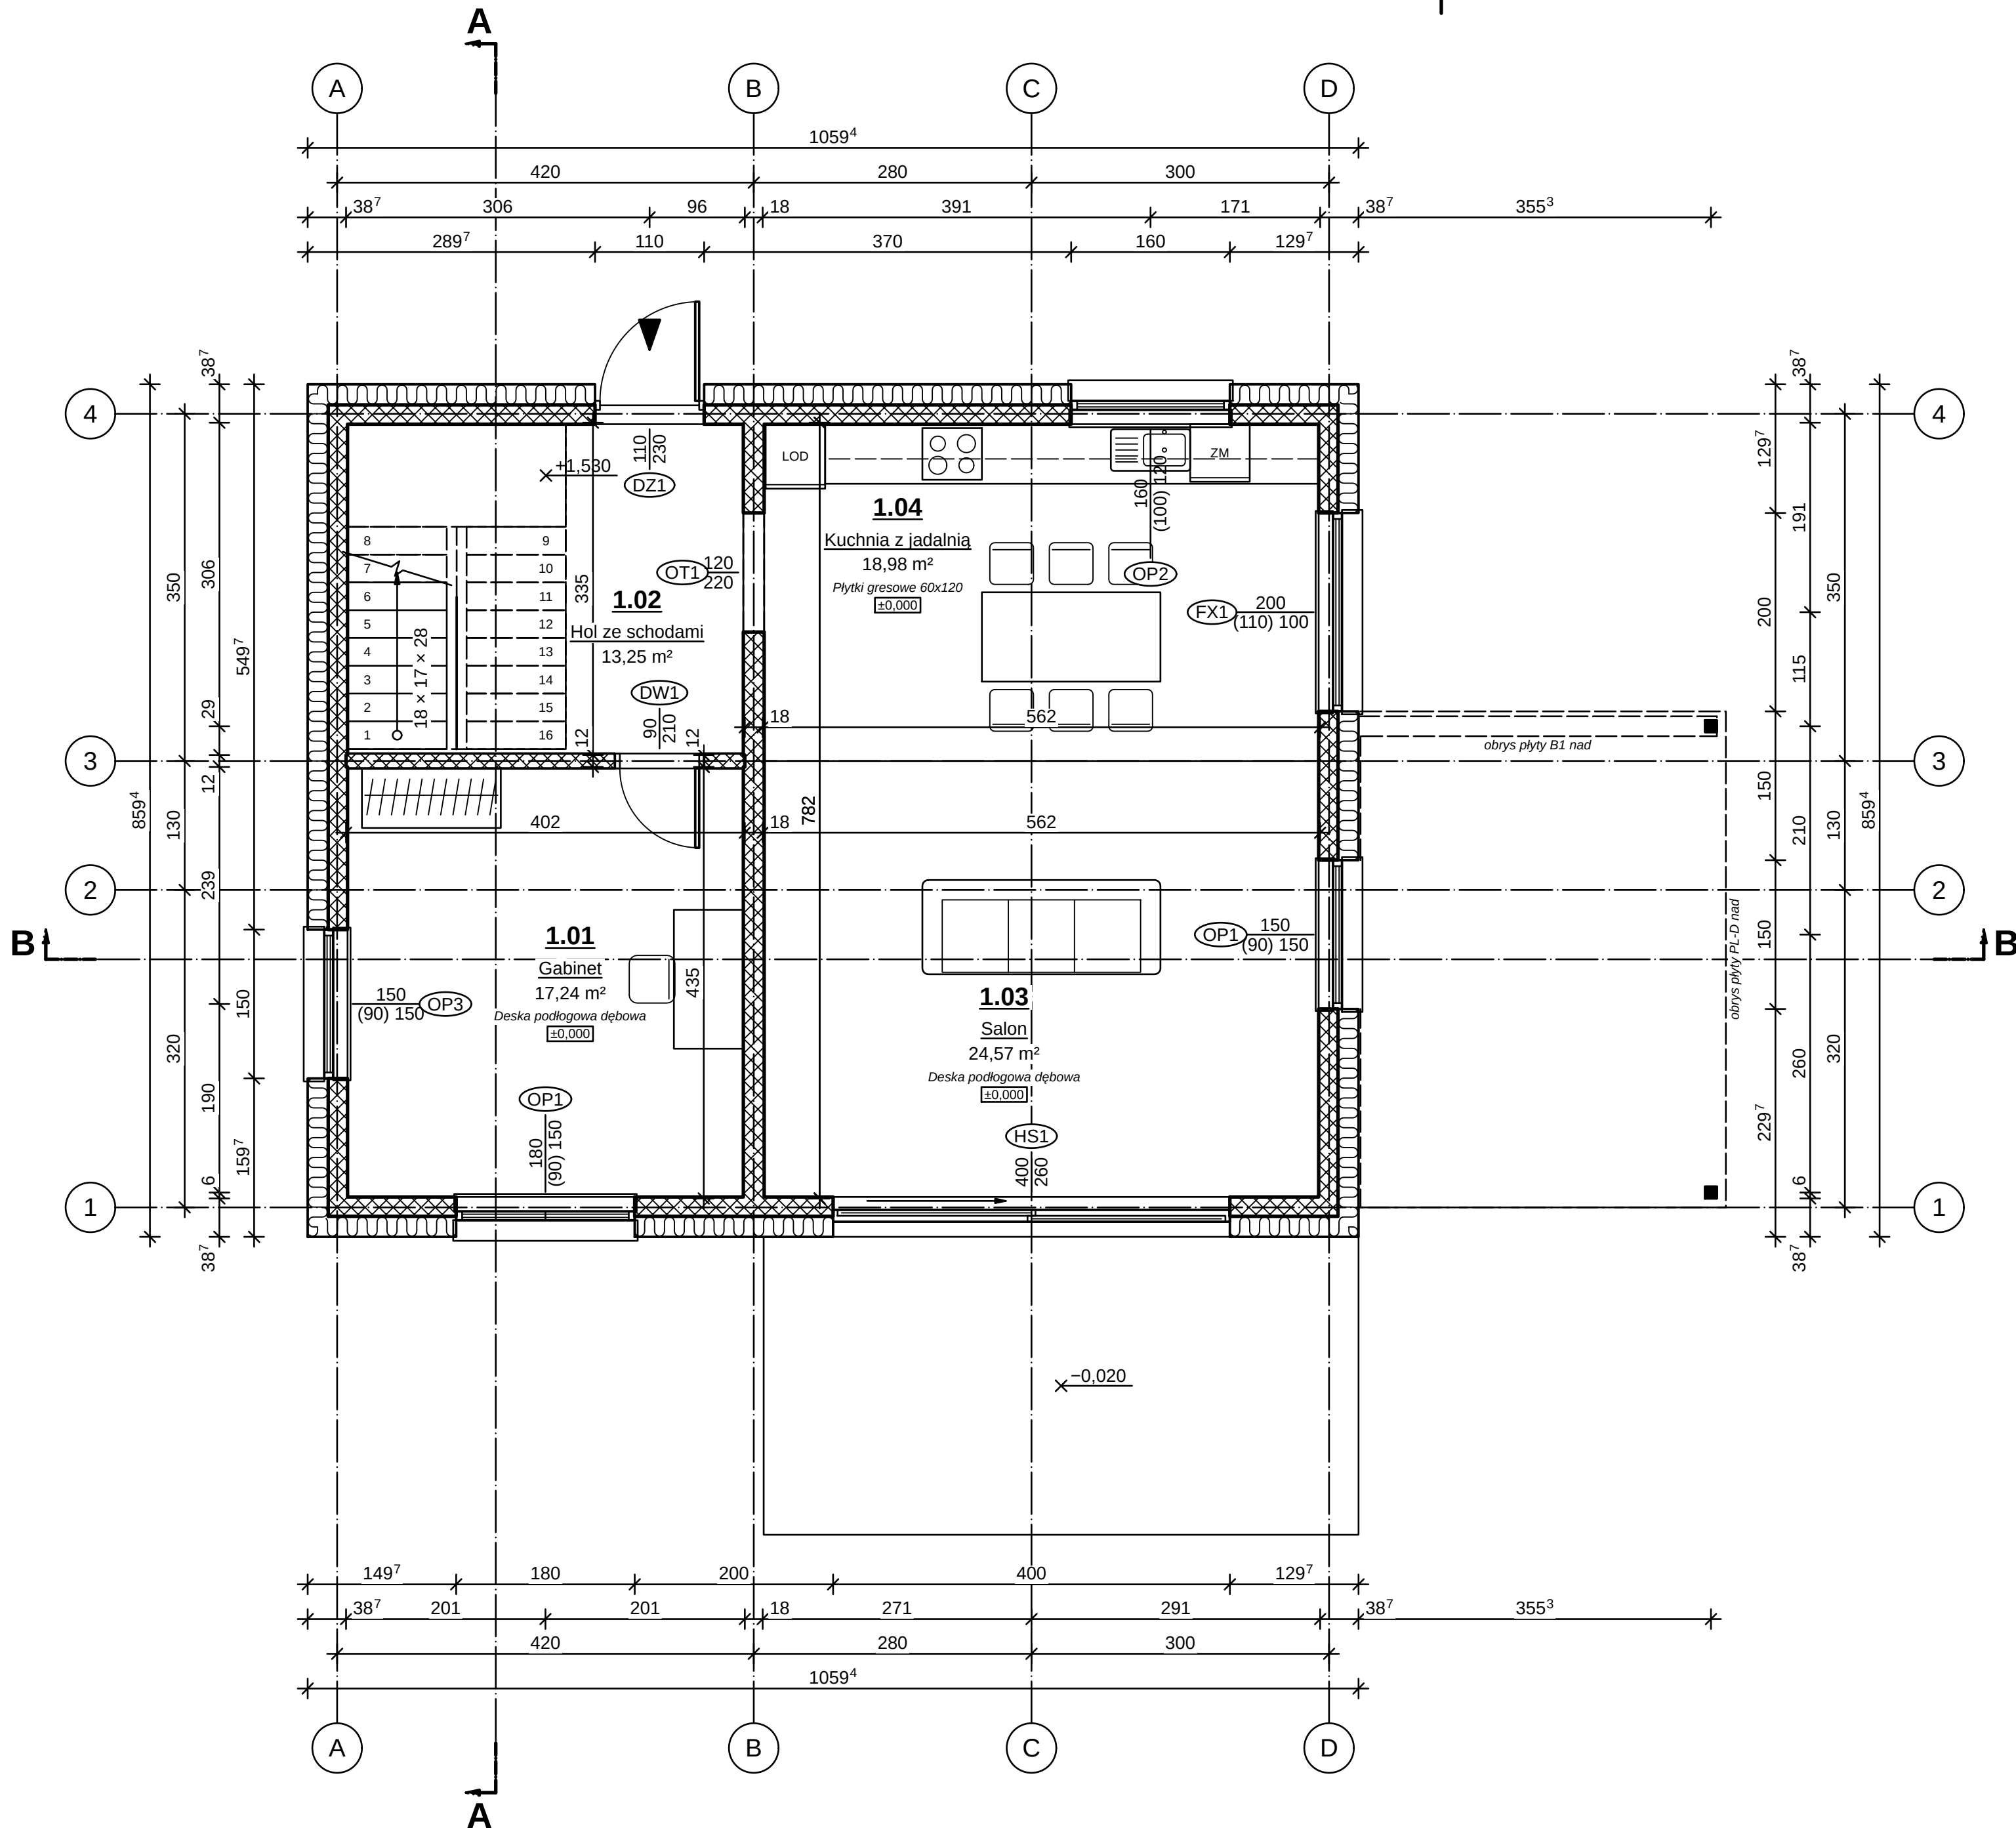

RZUT PARTERU 1:50

ZESTAWIENIE POMIESZCZEŃ

Nr	Nazwa pomieszczenia	Posadzka	Kat.	Wys. [m]	Pow. [m²]
1.03	Salon	Deska podłogowa dębowa	podst.	2,70	24,57
1.04	Kuchnia z jadalnią	Płytki gresowe 60x120	podst.	2,70	18,98
1.01	Gabinet	Deska podłogowa dębowa	podst.	2,70	17,24
1.02	Hol ze schodami	Płytki gresowe 60x120	ruchu	2,70	13,25
RAZEM powierzchnia netto					74,03
w tym użytkowa (podst. + pomoc.)					60,78

OZNACZENIA MATERIAŁÓW (PN-B-01030 + przyjęte)


	Styropian grafitowy EPS 031 — meander „UUU”		Stal konstrukcyjna S355, malowana proszkowo RAL 7016 — zaczemienie
	Bloczek wapienno-piaskowy 12 cm, kl. 15; Bloczek wapienno-piaskowy 18 cm, kl. 20 — kratka ukośna 45°/135°		

OZNACZENIA LINII

---	elementy nad płaszczyzną cięcia (obrysyt płyt, wsporników, brył wyższych kondygnacji)
---	elementy poniżej płaszczyzny cięcia (widok z góry)
---	osie konstrukcyjne; linia punktowa z pogrubionymi końcami — ślad przekroju

OBJAŚNIENIA I UWAGI

- Wymiary w cm (mm w indeksie górnym, np. 24^h = 24,5 cm), rzędne w m względem ±0,000 = 101,650 m n.p.m. (PL-EVRF2007-NH).
- Rzuty: płaszczyzna cięcia +1,10 m nad posadzką kondygnacji. Linia kreskową — elementy nad płaszczyzną cięcia (obrysyt płyt i wsporników, brył wyższych kondygnacji, otwory w stropie nad, belki); linią cienką — elementy poniżej (widok).
- Otwory: licznik — szerokość, mianownik — wysokość w świetle muru, w nawiasie wysokość parapetu; symbol stolarki wg zestawienia stolarki.
- Numeracja pomieszczeń wg PN-B-01025 / PN-EN ISO 4157-2: <nr> kondygnacji (partier = 1); <nr> <nr>; identyfikator w modelu: <kond>.<nr> (partier = 0).
- Drzwi: strona otwierania (lewej/prawej) wg modelu — patrzeć od strony, w którą otwiera się skrzydło.
- MODEL TESTOWY — rysunek próbny generatorów widoków; dane nie stanowią projektu.
- Rysunek wygenerowany automatycznie z modelu model/test/dom_testowy.yamli (wersja 1.0, 2026-09-25) — generatory lamela.views.

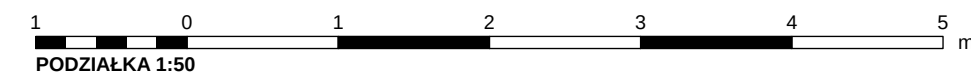

REW.	OPIS ZMIANY				DATA		
0	Próba generatorów widoków z modelu testowego				2026-09-25		
PRACOWNIA PROJEKTOWA PRACOWNIA PROJEKTOWA — nazwa do uzupełnienia adres pracowni do uzupełnienia					STADIUM PB	BRANŻA ARCHITEKTURA (AR)	
INWESTOR (do uzupełnienia)							
OBIEKT / NAZWA ZAMIERZENIA BUDOWLANEGO							
Budynek testowy pipeline'u (model testowy) — NIE jest projektem Domu LAMELA							
ADRES / LOKALIZACJA (NR DZIAŁKI, OBRĘB, JEDN. EWIDENCYJNA) dz. nr ewid. T-1/1, obręb 0000 Testowo						KAT. OBIEKTU I	
FUNKCJA		IMIĘ I NAZWISKO		SPECJALNOŚĆ, NR UPRAWNIEŃ		DATA	PODPIS
Projektant							
Projektant (wsp.)							
Sprawdzający							
Opracował							
TYTUŁ RYSUNKU							
RZUT PARTERU							
SKALA 1:50	FORMAT A3×3	DATA WYDANIA 2026-09-25	RODZAJ DOK. rzut	NR RYSUNKU T-AR-01		ARKUSZ 1/9	REW. 0