


PRZEKRÓJ A-A 1:50

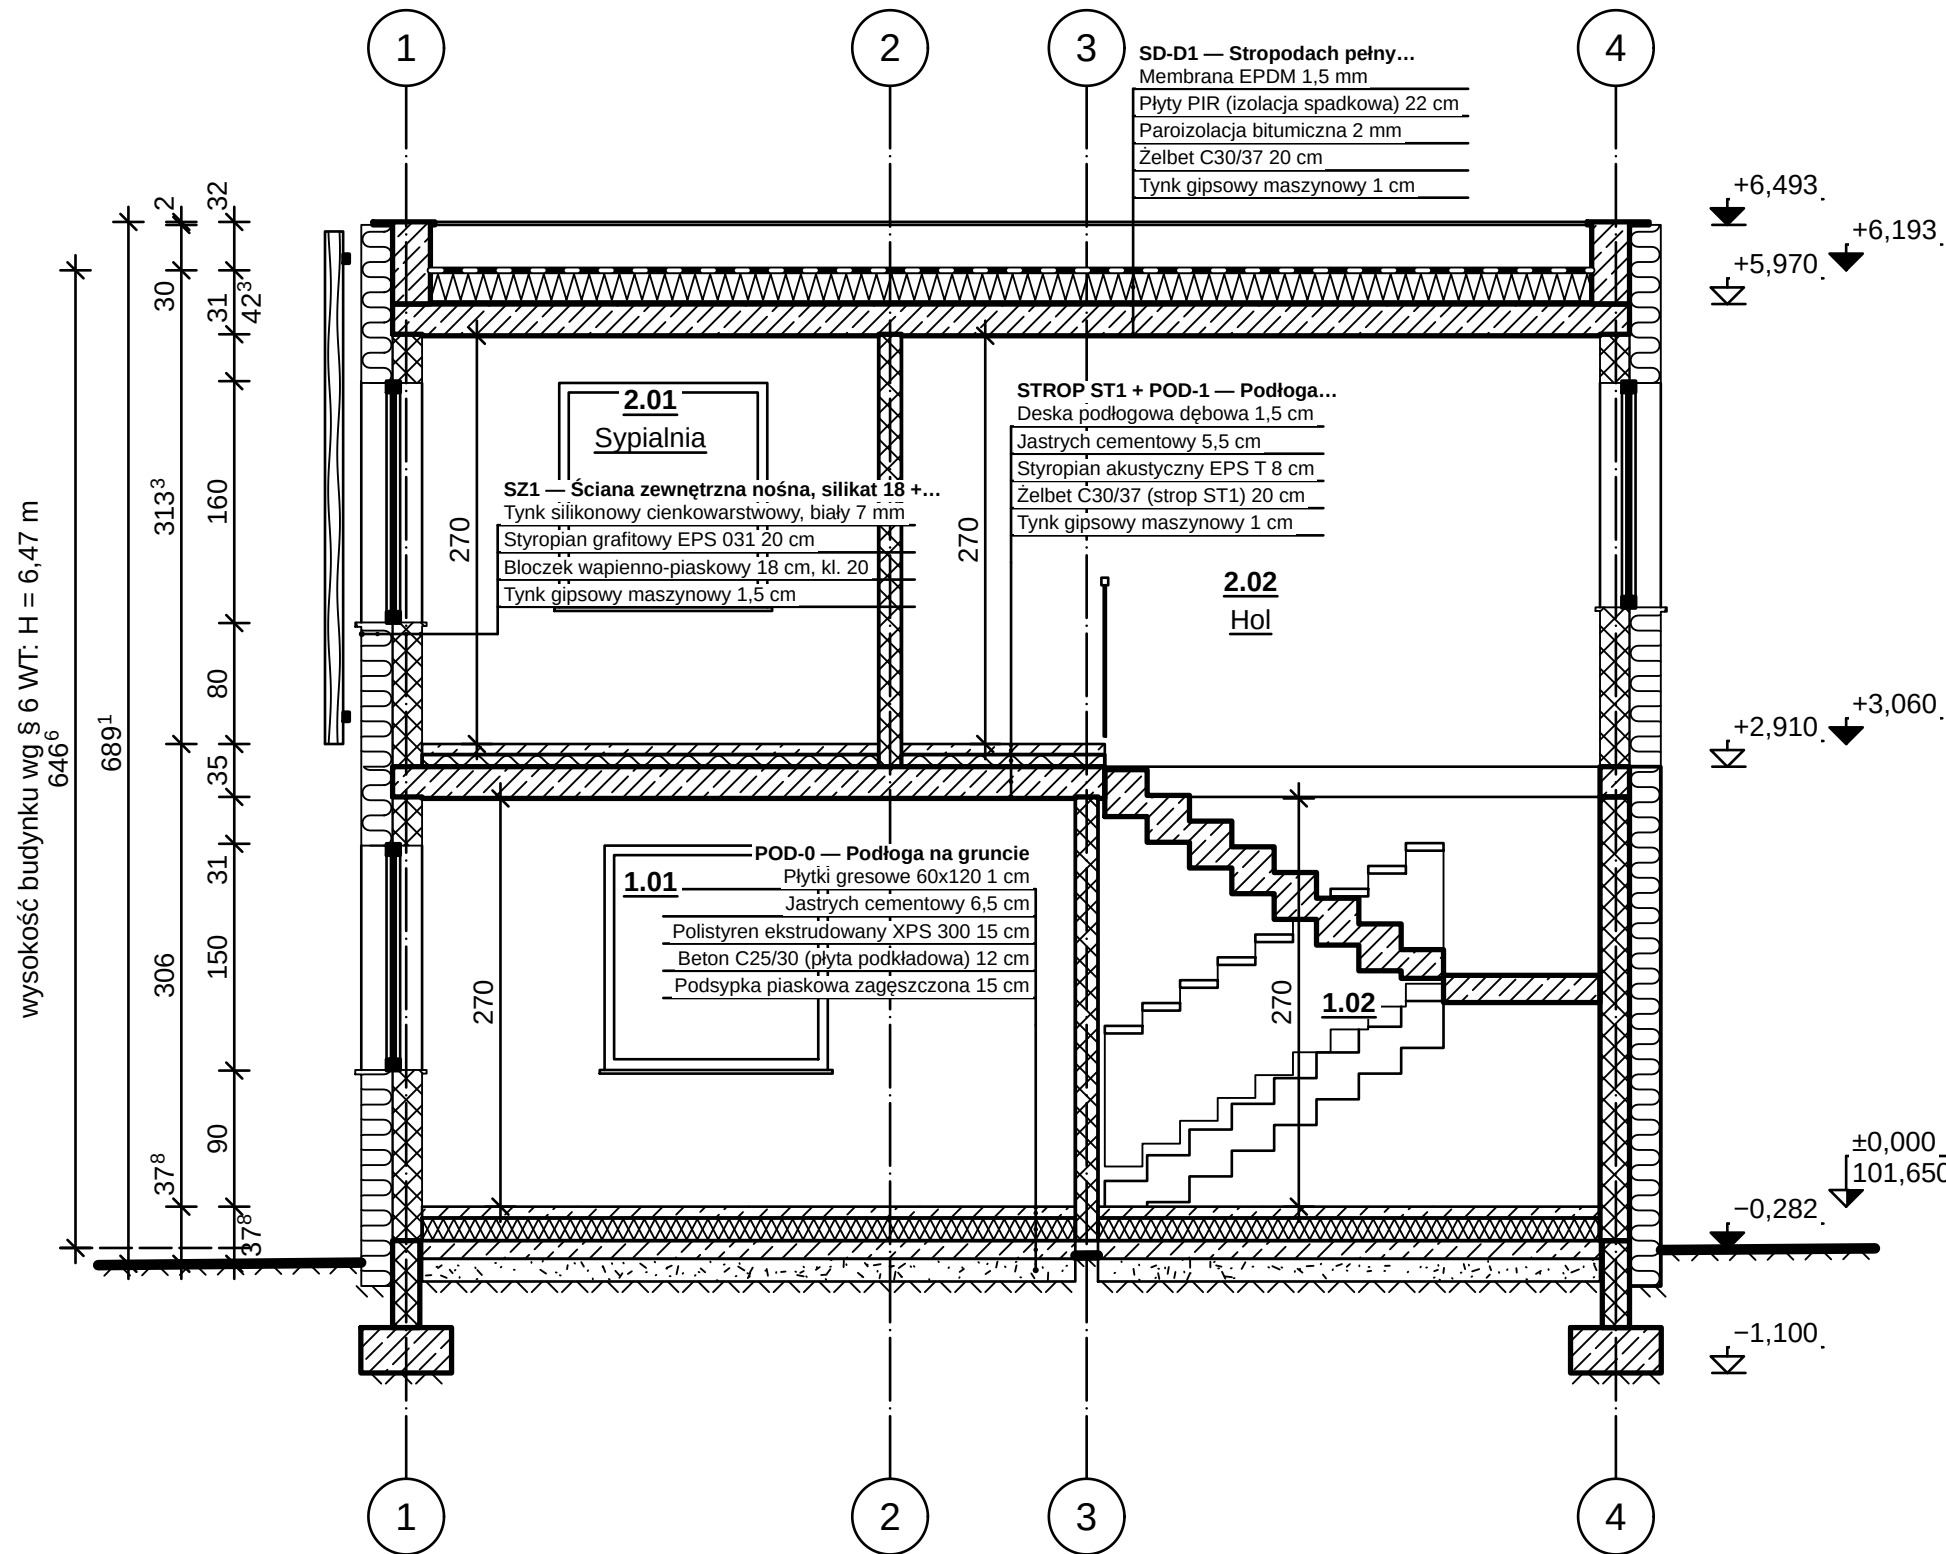


OZNACZENIA MATERIAŁÓW (PN-B-01030 + przyjęte)

	Jastrych cementowy; Beton C25/30 (płyta podkładowa) — 45° przerywane		Polistyren ekstrudowany XPS 300 — zygzak podwójny
	Drewno termojesion (lamelle elewacyjne) — przekrój wzdłuż włókien		Błoczek wapienno-piaskowy 12 cm, kl. 15; Błoczek wapienno-piaskowy 18 cm, kl. 20 — kratka ukośna 45°/135°
	grunt rodzimy		Podsypka piaskowa zagęszczona
	Styropian grafitowy EPS 031; Styropian akustyczny EPS T — meander „UUU”		Paroizolacja bitumiczna — linia kreskowa cienka 3/1 po ciepłej stronie
	Płyty PIR (izolacja spadkowa) — zygzak z okładzinami		Obróbki blacharskie (blacha powlekana); Stolarka — profile aluminiowe, antracyt; Stal malowana proszkowo (balustrady, rygle) — zaczernienie
	Membrana EPDM 1,5 mm — pas czarno-biały		Schody — płyta żelbetowa z okładziną; Żelbet C30/37 — 45° na przemian ciągłe i przerywane

OBJAŚNIENIA I UWAGI

- Wymiary w cm (mm w indeksie górnym, np. 24⁵ = 24,5 cm), rzędne w m względem ±0,000 = 101,650 m n.p.m. (PL-EVRF2007-NH).
- Rzędne: trójkąt zaczerniony — poziom wykończenia, niezaczerniony — konstrukcji, w połowie zaczerniony — poziom ±0,000 z rzędną bezwzględną (PN-B-01025).
- Wysokość budynku wg § 6 WT: od terenu przy najniższej położonym wejściu (−0,273) do wierzchu stropodachu D1 (+6,193) — H = 6,47 m (bez attyk).
- Opisy warstw: kod i nazwa przegrody z modelu, materiały i grubości wg modelu (od góry / od lewej).
- MODEL TESTOWY — rysunek próbny generatorów widoków; dane nie stanowią projektu.
- Rysunek wygenerowany automatycznie z modelu model/test/dom_testowy.yaml (wersja 1.0, 2026-09-25) — generatory lamela.views.

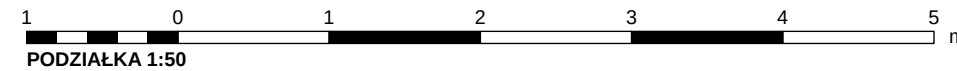

REW.	OPIS ZMIANY			DATA	
0	Próba generatorów widoków z modelu testowego			2026-09-25	
PRACOWNIA PROJEKTOWA PRACOWNIA PROJEKTOWA — nazwa do uzupełnienia adres pracowni do uzupełnienia			STADIUM PB	BRANŻA ARCHITEKTURA (AR)	
INWESTOR (do uzupełnienia)					
OBIEKT / NAZWA ZAMIERZENIA BUDOWLANEGO					
Budynek testowy pipeline'u (model testowy) — NIE jest projektem Domu LAMELA					
ADRES / LOKALIZACJA (NR DZIAŁKI, OBRĘB, JEDN. EWIDENCYJNA) dz. nr ewid. T-1/1, obręb 0000 Testowo				KAT. OBIEKTU I	
FUNKCJA	IMIĘ I NAZWISKO		SPECJALNOŚĆ, NR UPRAWNIEŃ	DATA	PODPIS
Projektant					
Projektant (wsp.)					
Sprawdzający					
Opracował					
TYTUŁ RYSUNKU					
PRZEKRÓJ A-A					
SKALA 1:50	FORMAT A2	DATA WYDANIA 2026-09-25	RODZAJ DOK. przekrój	NR RYSUNKU T-AR-04	ARKUSZ 4/9
					REW. 0