



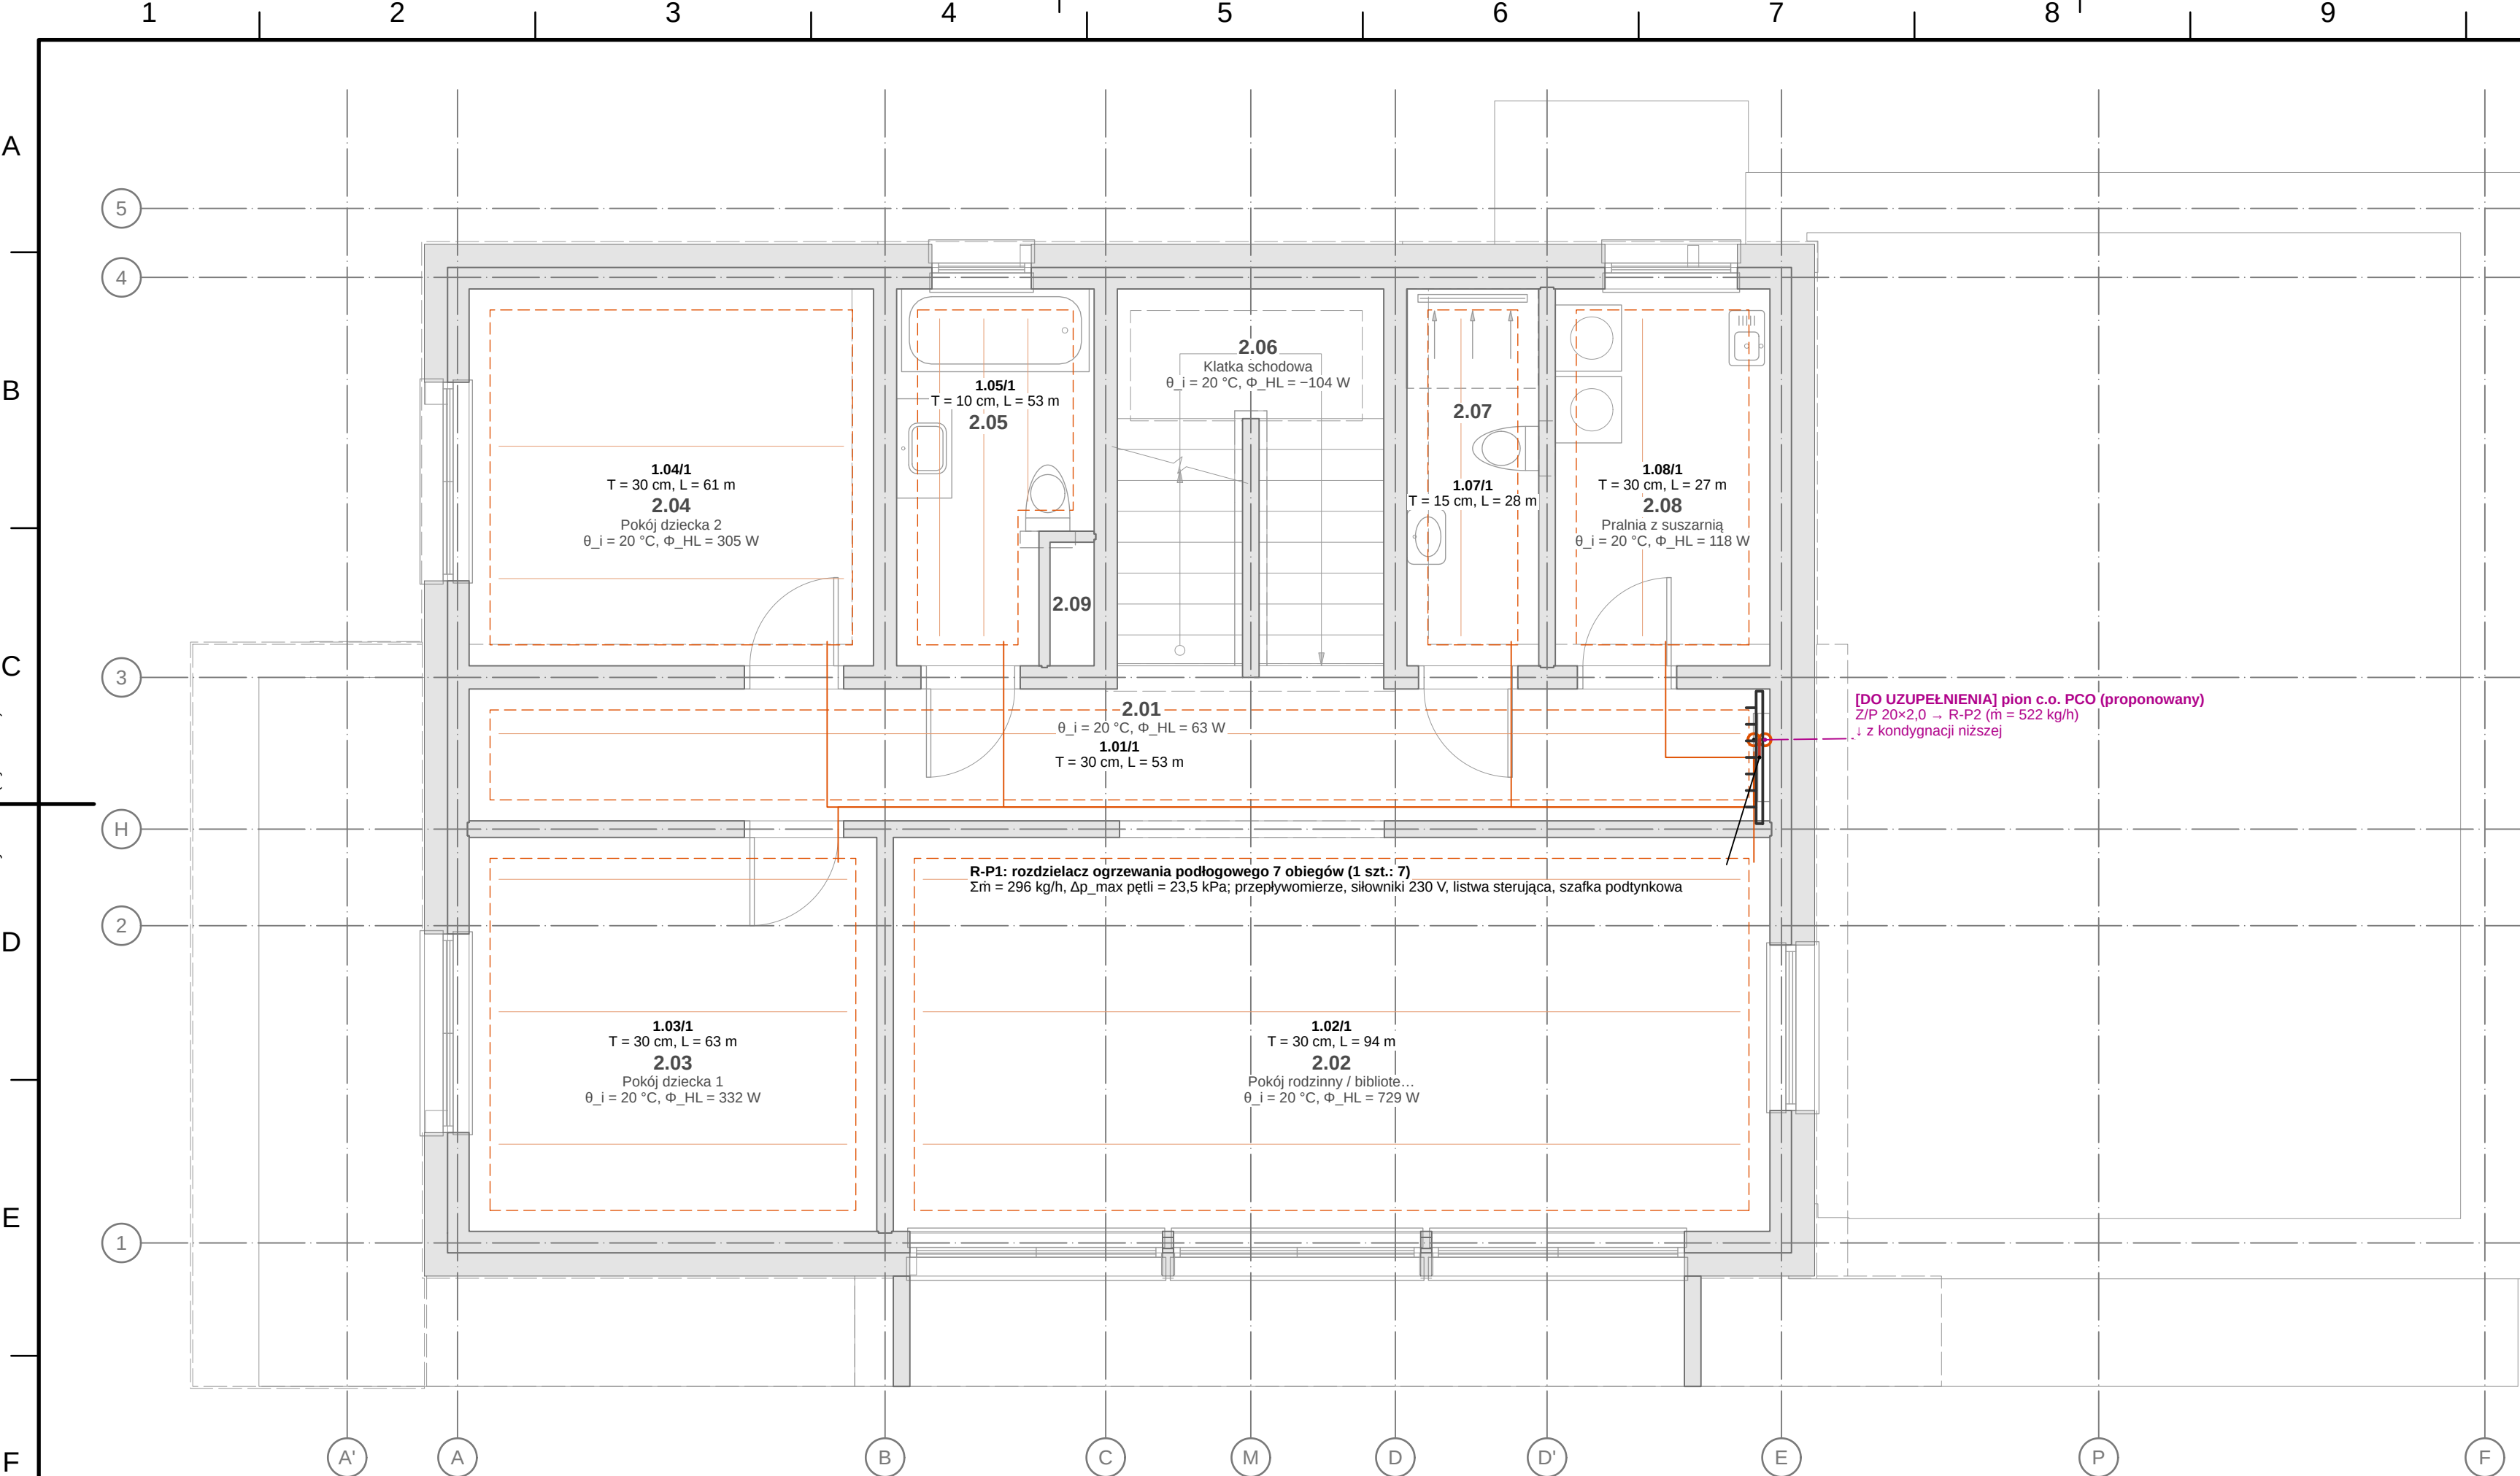

OGRZEWANIE — RZUT I PIĘTRA 1:50

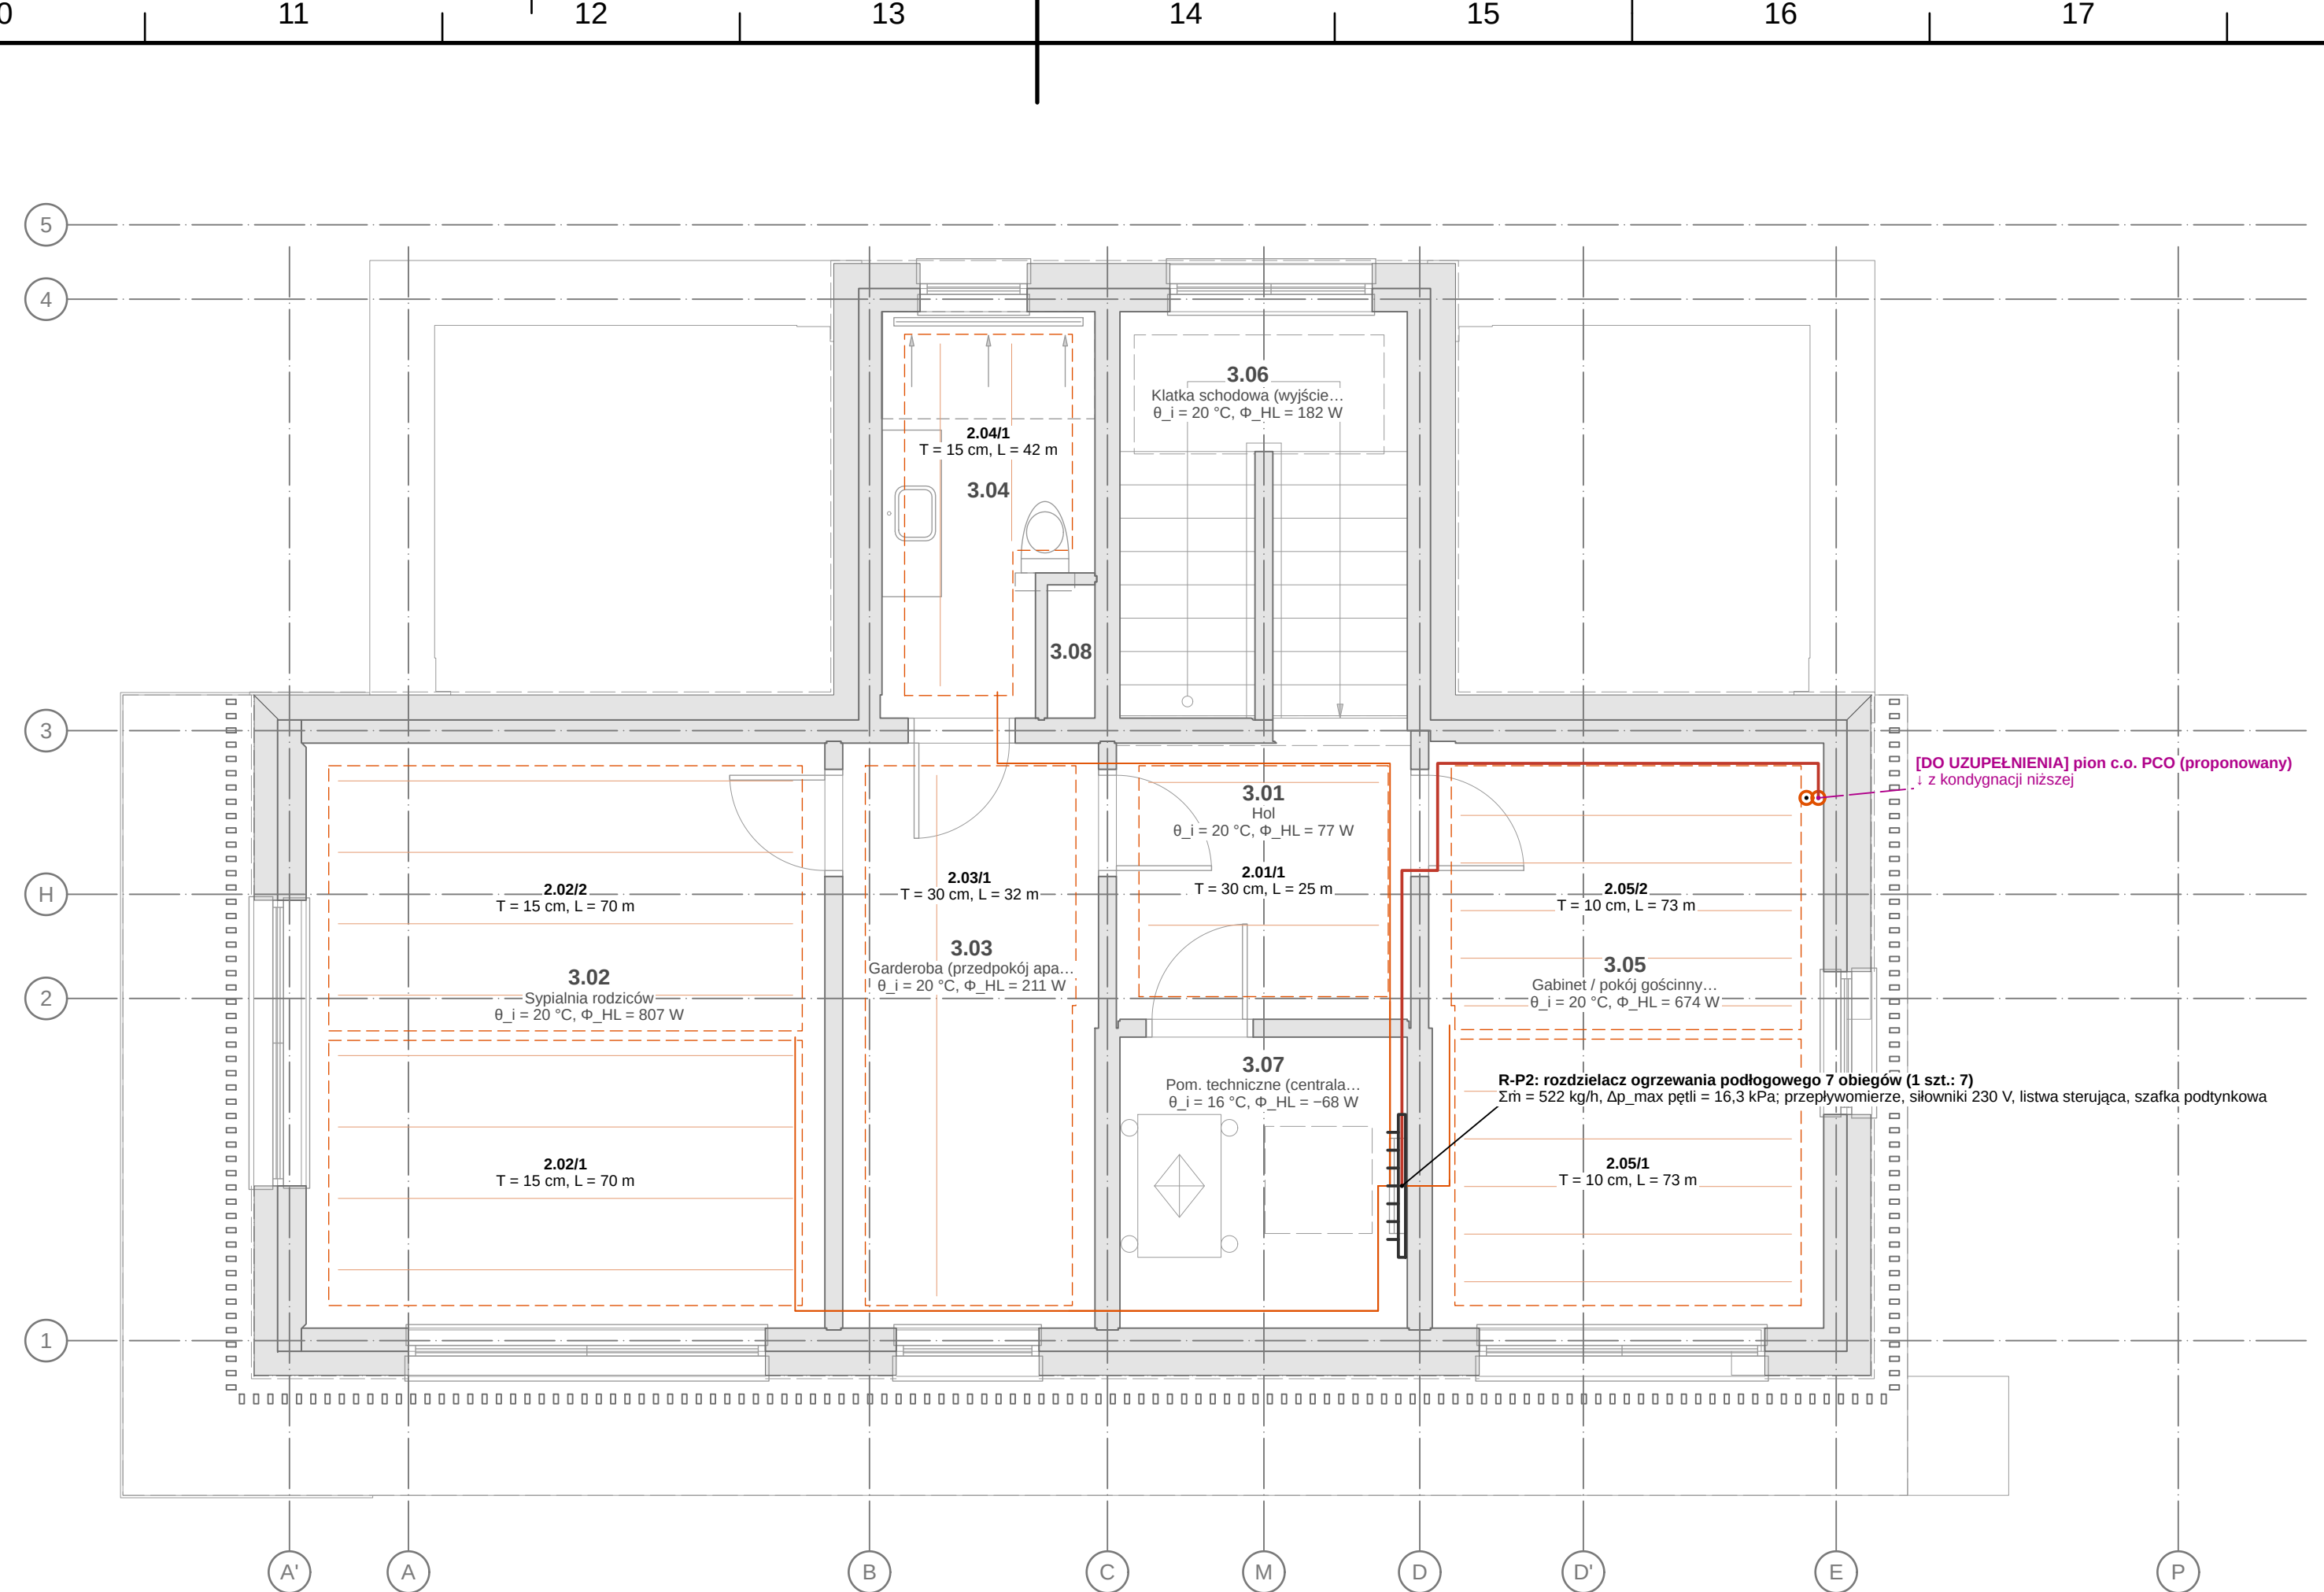

OGRZEWANIE — RZUT II PIĘTRA 1:50

PĘTLE OGRZEWANIA PODŁOGOWEGO — P2 (PN-EN 1264)

Pętla	T [cm]	L [m]	m [kg/h]	Δp [kPa]
2.01/1	30	24,7	6	5,1
2.02/1	15	69,5	111	16,3
2.02/2	15	69,5	111	16,3
2.03/1	30	31,8	59	6,1
2.04/1	15	41,6	49	6,2
2.05/1	10	72,7	93	13,8
2.05/2	10	72,7	93	13,8

OBJAŚNIENIA I UWAGI

- Średnice przewodów w mm (d_z × s — rury wielowarstwowe, Ø/DN — kanalizacja, kanały wentylacyjne), przekroje żył w mm², odległości i rzędne w m; ±0,000 = 101,650 m n.p.m. (PL-EVRF2007-NH).
- Rysunki instalacji na podkładzie rzutu architektury (PB-AR); podkład — linie cienie szare (warstwy I-PODKŁAD).
- Ogrzewanie podłogowe niskotemperaturowe wg PN-EN 1264-1...5, obciążenie cieplne pomieszczeń wg PN-EN 12831-1 (moduł fizyki/energii (PN-EN 12831)); θ_{v,des} = 35,0 °C, α ≤ 5 K; rury PE-X/AlPE-X 16×2 (lub równoważne) na płycie systemowej z izolacją; regulacja pomieszczeniowa — termostaty i siłowniki (WT § 135 ust. 7).
- Strefy pętli (obszar, rozstaw T, długość L) z obliczeń lamela.obliczenia.sanitarnie.ogrzewanie; granice stref i przebieg przyłączy pętli wyznaczono algorytmicznie (podział pomieszczenia na pasy o równych polach, przyłącza ortogonalnie od rozdzielacza) — do uściślenia w projekcie wykonawczym dostawcy systemu.
- Źródło ciepła: PC powietrze-woda R290 (W-155), θ_{b,iv} = -9,6 °C, SCOP 4,7; bufor ≥ 80 dm³, NW c.o. 18 dm³, NW c.w.u. 50 dm³ (obliczenia) — dane PC przykładowe, zastąpić DTR wybranego wyrobu (lub równoważnego).
- Próba szczelności instalacji ogrzewania podłogowego wg PN-EN 1264-4 (przed wylaniem jastrychu, ciśnienie 1,5 × p_{rob} ≥ 6 bar); wygrzewanie jastrychu wg PN-EN 1264-4.
- Rysunek wygenerowany automatycznie z modelu model/budynek.yaml (wersja 1.0, 2026-09-25) — generatory lamela.views.


OZNACZENIA — LEGENDA SYMBOLI

Oznaczenia instalacji sanitarnych — praktyka branżowa (PN-B-01410, PN-B-01411, PN-B-01430 — normy wycofane, bez następcy); armatura i urządzenia wg PN-EN ISO 10628-2 / PN-EN ISO 14617; rodzaje powierzchni wg PN-EN 16798-3 (ODA, SUP, ETA, EHA). Obowiązuje legenda na arkuszu.

— podkład architektoniczny (rzut AR — ściany przecięte, stolarka, wyposażenie) — linie cienie szare
— przyłącza pętli ogrzewania podłogowego (zasilanie/powrót PE-X/AlPE-X 16×2, prowadzone wiązką od rozdzielacza)
— Z/P — przewody zasilania i powrotu c.o. (PC → bufor → rozdzielacz), pion c.o.
— strefa pętli ogrzewania podłogowego <pm>×<nr>; T — rozstaw rur, L — długość pętli (z obliczeń PN-EN 1264); meander symboliczny (co 4 rozstawy)
— pion c.o. (zasilanie/powrót rozdzielczy)
— R — rozdzielacz ogrzewania podłogowego z przepływomierzami i siłownikami

PĘTLE OGRZEWANIA PODŁOGOWEGO — P1 (PN-EN 1264)

Pętla	T [cm]	L [m]	m [kg/h]	Δp [kPa]
1.01/1	30	52,6	4	5,1
1.02/1	30	94,1	124	23,5
1.03/1	30	63,1	52	6,9
1.04/1	30	61,3	44	6,6
1.05/1	10	53,3	33	6,0
1.07/1	15	27,6	31	5,5
1.08/1	30	26,6	8	5,1

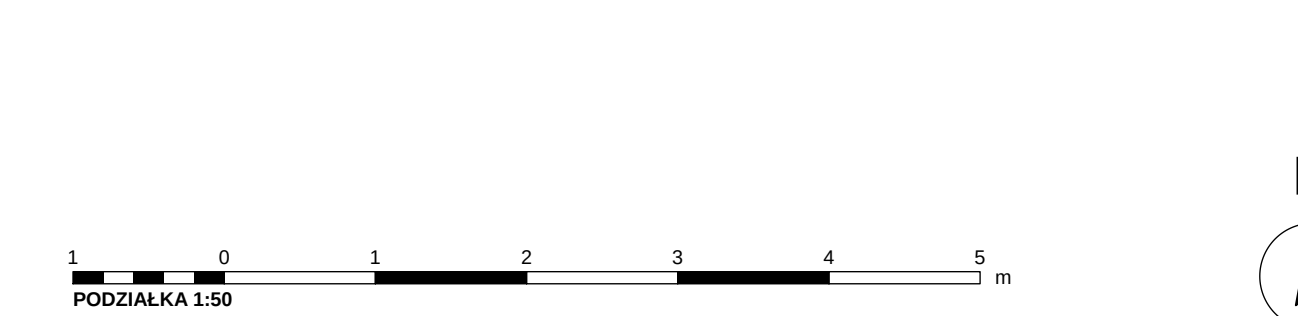

REW.	OPIS ZMIANY	DATA
0	Wydanie — rysunek wygenerowany z modelu	2026-09-25
PRACOWNIA PROJEKTOWA PRACOWNIA PROJEKTOWA — nazwa do uzupełnienia		STADIUM PT
adres pracowni do uzupełnienia		BRANŻA INSTALACJE SANITARNE (IS)
INWESTOR (do uzupełnienia)		
OBIEKT / NAZWA ZAMIERZENIA BUDOWLANEGO Budynek mieszkalny jednorodzinny wolnostojący „Dom LAMELA”		
ADRES / LOKALIZACJA (NR DZIAŁKI, OBRĘB, JEDN. EWIDENCYJNA) ul. Lipowa (fikcyjna), dz. nr ewid. 123/4, obręb 0005 Przykładowo, gm. Przykładowo (fikcyjna)		KAT. OBIEKTU I
FUNKCJA	IMIĘ I NAZWISKO	SPECJALNOŚĆ, NR UPRAWNIEN
Projektant	[DO UZUPEŁNIENIA]	[DO UZUPEŁNIENIA]
Projektant (wsp.)	[DO UZUPEŁNIENIA]	[DO UZUPEŁNIENIA]
Sprawdzający	nie dotyczy (art. 20 ust. 3 pkt 2 PB)	—
Opracował	[DO UZUPEŁNIENIA]	[DO UZUPEŁNIENIA]
TYTUŁ RYSUNKU OGRZEWANIE — RZUTY I PIĘTRA I II PIĘTRA		
SKALA 1:50	FORMAT 1320×297	DATA WYDANIA 2026-09-25
RODZAJ DOK. rzut instalacji	NR RYSUNKU PT-IS-07	ARKUSZ 7/11
REW. 0		