


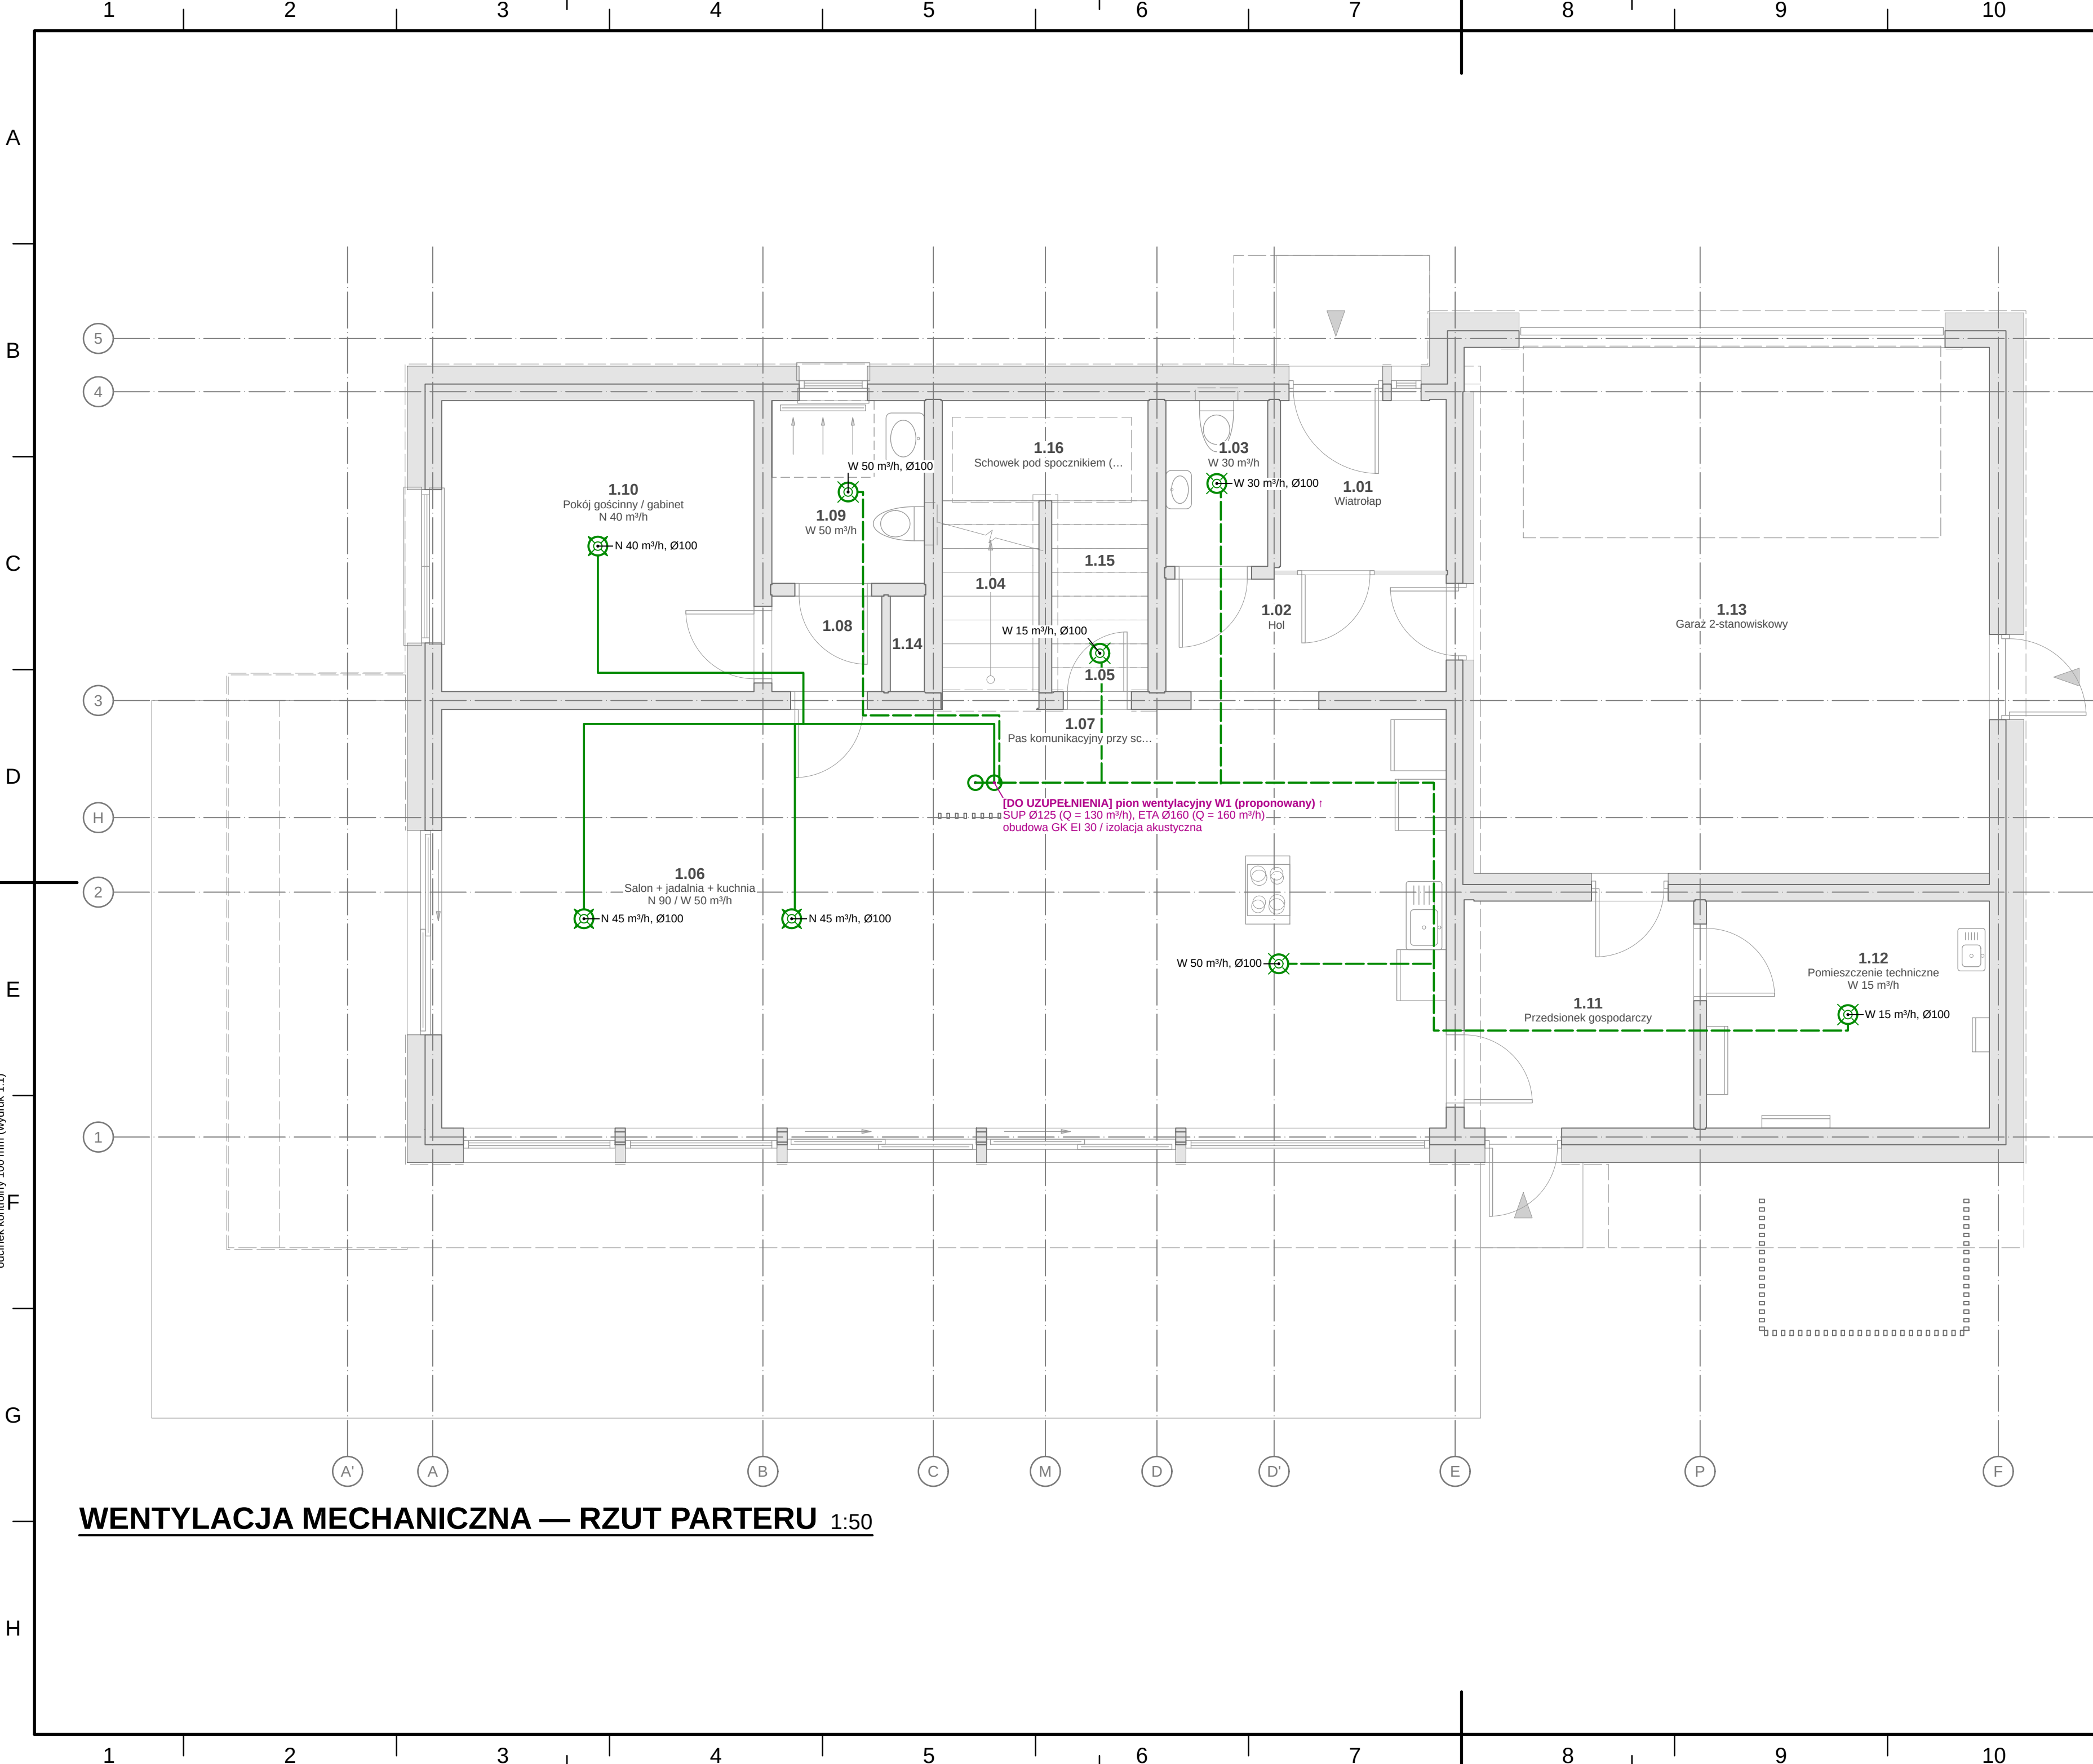

WENTYLACJA MECHANICZNA — RZUT PARTERU 1:50

OZNACZENIA — LEGENDA SYMBOLI

Oznaczenia instalacji sanitarnych — praktyka brązowa (PN-B-01410, PN-B-01411, PN-B-01430 — normy wycofane, bez następcy); armatura i urządzenia wg PN-EN ISO 10628-2 / PN-EN ISO 14617; rodzaje powietrza wg PN-EN 16798-3 (ODA, SUP, ETA, EHA). Obowiązuje legenda na arkuszu.



- podkład architektoniczny (rzut AR — ściany przecięte, stolarka, wyposażenie) — linie cienkie szare
- SUP — powietrze nawiewane (kanały okrągłe, izolowane w przestrzeniach nieogrzewanych)
- ETA — powietrze wywiewane
- nawiewnik (anemostat/zawór nawiewny) — N, wydatek [m³/h], średnica przyłącza
- wywiewnik (zawór wywiewny) — W, wydatek [m³/h]
- pion wentylacyjny (kanał pionowy SUP/ETA)

STRUMIENIE POWIETRZA — P0 [m³/h]

Pom.	Nazwa	Nawiew	Wywiew
0.03	WC gościnne	—	30
0.05	Spiżarnia	—	15
0.06	Salon + jadalnia + kuchnia	90	50
0.09	Łazienka gościnna (natrysk)	—	50
0.10	Pokój gościnny / gabinet	40	—
0.12	Pomieszczenie techniczne	—	15

OBJAŚNIENIA I UWAGI

- Średnice przewodów w mm (d, z×s — rury wielowarstwowe, Ø/DN — kanalizacja, kanały wentylacyjne), przekroje żył w mm², odległości i rzędne w m; ±0,000 = 101,650 m n.p.m. (PL-EVRF2007-NH).
- Rysunki instalacji na podkładzie rzutów architektury (PB-AR); podkład — linie cienkie szare (warstwy I-PODKŁAD*).
- Wentylacja mechaniczna nawiewno-wywiewna z odyskiem ciepła wg WT § 147–150 i PN-EN 16798-3 (oznaczenia ODA/SUP/ETA/EHA); strumienie powietrza z bilansu wentylacji (lamela.obliczenia.energia.wentylacja, PN-B-03430/Az3 powołana w WT § 149) — nawiew do pokoi, wywiew z kuchni, łazienek, WC, pralni, spiżarni.
- Średnice kanałów dobrane dla v ≤ 2,5 m/s (przyłącza) i ≤ 3,5 m/s (pnie); kanały okrągłe stalowe ocynkowane (typu spiro) lub system rozdzielaczy z przewodami elastycznymi (lub równoważne), z tłumikami akustycznymi za centralą; przepływ powietrza między pomieszczeniami przez podcięcia drzwi ≥ 1 cm (przepływ transferowy).
- Trasy kanałów i lokalizację pionu wyznaczono algorytmicznie (ortogonalnie, w przestrzeni sufitów podwieszanych/stropów) — do koordynacji z konstrukcją i architekturą (sufity SUF_GK).
- Kanały ODA i EHA w obrębie budynku — izolacja paroszczelna ≥ 50 mm; kanały SUP/ETA w przestrzeniach nieogrzewanych — izolacja ≥ 50 mm. Okap kuchenny — z recykulacją (filtr węglowy).
- Bilans na rysunkach: Σ nawiew = 365 m³/h, Σ wywiew = 365 m³/h — strumienie = max(model, bilans modułu energii: strumienie z modelu ("pomieszczenia[.went] — sprawdzone: minima, bilans ±10 %, 20 m³/h-os.); nastawy regulacyjne nawiewników wyrównać do bilansu zrównoważonego przy rozruchu (PN-EN 12599).
- Rysunek wygenerowany automatycznie z modelu model/budynek.yaml (wersja 1.0, 2026-09-25) — generatory lamela.views.

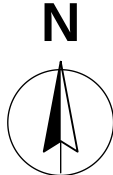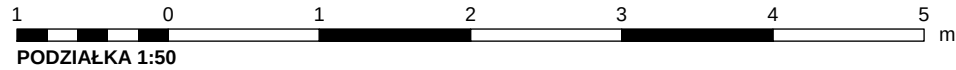

REW.	OPIS ZMIANY			DATA		
0	Wydanie — rysunek wygenerowany z modelu			2026-09-25		
PRACOWNIA PROJEKTOWA PRACOWNIA PROJEKTOWA — nazwa do uzupełnienia adres pracowni do uzupełnienia			STADIUM PT	BRANŻA INSTALACJE SANITARNE (IS)		
INWESTOR (do uzupełnienia)						
OBIEKT / NAZWA ZAMIERZENIA BUDOWLANEGO Budynek mieszkalny jednorodzinny wolnostojący „Dom LAMELA”						
ADRES / LOKALIZACJA (NR DZIAŁKI, OBREB, JEDN. EWIDENCYJNA) ul. Lipowa (fikcyjna), dz. nr ewid. 123/4, obręb 0005 Przykładowo, gm. Przykładowo (fikcyjna)				KAT. OBIEKTU I		
FUNKCJA	IMIĘ I NAZWISKO		SPECJALNOŚĆ, NR UPRAWNIEN		DATA	PODPIS
Projektant	[DO UZUPEŁNIENIA]		[DO UZUPEŁNIENIA]			
Projektant (wsp.)	[DO UZUPEŁNIENIA]		[DO UZUPEŁNIENIA]			
Sprawdzający	nie dotyczy (art. 20 ust. 3 pkt 2 PB)		—			
Opracował	[DO UZUPEŁNIENIA]		[DO UZUPEŁNIENIA]			
TYTUŁ RYSUNKU WENTYLACJA MECHANICZNA — RZUT PARTERU						
SKALA 1:50	FORMAT 710×420	DATA WYDANIA 2026-09-25	RODZAJ DOK rzut instalacji	NR RYSUNKU PT-IS-08		ARKUSZ 8/11
REW.						0