


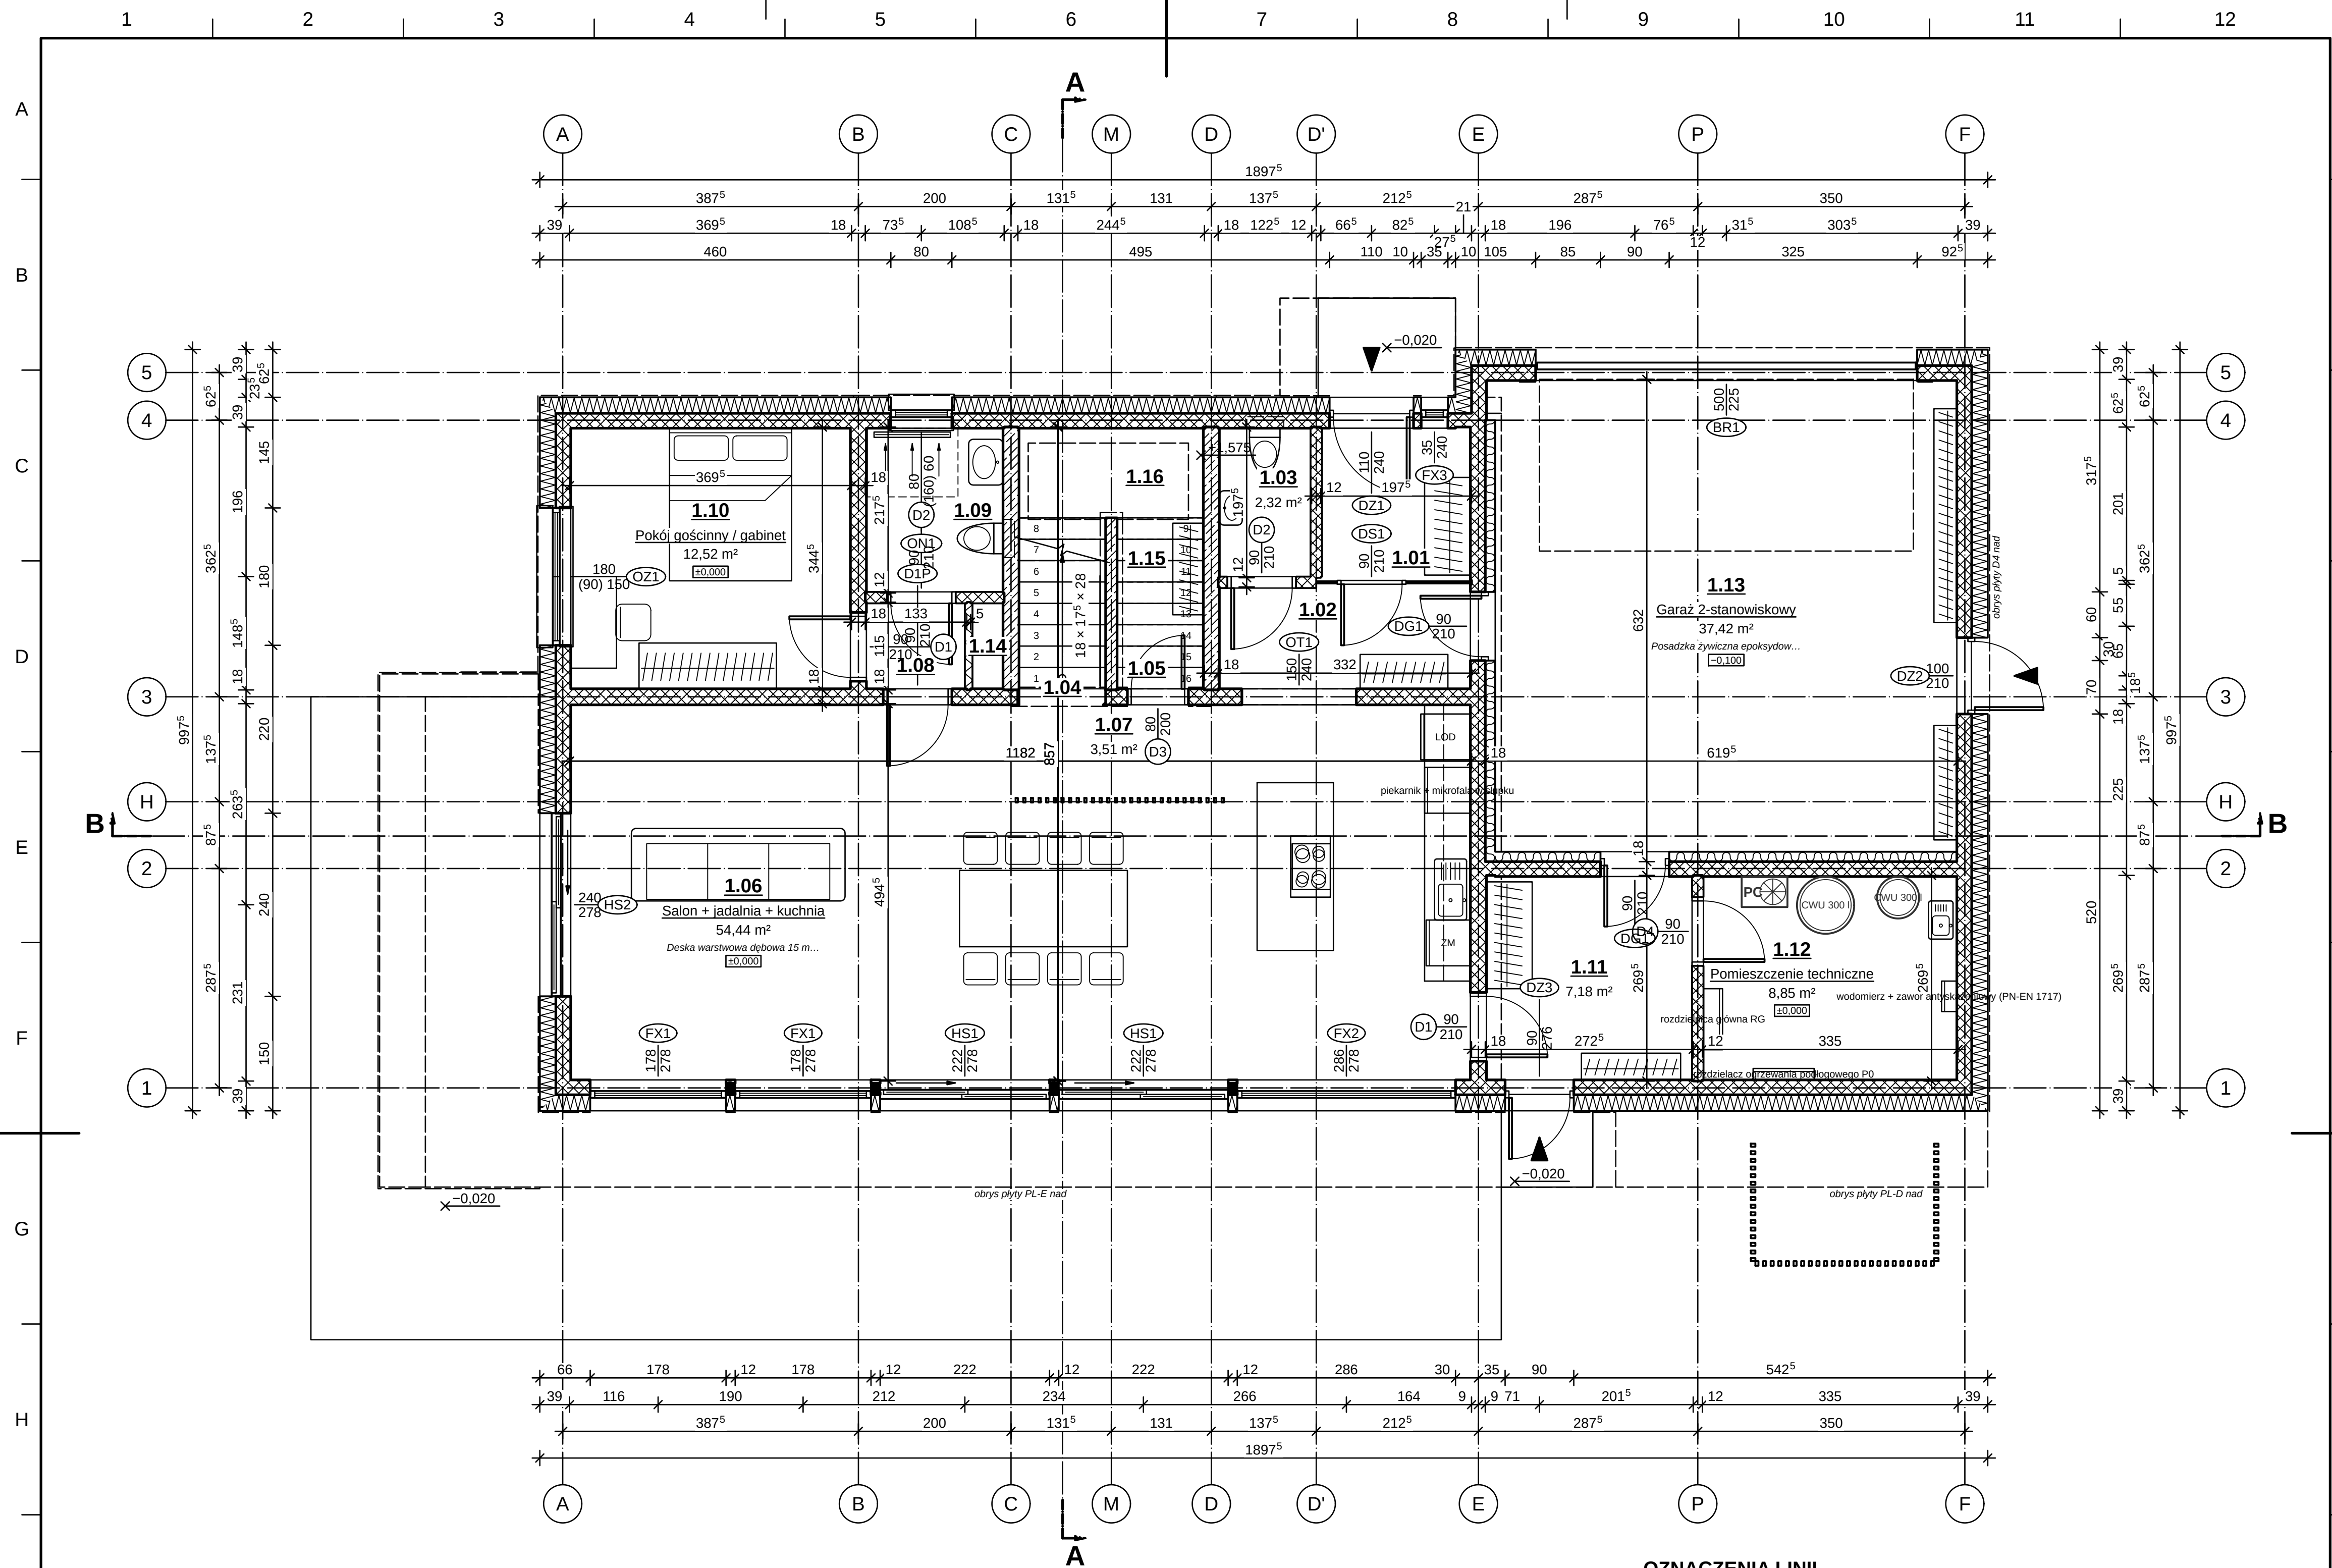

RZUT PARTERU 1:50

- OBJAŚNIENIA I UWAGI**
- Wymiary w cm (mm w indeksie górnym, np. 24⁵ = 24,5 cm), rzędne w m względem ±0,000 = 101,650 m n.p.m. (PL-EVRF2007-NH).
 - Rzuty: płaszczyzna cięcia +1,10 m nad posadzką kondygnacji. Linia kreskową — elementy nad płaszczyzną cięcia (obrysy płyt i wsporników, brył wyższych kondygnacji), otwory w stropie nad, belki); linią cieniłą — elementy poniżej (widok).
 - Otwory: licznik — szerokość, mianownik — wysokość w świetle muru, w nawiasie wysokość parapetu; symbol stolarki wg zestawienia stolarki.
 - Numeracja pomieszczeń wg PN-B-01025 / PN-EN ISO 4157-2: <nr kondygnacji (parter = 1)> <nr>; identyfikator w modelu: <kond> <nr> (parter = 0).
 - Drzwi: strona otwierania (lewe/prawe) wg modelu — patrząc od strony, w którą otwiera się skrzydło.
 - Rysunek wygenerowany automatycznie z modelu modelbudynek.yam1 (wersja 1.0, 2026-09-25) — generatory lamela.views.

ZESTAWIENIE POMIESZCZEŃ



Nr	Nazwa pomieszczenia	Posadzka	Kat.	Wys. [m]	Pow. [m²]
1.06	Salon + jadalnia + kuchnia	Deska warstwowa dębowa 15 mm, klejona	podst.	2,77	54,44
1.13	Garaż 2-stanowiskowy	Posadzka żywiczna epoksydowa antypoślizgowa (garaż)	podst.	2,76	37,42
1.10	Pokój gościnny / gabinet	Deska warstwowa dębowa 15 mm, klejona	podst.	2,77	12,52
1.12	Pomieszczenie techniczne	Płytki gresowe 60x120 na kleju C2TE \$1	techn.	2,76	8,85
1.11	Przedśionek gospodarczy	Płytki gresowe 60x120 na kleju C2TE \$1	ruchu	2,76	7,18
1.02	Hol	Płytki gresowe 60x120 na kleju C2TE \$1	ruchu	2,77	4,44
1.01	Wiatrołap	Płytki gresowe 60x120 na kleju C2TE \$1	ruchu	2,77	3,89
1.09	Łazienka gościnna (natrysk)	Płytki gresowe 60x120 na kleju C2TE \$1	pomoc.	2,77	3,84
1.07	Pas komunikacyjny przy schodach	Deska warstwowa dębowa 15 mm, klejona	ruchu	2,77	3,51
1.16	Schówek pod spocznikiem (h < 1,40)	Płytki gresowe 60x120 na kleju C2TE \$1	pomoc.	1,37	2,91
1.04	Klatka schodowa	Deska warstwowa dębowa 15 mm, klejona	ruchu	2,77	2,78
1.03	WC gościnne	Płytki gresowe 60x120 na kleju C2TE \$1	pomoc.	2,77	2,32
1.15	Schówek pod schodami (h 1,40-2,20)	Płytki gresowe 60x120 na kleju C2TE \$1	pomoc.	1,80	1,45
1.08	Przedpokój gościnny	Deska warstwowa dębowa 15 mm, klejona	ruchu	2,77	1,44
1.05	Spizarnia	Płytki gresowe 60x120 na kleju C2TE \$1	pomoc.	2,77	1,02
1.14	Szacht instalacyjny SI		techn.	2,77	0,45
RAZEM powierzchnia netto					148,45
w tym użytkowa (podst. + pomoc.)					115,91

OZNACZENIA MATERIAŁÓW (PN-B-01030 + przyjęte)

- Wełna mineralna 035 (szkielet, docieplenia, ściana dom-garaż)
— meander „UUU”
Styropian grawitacyjny EPS 031 (ETICS, NRO w systemie) —
zryzek „VVV”
- Stal konstrukcyjna S355 (słupy RK, rama boksu C), cynkowana
ogniowo + malowana proszkowo RAL 7016 — zacierzenie
- Ścianka szklana VSG 2 x 8 mm w ramie aluminiowej (wiatrołap /
hol)
- Błoczek wapienno-piaskowy 12 cm, kl. 15 (ścianki działowe,
licowy w klatce); Błoczek wapienno-piaskowy (silikat) 18 cm, kl.
20, gr. 1, na zaprawie cienkowarstwowej — kratka ukośna
45°/135°
- Żelbet C25/30, B500SP (stropy, płyta fundamentowa, ściany) —
45° na przemian ciagle i przerywane

OZNACZENIA LINII

- elementy nad płaszczyzną cięcia (obrysy płyt, wsporników, brył wyższych kondygnacji)
- elementy poniżej płaszczyzny cięcia (widok z góry)
- osie konstrukcyjne; linia punktowa z pogrubionymi końcami — ślad przekroju

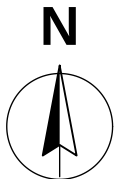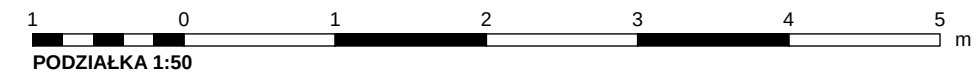

REW.	OPIS ZMIANY	DATA
0	Wydanie — rysunek wygenerowany z modelu	2026-09-25
PRACOWNIA PROJEKTOWA PRACOWNIA PROJEKTOWA — nazwa do uzupełnienia		STADIUM PB
adres pracowni do uzupełnienia		BRANŻA ARCHITEKTURA (AR)
INWESTOR (do uzupełnienia)		
OBIEKT / NAZWA ZAMIERZENIA BUDOWLANEGO Budynek mieszkalny jednorodzinny wolnostojący „Dom LAMELA”		
ADRES / LOKALIZACJA (NR DZIAŁKI, OBRĘB, JEDN. EWIDENCYJNA) ul. Lipowa (fikcyjna), dz. nr ewid. 123/4, obręb 0005 Przykładowo, gm. Przykładowo (fikcyjna)		KAT. OBIEKTU I
FUNKCJA	IMIĘ I NAZWISKO	SPECJALNOŚĆ, NR UPRAWNIEN
Projektant	[DO UZUPEŁNIENIA]	[DO UZUPEŁNIENIA]
Projektant (wsp.)	[DO UZUPEŁNIENIA]	[DO UZUPEŁNIENIA]
Sprawdzający	nie dotyczy (art. 20 ust. 3 pkt 2 PB)	—
Opracował	[DO UZUPEŁNIENIA]	[DO UZUPEŁNIENIA]
TYTUŁ RYSUNKU RZUT PARTERU		
SKALA 1:50	FORMAT 630×594	DATA WYDANIA 2026-09-25
RODZAJ DOK. rzut	NR RYSUNKU PB-AR-01	ARKUSZ 1/5
		REW. 0