


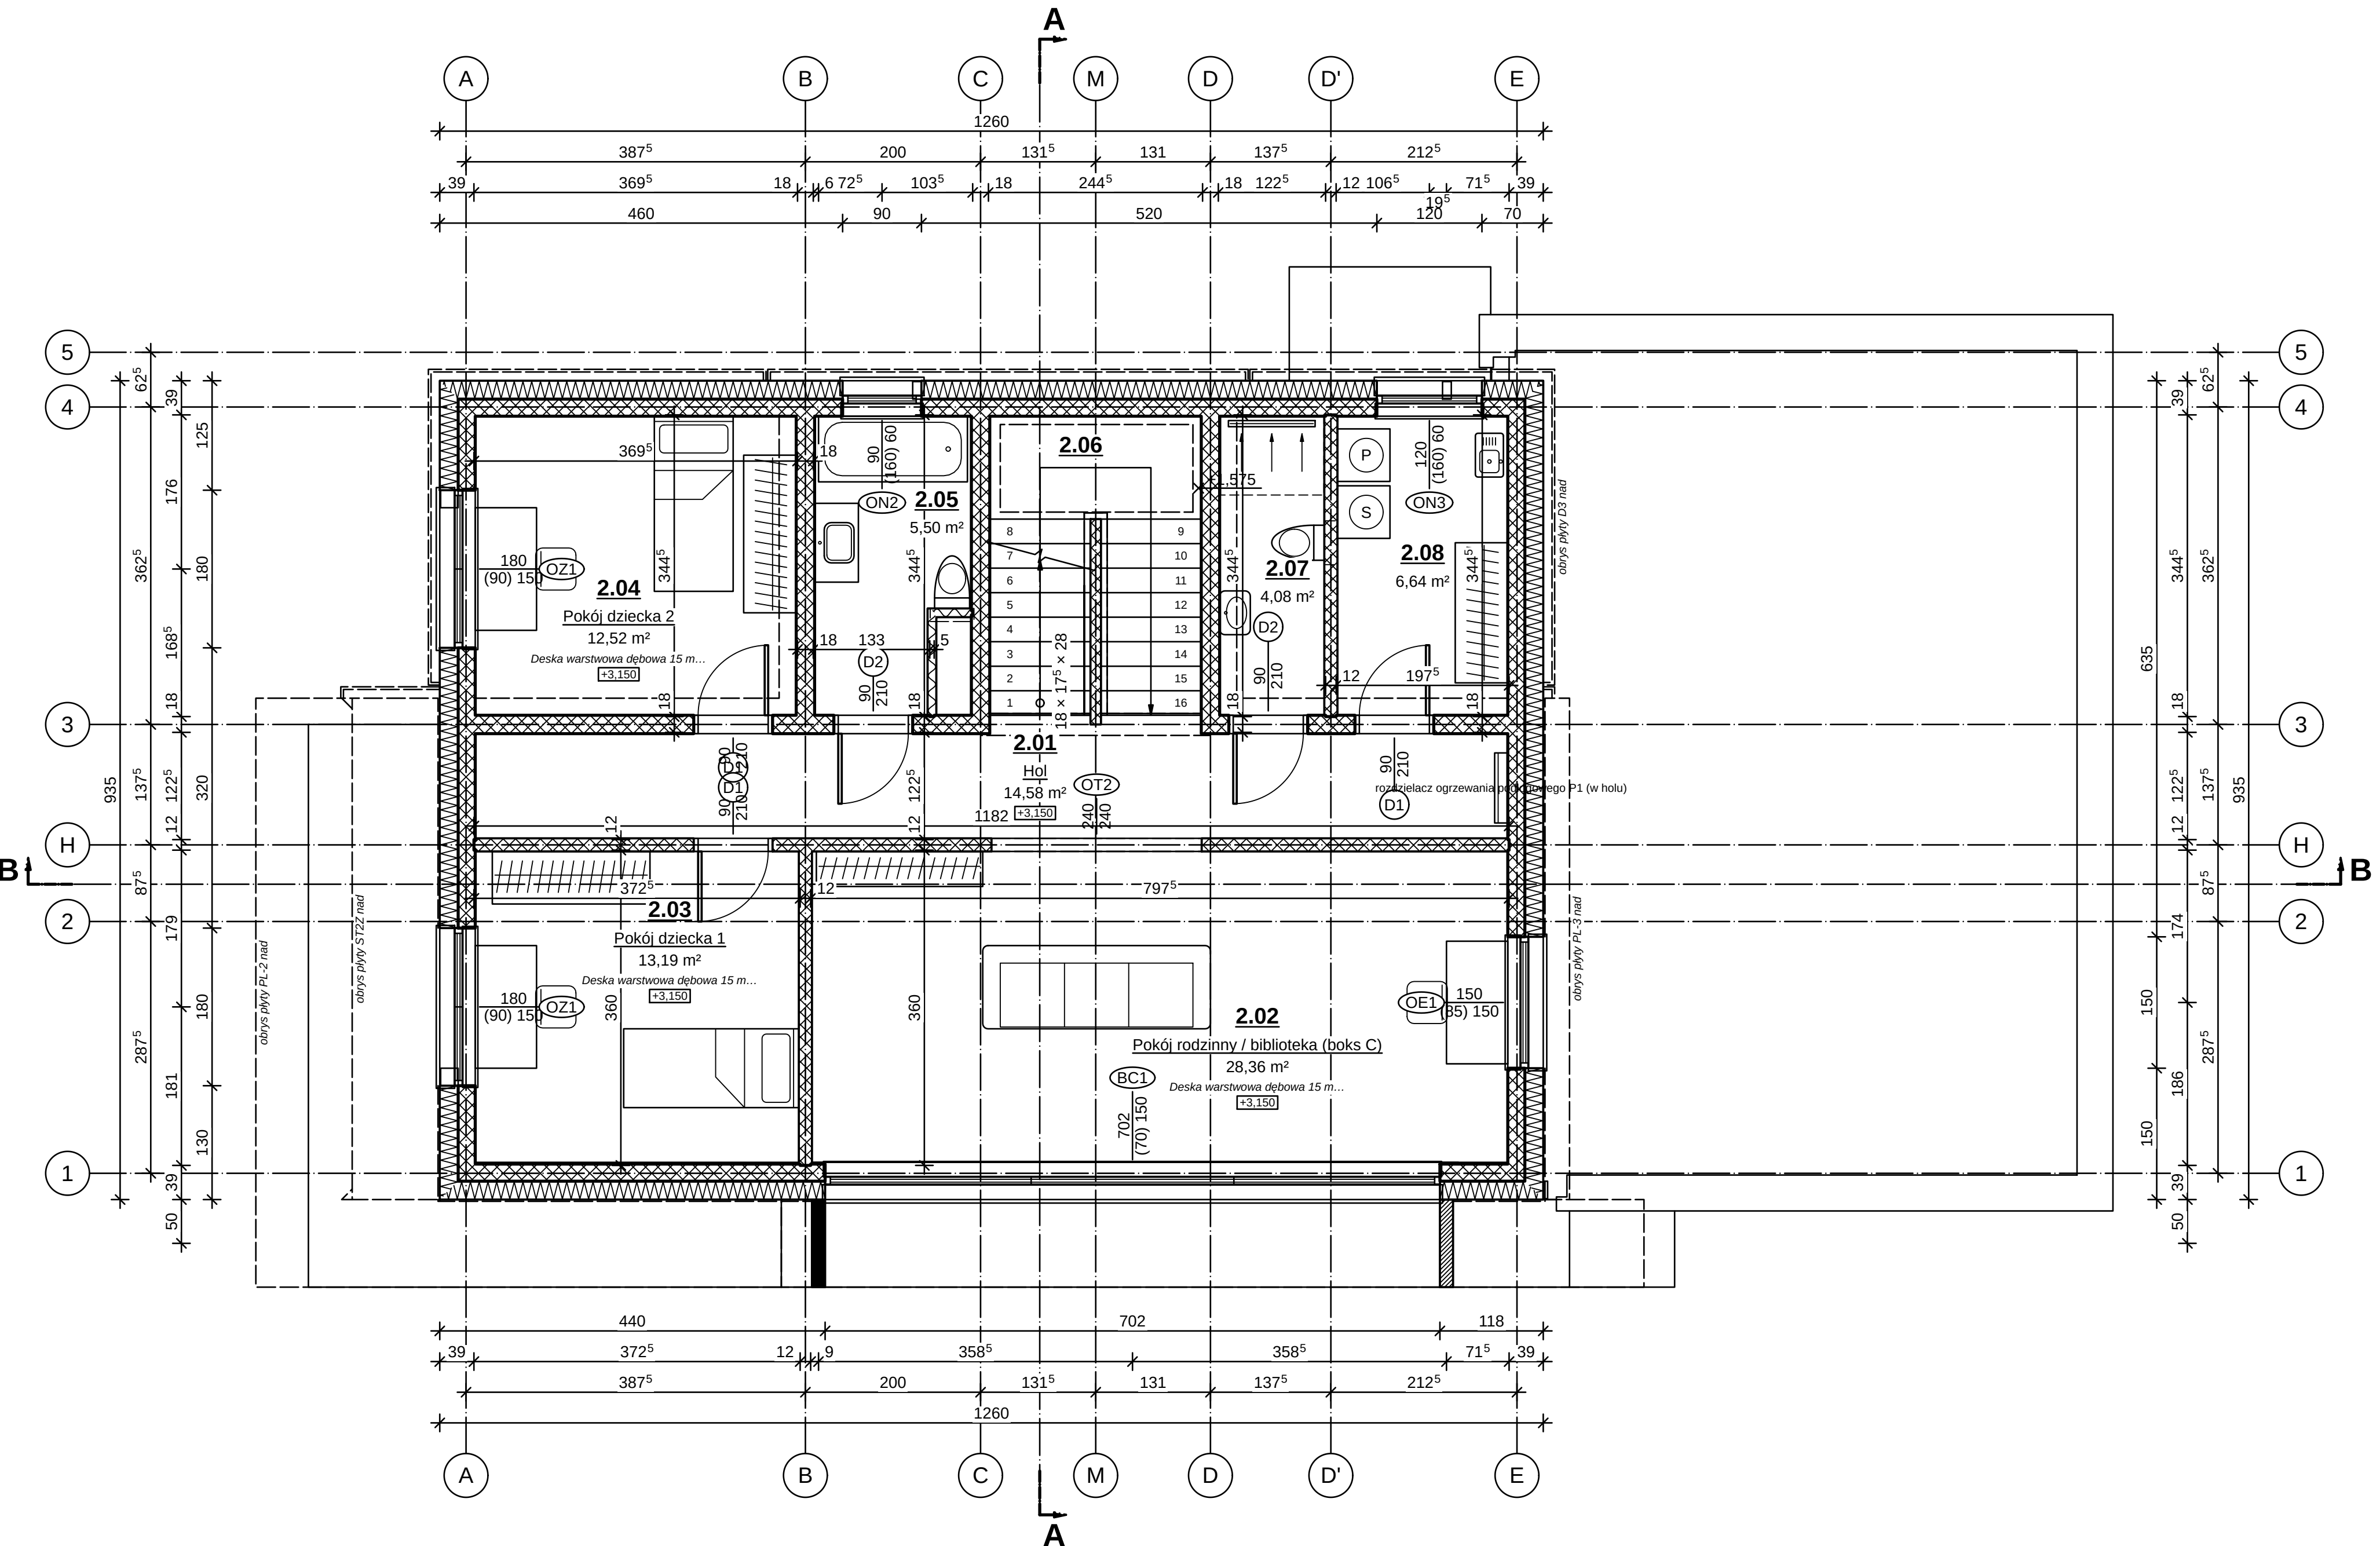


Nr	Nazwa pomieszczenia	Posadzka	Kat.	Wys. [m]	Pow. [m²]
2.02	Pokój rodzinny / biblioteka (boks C)	Deska warstwowa dębowa 15 mm, klejona	podst.	2,77	28,36
2.01	Hol	Deska warstwowa dębowa 15 mm, klejona	ruchu	2,77	14,58
2.03	Pokój dziecka 1	Deska warstwowa dębowa 15 mm, klejona	podst.	2,77	13,19
2.04	Pokój dziecka 2	Deska warstwowa dębowa 15 mm, klejona	podst.	2,77	12,52
2.08	Pralnia z suszarnią	Płytki gresowe 60x120 na kleju C2TE S1	pomoc.	2,77	6,64
2.05	Łazienka dzieci (wanna)	Płytki gresowe 60x120 na kleju C2TE S1	pomoc.	2,77	5,50
2.07	WC z natryskiem	Płytki gresowe 60x120 na kleju C2TE S1	pomoc.	2,77	4,08
2.06	Klatka schodowa	Deska warstwowa dębowa 15 mm, klejona	ruchu	2,77	0,00
	RAZEM powierzchnia netto				84,88
	w tym użytkowa (podst. + pomoc.)				70,30

	Włna mineralna 035 (szkielet, docieplenia, ściana dom-garaż) – meander „VVV”		Blotczyk wapieno-piaskowy 12 cm, kl. 15 (ściana ścianki, bloty w klatce); Blotczyk wapieno-piaskowy (słiskat) 18 cm, kl. 20, gr. 1, na zaprawie cienkowarstwowej – kratka ukośna 45°/135°
	Stropian gipsowy EFS 031 (ETICS, NRO w systemie) – ryzyzak „VVV”		Rama boku C: ruszt stalowy ocynkowany w oddzielnie z blachy aluminiowej RAL 7016 (pusta w środku); Szt konstrukcyjna S355 (kuty RK, rama boku C), cynkowana ocynk + malowana proszkowo RAL 7016 – zaczerpienie

— — — — — elementy nad płaszczyzną cięcia (obrysy płyt, wsporników, brył wyższych kondygnacji)
 ————— elementy poniżej płaszczyzny cięcia (widok z góry)
 — · — · — osie konstrukcyjne; linia punktowa z pogrubionymi końcami — ślad przekroju

1. Wymiary w cm (mm w indeksie górnym, np. 24⁺ = 24,5 cm), rzędne w m względem s.p.m.0 = 101,650 m n.p.m. (PL-EVRF7-2007-NH).
 2. Rzut: płaszczyzna cieką +1,10 m nad posadzką kondygnacji. Linia kropkowana – elementy nad płaszczyzną cieką (obrys był i isoparkiów, brył wyższych kondygnacji, otwory w stropie nad belką, linia kielik – elementy poniżej wysokości).
 3. Symbolizacja: $\square$ – szerokość; $\triangle$ – wysokość; $\circ$ – światło muru; $\diamond$ – światło parawanu; symbol słownika był zestawienia stolarki.
 4. Numeracja pomieszczeń wg PN-B-01:0125 – PN-EN ISO 9176 – kodowania: p[okój] - nr; identyfikator w modelu: <kond>-nr [parter] = nr.
 5. Druki: strona otwierania {ewelpar} wg modelu /patrz: adres url, w której otworzyła się skrzydło.
 6. Rysunek wygenerowany automatycznie z danych z pliku ~/home/user/ajhouse/model/budynek.yaml (wersja 1.0, 2026-09-25) – generatory lamela.view

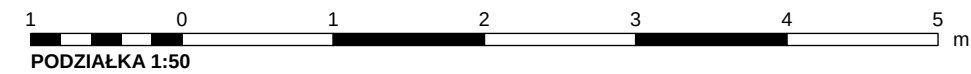

REW.		OPIS ZMIANY		DATA	
0		Wydanie — rysunek wygenerowany z modelu			2026-09-25
PRACOWNIA PROJEKTOWA PRACOWNIA PROJEKTOWA — nazwa do uzupełnienia adres pracowni do uzupełnienia				STADIUM PB	BRANŻA ARCHITEKTURA (AR)
INWESTOR (do uzupełnienia)					
OBIEKT / NAZWA ZAMIERZENIA BUDOWLANEGO					
Budynek mieszkalny jednorodzinny wolnostojący „Dom LAMELA”					
ADRES / LOKALIZACJA (NR DZIAŁKI, OBRĘB, JEDN. EWIDENCYJNA) ul. Lipowa / Łokalizacja, dz. nr ewid. 123/4, obręb 0005 Przykładowo, gm. Przykładowo					KAT. OBIEKTU I
FUNKCJA	IMIĘ I NAZWISKO	SPECJALNOŚĆ, NR UPRAWNIENI		DATA	PODPIS
Projektant					
Projektant (wsp.)					
Sprawdzający					
Opracował					
TYTUŁ RYSUNKU					
RZUT I PIĘTRA					
SKALA 1:50	FORMAT A3×3	DATA WYDANIA 2026-09-25	RODZAJ DOK. rzut	NR RYSUNKU PB-AR-02	ARKUSZ 2/10
					REW. 0