


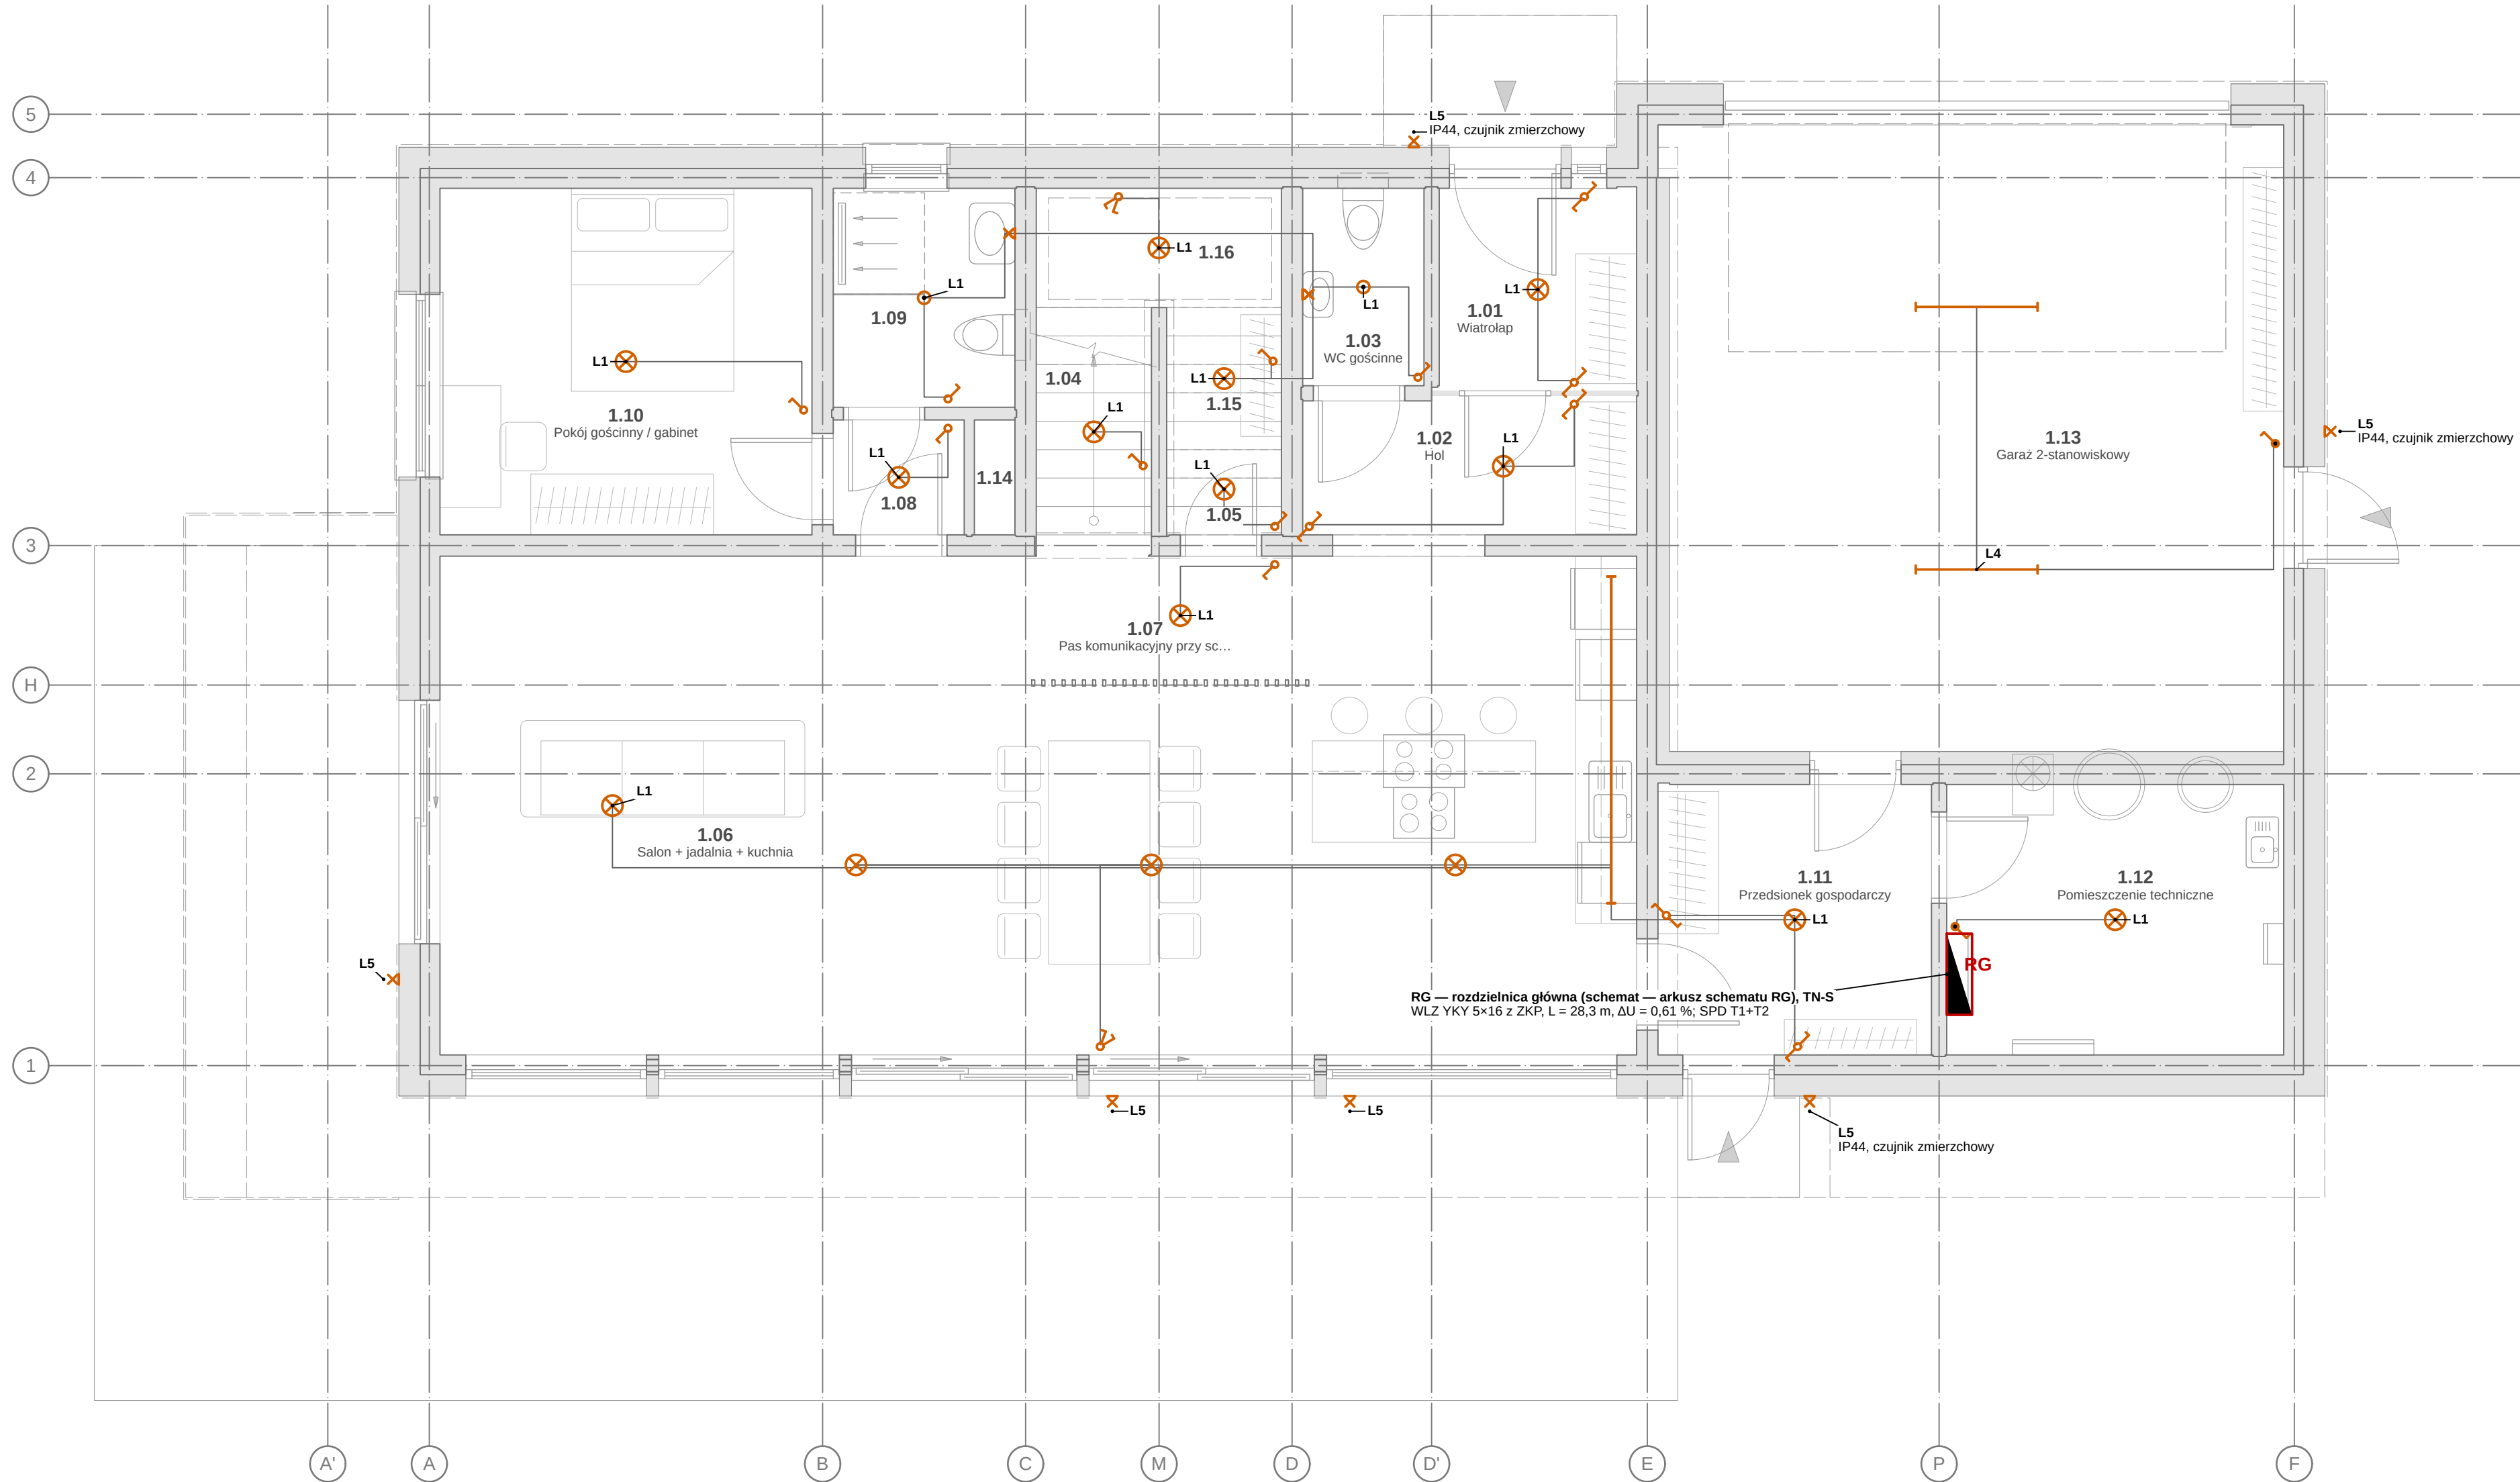

INSTALACJA OŚWIETLENIA — RZUT PARTERU 1:50

OZNACZENIA — LEGENDA SYMBOLI


podkład architektoniczny (rzut AR — ściany przecięte, stolarka, wyposażenie) — linie cienkie szare	oprawa liniowa LED (garaż IP65; pod szafkami kuchennymi)
przewody obwodów oświetlenia YDYp 3×1,5 / 4×1,5 (w tynku, w stropie) — połączenia punktów (przebieg schematyczny)	oprawa wpuszczana (downlight) IP44 — strefy łazienek wg PN-HD 60364-7-701
oprawa oświetleniowa sufitowa (PN-EN 60617-11-15)	wypust / oprawa ścienna (kinkiet), nad lustrem IP44
łącznik jednobiegunowy, h = 1,10 m (IP44 — zaczerpnięty)	łącznik świecznikowy (dwuobwodowy)
łącznik schodowy (przełącznik dwukierunkowy)	RG — rozdzielnica główna (PN-EN IEC 61439-3)

OBWODY NA ARKUSZU (lamela.obliczenia.elektryka.obwody)

Obw.	Odbiorniki	Zab.	Przewód	L [m]	ΔU [%]	Faza	RCD
L1	Oświetlenie P0	B10	YDYp 3×1,5	15,8	1,03	L2	RCBO typ A 30 mA
L4	Oświetlenie garażu i pom. technicznego	B10	YDYp 3×1,5	5,5	0,68	L3	RCBO typ A 30 mA
L5	Oświetlenie zewnętrzne (wejście, elewacje, taras)	B10	YDYp 3×1,5	16,8	0,77	L1	RCBO typ A 30 mA

OBJAŚNIENIA I UWAGI

- Wymiary w cm (mm w indeksie górnym, np. 24^h = 24,5 cm), rzędne w m względem ±0,000 = 101,650 m n.p.m. (PL-EVRF2007-NH).
- Rysunki instalacji na podkładzie rzutów architektury (PB-AR); podkład — linie cienkie szare (warstwy i-PODKŁADY).
- Instalacja oświetlenia wg PN-HD 60364 (seria), WT S 180-186 i S 64 (oświetlenie wejścia); natężenie oświetlenia wg PN-EN 12464-1 (wartości zalecane); obwody i zabezpieczenia z obliczeń (lamela.obliczenia.elektryka); wyłączniki nadprądowe B10, RCBO/RCD 30 mA.
- Rozmieszczenie opraw i łączników wyznaczono algorytmicznie (model nie zawiera punktów elektrycznych); oprawy w siatce ok. 3 m w obrysie pomieszczenia, łączniki przy drzwiach od strony klamki 0,15 m od ościeżnicy na h = 1,10 m; typy opraw — do uzgodnienia z Inwestorem (projekt oświetlenia wnętrza).
- Przewody YDYp 3×1,5 (4×1,5 łączniki schodowe/świecznikowe) w tynku i w warstwach stropu, w strefach instalacyjnych; w łącznikach osprzęt poza strefami 0–1 wg PN-HD 60364-7-701, IP44 w strefie 2.
- Rysunek wygenerowany automatycznie z modelu /home/user/aihouse/model/budynek.yaml (wersja 1.0, 2026-09-25) — generatory lamela.views.

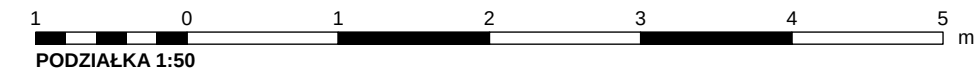

REW.	OPIS ZMIANY	DATA
0	Wydanie — rysunek wygenerowany z modelu	2026-09-25
PRACOWNIA PROJEKTOWA	PRACOWNIA PROJEKTOWA — nazwa do uzupełnienia	STADIUM PT
adres pracowni do uzupełnienia	BRANŻA INSTALACJE ELEKTRYCZNE (IE)	
INWESTOR (do uzupełnienia)	Budynek mieszkalny jednorodzinny wolnostojący „Dom LAMELA”	
OBIĘKT / NAZWA ZAMIERZENIA BUDOWLANEGO		
ADRES / LOKALIZACJA (NR DZIAŁKI, OBRĘB, JEDN. EWIDENCYJNA) ul. Lipowa (fikcyjna), dz. nr ewid. 123/4, obręb 0005 Przykładowo, gm. Przykładowo (fikcyjna)	KAT. OBIĘKTU I	
FUNKCJA	IMIĘ I NAZWISKO	SPECJALNOŚĆ, NR UPRAWNIENI
Projektant	DATA	PODPIS
Projektant (wsp.)		
Sprawdzający		
Opracował		
TYTUŁ RYSUNKU	INSTALACJA OŚWIETLENIA — RZUT PARTERU	
SKALA 1:50	FORMAT A3×3	DATA WYDANIA 2026-09-25
RODZAJ DOK. rzut instalacji	NR RYSUNKU PT-IE-01	ARKUSZ 1/14
REW. 0		