


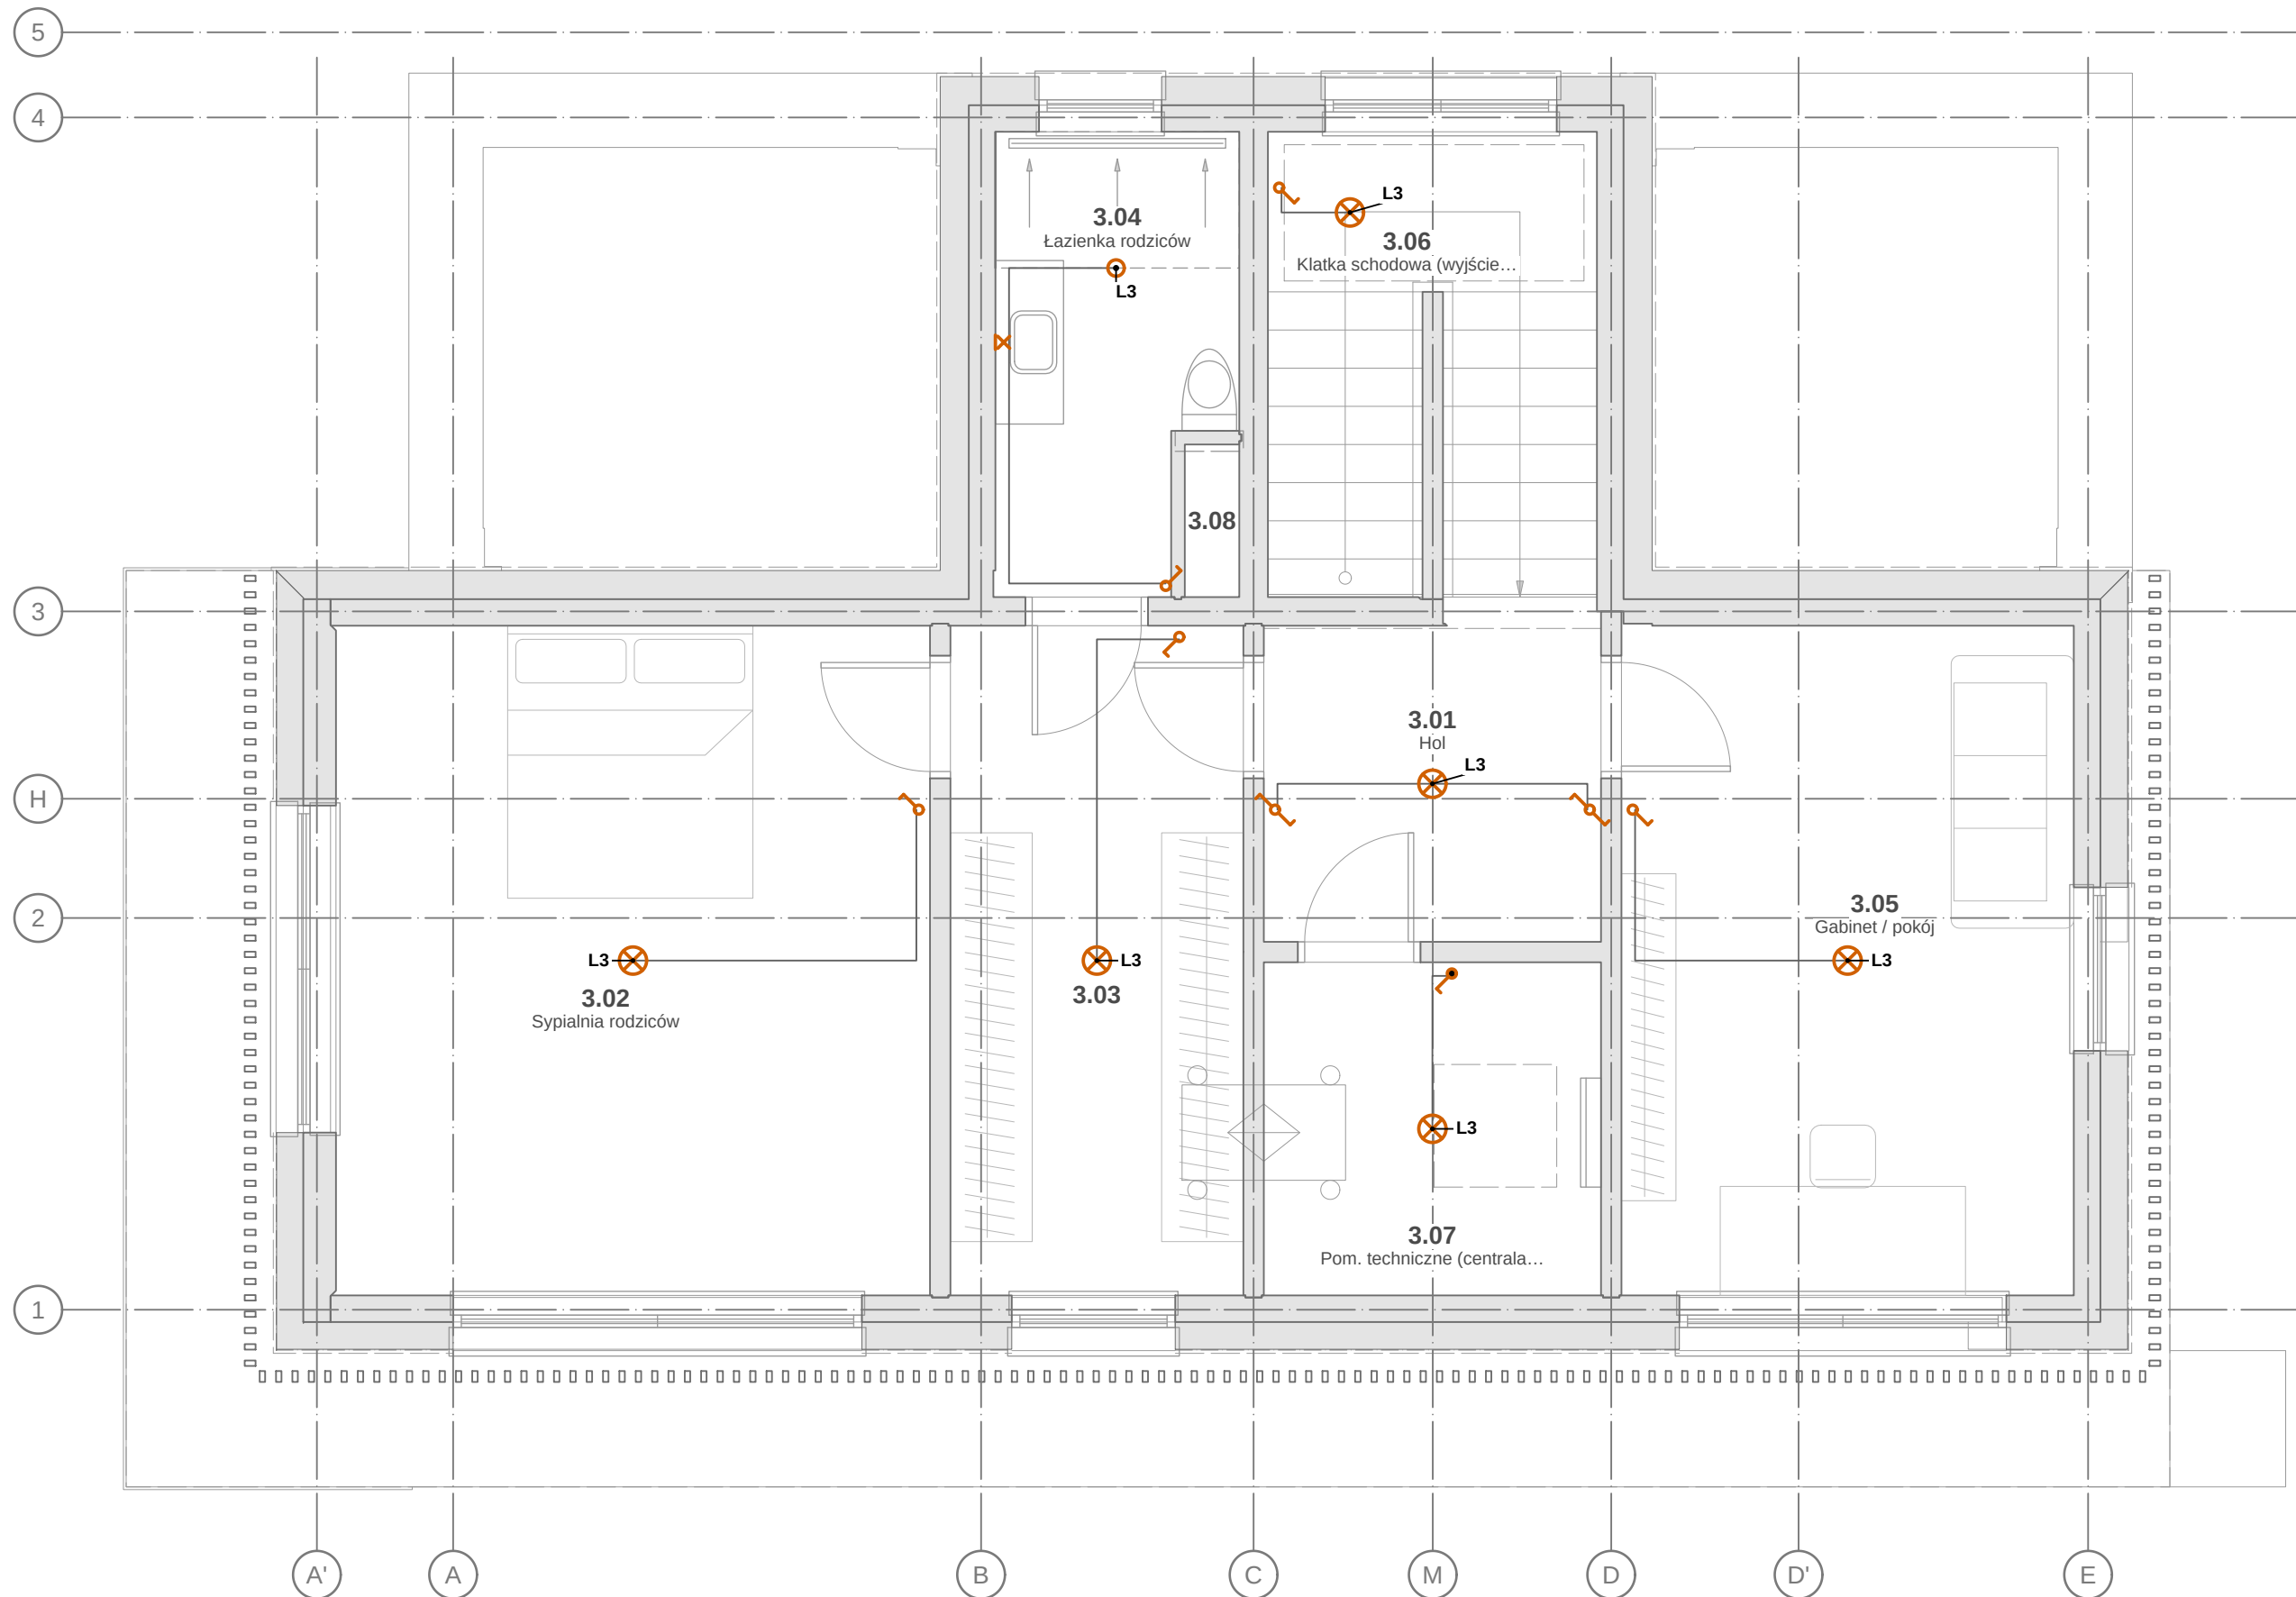

## OZNACZENIA — LEGENDA SYMBOLI

- |                                                                                     |   |                                                                                     |                                                                          |
|-------------------------------------------------------------------------------------|---|-------------------------------------------------------------------------------------|--------------------------------------------------------------------------|
|                                                                                     | podkład architektoniczny (rzut AR — ściany przecięcie, stolarka, wyposażenie) — linie cienkie szare        |  | łącznik schodowy (przełącznik dwukierunkowy)                             |
|                                                                                     | przewody oświetlenia YDYg 3x1,5 / 4x1,5 (w tynku, w stropie) — połączenia punktowe (przebieg schematyczny) |  | oprawa wpuszczana (downlight) IP44 — strefy łazienek w PN-HD 60364-7-701 |
|  | oprawa oświetleniowa sufitowa (PN-EN 60617-11-15)                                                          |  | wypust / oprawa ścienna (kinkiet), nad lustrem IP44                      |
|  | łącznik jednobiegunowy, h = 1,10 m (IP44 — zaznaczony)                                                     |                                                                                     |                                                                          |

## OBWODY NA ARKUSZU (lamela.obliczenia.elektryka.obwody)

| Obw. | Odbiorniki     | Zab. | Przewód    | L [m] | $\Delta U$ [%] | Faza | RCD              |
|------|----------------|------|------------|-------|----------------|------|------------------|
| L3   | Oświetlenie P2 | B10  | YDYp 3x1,5 | 27,8  | 1,05           | L2   | RCBO typ A 30 mA |

## OBJAŚNIENIA I UWAGI

1. Wymiar y cm (mm w indeksie górnym, np. 24" = 24,5 cm), rzędne w m względem zrostu (warstw) 101,650 m n.p.m. (PL-EVPR7027-NH).
2. Rysunki instalacji na podłożach rzek i potoków (PB-AR), podkład – linie cieniarsze sąsiadujące (warstwa I+PODKŁAD).
3. Instalacja oświetlenia wg PN-HD 60364 (seria), WT 5 i 180–185 i 84 (oświetlenie wejścia); natężenie oświetlenia wg PN-EN 12464-1 (wartości zalecane); oświetlenie zewnętrzne – oświetlenie zewnętrzne – oświetlenie zewnętrzne – oświetlenie zewnętrzne – oświetlenie zewnętrzne.
4. Rozmieszczenie oprawy i łączników wzbudzenia (oświetlenie nie zawiera punktu elektrycznego); oprawy w słatce ok. 1 m w wysięgu pomieszczenia, łączniki przy drzwiach od strony klatki 0,15 m od ościeżnicy na h = 1,10 m; typy oprawy – do uzgodnienia z Inwestorem (projekt oświetlenia).
5. Rozmieszczenie i wytyczenie linii i słupów (1x1,5 m) w warstwach stropu, w strzechach instalacji, w klatkach osprzęt. (projekt oświetlenia).
6. Rysunek wygenerowany automatycznie z modelu `home/user/aihouse/model/budynki.yaml` (wersja 1.0, 2026-09-25) – generatory lamela.wy.



|   |                                         |                                   |                                |                                              |                          |
|---|-----------------------------------------|-----------------------------------|--------------------------------|----------------------------------------------|--------------------------|
| REW.   | OPIS ZMIANY                             |                                   |                                | DATA                                         |                          |
| 0   | Wydanie — rysunek wygenerowany z modelu |                                   |                                | 2026-09-25                                   |                          |
| PRACOWNIA PROJEKTOWA   |                                         |                                   | STADIUM<br><b>PT</b>           | BRANŻA<br><b>INSTALACJE ELEKTRYCZNE (IE)</b> |                          |
| PRACOWNIA PROJEKTOWA — nazwa do uzupełnienia<br>adres pracowni do uzupełnienia                                                                              |                                         |                                   |                                |                                              |                          |
| INWESTOR<br>(do uzupełnienia)   |                                         |                                   |                                |                                              |                          |
| OBIEKT / NAZWA ZAMIERZENIA BUDOWLANEGO   |                                         |                                   |                                |                                              |                          |
| Budynek mieszkalny jednorodzinny wolnostojący „Dom LAMELA”                                                                                                  |                                         |                                   |                                |                                              |                          |
| ADRES / LOKALIZACJA (NR DZIAŁKI, OBRĘB, JEDN. EWIDENCYJNA)<br>ul. Lipowa (fikcyjna), dz. nr ewid. 123/4, obręb 0005 Przykładowo, gm. Przykładowo (fikcyjna) |                                         |                                   |                                |                                              | KAT. OBIEKTU<br><b>I</b> |
| FUNKCJA   | IMIĘ I NAZWISKO                         |                                   | SPECJALNOŚĆ, NR UPRAWNIENI     | DATA                                         | PODPIS                   |
| Projektant   |                                         |                                   |                                |                                              |                          |
| Projektant (wsp.)   |                                         |                                   |                                |                                              |                          |
| Sprawdzający   |                                         |                                   |                                |                                              |                          |
| Opracował   |                                         |                                   |                                |                                              |                          |
| TYTUŁ RYSUNKU   |                                         |                                   |                                |                                              |                          |
| INSTALACJA OŚWIETLENIA — RZUT II PIĘTRA   |                                         |                                   |                                |                                              |                          |
| SKALA<br><b>1:50</b>   | FORMAT<br><b>A3×3</b>                   | DATA WYDANIA<br><b>2026-09-25</b> | RODZAJ DOK.<br>rzut instalacji | NR RYSUNKU<br><b>PT-IE-03</b>                | ARKUSZ<br><b>3/14</b>    |
|   |                                         |                                   |                                |                                              | REW.<br><b>0</b>         |