


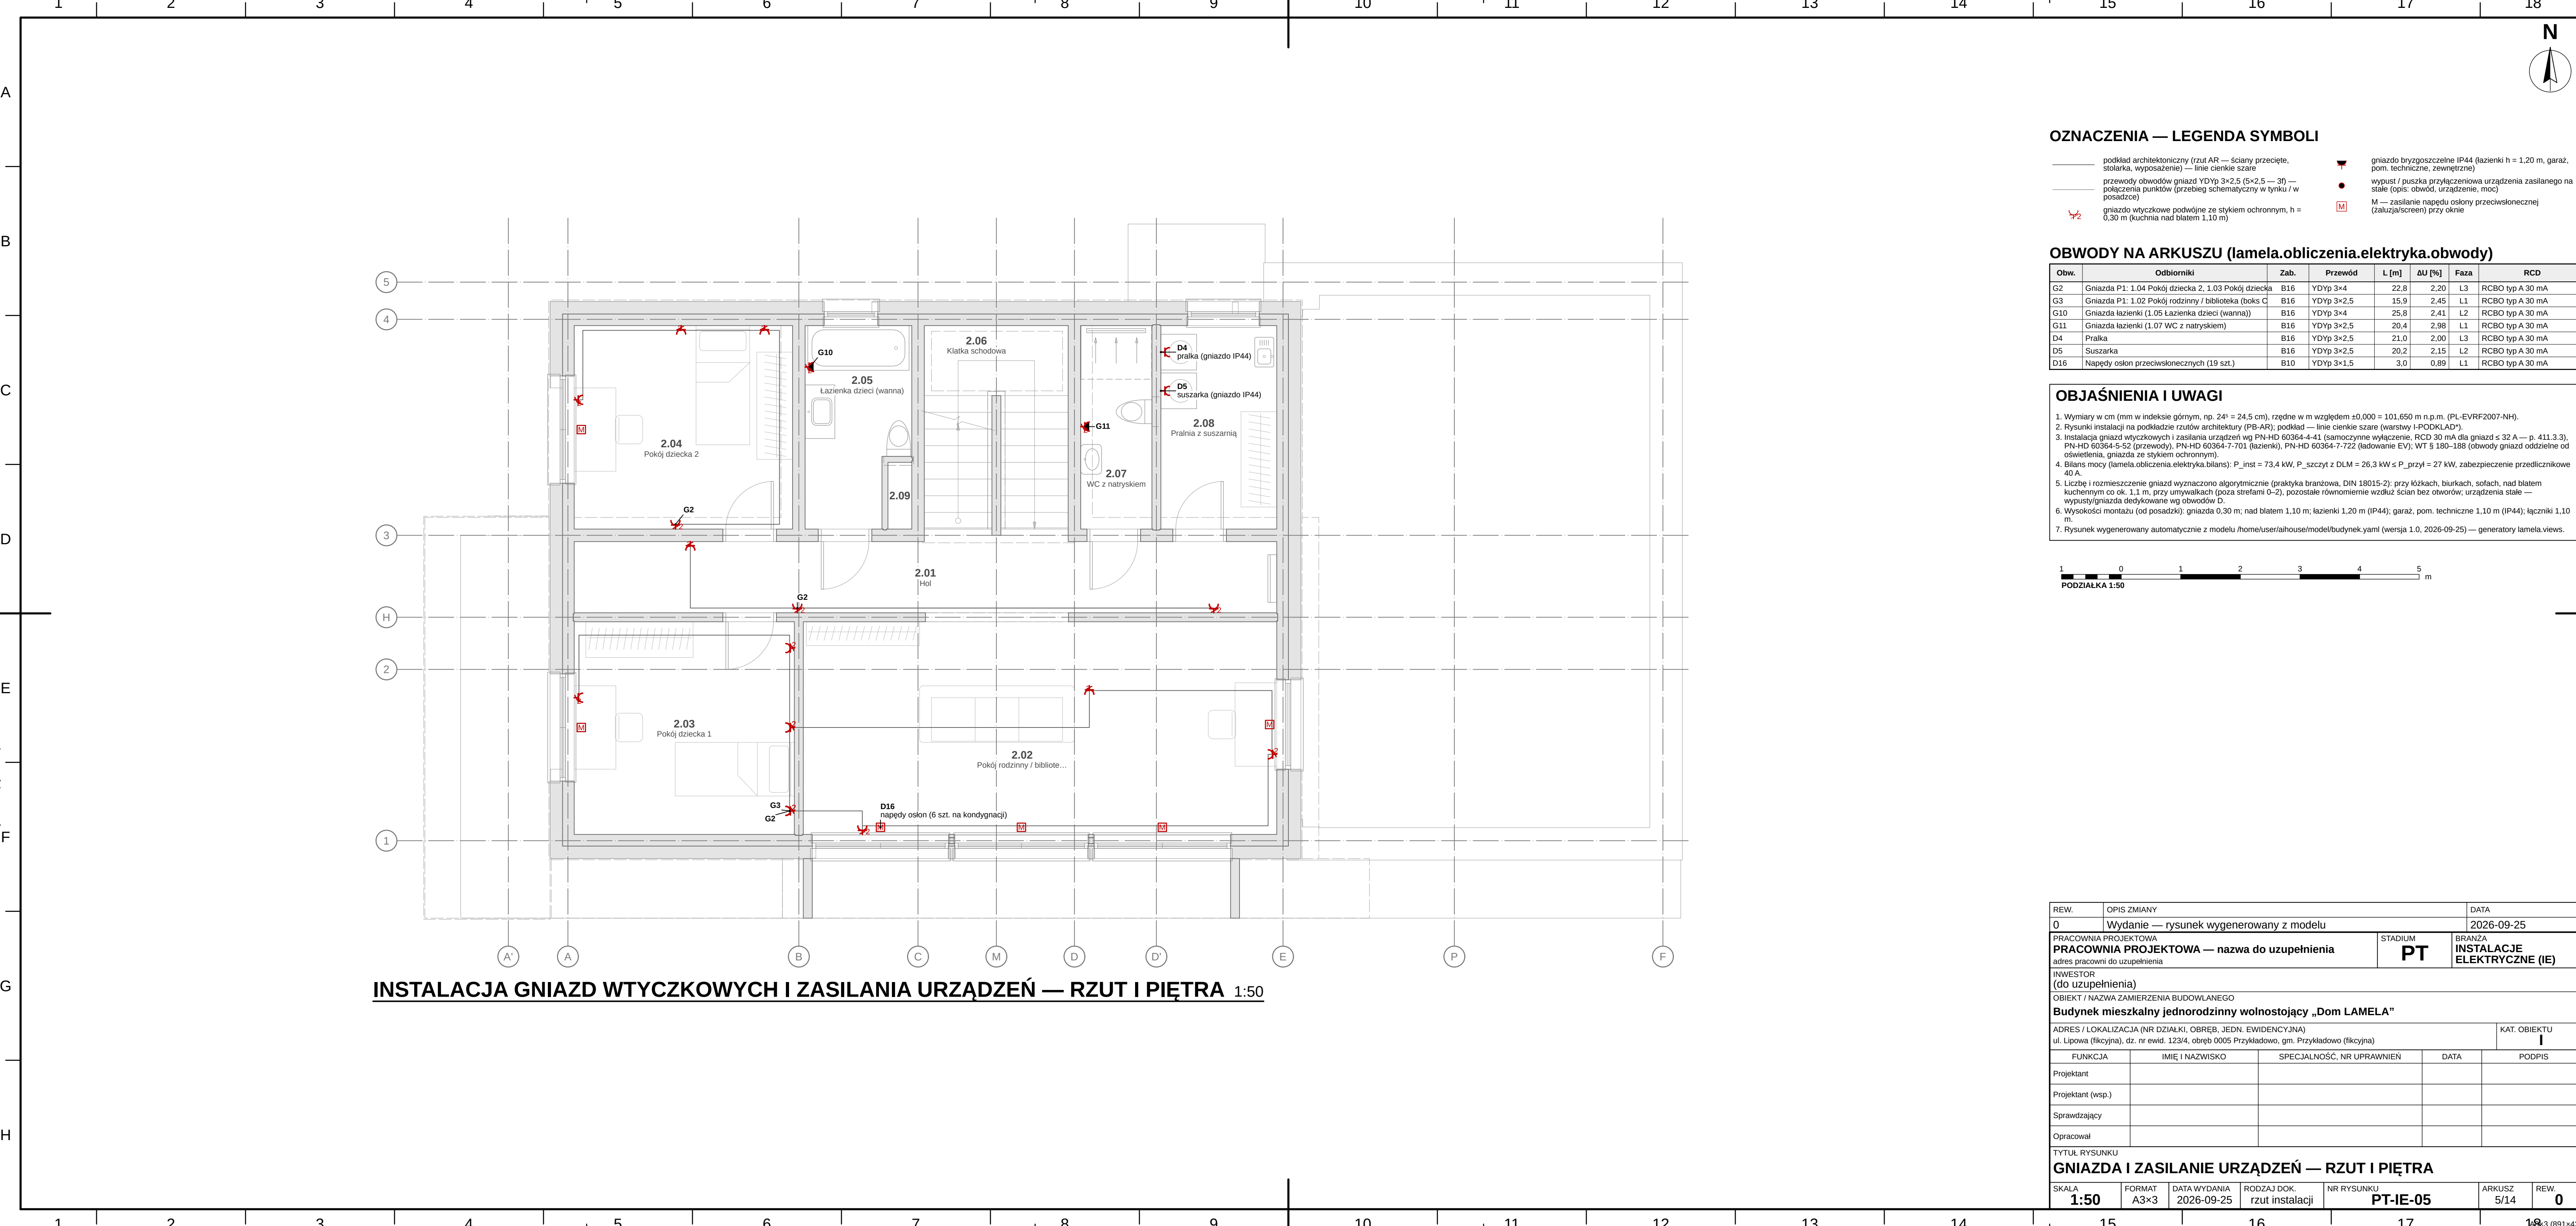

odcinek kontynuacji 100 mm (wydruk 1:1)

OZNACZENIA — LEGENDA SYMBOLI


—	podkład architektoniczny (rzut AR — ściany przecięte, stolarka, wyposażenie) — linie cienkie szare	▼	gniazdo bryzgoszczelne IP44 (łazienki h = 1,20 m, garaż, pom. techniczne, zewnętrzne)
—	przewody obwodów gniazd YDyp 3×2,5 (5×2,5 — 3f) — połączenia punktów (przebieg schematyczny w tynku / w posadzce)	●	wypust / puszka przyłączeniowa urządzenia zasilanego na stałe (opis: obwód, urządzenie, moc)
✂	gniazdo wtyczkowe podwójne ze stykiem ochronnym, h = 0,30 m (kuchnia nad blatem 1,10 m)	[M]	M — zasilanie napędu osłony przeciwsłonecznej (zaluza/screen) przy oknie

OBWODY NA ARKUSZU (lamela.obliczenia.elektryka.obwody)

Obw.	Odbiorniki	Zab.	Przewód	L [m]	ΔU [%]	Faza	RCD
G2	Gniazda P1: 1.04 Pokój dziecka 2, 1.03 Pokój dziecka	B16	YDyp 3×4	22,8	2,20	L3	RCBO typ A 30 mA
G3	Gniazda P1: 1.02 Pokój rodzinny / biblioteka (boks C	B16	YDyp 3×2,5	15,9	2,45	L1	RCBO typ A 30 mA
G10	Gniazda łazienki (1.05 Łazienka dzieci (wanna))	B16	YDyp 3×4	25,8	2,41	L2	RCBO typ A 30 mA
G11	Gniazda łazienki (1.07 WC z natryskiem)	B16	YDyp 3×2,5	20,4	2,98	L1	RCBO typ A 30 mA
D4	Pralka	B16	YDyp 3×2,5	21,0	2,00	L3	RCBO typ A 30 mA
D5	Suszarka	B16	YDyp 3×2,5	20,2	2,15	L2	RCBO typ A 30 mA
D16	Napędy osłon przeciwsłonecznych (19 szt.)	B10	YDyp 3×1,5	3,0	0,89	L1	RCBO typ A 30 mA

OBJAŚNIENIA I UWAGI

- Wymiary w cm (mm w indeksie górnym, np. 24^o = 24,5 cm), rzędne w m względem ±0,000 = 101,650 m n.p.m. (PL-EVRF2007-NH).
- Rysunki instalacji na podkładzie rzutów architektury (PB-AR); podkład — linie cienkie szare (warstwy I-PODKŁAD).
- Instalacja gniazd wtyczkowych i zasilania urządzeń wg PN-HD 60364-4-41 (samoczynne wyłączenie, RCD 30 mA dla gniazd ≤ 32 A — p. 411.3.3), PN-HD 60364-5-52 (przewody), PN-HD 60364-7-701 (łazienki), PN-HD 60364-7-722 (ładowanie EV), WT § 180–188 (obwody gniazd oddzielne od oświetlenia, gniazda ze stykiem ochronnym).
- Bilans mocy (lamela.obliczenia.elektryka.bilans): P_inst = 73,4 kW, P_szczyt z DLM = 26,3 kW ≤ P_przyl = 27 kW, zabezpieczenie przedlicznikowe 40 A.
- Liczbę i rozmieszczenie gniazd wyznaczono algorytmicznie (grafika branżowa, DIN 18015-2): przy krzesełkach, biurkach, sofach, nad blatem kuchennym co ok. 1,1 m, przy umywalkach (poza strefami 0–2), pozostałe równomiernie wzdłuż ścian bez otworów, urządzenia stałe — wypusty/gniazda dedykowane wg obwodów D.
- Wysokości montażu (od posadzki): gniazda 0,30 m; nad blatem 1,10 m; łazienki 1,20 m (IP44); garaż, pom. techniczne 1,10 m (IP44); łączniki 1,10 m.
- Rysunek wygenerowany automatycznie z modelu /home/user/aihouse/model/budynek.yaml (wersja 1.0, 2026-09-25) — generatory lamela.views.

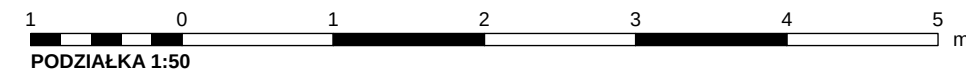

REW.	OPIS ZMIANY	DATA
0	Wydanie — rysunek wygenerowany z modelu	2026-09-25
PRACOWNIA PROJEKTOWA	PRACOWNIA PROJEKTOWA — nazwa do uzupełnienia	STADIUM PT
adres pracowni do uzupełnienia	BRANŻA INSTALACJE ELEKTRYCZNE (IE)	
INWESTOR (do uzupełnienia)	OBIEKT / NAZWA ZAMIERZENIA BUDOWLANEGO Budynek mieszkalny jednorodzinny wolnostojący „Dom LAMELA”	
ADRES / LOKALIZACJA (NR DZIAŁKI, OBRĘB, JEDN. EWIDENCYJNA)	KAT. OBIEKTU I	
ul. Lipowa (fikcyjna), dz. nr ewid. 123/4, obręb 0005 Przykładowo, gm. Przykładowo (fikcyjna)		
FUNKCJA	IMIĘ I NAZWISKO	SPECJALNOŚĆ, NR UPRAWNIEN
Projektant		DATA
Projektant (wsp.)		PODPIS
Sprawdzający		
Opracował		
TYTUŁ RYSUNKU	Gniazda i zasilanie urządzeń — rzut i piętra	
SKALA 1:50	FORMAT A3×3	DATA WYDANIA 2026-09-25
RODZAJ DOK. rzut instalacji	NR RYSUNKU PT-IE-05	ARKUSZ 5/14
REW. 0		