


SCHEMAT IDEOWY ROZDZIELNICY GŁÓWNEJ RG

Schemat ideowy RG — Dom LAMELA. Dane przykładowe [ZAL]; wartości z obliczeń obwodów (lamela.obliczenia.elektryka.obwody).

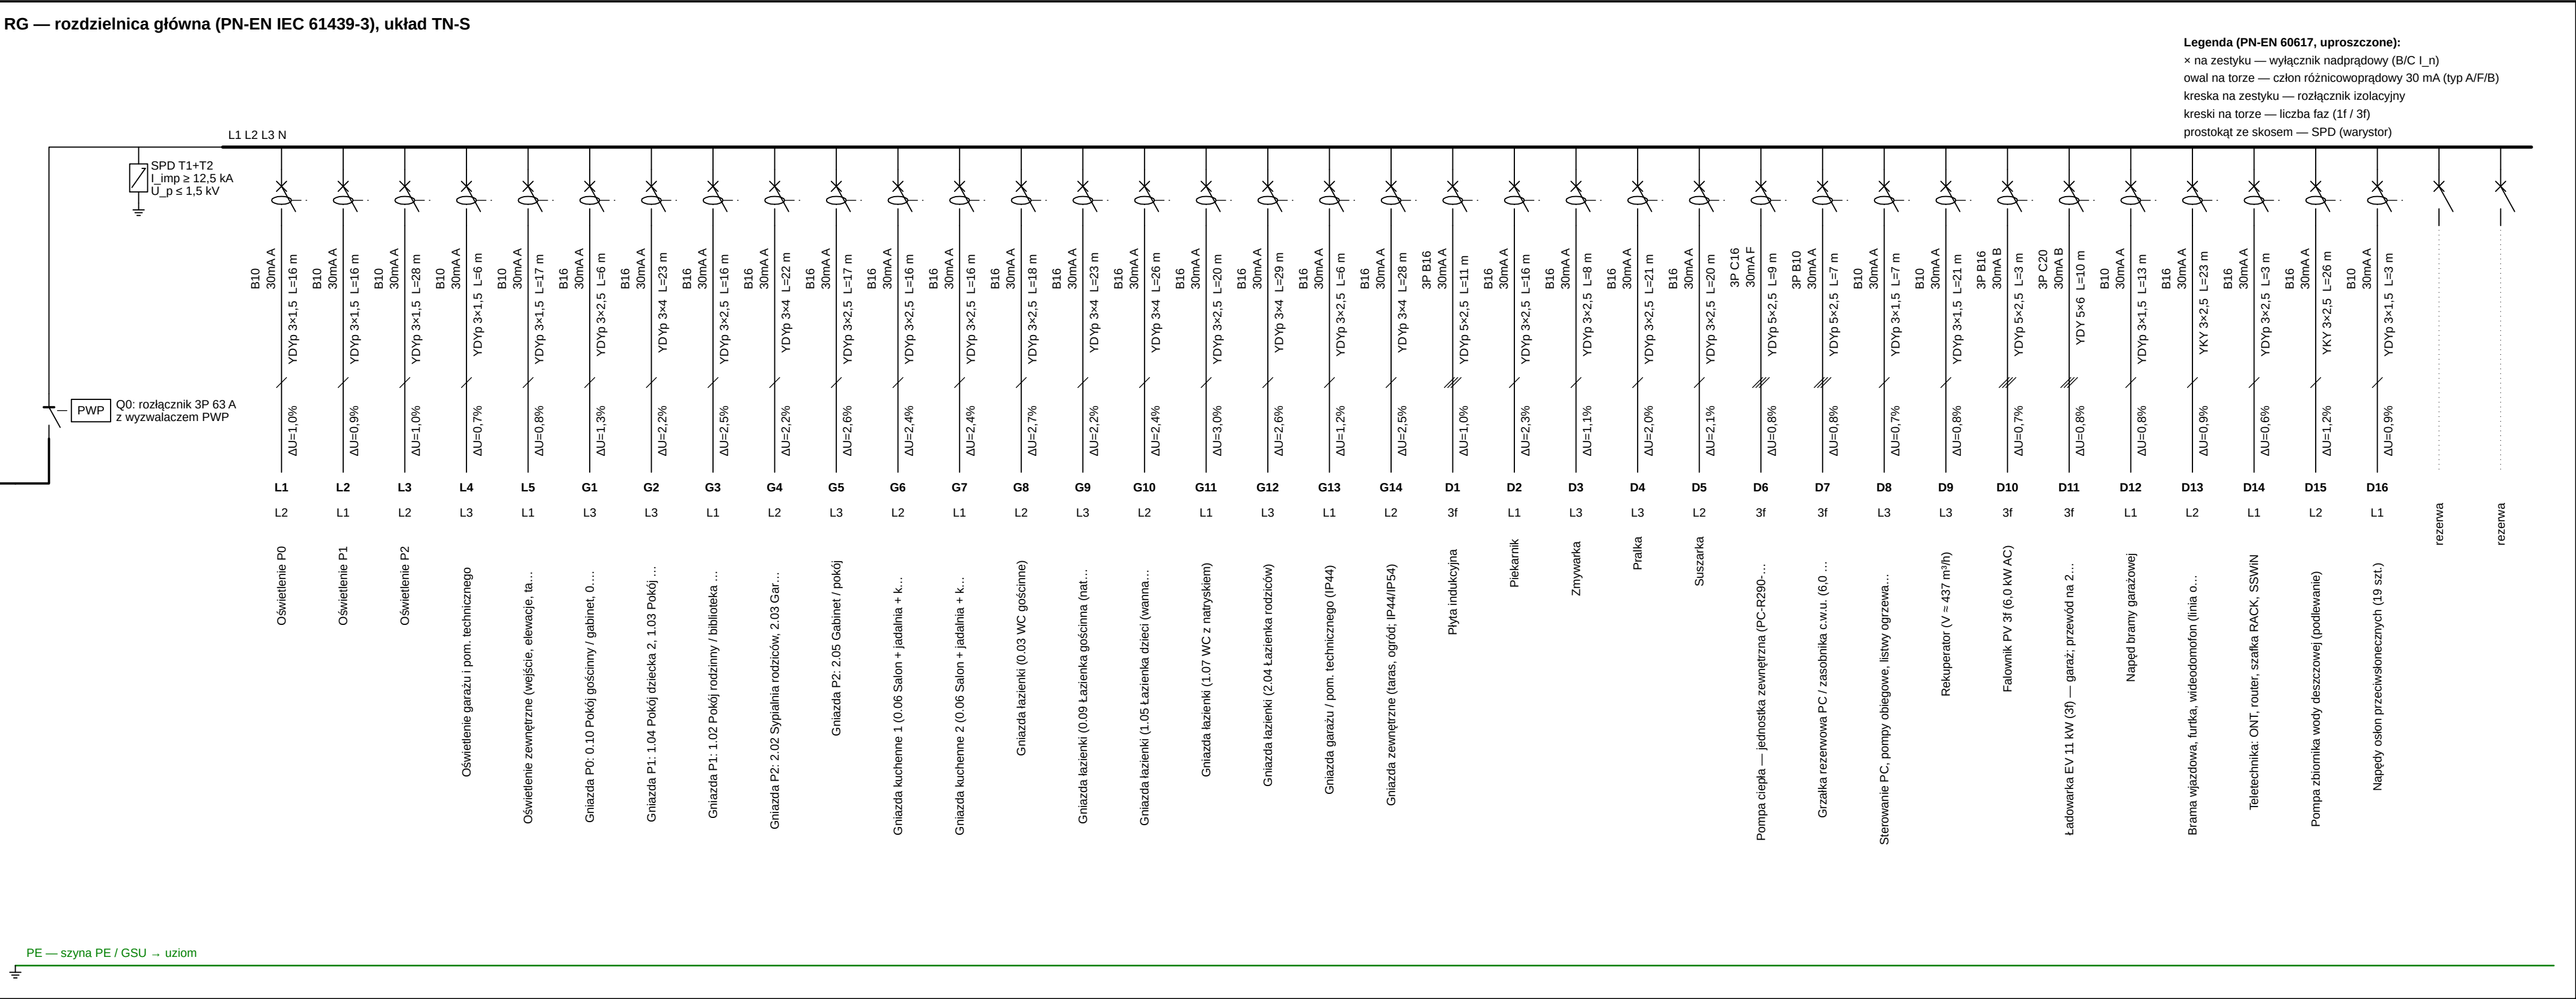

OZNACZENIA

Legenda symboli — na schemacie (PN-EN 60617 / PN-EN ISO 14617 w uproszczeniu; oznaczenia instalacji sanitarnych — praktyka branżowa).

OBJAŚNIENIA I UWAGI

- Schemat bez skali; rzędne w m względem ±0.000 (posadzka parteru), średnice w mm.
- Rysunki instalacji na podkładzie rzutów architektury (PB-AR); podkład — linie cienkie szare (warstwy I-PODKLAD').
- Schemat odtworzony wektorowo z funkcji lamela.obliczenia.elektryka.schemat\_rg (dane: obwody, WLZ, SPD, PWP) — treść i wartości z obliczeń na aktualnym modelu; skala rysunkowa 1.23 mm/jedn. (pismo ≥ 1,8 mm), przesunięto 0 napisów kolidujących.
- Dane urządzeń przykładowe (bez nazw handlowych) — do zastąpienia DTR wybranych wyrobów (lub równoważnych).
- WLZ YKY 5×16, L = 28,3 m; SPD: SPD typ 1+2 (T1+T2), I<sub>imp</sub> ≥ 12,5 kA/biegun, U<sub>p</sub> ≤ 1,5 kV, U<sub>c</sub> ≥ 275 V; układ 3+1 (TN-S) lub 4+0 przy rozdziale PEN w RG.
- Aparatura modułowa wg PN-EN 60898-1, PN-EN 61009-1, PN-EN 61008-1; rozdzielnica wg PN-EN IEC 61439-3; PWP wg WT § 183 (przycisk przy wejściu, oznakowany).
- Rysunek wygenerowany automatycznie z modelu /home/user/aihouse/model/budynek.yaml (wersja 1.0, 2026-09-25) — generatory lamela.views.

|                                                                                               |                                         |                            |                                   |                            |                   |                                       |
|-----------------------------------------------------------------------------------------------|-----------------------------------------|----------------------------|-----------------------------------|----------------------------|-------------------|---------------------------------------|
| REW.                                                                                          | OPIS ZMIANY                             |                            |                                   |                            | DATA              |                                       |
| 0                                                                                             | Wydanie — rysunek wygenerowany z modelu |                            |                                   |                            | 2026-09-25        |                                       |
| PRACOWNIA PROJEKTOWA                                                                          |                                         |                            |                                   |                            | STADIUM<br>PT     | BRANZA<br>INSTALACJE ELEKTRYCZNE (IE) |
| PRACOWNIA PROJEKTOWA — nazwa do uzupełnienia                                                  |                                         |                            |                                   |                            |                   |                                       |
| adres pracowni do uzupełnienia                                                                |                                         |                            |                                   |                            |                   |                                       |
| INWESTOR                                                                                      |                                         |                            |                                   |                            |                   |                                       |
| (do uzupełnienia)                                                                             |                                         |                            |                                   |                            |                   |                                       |
| OBIEKT / NAZWA ZAMIERZENIA BUDOWLANEGO                                                        |                                         |                            |                                   |                            |                   |                                       |
| Budynek mieszkalny jednorodzinny wolnostojący „Dom LAMELA”                                    |                                         |                            |                                   |                            |                   |                                       |
| ADRES / LOKALIZACJA (NR DZIAŁKI, OBRĘB, JEDN. EWIDENCYJNA)                                    |                                         |                            |                                   |                            | KAT. OBIEKTU<br>I |                                       |
| ul. Lipowa (fikcyjna), dz. nr ewid. 123/4, obręb 0005 Przykładowo, gm. Przykładowo (fikcyjna) |                                         |                            |                                   |                            |                   |                                       |
| FUNKCJA                                                                                       |                                         | IMIĘ I NAZWISKO            |                                   | SPECJALNOŚĆ, NR UPRAWNIENI | DATA              | PODPIS                                |
| Projektant                                                                                    |                                         |                            |                                   |                            |                   |                                       |
| Projektant (wsp.)                                                                             |                                         |                            |                                   |                            |                   |                                       |
| Sprawdzający                                                                                  |                                         |                            |                                   |                            |                   |                                       |
| Opracował                                                                                     |                                         |                            |                                   |                            |                   |                                       |
| TYTUŁ RYSUNKU                                                                                 |                                         |                            |                                   |                            |                   |                                       |
| SCHEMAT ROZDZIELNICY GŁÓWNEJ RG                                                               |                                         |                            |                                   |                            |                   |                                       |
| SKALA<br>—                                                                                    | FORMAT<br>A3×3                          | DATA WYDANIA<br>2026-09-25 | RODZAJ DOK.<br>schemat instalacji | NR RYSUNKU<br>PT-IE-14     | ARKUSZ<br>14/14   | REW.<br>0                             |