


odcinek kontrolny 100 mm (wydruk 1:1)

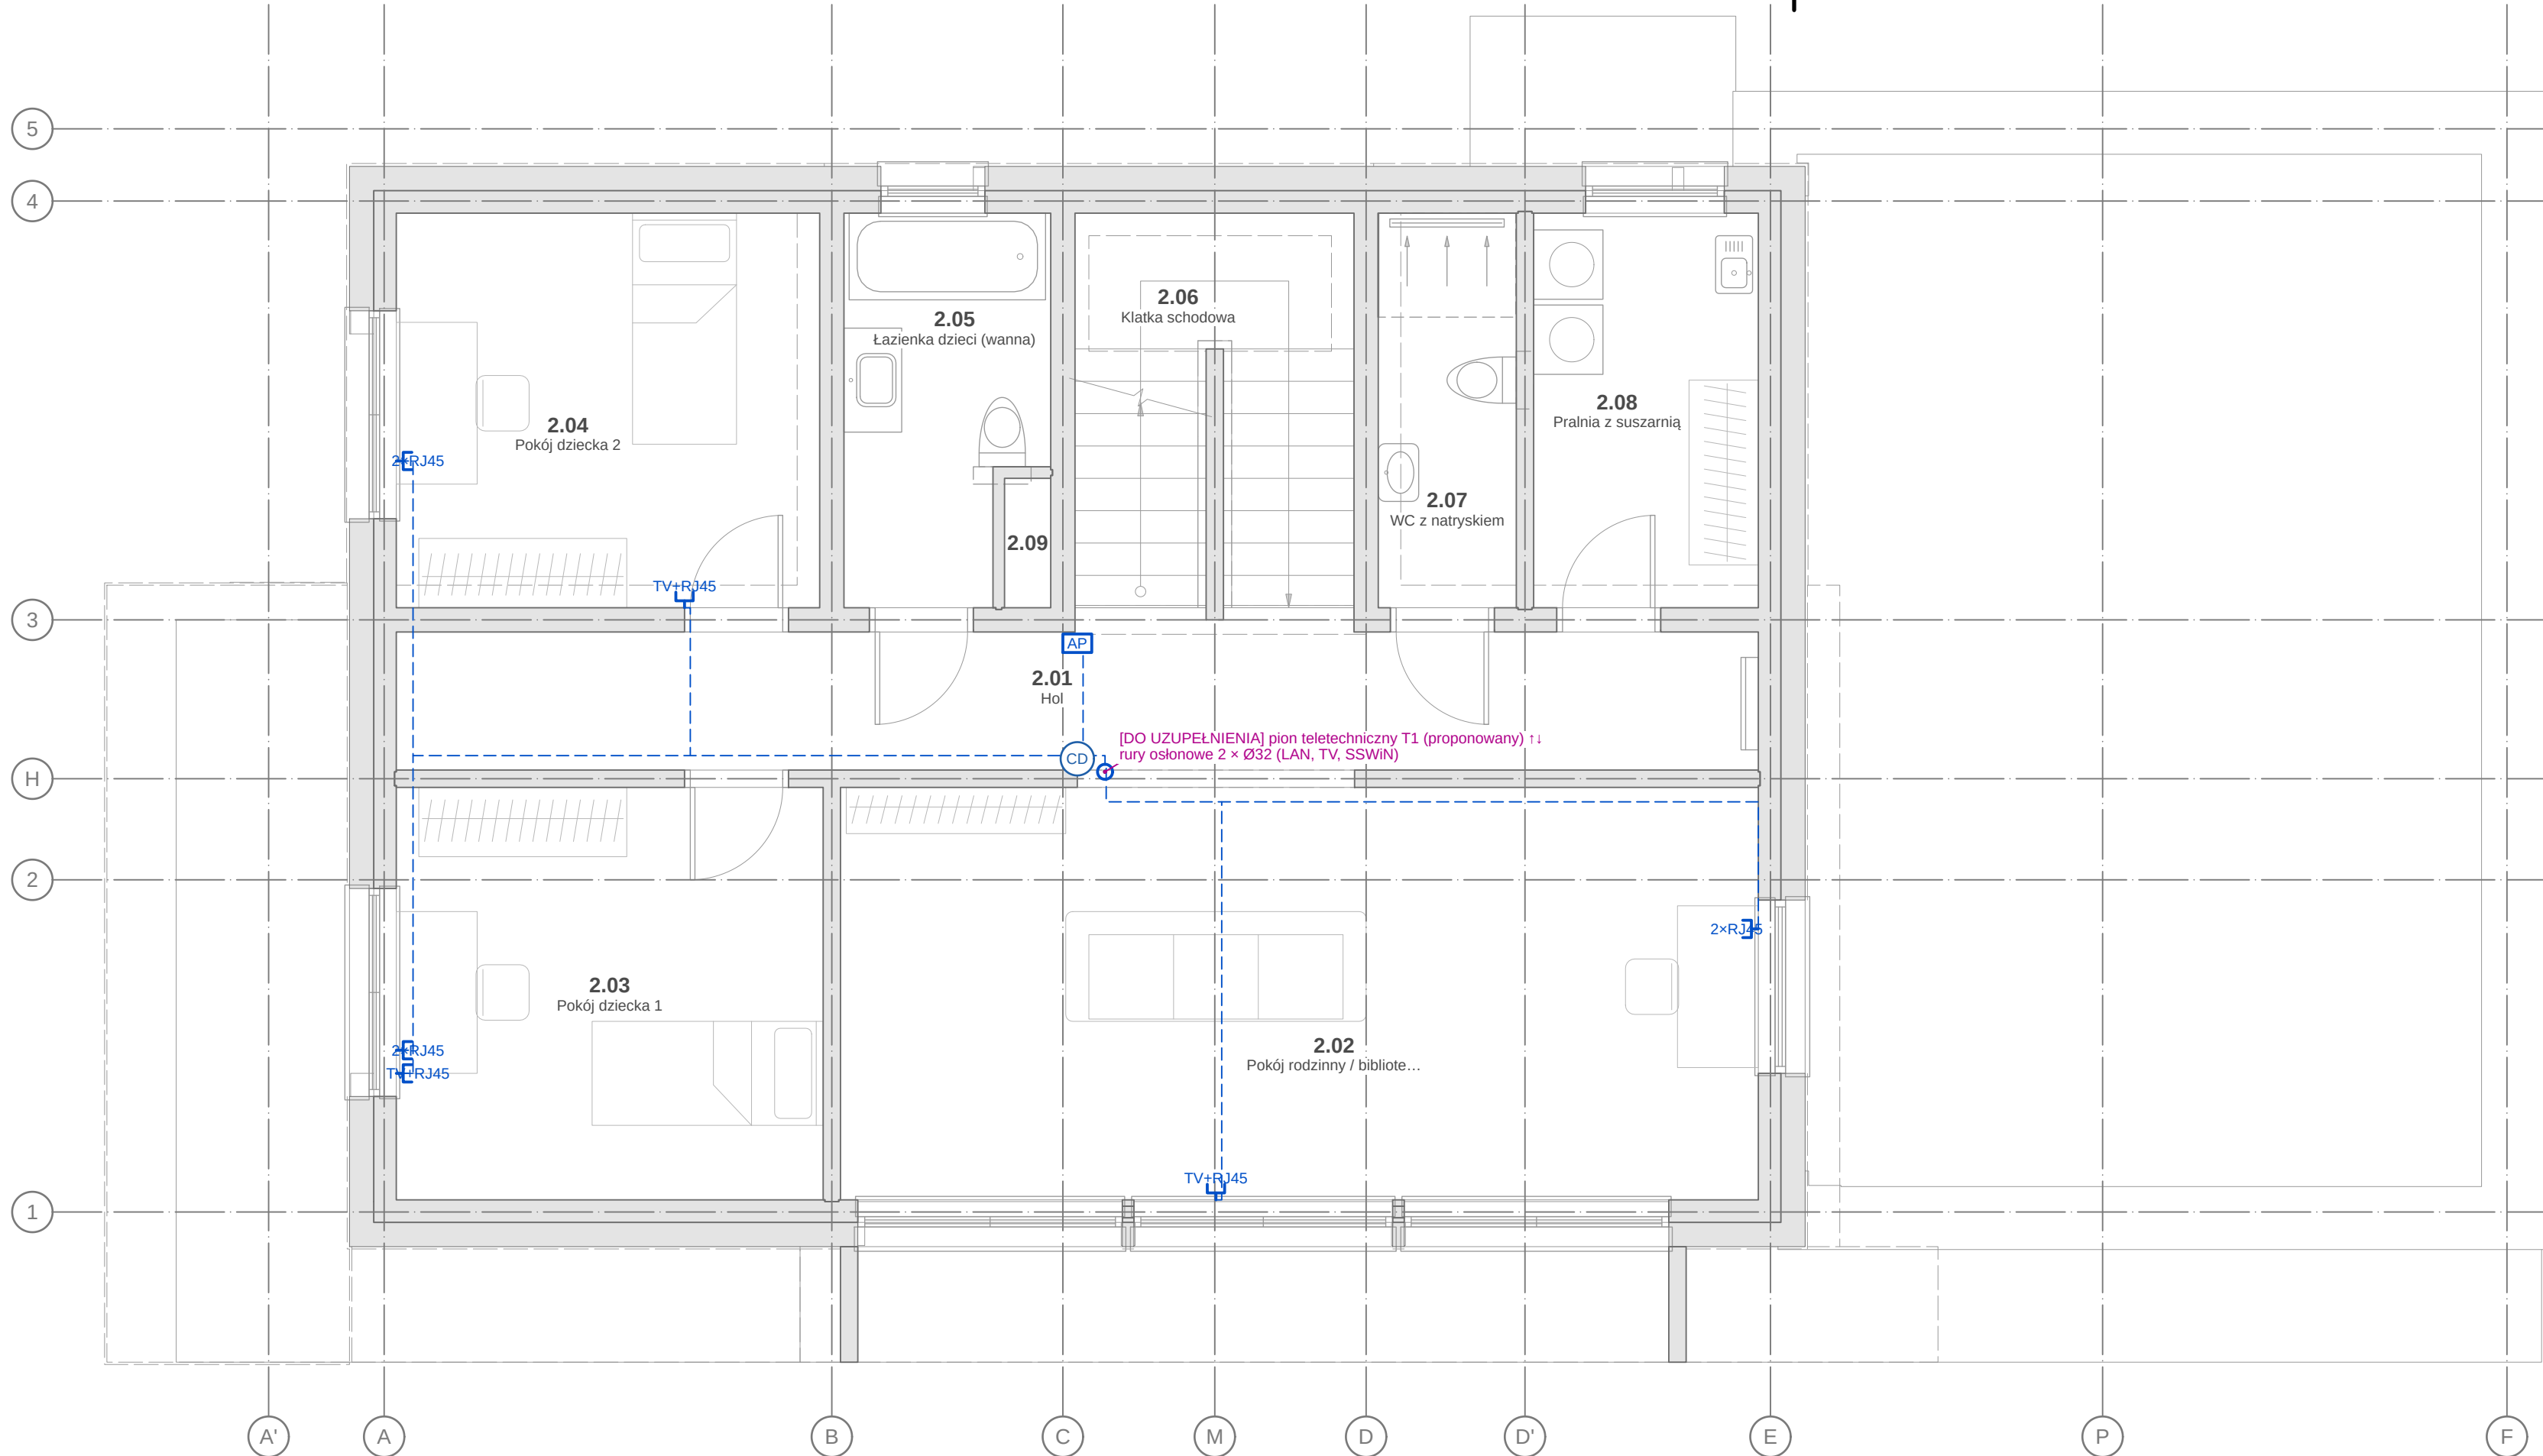

INSTALACJE TELETECHNICZNE — RZUT I PIĘTRA 1:50


## OZNACZENIA — LEGENDA SYMBOLI

Symbole instalacji elektrycznych wg IEC 60617 (baza IEC; PN-EN 60617 — wycofana, stosowana jako praktyka branżowa) i PN-EN ISO 14617; oznaczenia teletechniczne — praktyka branżowa. Obowiązuje legenda na arkuszu.

- podkład architektoniczny (rzut AR — ściany przecięte, stolarka, wyposażenie) — linie cienkie szare
- okablowanie strukturalne: skrętka kat. 6A U/FTP (LAN), koncentryk (TV/SAT), przewody SSWIN i wideodomofonu — w rurach osłonowych, gwiazdziście od RACK

## OBJAŚNIENIA I UWAGI

- Średnice przewodów w mm (d, z×s — rury wielowarstwowe, Ø/DN — kanalizacja, kanały wentylacyjne), przekroje żył w mm<sup>2</sup>, odległości i rzędne w m; ±0,000 = 101,650 m n.p.m. (PL-EVRF2007-NH).
- Rysunki instalacji na podkładzie rzutów architektury (PB-AR); podkład — linie cienkie szare (warstwy I-PODKŁAD\*).
- Instalacje telekomunikacyjne wg WT § 192a–192c (instalacja telekomunikacyjna budynku, przyłącze światłowodowe — art. 10 ustawy o wspieraniu rozwoju usług i sieci telekomunikacyjnych), PN-EN 50173-4 (okablowanie strukturalne w domach), PN-EN 50174-2 (instalowanie), SSWIN wg PN-EN 50131-1 (stopień 2).
- Punkty teleinformatyczne rozmieszczono algorytmicznie: przy biurkach 2×RJ45, na ścianie naprzeciw łóżek i sofy (TV + RJ45), AP Wi-Fi w komunikacji każdej kondygnacji; czujki ruchu w pomieszczeniach parteru z oknami/drzwiami zewnętrznymi. Okablowanie gwiazdźiste do RACK — trasy schematyczne.
- Przewody teletechniczne prowadzić w odległości ≥ 0,1 m od przewodów elektroenergetycznych (lub z przegrodą), w rurach osłonowych Ø20–Ø32; ekranowanie wg PN-EN 50174-2.
- Rysunek wygenerowany automatycznie z modelu model/budynek.yaml (wersja 1.0, 2026-09-25) — generatory lamela.views.

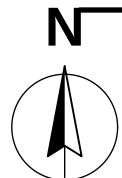

|   |                                         |                            |                                |                                       |                |
|---|-----------------------------------------|----------------------------|--------------------------------|---------------------------------------|----------------|
| REW.   | OPIS ZMIANY                             |                            |                                | DATA                                  |                |
| 0   | Wydanie — rysunek wygenerowany z modelu |                            |                                | 2026-09-25                            |                |
| PRACOWNIA PROJEKTOWA<br>PRACOWNIA PROJEKTOWA — nazwa do uzupełnienia<br>adres pracowni do uzupełnienia                                                      |                                         |                            | STADIUM<br>PT                  | BRANŻA<br>INSTALACJE ELEKTRYCZNE (IE) |                |
| INWESTOR<br>(do uzupełnienia)   |                                         |                            |                                |                                       |                |
| OBIEKT / NAZWA ZAMIERZENIA BUDOWLANEGO<br>Budynek mieszkalny jednorodzinny wolnostojący „Dom LAMELA”                                                        |                                         |                            |                                |                                       |                |
| ADRES / LOKALIZACJA (NR DZIAŁKI, OBRĘB, JEDN. EWIDENCYJNA)<br>ul. Lipowa (fikcyjna), dz. nr ewid. 123/4, obręb 0005 Przykładowo, gm. Przykładowo (fikcyjna) |                                         |                            |                                | KAT. OBIEKTU<br>I                     |                |
| FUNKCJA   | IMIĘ I NAZWISKO                         | SPECJALNOŚĆ, NR UPRAWNIEN  | DATA                           | PODPIS                                |                |
| Projektant   | [DO UZUPEŁNIENIA]                       | [DO UZUPEŁNIENIA]          |                                |                                       |                |
| Projektant (wsp.)   | [DO UZUPEŁNIENIA]                       | [DO UZUPEŁNIENIA]          |                                |                                       |                |
| Sprawdzający   | nie dotyczy (art. 20 ust. 3 pkt 2 PB)   | —                          |                                |                                       |                |
| Opracował   | [DO UZUPEŁNIENIA]                       | [DO UZUPEŁNIENIA]          |                                |                                       |                |
| TYTUŁ RYSUNKU<br>TELETECHNIKA — RZUT I PIĘTRA   |                                         |                            |                                |                                       |                |
| SKALA<br>1:50   | FORMAT<br>690×297                       | DATA WYDANIA<br>2026-09-25 | RODZAJ DOK.<br>rzut instalacji | NR RYSUNKU<br>PT-IE-08                | ARKUSZ<br>8/14 |
|   |                                         |                            |                                |                                       | REW.<br>0      |