

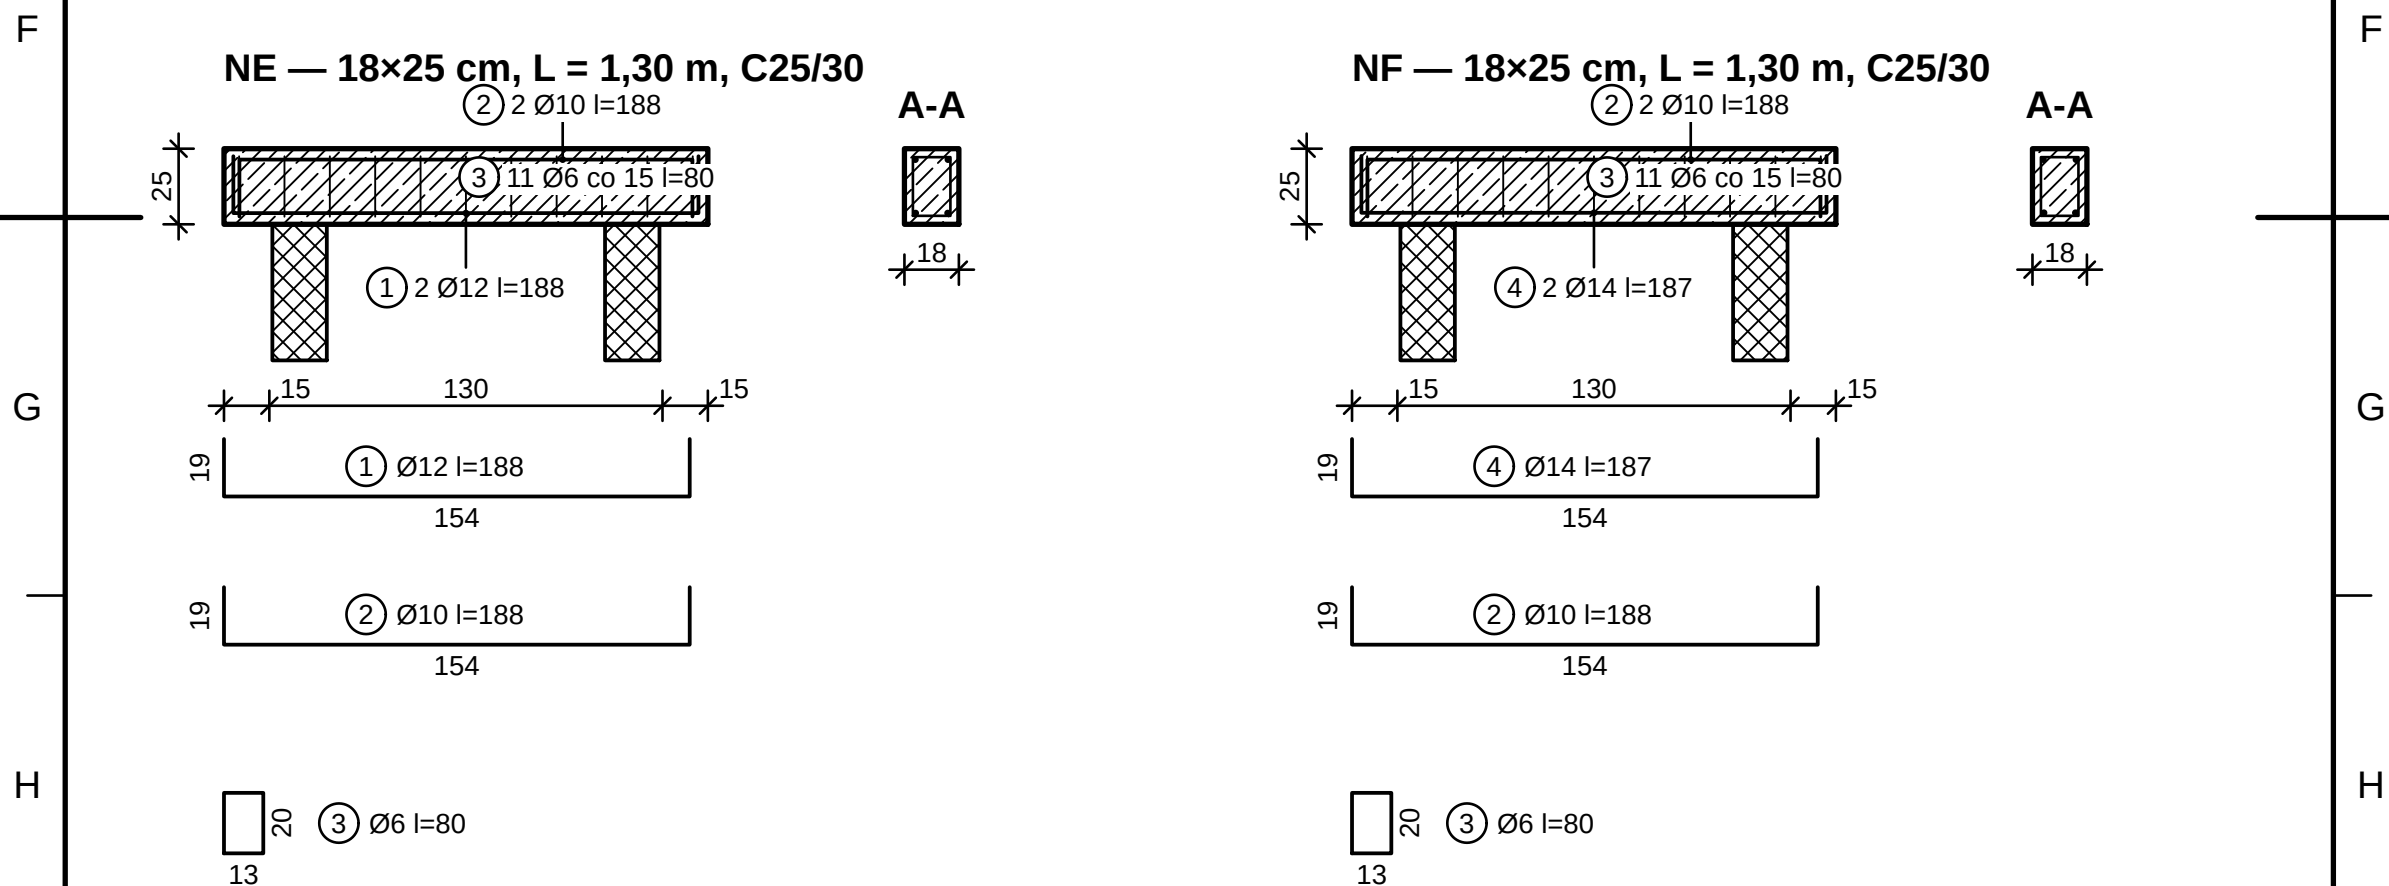


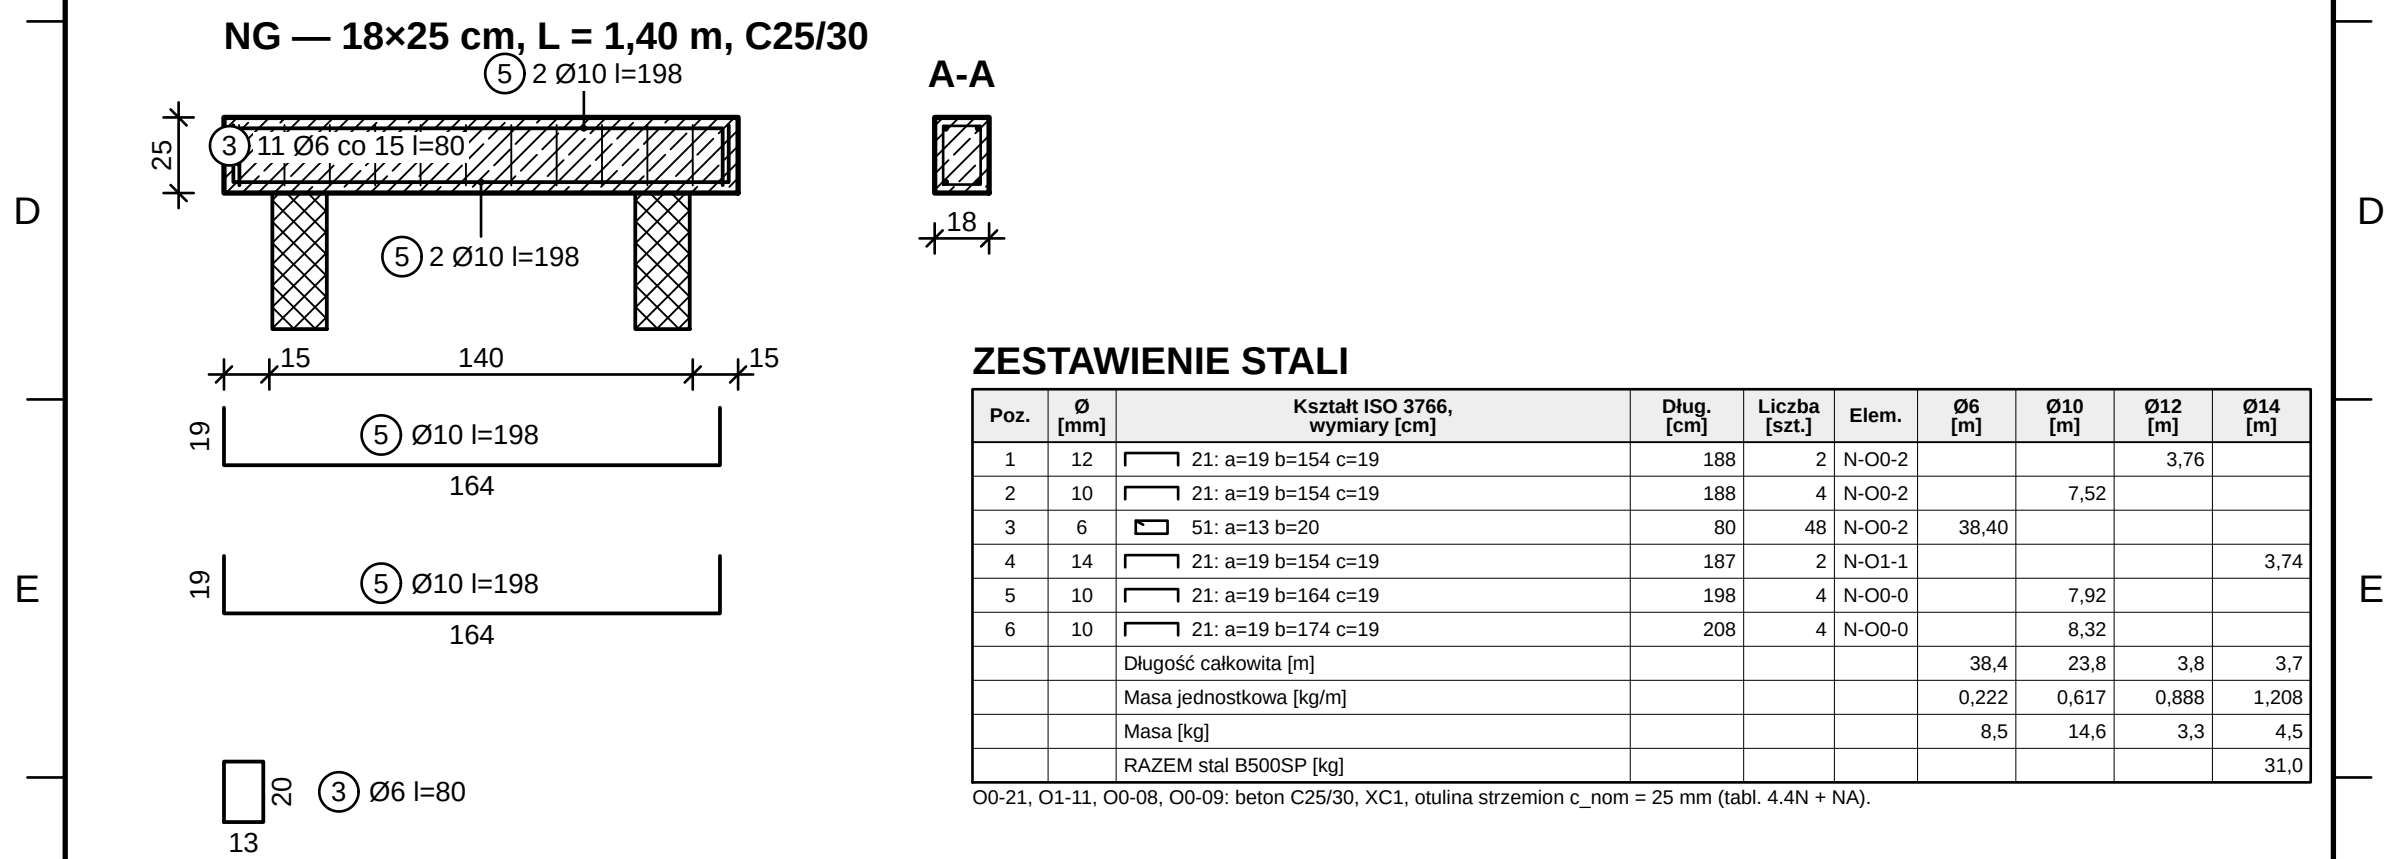

ZBROJENIE NADPROŽY NE, NF, NG, NH 1:25

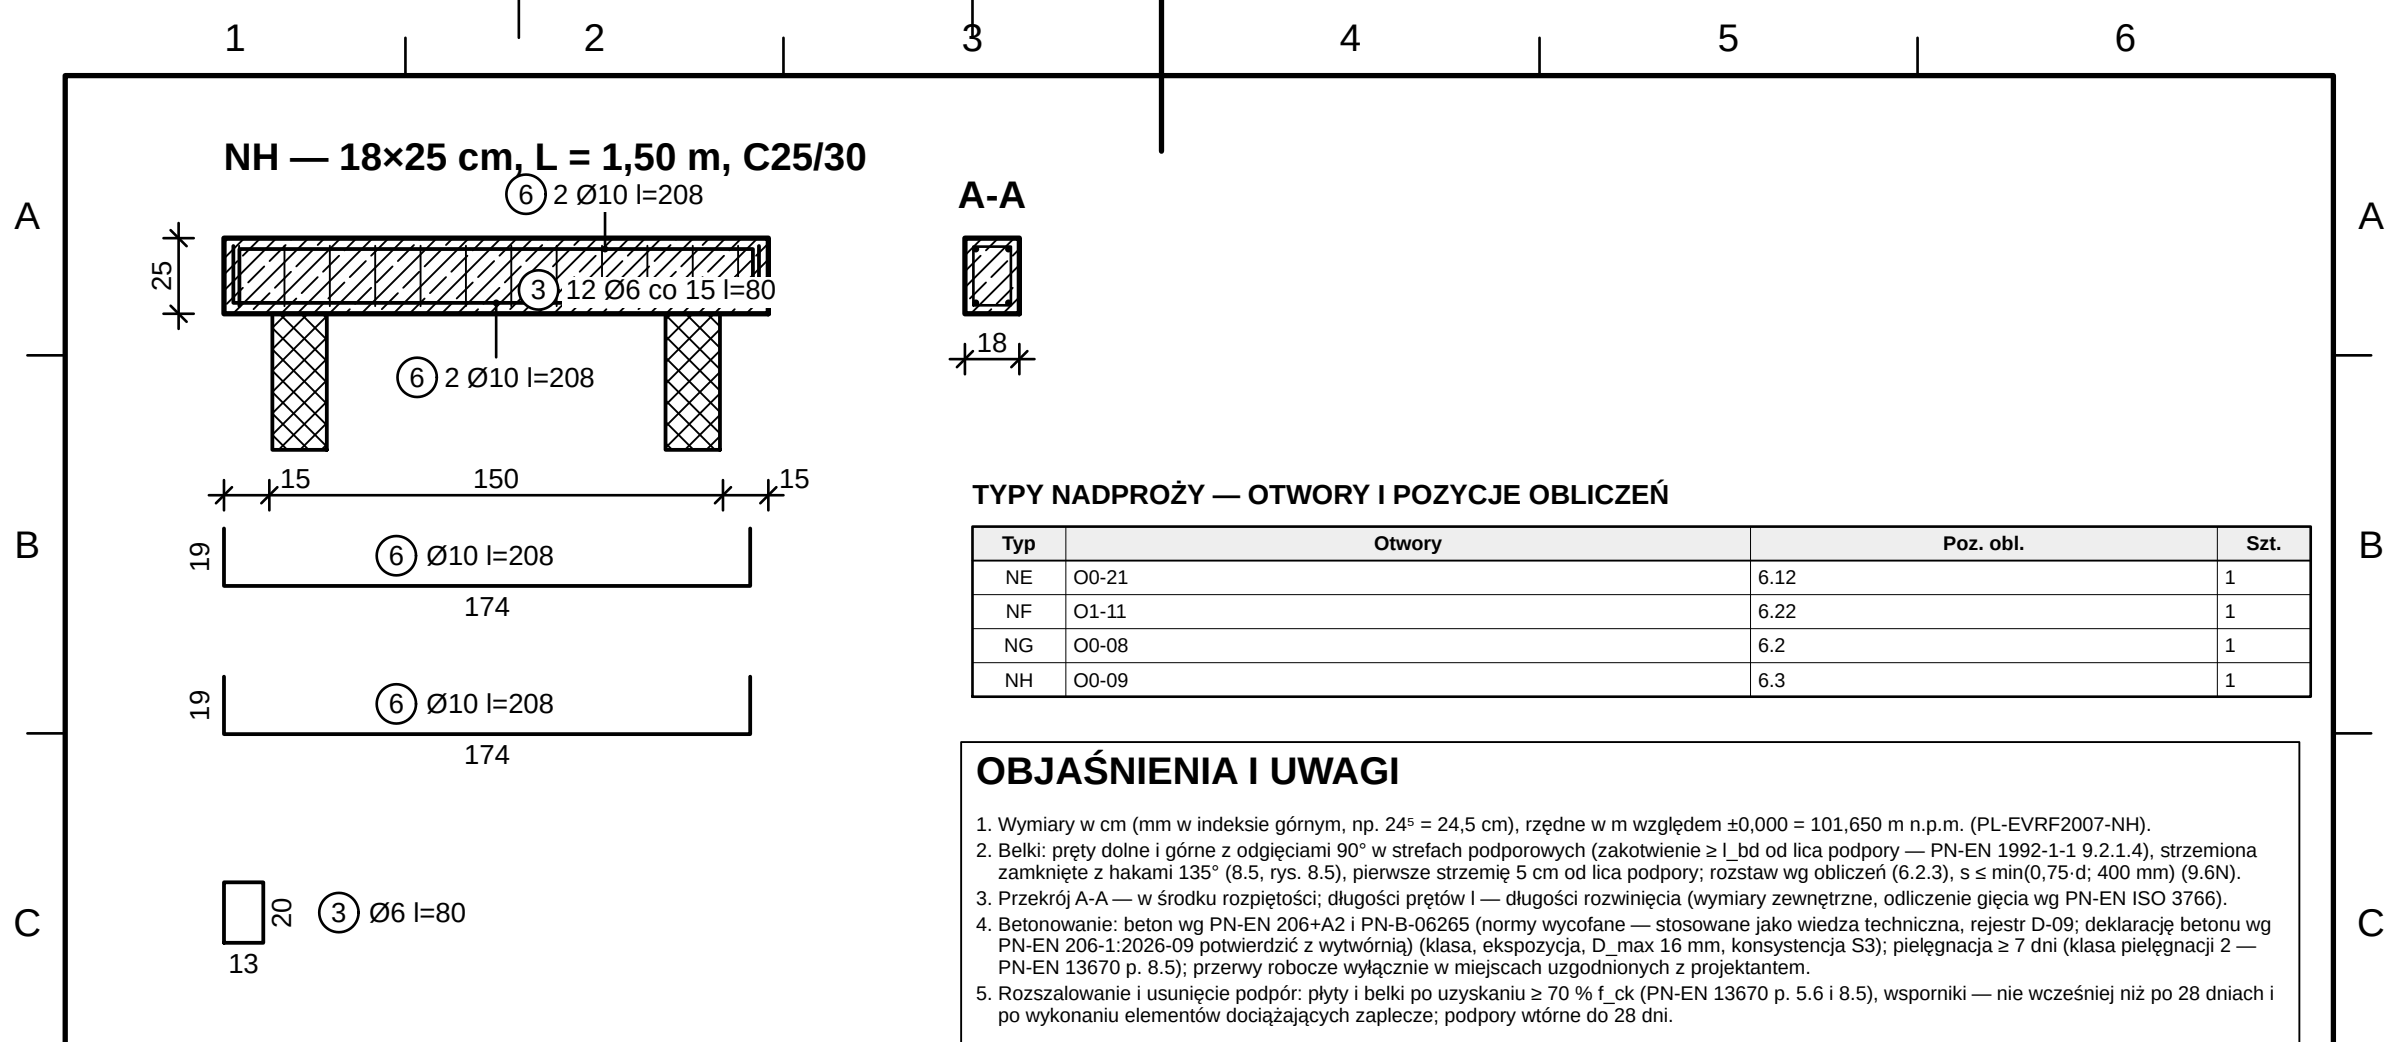