

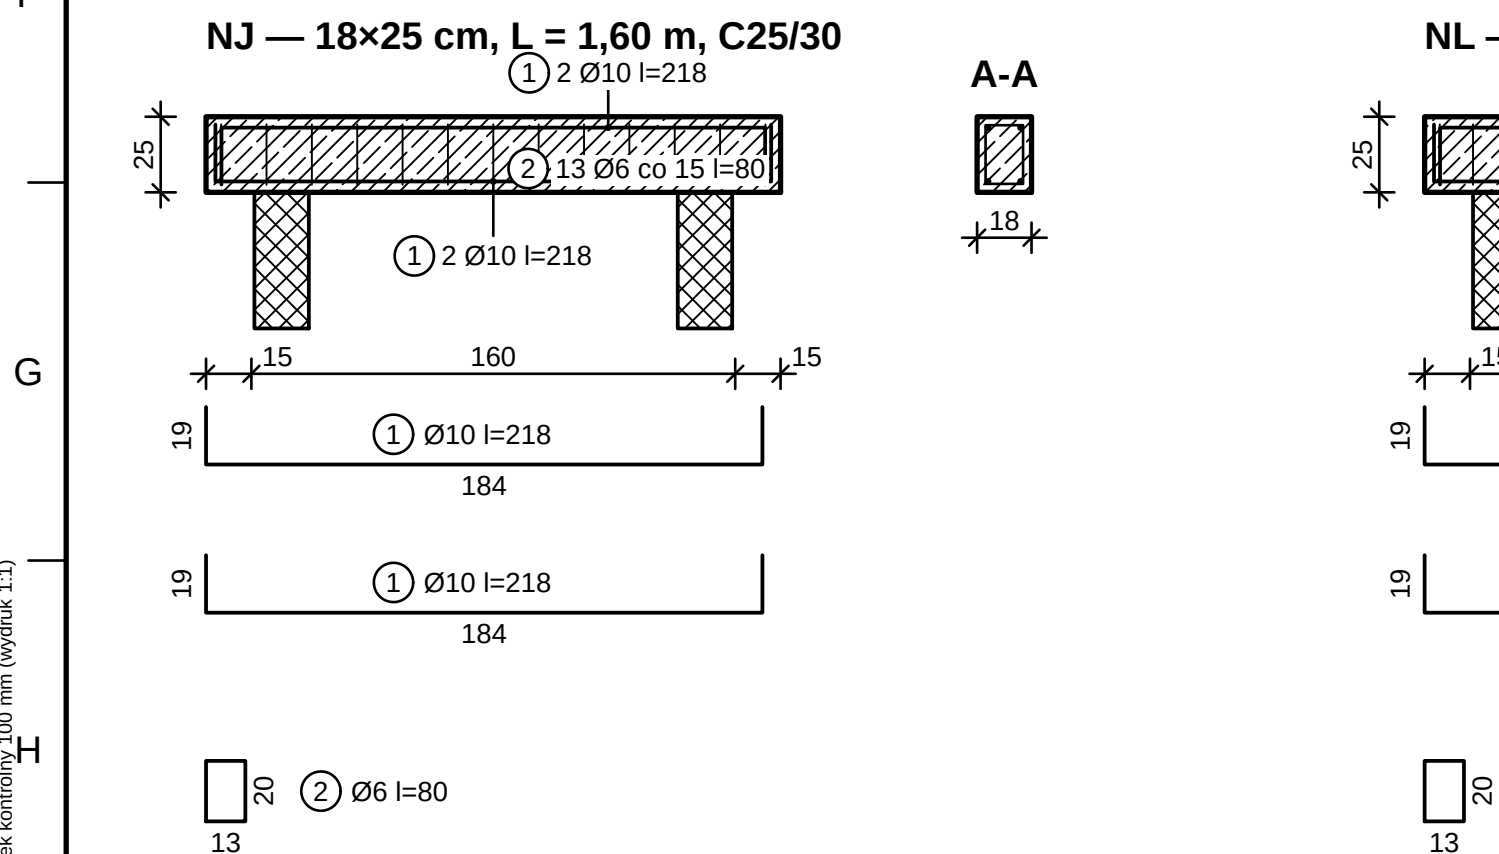
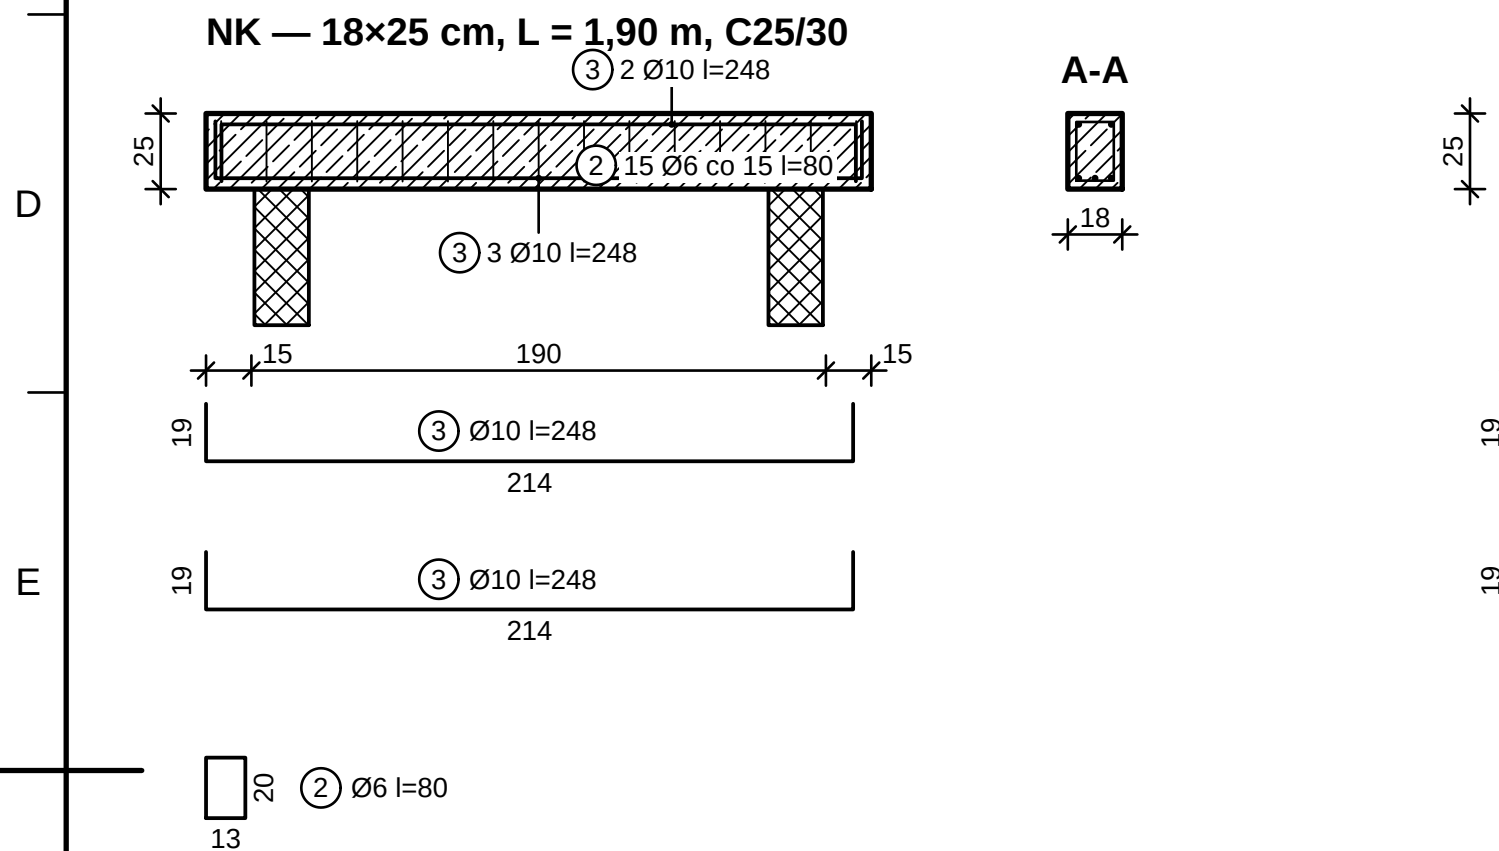


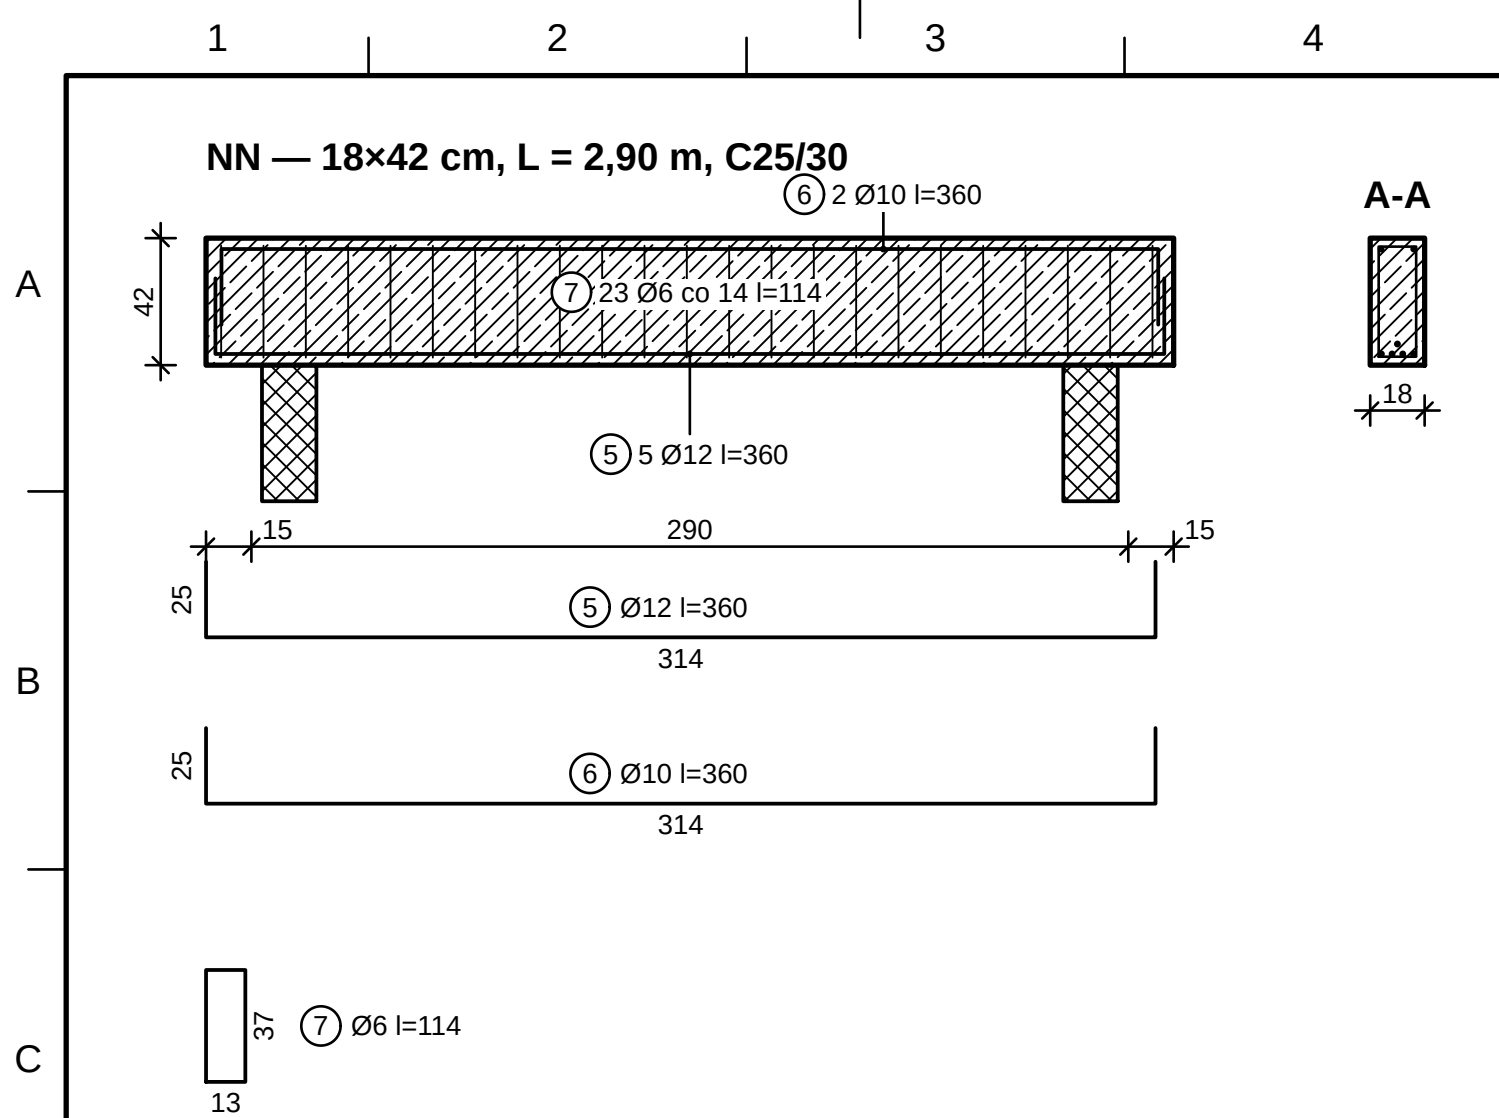

ZBROJENIE NADPROŽY NJ, NK, NL, NM, NN 1:25

TYPY NADPROŻY — OTWORY I POZYCJE OBLICZEŃ

Typ	Otworky	Poz. obl.	Szt.
NJ	O1-04	6.17	1
NK	O1-02	6.15	1
NL	O0-18	6.11	1
NM	O0-12	6.6	1
NN	O0-11	6.5	1

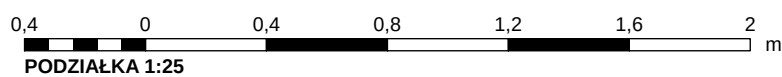



ZESTAWIENIE STALI

Poz.	Ø [mm]	Kształt ISO 3766, wymiary [cm]	Dług. [cm]	Liczba [szt.]	Elem.	Ø6 [m]	Ø10 [m]	Ø12 [m]
1	10	 21: a=19 b=184 c=19	218	4	N-O1-0		8,72	
2	6	 51: a=13 b=20	80	69	N-O1-0	55,20		
3	10	 21: a=19 b=214 c=19	248	14	N-O1-0		34,72	
4	10	 21: a=19 b=254 c=19	288	4	N-O0-1		11,52	
5	12	 21: a=25 b=314 c=25	360	5	N-O0-1			18,00
6	10	 21: a=25 b=314 c=25	360	2	N-O0-1		7,20	
7	6	 51: a=13 b=37	114	24	N-O0-1	27,36		
		Długość całkowita [m]				82,6	62,2	18,0
		Masa jednostkowa [kg/m]				0,222	0,617	0,888
		Masa [kg]				18,3	38,3	16,0
		RAZEM stal B500SP [kg]						72,6

O1-04, O1-02, O0-18, O0-12, O0-11: beton C25/30, XC1, otulina strzemion $c_{nom} = 25 \text{ mm}$ (tabl. 4.4N + NA)

OBJAŚNIENIA I UWAGI

1. Wymiary w cm (mm w indeksie górnym, np. 24" = 24,5 cm), rzędne w m względem 0,00 = 101,650 m n.p.m. (PL-EVRF2007-NH).
2. Belki: prety dolne i górne z odciągami 90° np. w strefach podporowych (zakotwienie z 1_bld od lica podopory — PN-EN 1992-1-1 9.2.1.4), strzemiona zamknięte z hakami 135° (8.5, rys. 8.5), pierwsze strzemie 5 cm od lica podopory; rozstaw wzdłuż obliczeń (6.2.3), s ≤ min(0,75; d; 400 mm) (9.6N).
3. Przekrój A-A — w środku rozpiętości; długości prętów I — długości rozcinania (wymiary zewnętrzne, odcięcie gęścią w PN-EN ISO 3766).
4. Betonowanie: beton wg PN-EN 206+A2 i PN-B-06265 (normy wycofane — stosowane jako wiedza techniczna), rejestr D-09; deklaracje betonu wg PN-EN 206-1:2026-09 potwierdź z wytwórną (klasa, ekspozycja, D_max 16 mm, konsystencja S3); pełniaczność ≥ 7 dni (klasa pełniaczności 2 — PN-EN 13670 p. 8.5); przewzy robocze wyciągnięte w miejscach zdokonywanych z projektem.
5. Rozszalowanie i usunięcie podopór: płyty i belki po uzyskaniu ≥ 70 % f_{cd} (PN-EN 13670 p. 5.6 i 8.5), wsporniki — nie wcześniej niż po 28 dniach i po wykonaniu elementów dociągających zaplecze; podopory wtórne do 28 dni.
6. Nadproża pogrupowane w typy (jednokowy przekrój, długość i zbrojenie z obliczeń); liczby sztuk w zestawieniu — łącznie dla wszystkich nadproży typu.
7. Rysunek wygenerowany automatycznie z modelu model/budynek.yaml (wersja 1.0, 2026-09-25) — generatory lamela.views.

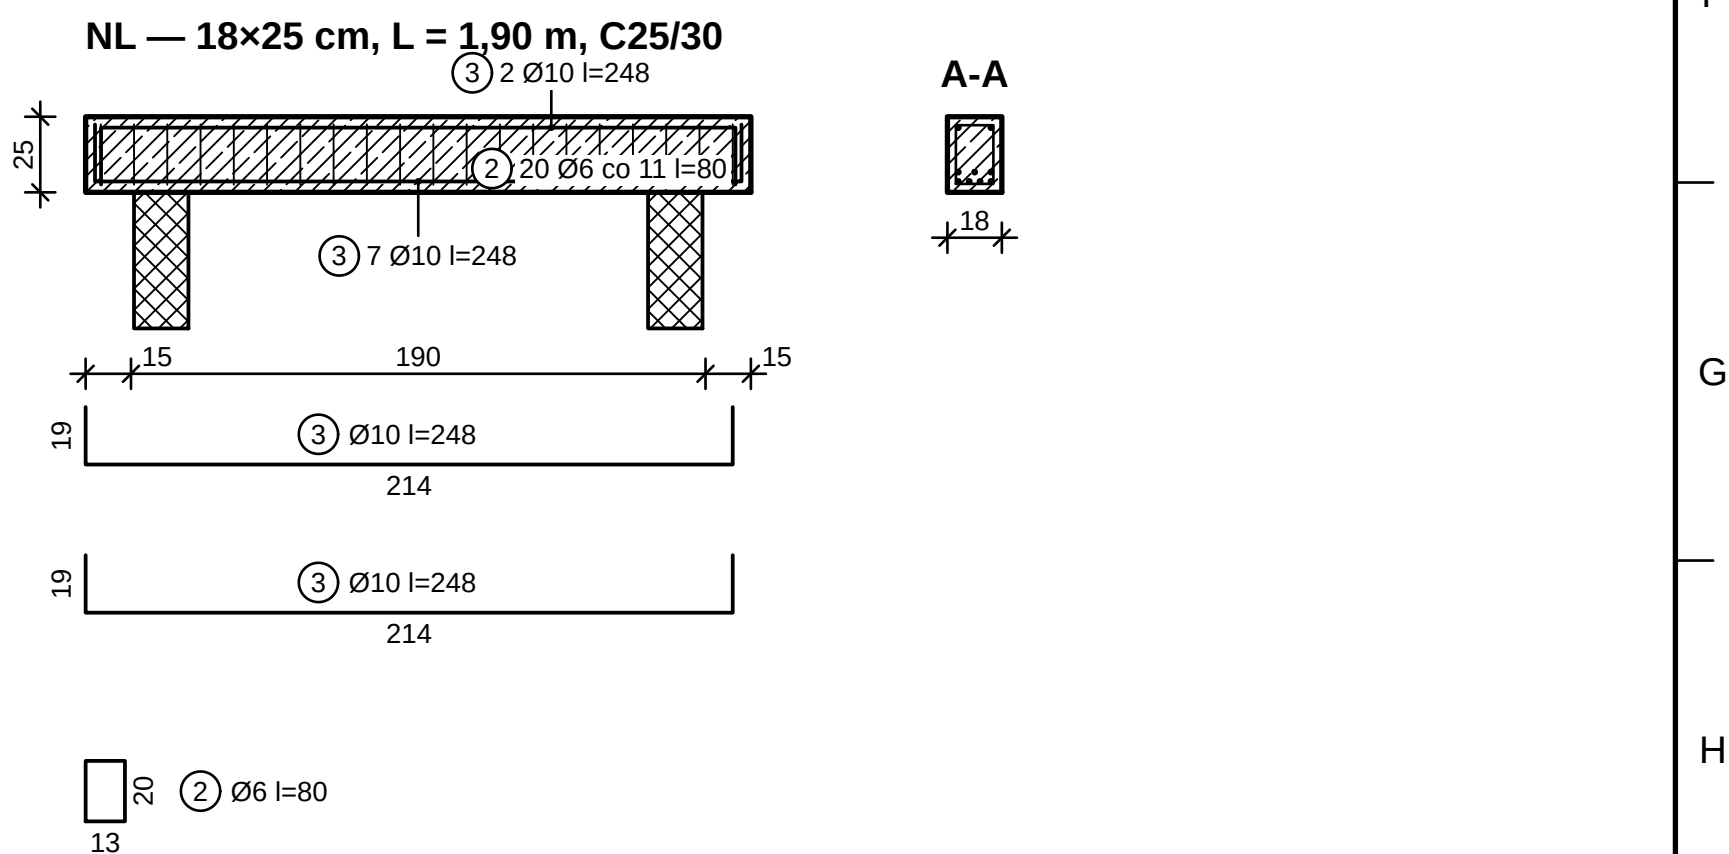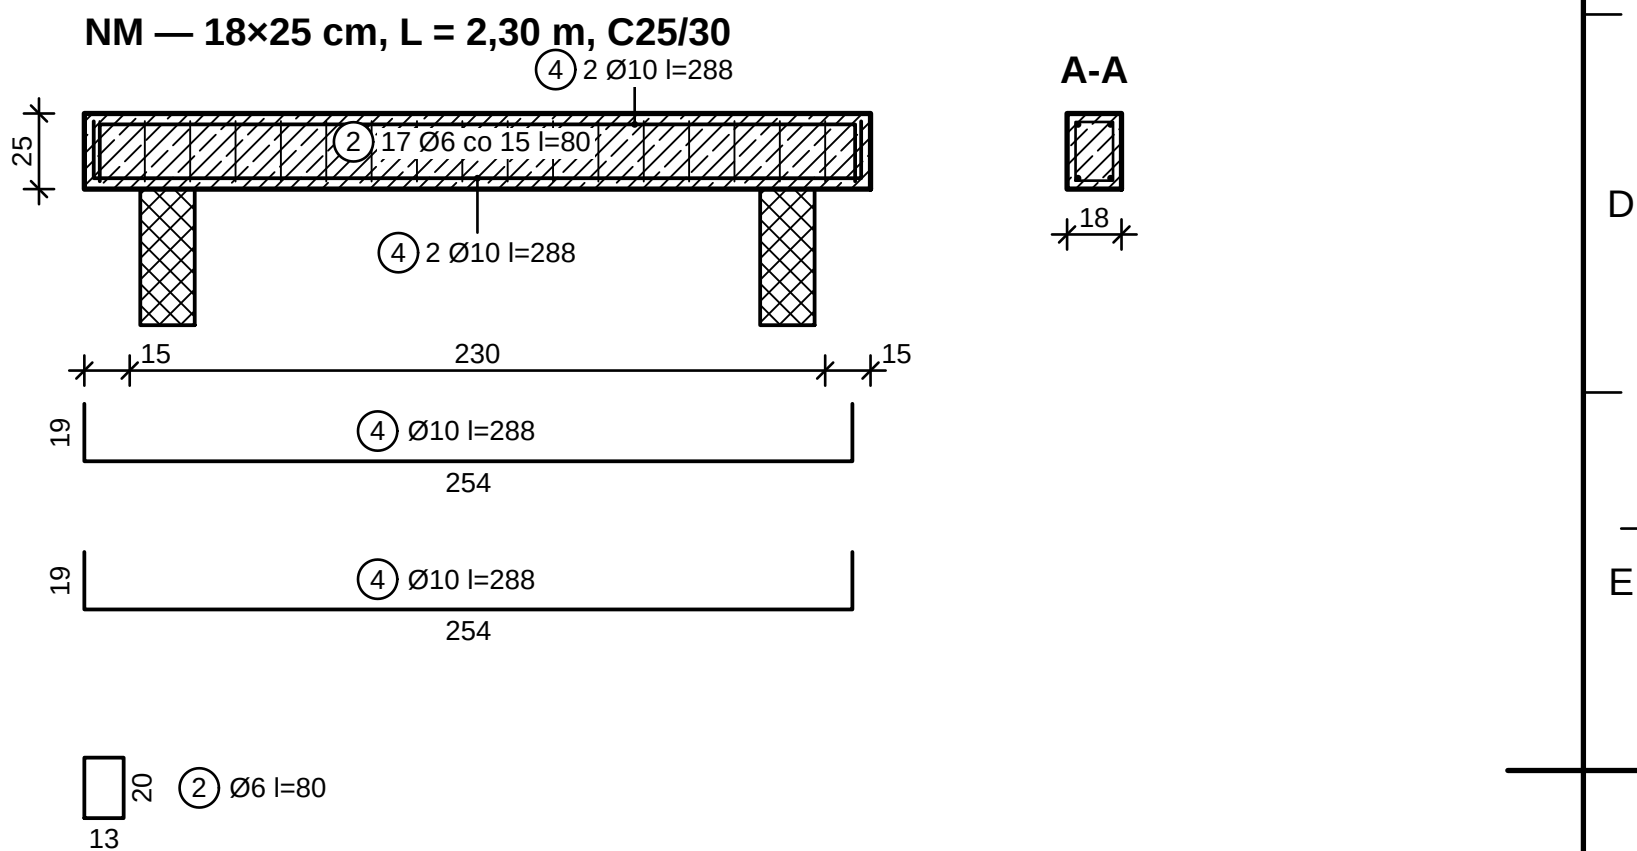

REW.	OPIS ZMIANY		DATA			
0	Wydanie — rysunek wygenerowany z modelu		2026-09-25			
PRACOWNIA PROJEKTOWA PRACOWNIA PROJEKTOWA — nazwa do uzupełnienia adres pracowni do uzupełnienia		STADIUM PT	BRANŻA KONSTRUKCJA (BO)			
INWESTOR (do uzupełnienia)						
OBIEKT / NAZWA ZAMIERZENIA BUDOWLANEGO Budynek mieszkalny jednorodzinny wolnostojący „Dom LAMELA”						
ADRES / LOKALIZACJA (NR DZIAŁKI, OBRĘB, JEDN. EWIDENCYJNA) ul. Lipowa (fikcyjna), dz. nr ewid. 123/4, obręb 0005 Przykładowo, gm. Przykładowo (fikcyjna)			KAT. OBIEKTU I			
FUNKCJA	IMIĘ I NAZWISKO	SPECJALNOŚĆ, NR UPRAWNIENIĆ	DATA	PODPIS		
Projektant	[DO UZUPEŁNIENIA]	[DO UZUPEŁNIENIA]				
Projektant (wsp.)	[DO UZUPEŁNIENIA]	[DO UZUPEŁNIENIA]				
Sprawdzający	nie dotyczy (art. 20 ust. 3 pkt 2 PB)	—				
Opracował	[DO UZUPEŁNIENIA]	[DO UZUPEŁNIENIA]				
TYTUŁ RYSUNKU ZBROJENIE NADPROŻY (3)						
SKALA 1:25	FORMAT 420x530	DATA WYDANIA 2026-09-25	RODZAJ DOK. rysunek zbrojenia	NR RYSUNKU PT-BO-25	ARKUSZ 25/27	REW. 0