

odcinek kontury 100 mm (wydruk 1:1)


RZUT PARTERU 1:50

ZESTAWIENIE POMIESZCZEŃ					
Nr	Nazwa pomieszczenia	Posadzka	Kat.	Wys. [m]	Pow. [m²]
1.06	Salon + jadalnia + kuchnia	Deska warstwowa dębowa 15 mm, klejona na podst.	podst.	2,77	54,44
1.13	Garaż 2-stanowiskowy	Posadzka żywiczna epoksydowa antypoślizgowa (garaż)	garaż	2,76	37,42
1.10	Pokój gościnny / gabinet	Deska warstwowa dębowa 15 mm, klejona na podst.	podst.	2,77	12,52
1.12	Pomieszczenie techniczne	Płytki gresowe 60×120 na kleju C2TE S1 techn.	techn.	2,76	8,85
1.11	Przedśionek gospodarczy	Płytki gresowe 60×120 na kleju C2TE S1 ruchu	ruchu	2,76	7,18
1.05	Śpiżarnia (pod schodami)	Płytki gresowe 60×120 na kleju C2TE S1 pomoc.	pomoc.	1,90	5,40
1.02	Hol	Płytki gresowe 60×120 na kleju C2TE S1 ruchu	ruchu	2,77	4,44
1.01	Wiatrołap	Płytki gresowe 60×120 na kleju C2TE S1 ruchu	ruchu	2,77	3,89
1.09	Łazienka gościnna (natrysk)	Płytki gresowe 60×120 na kleju C2TE S1 pomoc.	pomoc.	2,77	3,84
1.07	Pas komunikacyjny przy schodach	Deska warstwowa dębowa 15 mm, klejona na ruchu	ruchu	2,77	3,51
1.04	Klatka schodowa	Deska warstwowa dębowa 15 mm, klejona na ruchu	ruchu	2,77	2,82
1.03	WC gościnne	Płytki gresowe 60×120 na kleju C2TE S1 pomoc.	pomoc.	2,77	2,32
1.08	Przedpokój gościnny	Deska warstwowa dębowa 15 mm, klejona na ruchu	ruchu	2,77	1,44
RAZEM powierzchnia netto					148,07
w tym użytkowa (podst. + pomoc.)					115,94

OZNACZENIA MATERIAŁÓW (PN-B-01030 + przyjęte)	
	Ściana szklana VSG 2 x 8 mm w ramie aluminiowej (wiatrołap / hol)
	Zelbet C25/30, B500SP (stropy, płyta fundamentowa, ściany) — 45° na przeniam ciagle i przerywane

OZNACZENIA LINII	
---	elementy nad płaszczyzną cięcia (obrys płyt, wsporników, brył wyższych kondygnacji)
---	elementy poniżej płaszczyzny cięcia (widok z góry)
---	osie konstrukcyjne; linia punktowa z pogrubionymi końcami — ślad przekroju

OBJAŚNIENIA I UWAGI	
1.	Wymiary w cm (mm w indeksie górnym, np. 24° = 24,5 cm), rzędne w m względem ±0,000 = 101,650 m n.p.m. (PL-EVRF2007-NH).
2.	Rzuty: płaszczyzna cięcia +1,10 m nad posadzką kondygnacji. Linia kreskową — elementy nad płaszczyzną cięcia (obrys płyt i wsporników, brył wyższych kondygnacji, otwory w stropie nad, belki); linia cieniłą — elementy poniżej (widok).
3.	Otwory: licznik — szerokość, mianownik — wysokość w świetle muru, w nawiasie wysokość parapetu; symbol stolarki wg zestawienia stolarki.
4.	Numeracja pomieszczeń wg PN-B-01025 / PN-EN ISO 4157-2: <nr kondygnacji (parter = 1)> <nr> identyfikator w modelu: <kond> <nr> (parter = 0).
5.	Drzwi: strona otwierania (lewe/prawe) wg modelu — patrząc od strony, w którą otwiera się skrzydło.
6.	Rysunek wygenerowany automatycznie z modelu /home/user/aihouse/model/budynek.yaml (wersja 1.0, 2026-09-25) — generatory lamela.views.

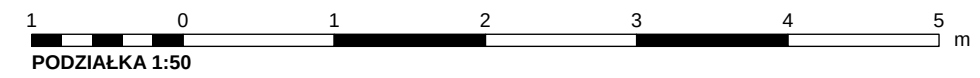

REW.	OPIS ZMIANY	DATA
0	Wydanie — rysunek wygenerowany z modelu	2026-09-25
PRACOWNIA PROJEKTOWA PRACOWNIA PROJEKTOWA — nazwa do uzupełnienia		STADIUM PB
adres pracowni do uzupełnienia		BRANŻA ARCHITEKTURA (AR)
INWESTOR (do uzupełnienia)		
OBJEKT / NAZWA ZAMIERZENIA BUDOWLANEGO Budynek mieszkalny jednorodzinny wolnostojący „Dom LAMELA”		
ADRES / LOKALIZACJA (NR DZIAŁKI, OBRĘB, JEDN. EWIDENCYJNA) ul. Lipowa (fikcyjna), dz. nr ewid. 1234, obręb 0005 Przykładowo, gm. Przykładowo (fikcyjna)		KAT. OBJEKTU I
FUNKCJA	IMIĘ I NAZWISKO	SPECJALNOŚĆ, NR UPRAWNIEN
Projektant		DATA
Projektant (wsp.)		PODPIS
Sprawdzający		
Opracował		
TYTUŁ RYSUNKU RZUT PARTERU		
SKALA 1:50	FORMAT A1	DATA WYDANIA 2026-09-25
RODZAJ DOK. Izut	NR RYSUNKU PB-AR-01	ARKUSZ 1/10
REW. 0		