


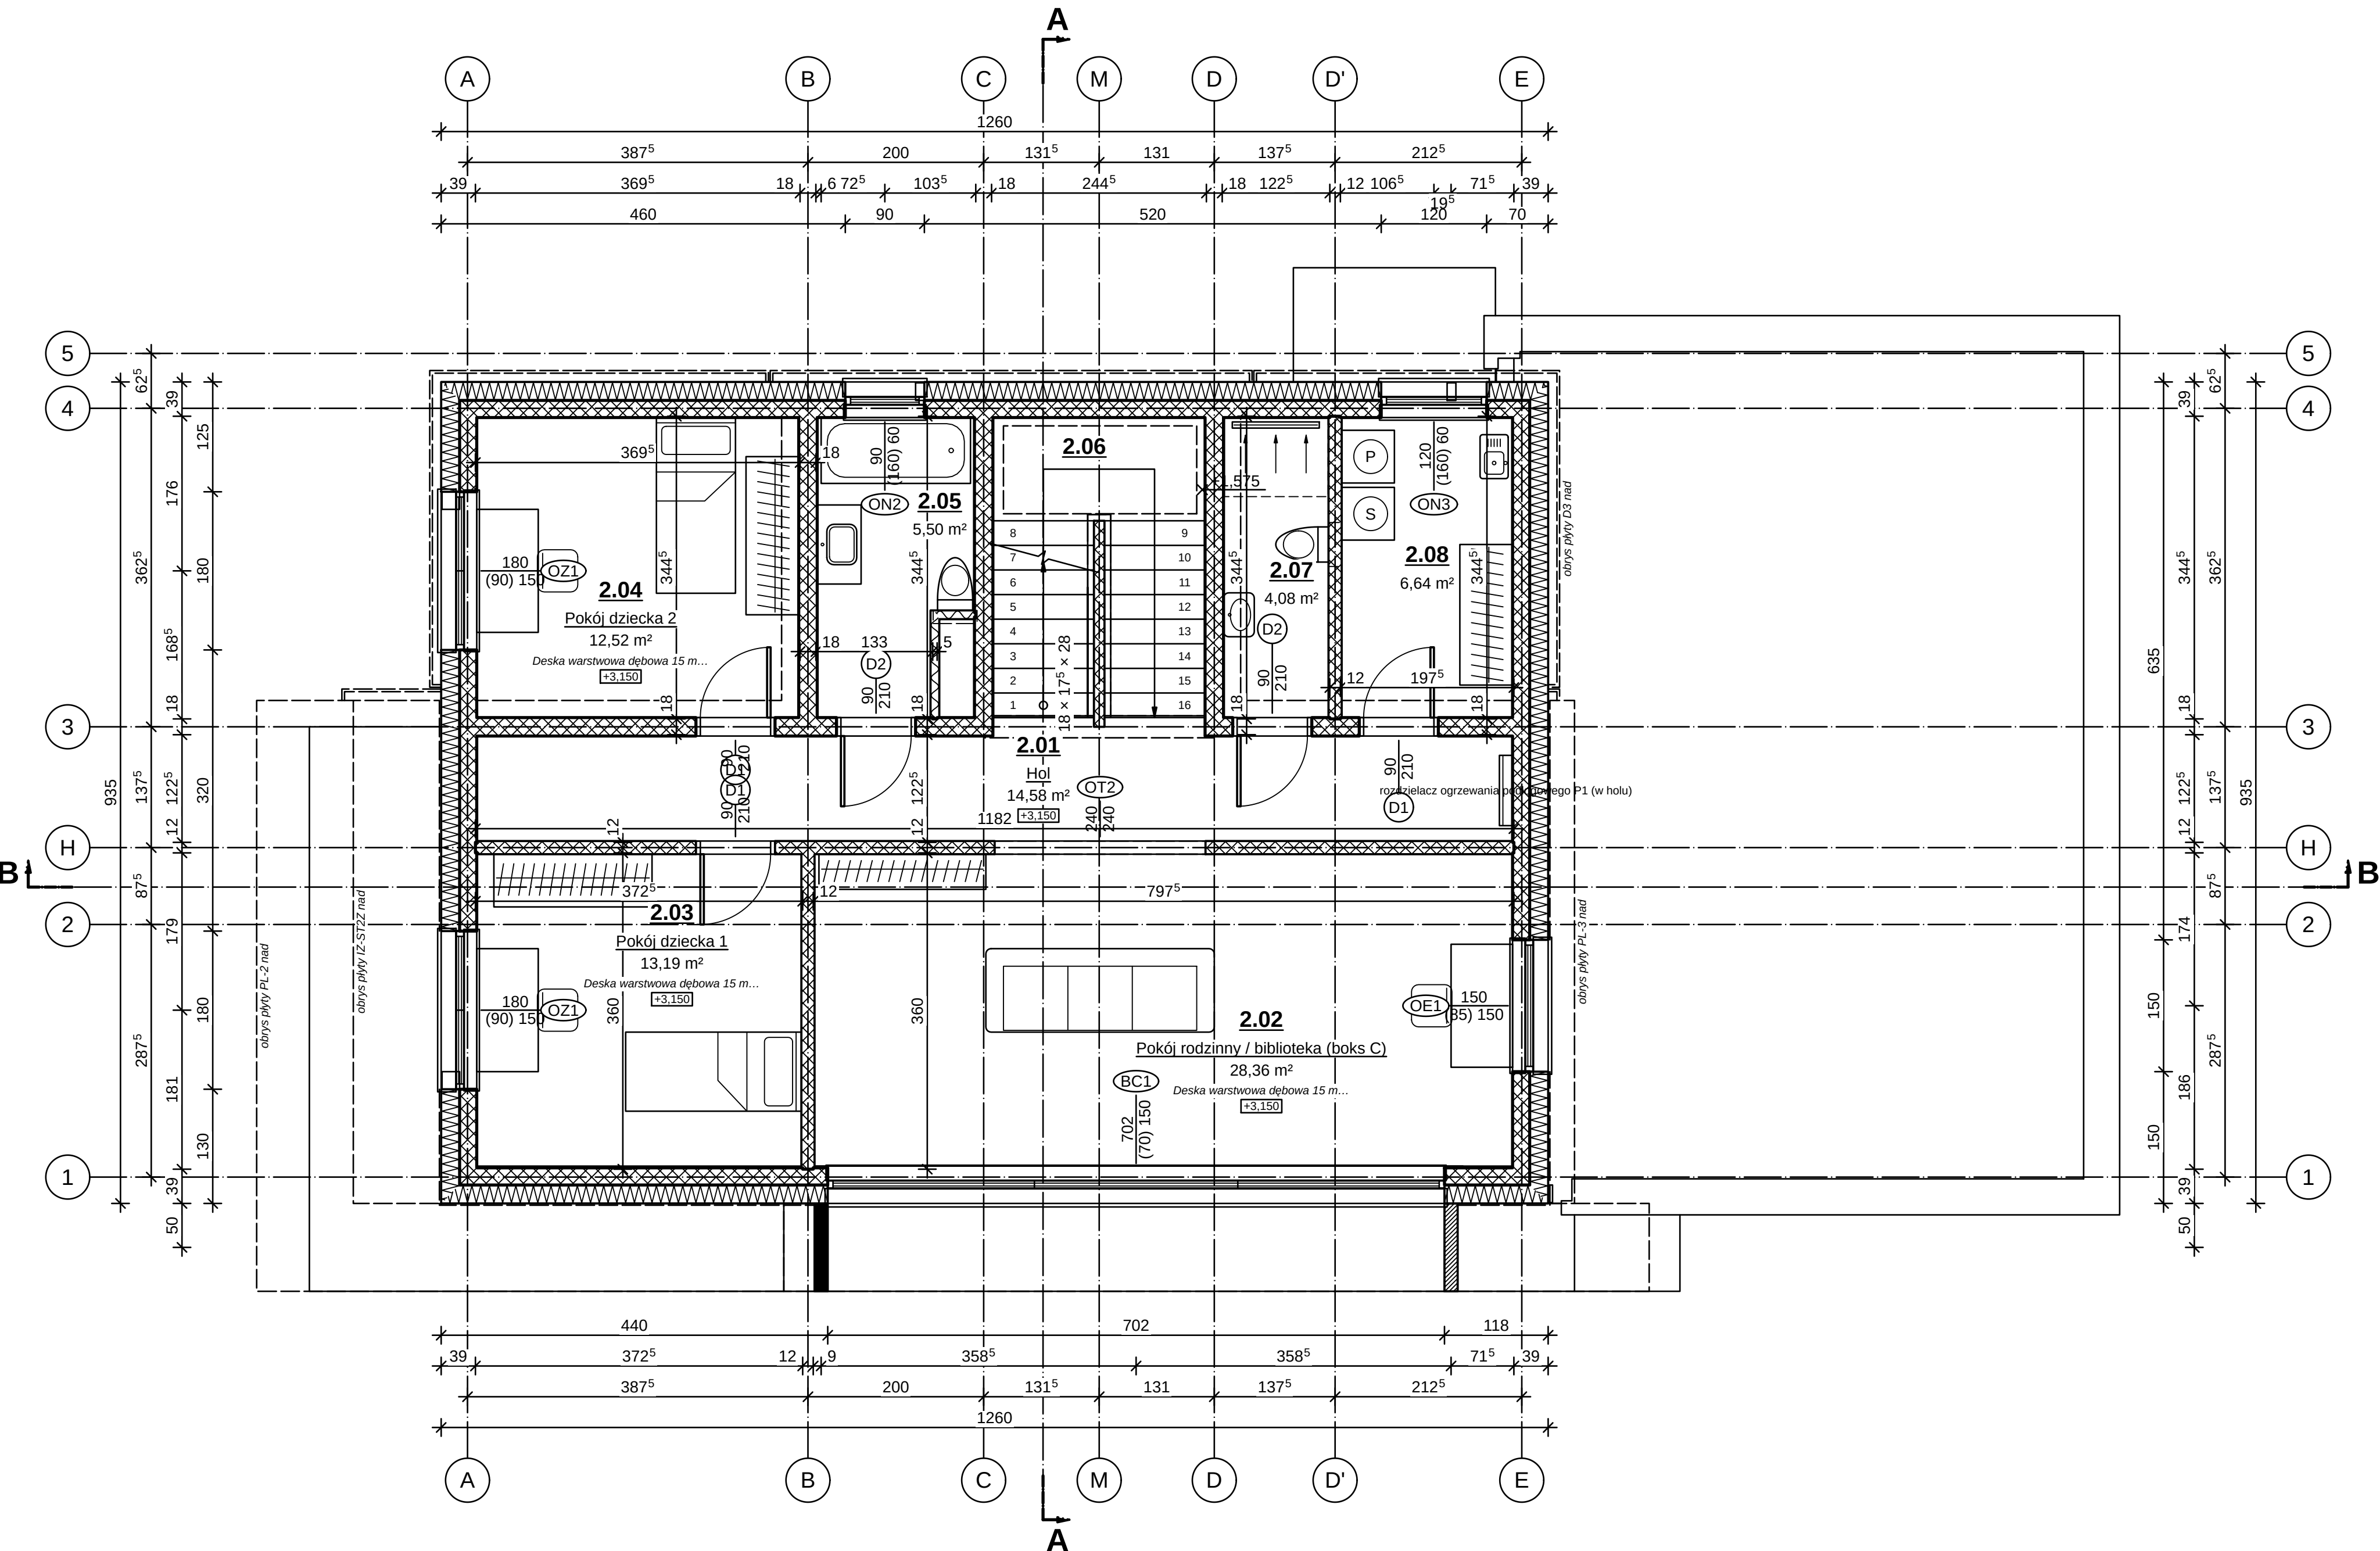

ZESTAWIENIE POMIESZCZEŃ

Nr	Nazwa pomieszczenia	Posadzka	Kat.	Wys. [m]	Pow. [m²]
2.02	Pokój rodzinny / biblioteka (boks C)	Deska warstwowa dębowa 15 mm, klejona	podst.	2,77	28,36
2.01	Hol	Deska warstwowa dębowa 15 mm, klejona	uchu	2,77	14,58
2.03	Pokój dziecka 1	Deska warstwowa dębowa 15 mm, klejona	podst.	2,77	13,19
2.04	Pokój dziecka 2	Deska warstwowa dębowa 15 mm, klejona	podst.	2,77	12,52
2.08	Pralnia z suszarnią	Płytki gresowe 60x120 na kleju C2TE \$1	pomoc.	2,77	6,64
2.05	Łazienka dzieci (wanna)	Płytki gresowe 60x120 na kleju C2TE \$1	pomoc.	2,77	5,50
2.07	WC z natryskiem	Płytki gresowe 60x120 na kleju C2TE \$1	pomoc.	2,77	4,08
2.06	Klatka schodowa	Deska warstwowa dębowa 15 mm, klejona	uchu	2,77	0,00
	RAZEM powierzchnia netto				84,88
	w tym użytkowa (podst. + pomoc.)				70,30

Wetna mineralna 035 (szkielet, docieplenia, ściana dom-garaz) – meander „UUU” Styropian grafitowy EPS 031 (ETICS, NRO w systemie) – zygzak „VVV”	Blockcyz wapienno-piaskowy 12 cm, kl. 15 (ściana ścianki, nogi w łazience); Blockcyz wapienno-piaskowy (śliska) 18 cm, kl. 20, gr. 1 na zaprawie cienkowarstwowej – kratka ukośna 45°/135° Rama boku C: ruszt stalowy ocynkowany w oddzielniz z blachy aluminiowej RAL 7016 (pusta w środku); Stal konstrukcyjna S355 (slaty RK, rama boku C); cynkowana ognowo + malowana proszkowo RAL 7016 – zaczerpienie
--	--

— — — — — elementy nad płaszczyzną cięcia (obrysy płyt, wsporników, brył wyższych kondygnacji)
 — — — — — elementy poniżej płaszczyzny cięcia (widok z góry)
 — — — — — osie konstrukcyjne; linia punktowa z pogrubionymi końcami — ślad przekroju

1. Wymiar: x cm (mm w indeksie górnym, np. 24⁺ = 24,5 cm), rzędne y w m względem 0+0 = 101,650 m n.p.m. (PL-EVRF7007-NH).
2. Rzut: planszyczna cisła +1,10 m nad posadzką podziemną. Linia kreskowa – elementy nad planszyczną cisłą (obrys pływ i isopiknów, brył wykopów i konstrukcji, otwory w terenie nad, belki), linie cisła – elementy poniżej wodosłupu.
3. Otwory: kątowa szerokość, min. głębokość i wysokość w m nad poziomem wysokości parapełu; symbol stołaki w zestawieniu stołaki.
4. Numeracja pomieszczeń: np. 01025 / PN-EV 01157-2 (01 – kod kondygnacji, 02 – kod pomieszczenia, 157 – kod identyfikator w zestawieniu stołaki) (parter = 0).
5. Rzut: sygnatura otwierania (lewe/prawe) w modelu – patrz od strony x , która otwiera się skrzydło.
6. Długość: wygenerowana automatycznie z modelu – `path=/od/user/aihouse/model/budynek.yaml` (wersja 1.0, 2026-09-25) – generatory lambda.views

