


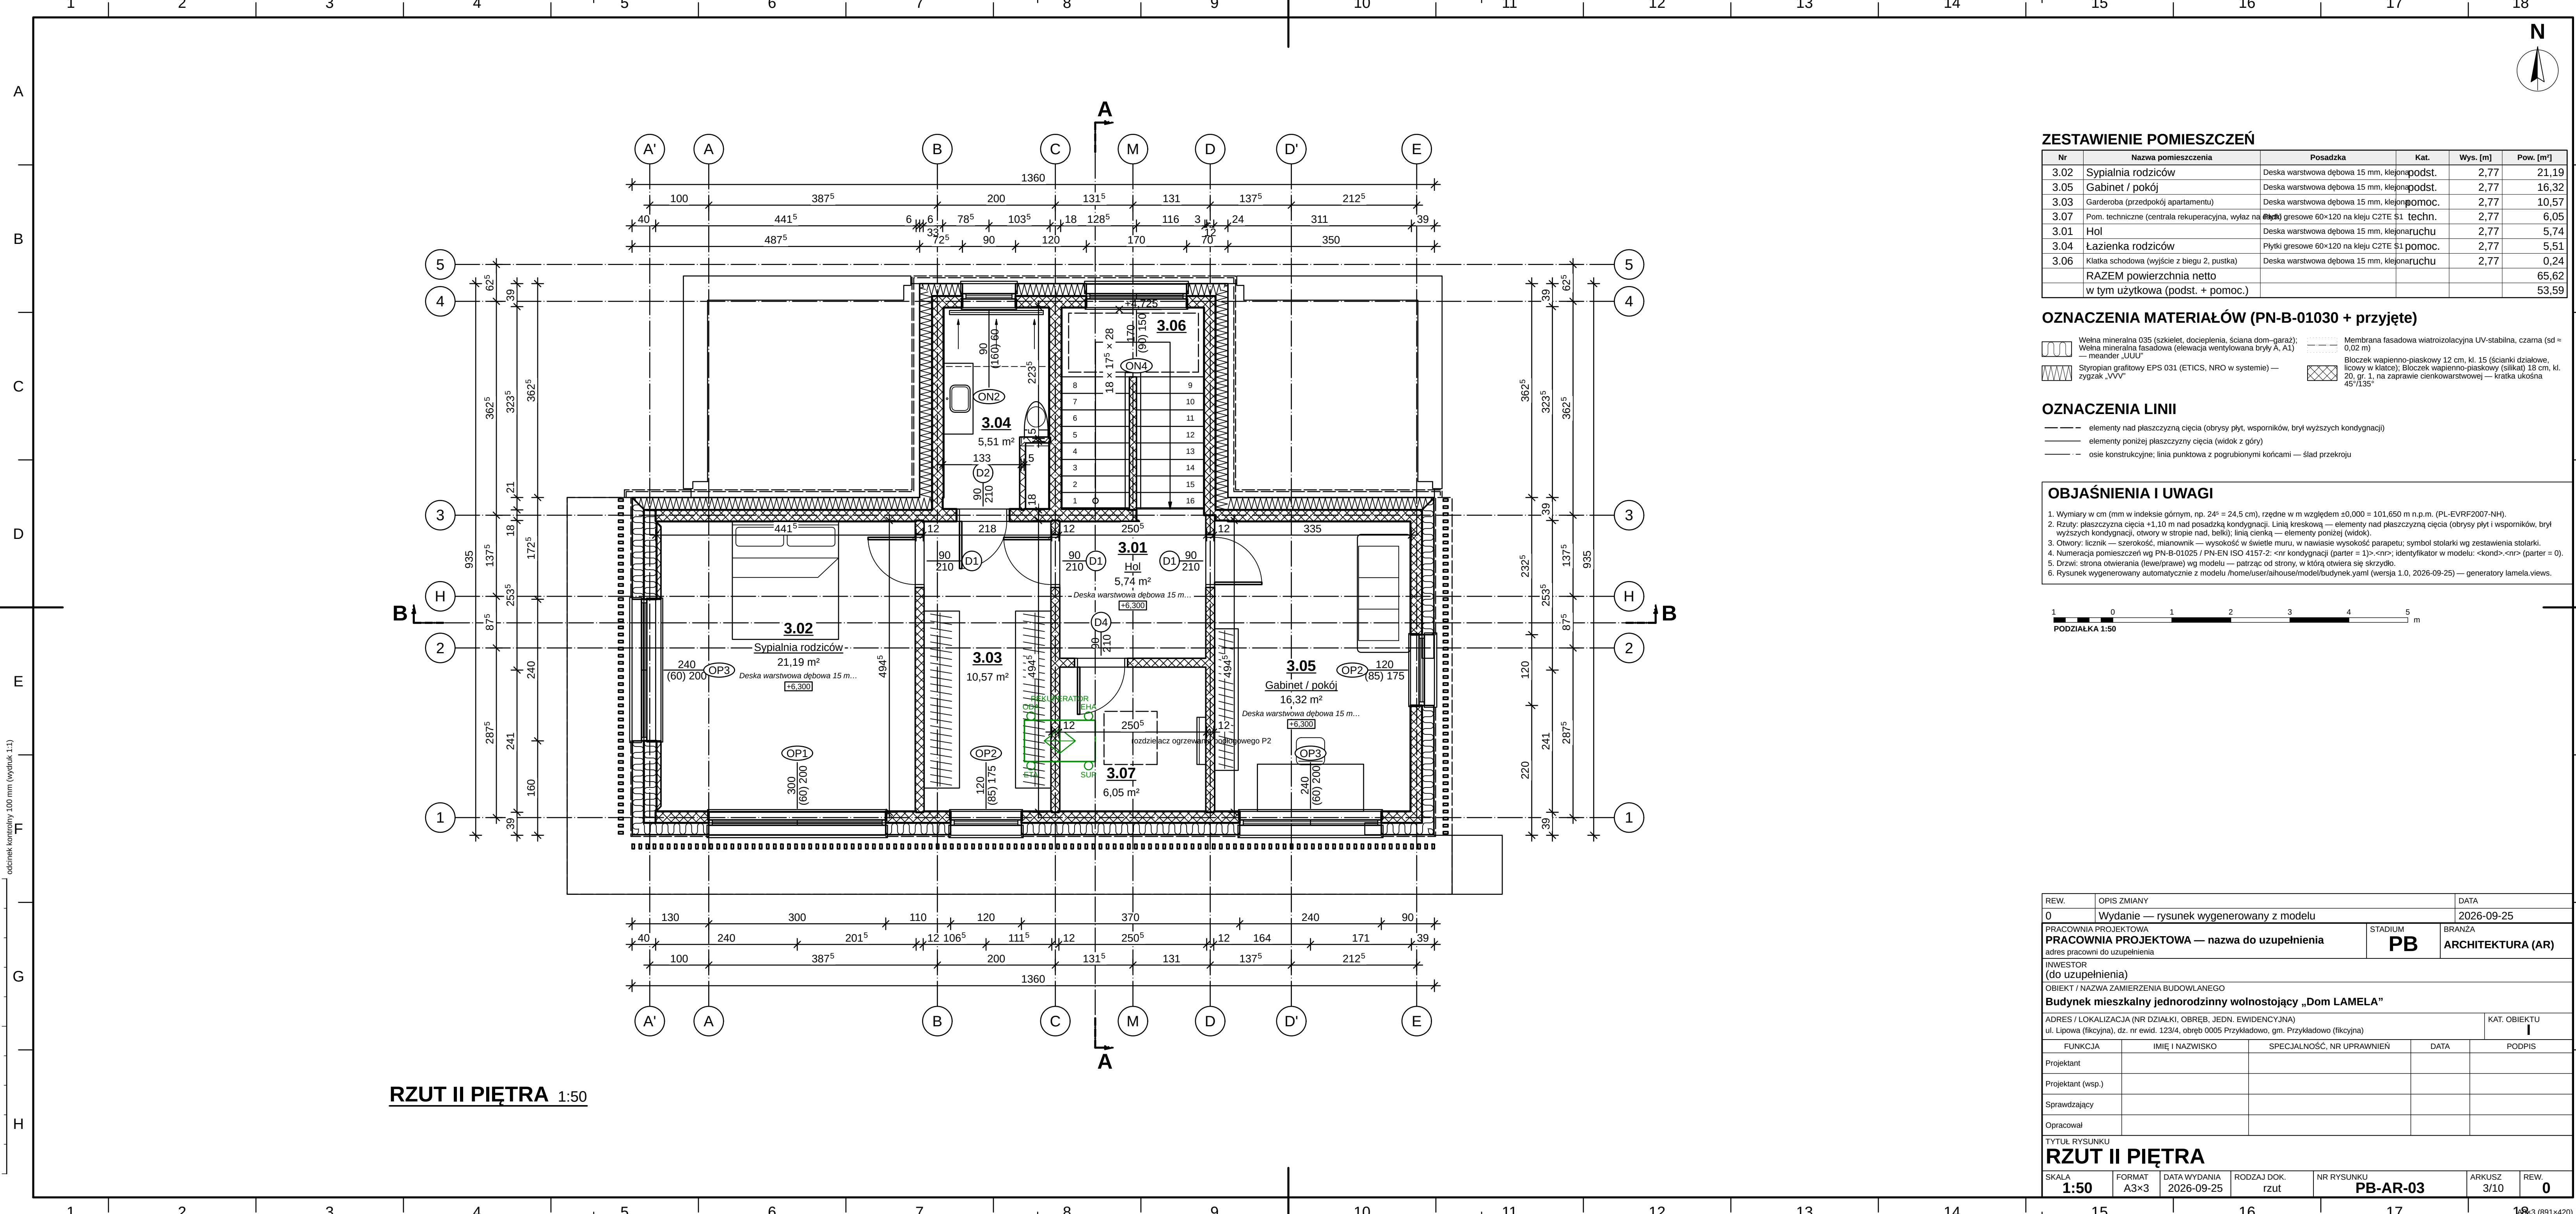

RZUT II PIĘTRA 1:50

ZESTAWIENIE POMIESZCZEŃ

Nr	Nazwa pomieszczenia	Posadzka	Kat.	Wys. [m]	Pow. [m²]
3.02	Sypialnia rodziców	Deska warstwowa dębowa 15 mm, klejona	podst.	2,77	21,19
3.05	Gabinet / pokój	Deska warstwowa dębowa 15 mm, klejona	podst.	2,77	16,32
3.03	Garderoba (przedpokój apartamentu)	Deska warstwowa dębowa 15 mm, klejona	pomoc.	2,77	10,57
3.07	Pom. techniczne (centrala rekuperacyjna, wylaz na dach)	Płytki gresowe 60×120 na kleju C2TE \$1 techn.	techn.	2,77	6,05
3.01	Hol	Deska warstwowa dębowa 15 mm, klejona	ruchu	2,77	5,74
3.04	Łazienka rodziców	Płytki gresowe 60×120 na kleju C2TE \$1	pomoc.	2,77	5,51
3.06	Klatka schodowa (wyjście z biegu 2, pustka)	Deska warstwowa dębowa 15 mm, klejona	ruchu	2,77	0,24
RAZEM powierzchnia netto					65,62
w tym użytkowa (podst. + pomoc.)					53,59

OZNACZENIA MATERIAŁÓW (PN-B-01030 + przyjęte)


	Wetna mineralna 035 (szkielet, docieplenia, ściana dom-garaż); Wetna mineralna fasadowa (elewacja wentylowana bryły A, A1)		Membrana fasadowa wiatroizolacyjna UV-stabilna, czarna (sd = 0,02 m)
	— meander „UUU”		— Błoczek wapienno-piaskowy 12 cm, kl. 15 (ścianki działkowe, licowy w klatce); Błoczek wapienno-piaskowy (silikat) 18 cm, kl. 20, gr. 1; na zaprawie cienkowarstwowej — kratka ukośna 45°/135°
	Styropian grafitowy EPS 031 (ETICS, NRO w systemie) — zygzak „VVV”		

OZNACZENIA LINII

- elementy nad płaszczyzną cięcia (obrysy płyt, wsporników, brył wyższych kondygnacji)
- elementy poniżej płaszczyzny cięcia (widok z góry)
- osie konstrukcyjne; linia punktowa z pogrubionymi końcami — ślad przekroju

OBJAŚNIENIA I UWAGI

- Wymiary w cm (mm w indeksie górnym, np. 24° = 24,5 cm), rzędne w m względem ±0,000 = 101,650 m n.p.m. (PL-EVRF2007-NH).
- Rzuty: płaszczyzna cięcia +1,10 m nad posadzką kondygnacji. Linia kreskowa — elementy nad płaszczyzną cięcia (obrysy płyt i wsporników, brył wyższych kondygnacji, otwory w stropie nad, belki); linia cienka — elementy poniżej (widok).
- Otwory: licznik — szerokość, mianownik — wysokość w świetle muru, w nawiasie wysokość parapetu; symbol stolarki wg zestawienia stolarki.
- Numeracja pomieszczeń wg PN-B-01025 / PN-EN ISO 4157-2: <nr kondygnacji (parter = 1)>.<nr>; identyfikator w modelu: <kond>.<nr> (parter = 0).
- Drzwi: strona otwierania (lewe/prawe) wg modelu — patrząc od strony, w którą otwiera się skrzydło.
- Rysunek wygenerowany automatycznie z modelu /home/user/aihouse/model/budynek.yaml (wersja 1.0, 2026-09-25) — generatory lamela views.

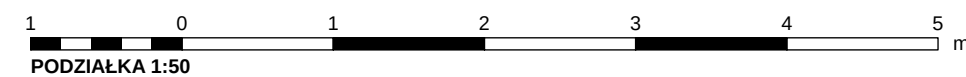

REW.	OPIS ZMIANY			DATA	
0	Wydanie — rysunek wygenerowany z modelu			2026-09-25	
PRACOWNIA PROJEKTOWA PRACOWNIA PROJEKTOWA — nazwa do uzupełnienia				STADIUM PB	BRANŻA ARCHITEKTURA (AR)
adres pracowni do uzupełnienia					
INWESTOR (do uzupełnienia)					
OBIEKT / NAZWA ZAMIERZENIA BUDOWLANEGO Budynek mieszkalny jednorodzinny wolnostojący „Dom LAMELA”					
ADRES / LOKALIZACJA (NR DZIAŁKI, OBRĘB, JEDN. EWIDENCYJNA) ul. Lipowa (fikcyjna), dz. nr ewid. 123/4, obręb 0005 Przykładowo, gm. Przykładowo (fikcyjna)					KAT. OBIEKTU I
FUNKCJA		IMIĘ I NAZWISKO		SPECJALNOŚĆ, NR UPRAWNIENI	DATA
Projektant					
Projektant (wsp.)					
Sprawdzający					
Opracował					
TYTUŁ RYSUNKU					
RZUT II PIĘTRA					
SKALA	FORMAT	DATA WYDANIA	RODZAJ DOK.	NR RYSUNKU	ARKUSZ
1:50	A3×3	2026-09-25	rzut	PB-AR-03	3/10
					REW.
					0