


PROJEKT ZAGOSPODAROWANIA DZIAŁKI — CZĘŚĆ

Lp.	Nr rys.	Tytuł rysunku	Skala	Format
1	PZT-01	PLAN ZAGOSPODAROWANIA DZIAŁKI	1:500	A2
2	PZT-02	PLAN SZCZEGÓŁOWY — WYMIARY I RZĘDNE	1:200	A2
3	PZT-03	RYSUNEK KOORDYNACYJNY UZBROJENIA TERENU	1:200	A2

PRACOWNIA PROJEKTOWA PRACOWNIA PROJEKTOWA — nazwa do uzupełnienia		STADIUM PB	BRANŻA ZAGOSPODAROWANIE TERENU			
INWESTOR (do uzupełnienia)						
OBIEKT / NAZWA ZAMIERZENIA BUDOWLANEGO Budynek mieszkalny jednorodzinny wolnostojący „Dom LAMELA” z zagospodarowaniem działki						
ADRES / LOKALIZACJA (NR DZIAŁKI, OBRĘB, JEDN. EWIDENCYJNA) ul. Lipowa (fikcyjna), dz. nr ewid. 123/4, obręb 0005 Przykładowo, gm. Przykładowo (fikcyjna)				KAT. OBIEKTU I		
FUNKCJA	IMIĘ I NAZWISKO	SPECJALNOŚĆ, NR UPRAWNIEŃ	DATA	PODPIS		
Projektant						
Projektant (wsp.)						
Sprawdzający						
Opracował						
TYTUŁ RYSUNKU SPIS RYSUNKÓW						
SKALA —	FORMAT A4	DATA WYDANIA 2026-09-25	RODZAJ DOK. spis	NR RYSUNKU PZT-00	ARKUSZ —	REW.

MAPA DO CELÓW PROJEKTOWYCH — PODKŁAD PRZYKŁADOWY

PODKŁAD PRZYKŁADOWY — mapa do celów projektowych fikcyjna [DANE PRZYKŁADOWE – FIKCYJNE], narysowana z modelu działki (działka.yaml); w projekcie rzeczywistym — aktualna mapa do celów projektowych wg art. 34 ust. 3 pkt 1 PB (z klauzulą urzędową lub oświadczeniem geodety — art. 34b PB), treść i opis mapy wg § 32–33 rozp. w sprawie standardów technicznych (t.j. Dz.U. 2022 poz. 1670), znaki wg zał. 4 rozp. w sprawie BDOT500 i mapy zasadniczej (Dz.U. 2021 poz. 1385; oba akty zweryfikowane w ELI 25.09.2026 — status: obowiązujące).

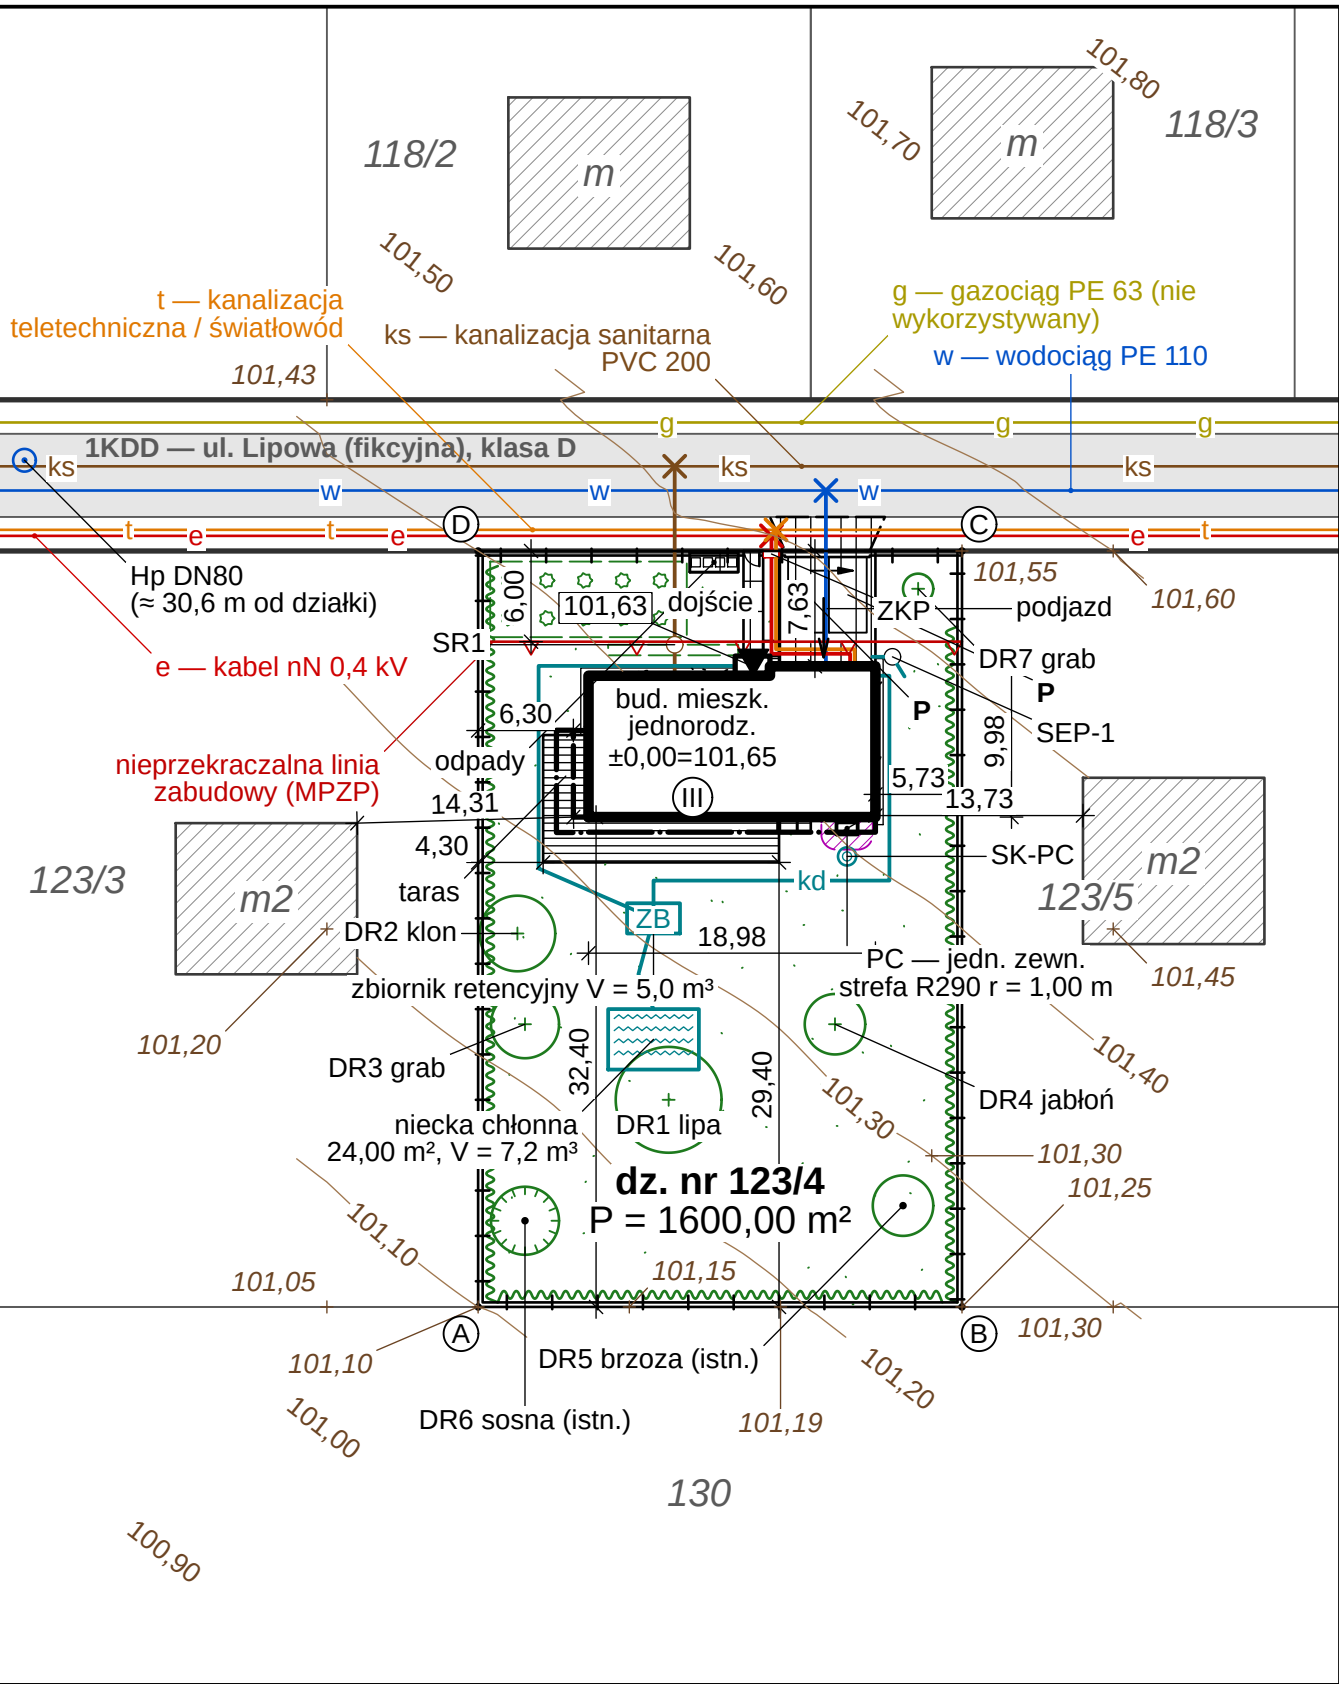

PLAN ZAGOSPODAROWANIA DZIAŁKI 1:500

ZESTAWIENIE POWIERZCHNI I WSKAŹNIKÓW ZAGOSPODAROWANIA (RPB § 14 pkt 4, MPZP)

Wskaźnik / element	Projekt	MPZP / wymaganie	Zgodność
Powierzchnia działki nr 123/4	1600,00 m ²	—	
Pow. zabudowy (upzp art. 2 pkt 35)	187,50 m ²	≤ 480,00 m ²	TAK
Udział pow. zabudowy	11,72%	≤ 30%	TAK
– z płytami i okapami (kontrolnie)	218,08 m ² (13,63%)	informacyjnie	TAK
Drogi, dojścia, place	64,87 m ²	—	
Taras naziemne, podesty	67,27 m ²	—	
Opaska żwirowa	13,13 m ²	—	
PBC (upzp art. 2 pkt 28)	1269,84 m ² (79,36%)	≥ 800,00 m ² (50%)	TAK
– z 50 % dachu ziel. D4 (rezerwa)	1299,37 m ² (81,21%)	informacyjnie	
Pow. kondygnacji nadz. (P0+P1+P2)	396,39 m ²	80,00 m ² –1280,00 m ²	TAK
Nadziemna intensywność zabudowy	0,248	0,05–0,80	TAK
Wysokość zabudowy (art. 2 pkt 30)	10,28 m	≤ 11,00 m	TAK
Wysokość budynku (WT § 6)	9,94 m	N: ≤ 12,00 m	TAK
Kondygnacje nadziemne	3	≤ 3	TAK
Miejsca postojowe (garaż + zewn.)	2 + 2	≥ 2	TAK
Dach — kąt nachylenia	1,1° (płaski)	płaski ≤ 12° lub 30–45°	TAK
Lico ścian od linii zabudowy	1,63 m	nie przekraczać	TAK
Elementy poza linią zabudowy	brak	—	

MPZP: uchwała nr XII/123/2024 Rady Gminy Przykładowo z 21.03.2024 — teren 3MN (fikcyjny). Limity: konfiguracja arkuszy (brief § 3) — BRAK W MODELU [DO UZUPEŁNIENIA]. Wartości z modułu lamela.wskazniki (jedyne źródło; definicje upzp art. 2 pkt 28–35, t.j. Dz.U. 2026 poz. 538): PBC bez nawierzchni ażurowych, opaski, pojemników i terenu nad zbiornikiem; dach zielony (≥ 10 m²) w 50 % — tylko rezerwa. Wysokość zabudowy = z_{top} 111,68 (wywiewka kanalizacyjna 1 (z = pokrycie + 0,50 m — ZAŁOŻENIE, brak rzędnej w modelu)) – t_{śr} 101,40 (t_{min} 101,32, t_{max} 101,48 na obwodzie rzutu ścian zewn.; w każdym punkcie niższa z rzędnych terenu istniejącego/projektowanego); bez założenia: 10,25 m (czerpnia wentylacji (dachowa)). WT § 6: od terenu przy wejściu O0-O4 (101,33) do wierzchu stropodachu D1 (bez attyki) — grupa N.

ODLEGŁOŚCI OD GRANIC DZIAŁKI (WT § 12)

Granica	Element (płaszczyzna ściany)	Odl. [m]	Wymagana [m]	Zgodność
S (130)	ściana P0 z otworami	32,40	≥ 4,00	TAK
S (130)	T1 — okap/płyta/taras	29,40	≥ 1,50	TAK
E (123/5)	ściana P0 z otworami	5,73	≥ 4,00	TAK
E (123/5)	ściana P2 bez otworów	15,60	≥ 3,00	TAK
E (123/5)	PL-D — okap/płyta/taras	5,73	≥ 1,50	TAK
N (1KDD)	ściana P0 z otworami	7,63	nie dot. (ust. 10)	—
N (1KDD)	ściana P2 bez otworów	11,88	nie dot. (ust. 10)	—
N (1KDD)	PL-DA — okap/płyta/taras	6,95	nie dot. (ust. 10)	—
W (123/3)	ściana P2 z otworami	6,30	≥ 4,00	TAK
W (123/3)	ściana P2 bez otworów	11,18	≥ 3,00	TAK
W (123/3)	T1 — okap/płyta/taras	4,30	≥ 1,50	TAK

WT § 12 ust. 1: 4,00 m — ściana z oknami/drzwiami, 3,00 m — bez otworów (każda płaszczyzna ściany osobno); ust. 6: 1,50 m — okap, taras, daszek; ust. 10: od działki drogowej — nie dotyczy. Odległość w poziomie w miejscu najmniejszego oddalenia (§ 9). WT stosowane na podstawie art. 102a PB.

LEGENDA


	zasięg podkładu mapowego (mapa do celów projektowych — PRZYKŁADOWA)		ogrodzenie projektowane (poz. 2.8; na granicy — odsunięte graficznie)
	granica działki budowlanej, punkt graniczny, narożnik (PN-B-01027 poz. 2.7)		brama przesuwana (poz. 2.9)
	linia rozgraniczająca drogi publicznej (PN-B-01027 poz. 2.5)		furtka otwierana do wewnątrz działki (WT § 42)
	jezdnia drogi publicznej (wg mapy)		jednostka zewn. pompy ciepła (fundament) i strefa czynnika R290
	budynek istniejący (mapa); m2 — mieszkalny, 2 kondygnacje		zbiornik retencyjny szczelny (ZB)
	nieprzekraczalna linia zabudowy wg MPZP (PN-B-01027 poz. 2.2)		niecka chłonna — ogród deszczowy (przelew zbiornika)
	budynek projektowany — obrys ścian parteru 1,0 m nad terenem (poz. 1.1)		miejsce włączenia przyłącza do sieci (PN-B-01027 poz. 6)
	obrys wyższych kondygnacji poza obrysem parteru (poz. 1.6 d)		złącze kablowo-pomiarowe ZKP (w linii ogrodzenia)
	obrys płyt wspornikowych, okapów i daszku — przewieszenia (poz. 1.6 c)		studzienka rewizyjna kanalizacji
	rzędna ±0,00 (posadzka parteru) w m n.p.m.; w kółku liczba kondygnacji nadziemnych		studnia chłonna skroplin pompy ciepła
	wejście główne do budynku (poz. 1.7)		hydrant zewnętrzny na sieci (Hp)
	wjazd do garażu		warstwa terenu istniejącego (PN-B-01027 poz. 5.2)
	zjazd z drogi publicznej — wg zezwolenia zarządcy drogi [DO UZUPEŁNIENIA]		rzędna terenu istniejącego [m n.p.m.]
	nawierzchnia z kostki betonowej (poz. 7.10)		rzędna terenu projektowanego [m n.p.m.]
	nawierzchnia z płyt betonowych (poz. 7.11)		wymiar / odległość w m z dokładnością 0,01 m
	płyty w trawie (ażur) — poza PBC		w — sieć wodociągowa istniejąca (mapa)
	taras naziemny — deska kompozytowa na legarach		w — przyłącze wodociągowe projektowane
	opaska żwirowa 16/32 na geowłókninie		ks — sieć kanalizacji sanitarnej istniejąca (mapa)
	stanowisko postojowe 2,50 × 5,00 m (WT § 21)		ks — przykanalik sanitarny projektowany
	osłona pojemników na odpady — segregacja (WT § 22)		kd — kanalizacja deszczowa projektowana (kolektory, przelew)
	trawnik projektowany (poz. 7.8)		e — linia kablowa nN istniejąca (mapa)
	rabata z krzewami		e — kabel nN projektowany (ZKP → RG)
	żywoplot projektowany (poz. 7.6)		t — sieć telekomunikacyjna istniejąca (mapa)
	drzewo liściaste projektowane (poz. 7.1)		t — przyłącze telekomunikacyjne projektowane
	drzewo istniejące — zachowane (poz. 7.2)		g — sieć gazowa istniejąca (mapa)

OBSZAR ODDZIAŁYWANIA OBIEKTU (PB art. 3 pkt 20; RPB § 14 pkt 8)


Obszar oddziaływania obiektu mieści się w całości w granicach działki 123/4 (PB art. 3 pkt 20); odległości od granic ≥ 4,0 m (ściany z otworami ≥ 5,70 m, płyty ≥ 5,20 m), przesłanianie i nasłonecznienie sąsiednich budynków (≥ 8 m od granic) bez ograniczeń (WT §13, §60), hałas PC ≤ 40 dB(A) nocą na granicy (W-024), wody opadowe zagospodarowane na działce (PW art. 234), brak odprowadzania na drogie. Podstawa ustalenia (RPB § 18 pkt 1): WT § 12, 13, 19, 23, 28–29, 60, 271 (art. 102a PB); u.d.p. art. 43; POŚ art. 144 ust. 2 i rozp. MŚ w sprawie dopuszczalnych poziomów hałasu (Dz.U. 2014 poz. 112); PW art. 234; ustalenia MPZP.

OBJAŚNIENIA I UWAGI

- Wymiary i odległości w m (dokładność 0,01 m), rzędne w m n.p.m. (PL-EVRF2007-NH).
- Układ współrzędnych: lokalny układ działki (x → wschód, y → północ, początek w narożniku A); w projekcie rzeczywistym — układ PL-2000 strefa 6 z mapy do celów projektowych.
- Obrys budynku — lico zewnętrzne ścian parteru na wys. 1,0 m nad terenem; wspornik bryły A (II piętro) — obrys wyższych kondygnacji; płyty wspornikowe, okapy i daszki — przewieszenia (PN-B-01027 poz. 1.6).
- Wody opadowe zagospodarowane w granicach działki: rury spustowe → kolektory KD → zbiornik retencyjny szczelny → przelew do niecki chłonnej; odwodnienie liniowe przed bramą — brak spływu na drogę (MPZP; u.d.p. art. 39 ust. 1 pkt 9; WT § 28–29).
- Wymiary i rzędne szczegółowe — rys. PZT-02; uzbrojenie i koordynacja sieci — rys. PZT-03.
- Zjazd z drogi 1KDD pokazano jako przedłużenie bramy do krawędzi jezdni — geometria zastępcza [DO UZUPEŁNIENIA]: szerokość, skosy/łuki, nawierzchnia i przepust wg zezwolenia zarządcy drogi (u.d.p. art. 29 ust. 3a).
- Braki danych modelu (9 poz.) oznaczono [DO UZUPEŁNIENIA]; wykaz: projekt/02_PZT/BRAKI_DANYCH.mxd.
- Rysunek wygenerowany automatycznie z modelu model/budynek.yaml (wersja 1.0, 2026-09-25) — generatory lamela.views.

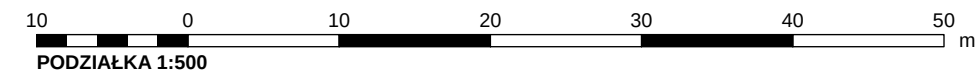

REW.	OPIS ZMIANY	DATA
0	Wydanie — rysunek wygenerowany z modelu	2026-09-25
PRACOWNIA PROJEKTOWA PRACOWNIA PROJEKTOWA — nazwa do uzupełnienia adres pracowni do uzupełnienia	STADIUM PB	BRANŻA ZAGOSPODAROWANIE TERENU
INWESTOR (do uzupełnienia)	OBJEKT / NAZWA ZAMIERZENIA BUDOWLANEGO Budynek mieszkalny jednorodzinny wolnostojący „Dom LAMELA” z zagospodarowaniem działki	
ADRES / LOKALIZACJA (NR DZIAŁKI, OBRĘB, JEDN. EWIDENCYJNA) ul. Lipowa (fikcyjna), dz. nr ewid. 123/4, obręb 0005 Przykładowo, gm. Przykładowo (fikcyjna)		KAT. OBIEKTU I
FUNKCJA	IMIĘ I NAZWISKO	SPECJALNOŚĆ, NR UPRAWNIENI
Projektant		DATA
Projektant (wsp.)		PODPIS
Sprawdzający		
Opracował		
TYTUŁ RYSUNKU PLAN ZAGOSPODAROWANIA DZIAŁKI		
SKALA 1:500	FORMAT A2	DATA WYDANIA 2026-09-25
RODZAJ DOK. plan zagospodarowania	NR RYSUNKU PZT-01	ARKUSZ 1/3
REW. 0		

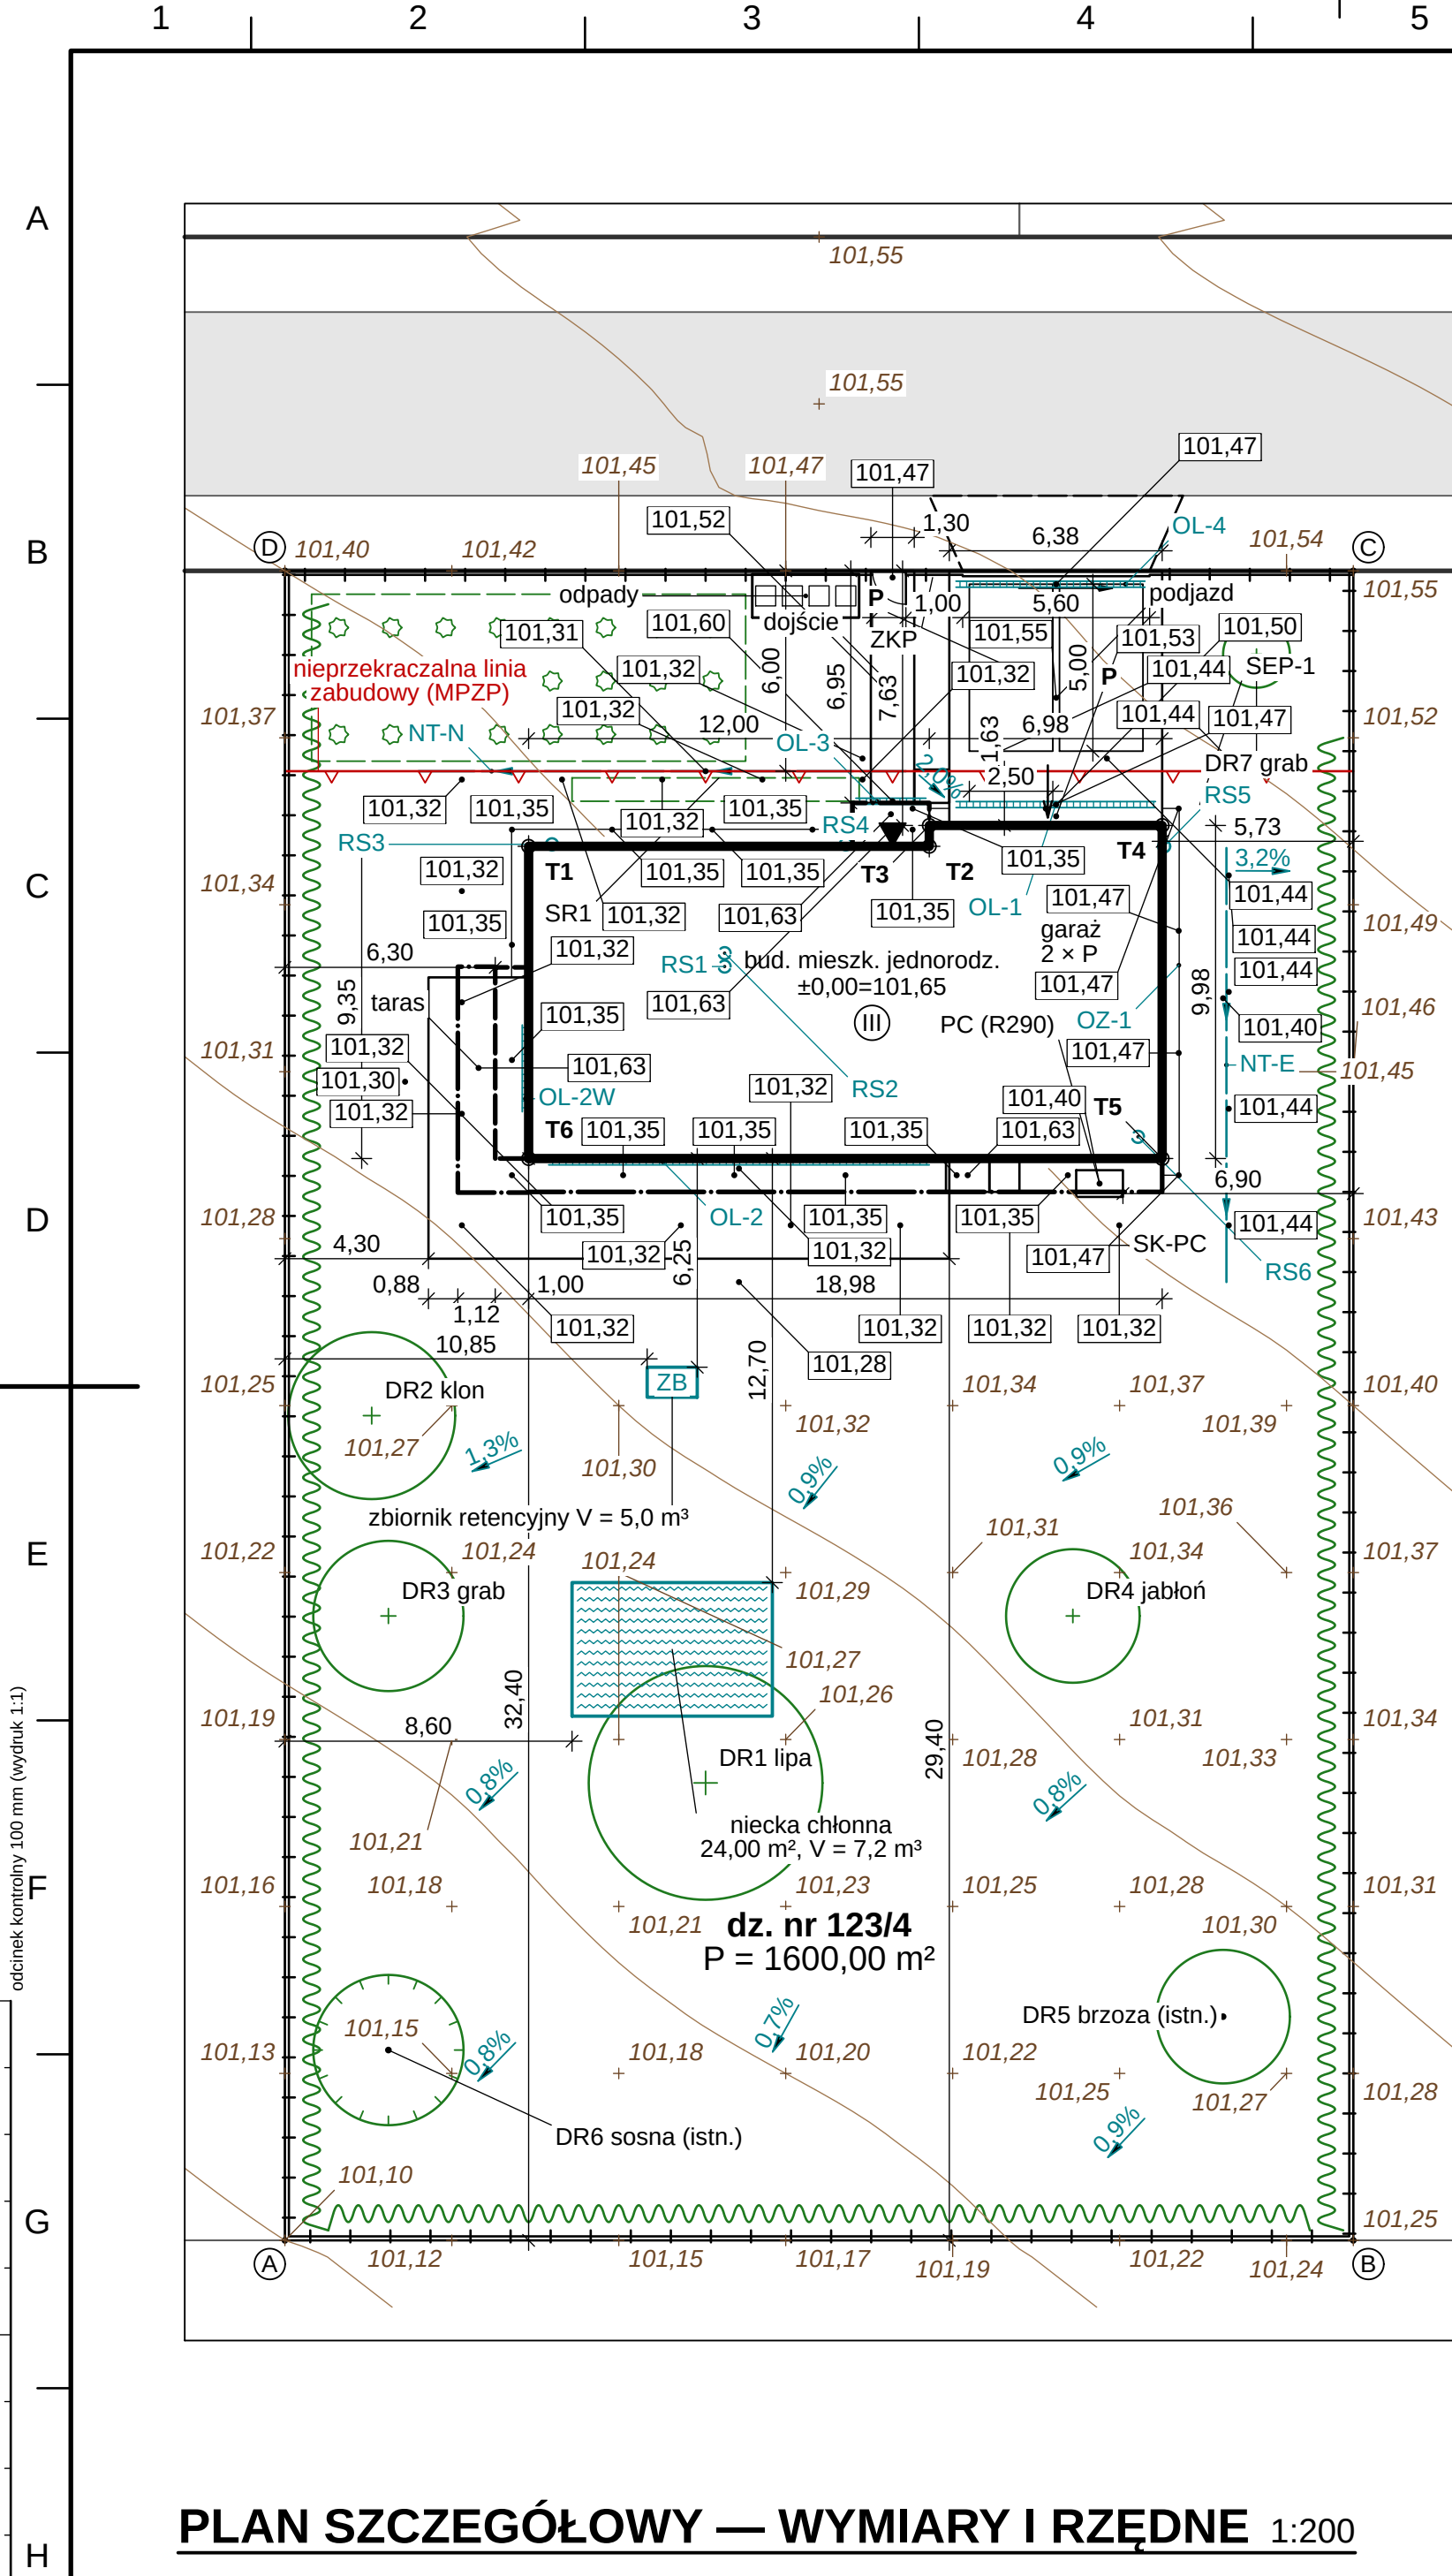

PLAN SZCZEGÓŁOWY — WYMIARY I RZĘDNE 1:200

WYKAZ PUNKTÓW TYCZENIA I GRANICZNYCH

Pkt	x [m]	y [m]	Opis
T1	7,30	41,75	narożnik obrysu parteru
T2	19,30	41,75	narożnik obrysu parteru
T3	19,30	42,38	narożnik obrysu parteru
T4	26,28	42,38	narożnik obrysu parteru
T5	26,28	32,40	narożnik obrysu parteru
T6	7,30	32,40	narożnik obrysu parteru
A	0,00	0,00	punkt graniczny działki
B	32,00	0,00	punkt graniczny działki
C	32,00	50,00	punkt graniczny działki
D	0,00	50,00	punkt graniczny działki

Układ lokalny działki: początek — narożnik A, x → wschód, y → północ. W projekcie rzeczywistym współrzędne w układzie PL-2000 (X — północ, Y — wschód) z mapy do celów projektowych; tyczenie — geodeta uprawniony (PB art. 43 ust. 1).

RZĘDNE CHARAKTERYSTYCZNE [m n.p.m.]

Poziom	Rzędna
±0,00 — posadzka parteru	101,65
T1 — deska kompozytowa...	101,63
T2 — płyty betonowe 60...	101,63
T3 — płyty betonowe 60...	101,63
teren proj. przy wejściu głównym	101,63
teren na obwodzie ścian — min.	101,32
teren na obwodzie ścian — maks.	101,48
najwyższy punkt budynku	111,68
zwierciadło wody gruntowej (ZWG)	97,60

Rzędne projektowane terenu: spadek ≥ 2 % od budynku; na granicach działki rzędne istniejące (bez zmiany spływu na działki sąsiednie — WT § 29, PW art. 234).

ODWODNIENIE POWIERZCHNIOWE

Ozn.	Typ	Wymiar	Spadek	Odbiornik
OL-1	liniowe	L = 5,98 m	0,5 %	SEP-1 → NT-E
OL-2	liniowe	L = 11,40 m	0,5 %	opaska / KD-W
OL-2W	liniowe	L = 2,60 m	0,5 %	KD-W
OL-3	liniowe	L = 2,10 m	0,5 %	KD-W
OL-4	liniowe	L = 5,98 m	0,5 %	SEP-1 → NT-E
OZ-1	opaska żwir.	b = 0,50 m	—	—
NT-N	niecka	L = 14,60 m	0,5 %	KD-W
NT-E	niecka	L = 13,00 m	0,6 %	ogród pd.
NCH-1	niecka	A = 24,00 m²	—	grunt (piaski, ZWG...

DR-0: NIE PROJEKTUJE SIĘ — piaski przepuszczalne, ZWG ≈ 3,8 m p.p.t., posadowienie ≈ 0,5 m p.p.t. (W-285); ochrona płyty: XPS + membrana SBS, opaska żwirowa i spadki terenu

NAWIERZCHNIE UTWARDZONE I TARASY

Ozn.	Nawierzchnia	Pow.	Spadek
U1	podjazd	48,61 m²	1,5 %
U2	dojście	9,04 m²	2,0 %
U3	łącznik dojście–podjazd	1,05 m²	2,0 %
U4	stanowisko pojemników	4,16 m²	2,0 %
U5	fundament jednostki zewn....	1,12 m²	—
U6	ścieżka gospodarcza	0,90 m²	2,0 %
T1	deska kompozytowa na lega...	63,08 m²	rz. 101,63
T2	płyty betonowe 60×60 na p...	2,99 m²	rz. 101,63
T3	płyty betonowe 60×60, spa...	1,30 m²	rz. 101,63

Kierunek spadku — strzałki na rysunku (od budynku, do odwodnień liniowych i niecek).

ODLEGŁOŚCI URZĄDZEŃ RETENCJI I PC

Element	Od	d [m]	min [m]	Zgodność
zbiornik	budynek	6,70	3,00	TAK
zbiornik	granica	11,60	2,00	TAK
zbiornik	drzewo	9,06	1,00	TAK
niecka	budynek	12,70	3,00	TAK
niecka	granica	8,60	2,00	TAK
niecka	drzewo	2,00	1,00	TAK
strefa R290	otwory, wpusty, studzienki	—	r = 1,00	TAK

Wymagania retencji — założenia projektowe (R8 pkt 3.5, W-144/W-145; nie przepis); zbiornik — odległość od środka (brak wymiarów w modelu); strefa R290 — W-156 (wytyczne producenta).

LEGENDA


	żywoplot projektowany (poz. 7.6)
	drzewo liściaste projektowane (poz. 7.1)
	drzewo istniejące — zachowane (poz. 7.2)
	ogrodzenie projektowane (poz. 2.8; na granicy — odsunięte graficznie)
	brama przesuwna (poz. 2.9)
	furtka otwierana do wewnątrz działki (WT § 42)
	zbiornik retencyjny szczelny (ZB)
	niecka chłonna — ogród deszczowy (przelew zbiornika)
	odwodnienie liniowe
	niecka trawiasta — grot w kierunku spływu
	rura spustowa: zewnętrzna / w szachcie (RS)
	warstwa terenu istniejącego (PN-B-01027 poz. 5.2)
	rzędna terenu istniejącego [m n.p.m.]
	rzędna terenu projektowanego [m n.p.m.]
	spadek nawierzchni [%] — grot w kierunku spadku
	kierunek spływu wód opadowych, spadek terenu [%]
	wymiar / odległość w m z dokładnością 0,01 m
	punkt tyczenia (narożnik obrysu parteru) — wykaz współrzędnych

OBJAŚNIENIA I UWAGI

- Wymiary i odległości w m (dokładność 0,01 m), rzędne w m n.p.m. (PL-EVRF2007-NH).
- Wymiary obrysu — lico zewnętrzne ścian parteru (1,0 m nad terenem); odległości od granic w miejscu najmniejszego oddalenia (WT § 9), z dokładnością 0,01 m (RPB § 15 ust. 3 w brzmieniu Dz.U. 2026 poz. 597, od 5.11.2026 — stosowane).
- Rzędne terenu istniejącego — z mapy (przykładowej); projektowanego — z modelu (działka.yaml: teren.punkty_projektowane); spadki nawierzchni wg modelu, kierunek wg terenu projektowanego; kierunki spływu na trawnikach — wg spadku terenu projektowanego (interpolacja).
- Wody opadowe z nawierzchni i dachów — na teren własny, do niecek i zbiornika (WT § 28 ust. 2); zakaz zmiany spływu w kierunku działek sąsiednich (WT § 29) i odprowadzania na drogę (u.d.p. art. 39).
- Punkty tyczenia — narożniki obrysu zewnętrznego ścian parteru; współrzędne w wykazie obok rysunku.
- Zjazd — geometria zastępcza [DO UZUPEŁNIENIA] (wg zezwolenia zarządcy drogi).
- Braki danych modelu oznaczono [DO UZUPEŁNIENIA]; wykaz: projekt/02_PZT/BRAKI_DANYCH.md.
- Rysunek wygenerowany automatycznie z modelu model/budynek.yaml (wersja 1.0, 2026-09-25) — generatory lamela.views.



REW.	OPIS ZMIANY			DATA			
0	Wydanie — rysunek wygenerowany z modelu			2026-09-25			
PRACOWNIA PROJEKTOWA PRACOWNIA PROJEKTOWA — nazwa do uzupełnienia adres pracowni do uzupełnienia			STADIUM PB	BRANŻA ZAGOSPODAROWANIE TERENU			
INWESTOR (do uzupełnienia)							
OBIEKT / NAZWA ZAMIERZENIA BUDOWLANEGO Budynek mieszkalny jednorodzinny wolnostojący „Dom LAMELA” z zagospodarowaniem działki							
ADRES / LOKALIZACJA (NR DZIAŁKI, OBRĘB, JEDN. EWIDENCYJNA) ul. Lipowa (fikcyjna), dz. nr ewid. 123/4, obręb 0005 Przykładowo, gm. Przykładowo (fikcyjna)				KAT. OBIEKTU I			
FUNKCJA		IMIĘ I NAZWISKO	SPECJALNOŚĆ, NR UPRAWNIEŃ		DATA	PODPIS	
Projektant							
Projektant (wsp.)							
Sprawdzający							
Opracował							
TYTUŁ RYSUNKU PLAN SZCZEGÓŁOWY — WYMIARY I RZĘDNE							
SKALA 1:200	FORMAT A2	DATA WYDANIA 2026-09-25	RODZAJ DOK. plan szczegółowy	NR RYSUNKU PZT-02		ARKUSZ 2/3	REW. 0

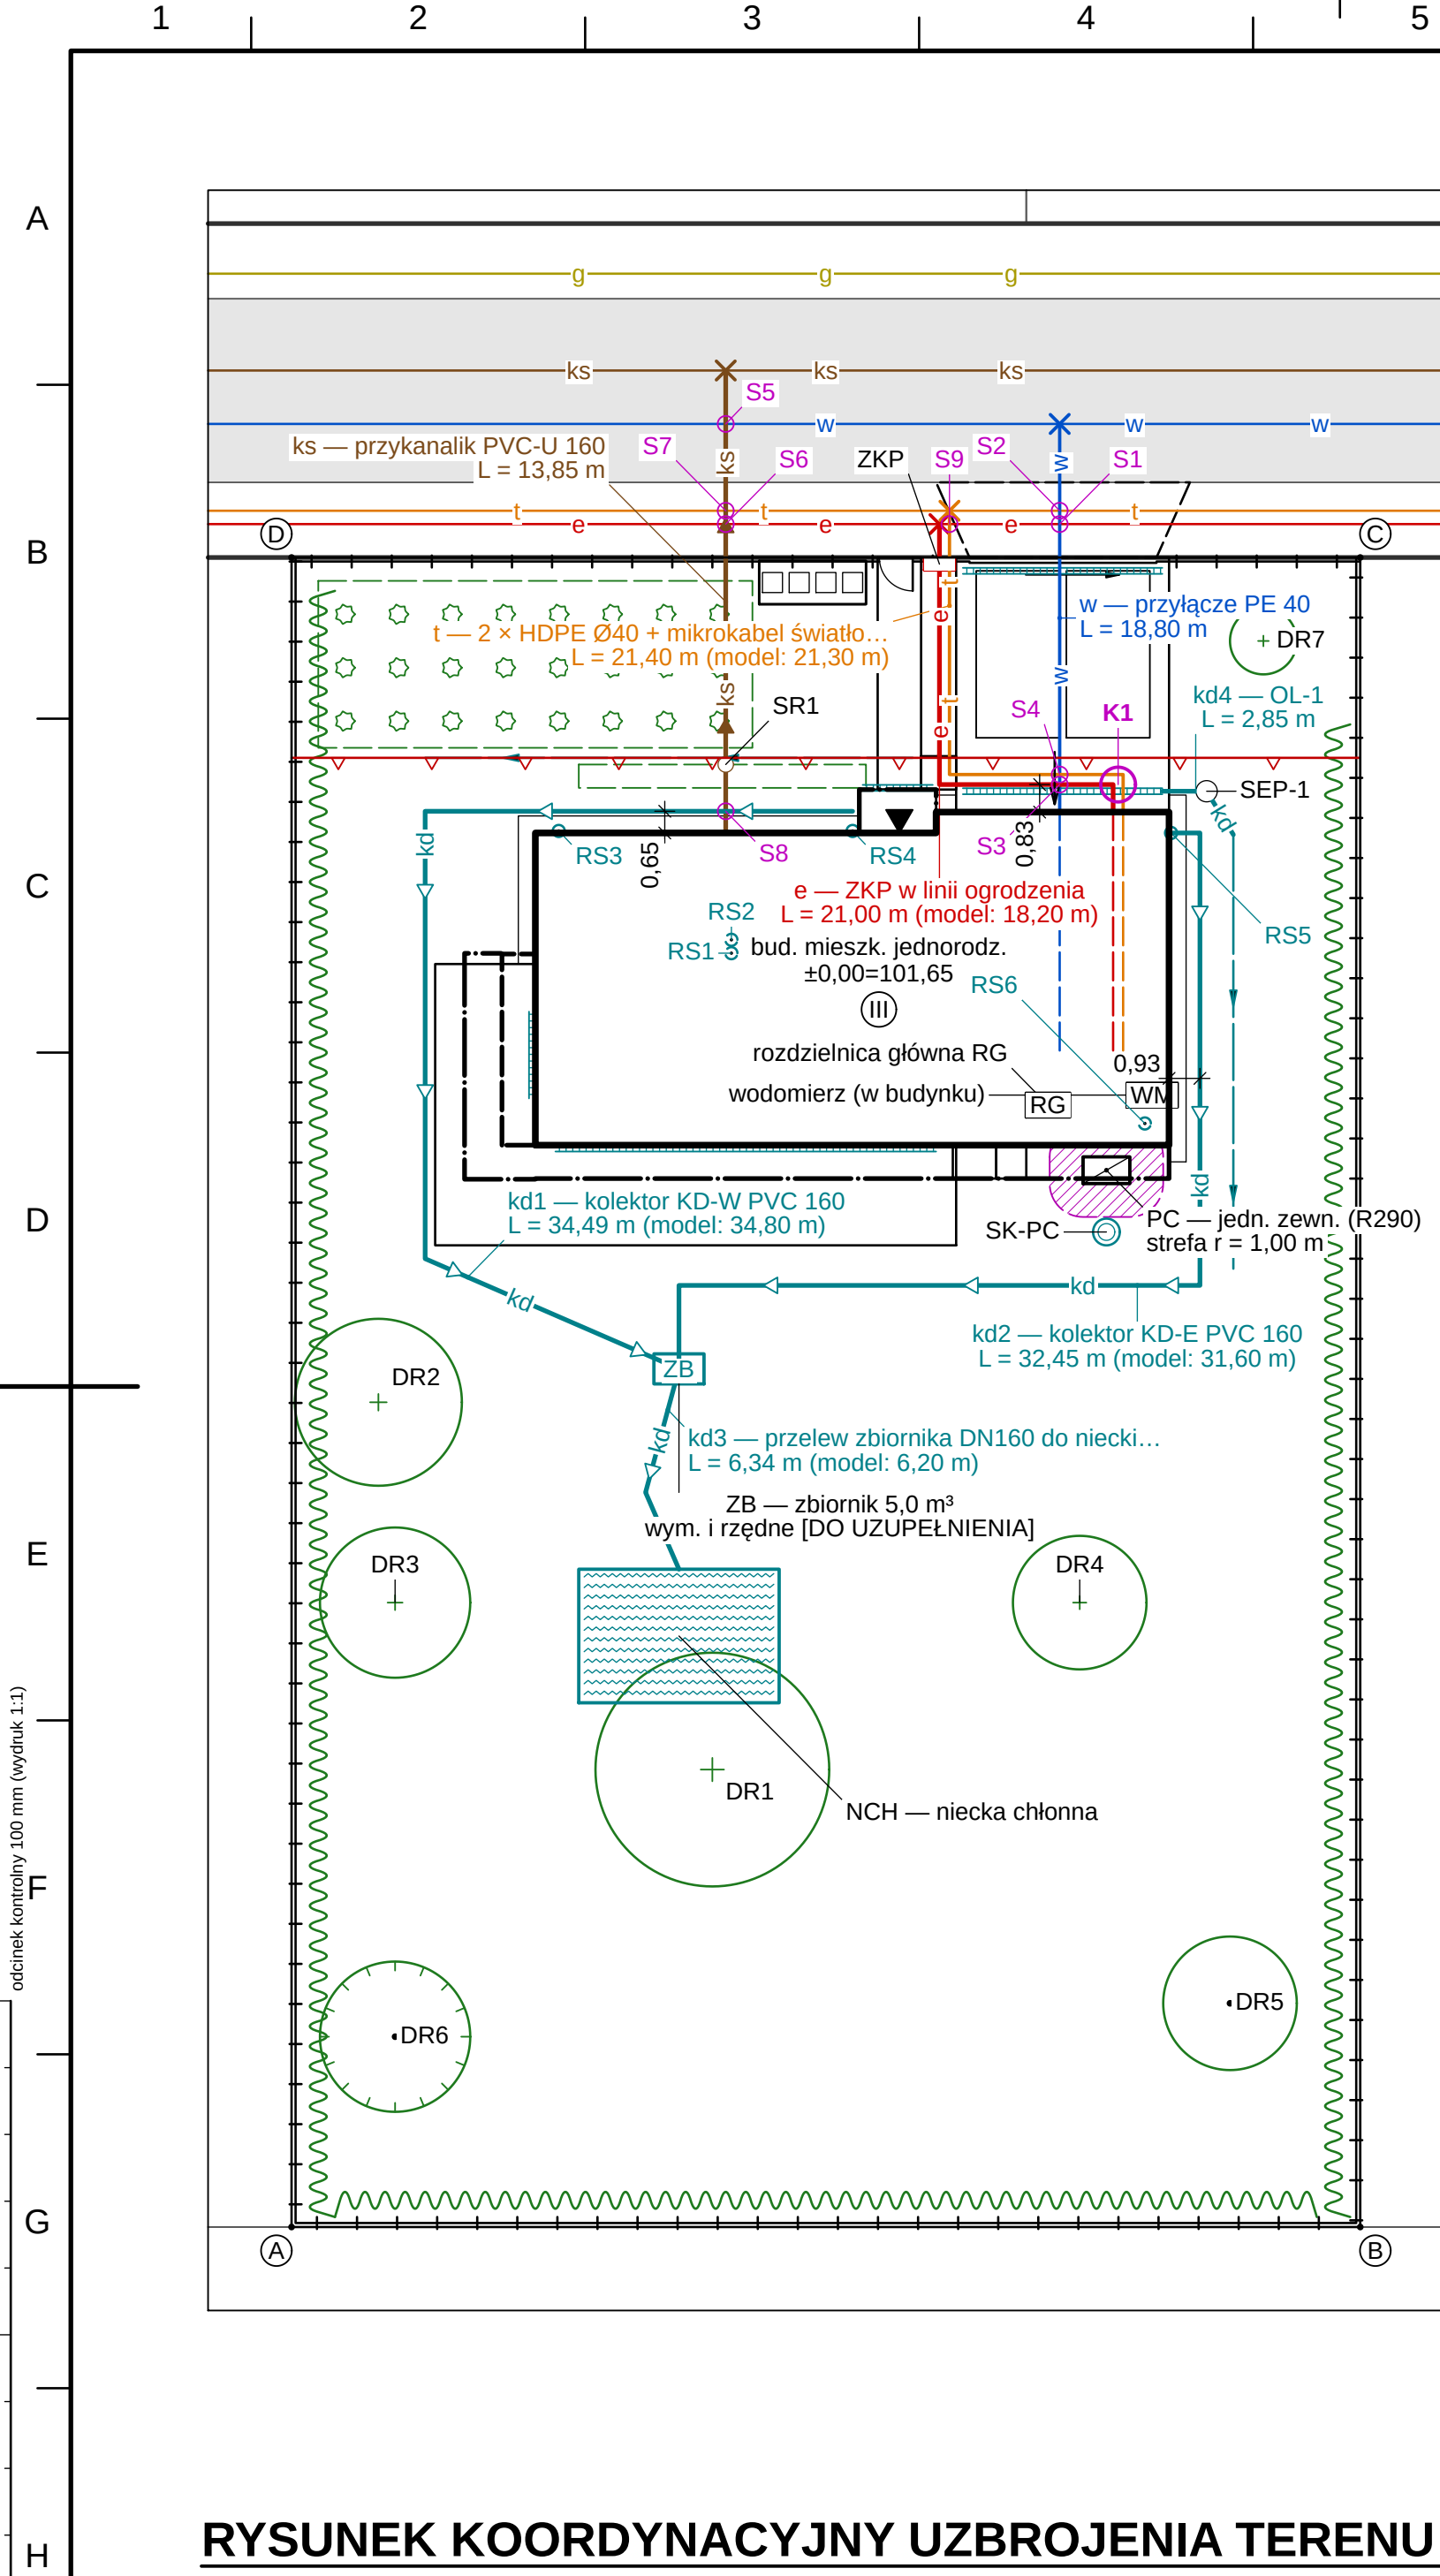

SIECI I PRZYŁĄCZA — PROJEKTOWANE I ISTNIEJĄCE

Ozn.	Sieć	Opis	L [m]	L model [m]
w	przyłącze wodociągowe	przyłącze PE 40	18,80	18,80
ks	kanalizacja sanitarna	przykanalik PVC-U 160	13,85	13,90
e	elektroenergetyczna nN (kabel)	ZKP w linii ogrodzenia	21,00	18,20
t	telekomunikacyjna (światłowód)	2 × HDPE Ø40 + mikrokabel świ...	21,40	21,30
kd1	kanalizacja deszczowa	kolektor KD-W PVC 160	34,49	34,80
kd2	kanalizacja deszczowa	kolektor KD-E PVC 160	32,45	31,60
kd3	kanalizacja deszczowa	przelew zbiornika DN160 do ni...	6,34	6,20
kd4	kanalizacja deszczowa	OL-1	2,85	2,90
w ist.	istniejąca (mapa)	wodociąg PE 110	—	—
ks ist.	istniejąca (mapa)	kanalizacja sanitarna PVC 200	—	—
e ist.	istniejąca (mapa)	kabel nN 0,4 kV	—	—
t ist.	istniejąca (mapa)	kanalizacja teletechniczna /...	—	—
g ist.	istniejąca (mapa)	gazociąg PE 63 (nie wykorzyst...	—	—

L — długość trasy w rzucie (z częścią pod budynkiem, linia kreskowa); średnice, spadki i rzędne dna przewodów [DO UZUPEŁNIENIA] (RPB § 15 ust. 2 pkt 11 — brak w modelu).

OBIEKTY UZBROJENIA I ODWODNIENIA

Ozn.	Opis
ZKP	złącze kablowo-pomiarowe we wnęce ogrodzenia
SR1	studzienka rewizyjna kanalizacji Ø425
PC-JZ	jednostka zewn. PC monoblok R290 w osłonie lamelowe...
SEP-1	osadnik z separatorem substancji ropopochodnych
SK-PC	studnia chłonna skroplin PC
HYDR	najbliższy hydrant zewnętrzny DN80
RS1	rura spustowa DN100 (w szachcie) z dachu D1
RS2	rura spustowa DN100 (w szachcie) z dachu D1
RS3	rura spustowa DN100 (zewn.) z dachu D2
RS4	rura spustowa DN100 (zewn.) z dachu D3
RS5	rura spustowa DN100 (zewn.) z dachu D4
RS6	rura spustowa DN100 (w szachcie) z dachu D4

KOORDYNACJA — ODLEGŁOŚCI POZIOME MIĘDZY SIECIAMI

Para sieci	d [m]	min [m]	Źródło wymagania	Zgodność
w — ks ist.	3,15	1,50	praktyka proj. (COBRTI INSTAL z. 3)*	TAK
w — kd2	3,40	1,50	praktyka proj. (COBRTI INSTAL z. 3)*	TAK
w — kd4	3,08	1,50	praktyka proj. (COBRTI INSTAL z. 3)*	TAK
e — t ist.	1,02	0,50	N SEP-E-004:2014*	TAK
e — t	0,30	0,50	N SEP-E-004:2014*	warunk.
e — kd1	2,72	0,50	N SEP-E-004:2014*	TAK
e — kd2	1,80	0,50	N SEP-E-004:2014*	TAK
e — kd4	1,48	0,50	N SEP-E-004:2014*	TAK
t — kd2	1,50	0,50	praktyka proj.*	TAK
t — kd4	1,18	0,50	praktyka proj.*	TAK
e — budynek	0,83	—	informacyjnie (lico ściany)	—
kd1 — budynek	0,65	—	informacyjnie (lico ściany)	—
kd2 — budynek	0,93	—	informacyjnie (lico ściany)	—

* wartości minimalne wg zasad wiedzy technicznej (N SEP-E-004, praktyka projektowa) — NIE są przepisem: WT § 26–28 określają tylko wymagania ogólne uzbrojenia działki; do potwierdzenia w warunkach przyłączenia gestorów [SPRAWDŹ]. „warunk.” — dopuszczalne przy rurach osłonowych.

SKRZYŻOWANIA SIECI

Nr	Sieci	x [m]	y [m]
S1	w × e ist.	23,00	51,00
S2	w × t ist.	23,00	51,40
S3	w × e	23,00	43,20
S4	w × t	23,00	43,50
S5	ks × w ist.	13,00	54,00
S6	ks × e ist.	13,00	51,00
S7	ks × t ist.	13,00	51,40
S8	ks × kd1	13,00	42,40
S9	t × e ist.	19,70	51,00

Odstęp pionowy na skrzyżowaniach — wg warunków gestorów sieci [DO UZUPEŁNIENIA] (brak rzędnych przewodów w modelu); kable w rurach osłonowych w obrębie skrzyżowań.

KOLIZJE I ZBLIŻENIA

Nr	Rodzaj	Opis	Ocena
K1	zbliżenie sieci	e–t: 0,30 m < 0,50 m	warunk.

K1: dopuszczalne przy ułożeniu w rurach osłonowych — uzgodnić z gestorami

LEGENDA

	granicza działki budowlanej, punkt graniczny, narożnik (PN-B-01027 poz. 2.7)		furtka otwierana do wnętrza działki (WT § 42)
	linia rozgraniczająca drogi publicznej (PN-B-01027 poz. 2.5)		jednostka zewn. pompy ciepła (fundament) i strefa czynnika R290
	jezdnia drogi publicznej (wg mapy)		niecka chłonna — ogród deszczowy (przelew zbiornika)
	nieprzekraczalna linia zabudowy wg MPZP (PN-B-01027 poz. 2.2)		odwodnienie liniowe
	budynek projektowany — obrys ścian parteru 1,0 m nad terenem (poz. 1.1)		niecka trawiasta — grot w kierunku spływu
	obrys wyższych kondygnacji poza obrysem parteru (poz. 1.6 d)		rura spustowa: zewnętrzna / w szachcie (RS)
	obrys płyt wspornikowych, okapów i daszku — przewieszenia (poz. 1.6 c)		miejsce włączenia przyłącza do sieci (PN-B-01027 poz. 6)
	±0,00=101,65		złącze kablowo-pomiarowe ZKP (w linii ogrodzenia)
	±0,00=101,65		studzienka rewizyjna kanalizacji
	wejście główne do budynku (poz. 1.7)		studnia chłonna skroplin pompy ciepła
	wjazd do garażu		skrzyżowanie sieci — zachować odstęp pionowy (tabela)
	zjazd z drogi publicznej — wg zezwolenia zarządcy drogi (DO UZUPEŁNIENIA)		zbliżenie / kolizja sieci (nr w tabeli koordynacji)
	nawierzchnia z kostki betonowej (poz. 7.10)		w — sieć wodociągowa istniejąca (mapa)
	nawierzchnia z płyt betonowych (poz. 7.11)		w — przyłącze wodociągowe projektowane
	płyty w trawie (ażur) — poza PBC		ks — sieć kanalizacji sanitarnej istniejąca (mapa)
	taras naziemny — deska kompozytowa na legarach		ks — przykanalik sanitarny projektowany
	opaska żwirowa 16/32 na geowłókninie		kd — kanalizacja deszczowa projektowana (kolektory, przelewy)
	stanowisko postojowe 2,50 × 5,00 m (WT § 21)		e — linia kablowa nN istniejąca (mapa)
	osłona pojemników na odpady — segregacja (WT § 22)		e — kabel nN projektowany (ZKP → RG)
	rabata z krzewami		t — sieć telekomunikacyjna istniejąca (mapa)
	zrywplot projektowany (poz. 7.6)		t — przyłącze telekomunikacyjne projektowane
	drzewo liściaste projektowane (poz. 7.1)		g — sieć gazowa istniejąca (mapa)
	drzewo istniejące — zachowane (poz. 7.2)		
	ogrodzenie projektowane (poz. 2.8; na granicy — odsunięte graficznie)		
	brama przesuwna (poz. 2.9)		

OBJAŚNIENIA I UWAGI

- Wymiary i odległości w m (dokładność 0,01 m), rzędne w m n.p.m. (PL-EVRF2007-NH).
- Oznaczenia sieci — kolory i litery wg mapy zasadniczej (zał. 4 rozp. w sprawie BDOT500 i mapy zasadniczej, Dz.U. 2021 poz. 1385): w — wodociąg, ks — kanalizacja sanitarna, kd — kanalizacja deszczowa, e — elektroenergetyczna, t — telekomunikacyjna, g — gazowa; istniejące — linia cienka (wg mapy), projektowane — gruba; w budynku/pod płytą — kreskowa; „x” — włączenie do sieci.
- Przyłącza w granicach działki nie podlegają narzędziu koordynacyjnej ZUD (PGiK art. 28b); roboty w pasie drogowym 1KDD — za zezwoleniem zarządcy drogi (u.d.p. art. 40).
- Skrzyżowań: 9; zbliżeń poniżej wartości minimalnych: 1 (tabela „Kolizje i zbliżenia”).
- Wody opadowe: rury spustowe RS → kolektory kd → zbiornik ZB → przelew do niecki chłonnej NCH; odwodnienia liniowe OL → kolektory kd (WT § 28 ust. 2).
- Drenaż opaskowy DR-0: NIE PROJEKTUJE SIĘ — piaski przepuszczalne, ZWG = 3,8 m p.p.t., posadowienie = 0,5 m p.p.t. (W-285); ochrona płyty: XPS + membrana SBS, opaska żwirowa i spadki terenu
- Braki danych modelu (9 poz.) — [DO UZUPEŁNIENIA]; wykaz: projekt/02_PZT/BRAKI_DANYCH.md.
- Rysunek wygenerowany automatycznie z modelu model/budynek.yaml (wersja 1.0, 2026-09-25) — generatory lamela.views.



REW.	OPIS ZMIANY	DATA				
0	Wydanie — rysunek wygenerowany z modelu	2026-09-25				
PRACOWNIA PROJEKTOWA PRACOWNIA PROJEKTOWA — nazwa do uzupełnienia adres pracowni do uzupełnienia		STADIUM PB	BRANŻA ZAGOSPODAROWANIE TERENU			
INWESTOR (do uzupełnienia)						
OBIEKT / NAZWA ZAMIERZENIA BUDOWLANEGO Budynek mieszkalny jednorodzinny wolnostojący „Dom LAMELA” z zagospodarowaniem działki						
ADRES / LOKALIZACJA (NR DZIAŁKI, OBRĘB, JEDN. EWIDENCYJNA) ul. Lipowa (fikcyjna), dz. nr ewid. 123/4, obręb 0005 Przykładowo, gm. Przykładowo (fikcyjna)			KAT. OBIEKTU I			
FUNKCJA	IMIĘ I NAZWISKO	SPECJALNOŚĆ, NR UPRAWNIEŃ	DATA	PODPIS		
Projektant						
Projektant (wsp.)						
Sprawdzający						
Opracował						
TYTUŁ RYSUNKU						
RYSUNEK KOORDYNACYJNY UZBROJENIA TERENU						
SKALA 1:200	FORMAT A2	DATA WYDANIA 2026-09-25	RODZAJ DOK. rysunek koordynacyjny	NR RYSUNKU PZT-03	ARKUSZ 3/3	REW. 0