



PRZEKRÓJ A-A (FRAGMENT) 1:50

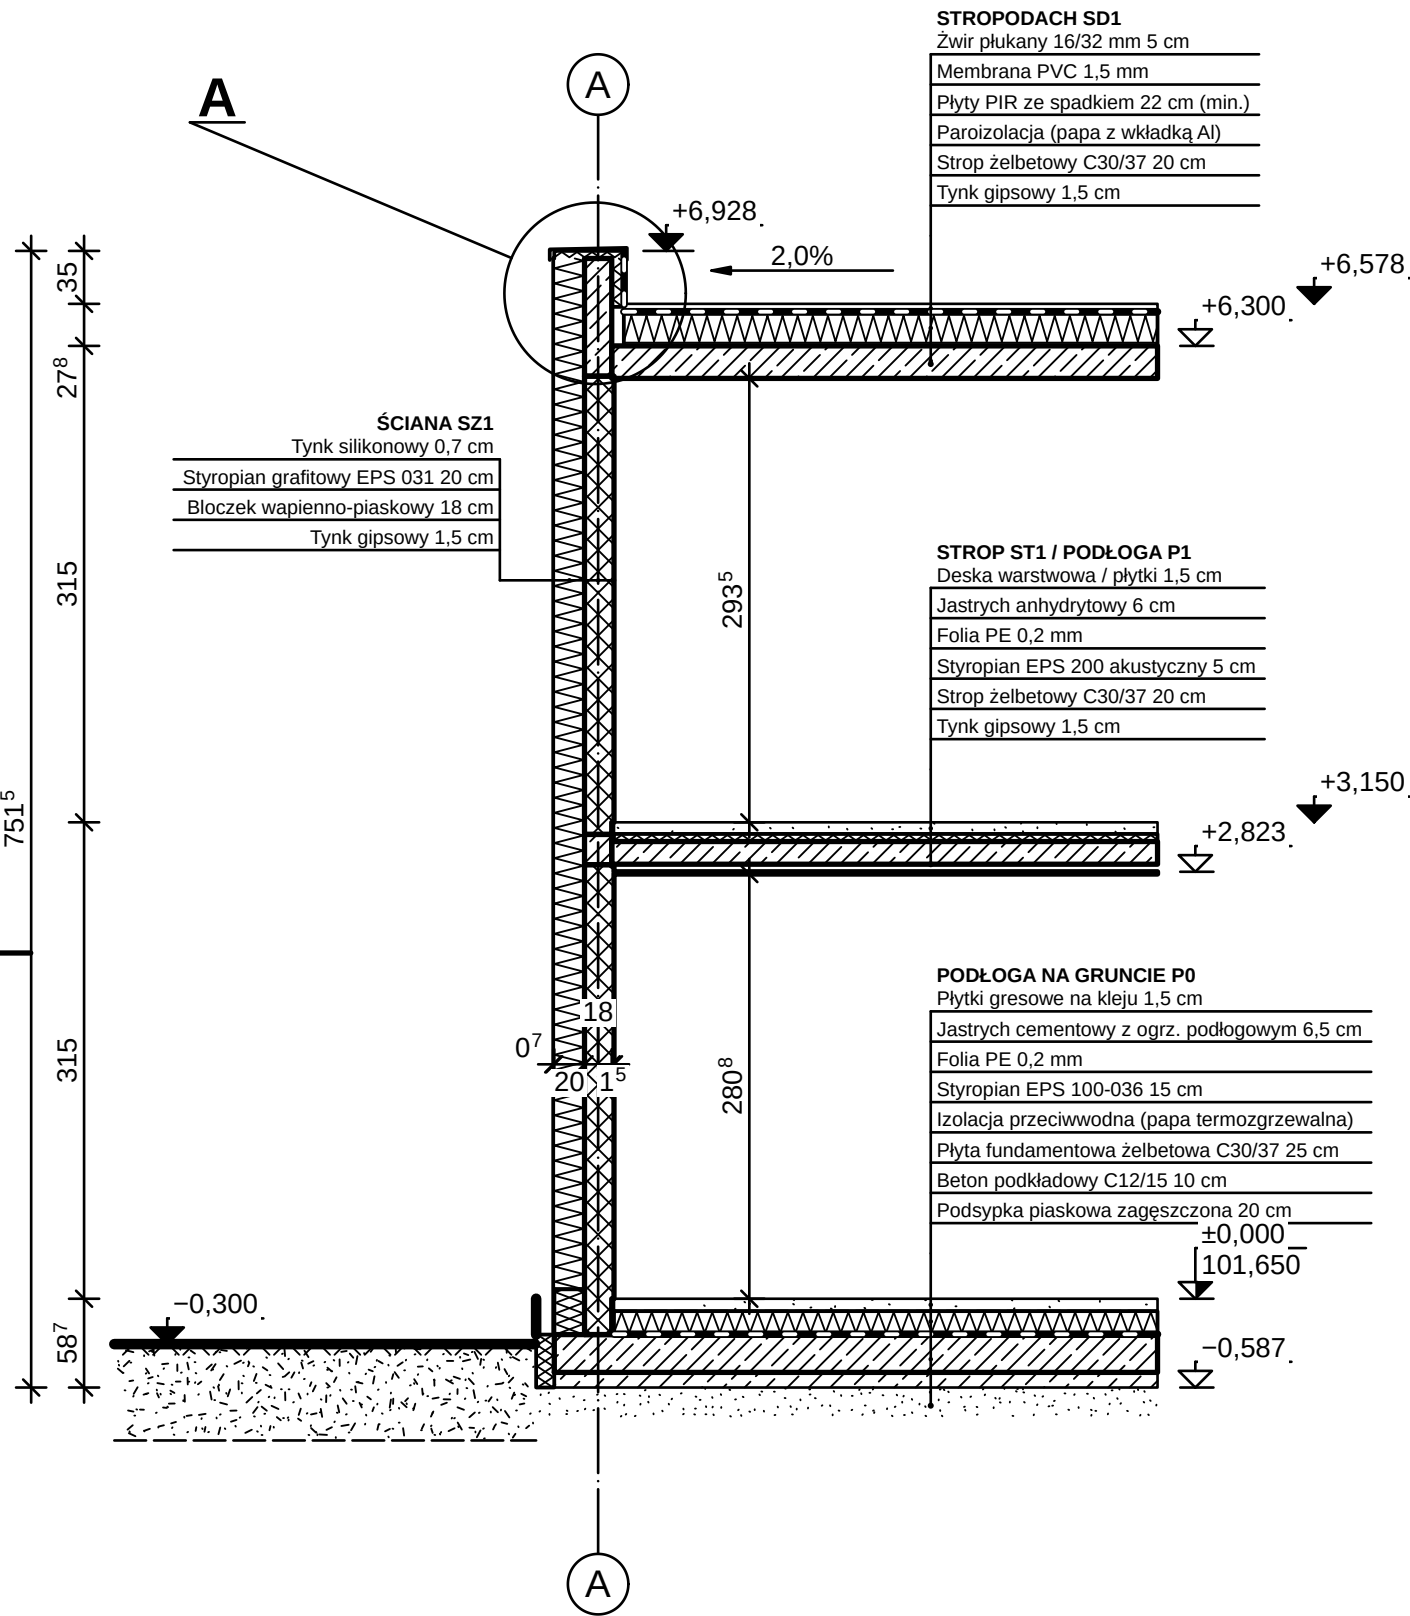

DETAL A — ATTYKA 1:20


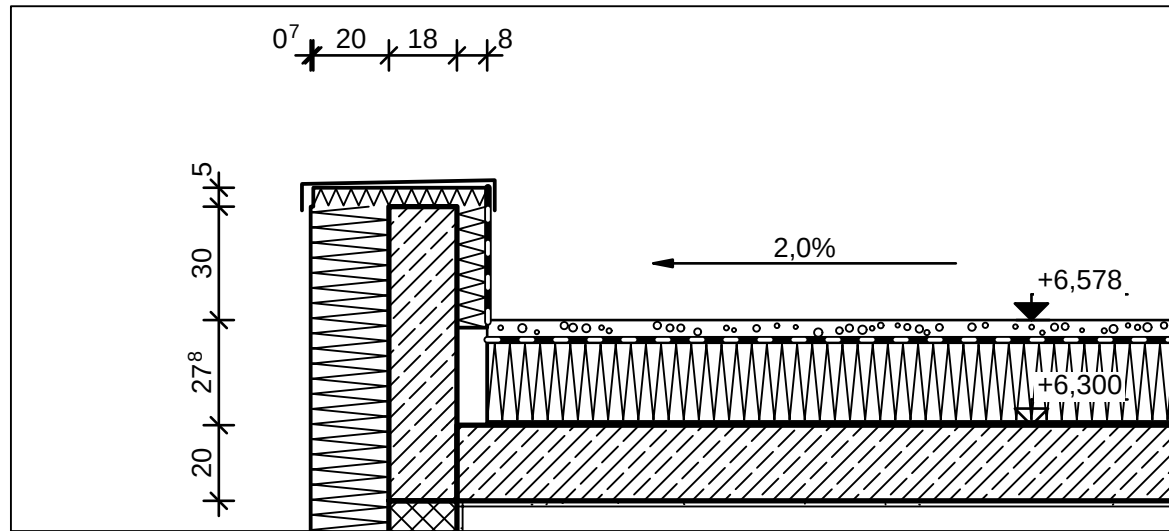


OZNACZENIA MATERIAŁÓW

	Beton zbrojony (żelbet) — 45° na przemian ciągle i przerywane		Paroizolacja (folia PE) — linia kreskowa cienka 3/1 po ciepłej stronie
	Beton niezbrojony, kamień — 45° przerywane		Jastrych (wylewka) cementowy/anhydrytowy — kropki
	Mur z bloczków wapienno-piaskowych (silikatowych) — kratka ukośna 45°/135°		Tynk, zaprawa — kropki nieregularne
	Izolacja termiczna twarda (EPS) — zygzak „VVV”		Piasek, podsypka piaskowa
	Izolacja termiczna twarda (XPS) — zygzak podwójny		Nasyp, zasypka (grunt nasypowy)
	Izolacja termiczna twarda (PIR/PUR) — zygzak z okładzinami		Żwir, tłuczeń
	Izolacja przeciwwodna (papa, membrana) — pas czarno-biały		Grunt rodzimy (powierzchnia gruntu w przekroju)

OBJAŚNIENIA I UWAGI

- Wymiary w cm (mm w indeksie górnym), rzędne w m względem $\pm 0,000 = 101,650$ m n.p.m.
- Rzędne: trójkąt zaczerpiony — wykończenie, niezaczerpiony — konstrukcja, w połowie zaczerpiony — poziom zerowy z rzędną bezwzględną (PN-B-01025).
- Rysunek testowy silnika — dane nie stanowią projektu.

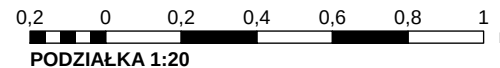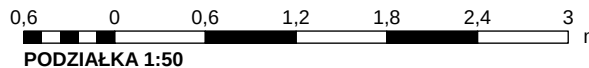

PRACOWNIA PROJEKTOWA PRACOWNIA PROJEKTOWA — nazwa do uzupełnienia adres pracowni do uzupełnienia			STADIUM PB	BRANŻA ARCHITEKTURA (AR)	
INWESTOR (do uzupełnienia)					
OBIEKT / NAZWA ZAMIERZENIA BUDOWLANEGO Budynek mieszkalny jednorodzinny „Dom LAMELA” — PRÓBA SILNIKA RYSUNKOWEGO (rysunek testowy)					
ADRES / LOKALIZACJA (NR DZIAŁKI, OBRĘB, JEDN. EWIDENCYJNA) dz. nr ewid. 123/4, obręb 0005 Przykładowo, jedn. ewid. Przykładowo (dane fikcyjne)					KAT. OBIEKTU I
FUNKCJA	IMIĘ I NAZWISKO	SPECJALNOŚĆ, NR UPRAWNIENI		DATA	PODPIS
Projektant					
Projektant (wsp.)					
Sprawdzający					
Opracował					
TYTUŁ RYSUNKU PRZEKRÓJ PRÓBNY A-A					
SKALA 1:50	FORMAT A3	DATA WYDANIA 2026-09-25	RODZAJ DOK. przekrój	NR RYSUNKU DEMO-02	ARKUSZ 2/3
					REW. 0