


RZUT II PIĘTRA 1:50

OZNACZENIA LINII

- elementy nad płaszczyzną cięcia (obrysy płyt, wsporników, brył wyższych kondygnacji)
--- elementy poniżej płaszczyzny cięcia (widok z góry)
--- osie konstrukcyjne; linia punktowa z pogrubionymi końcami — ślad przebiegu

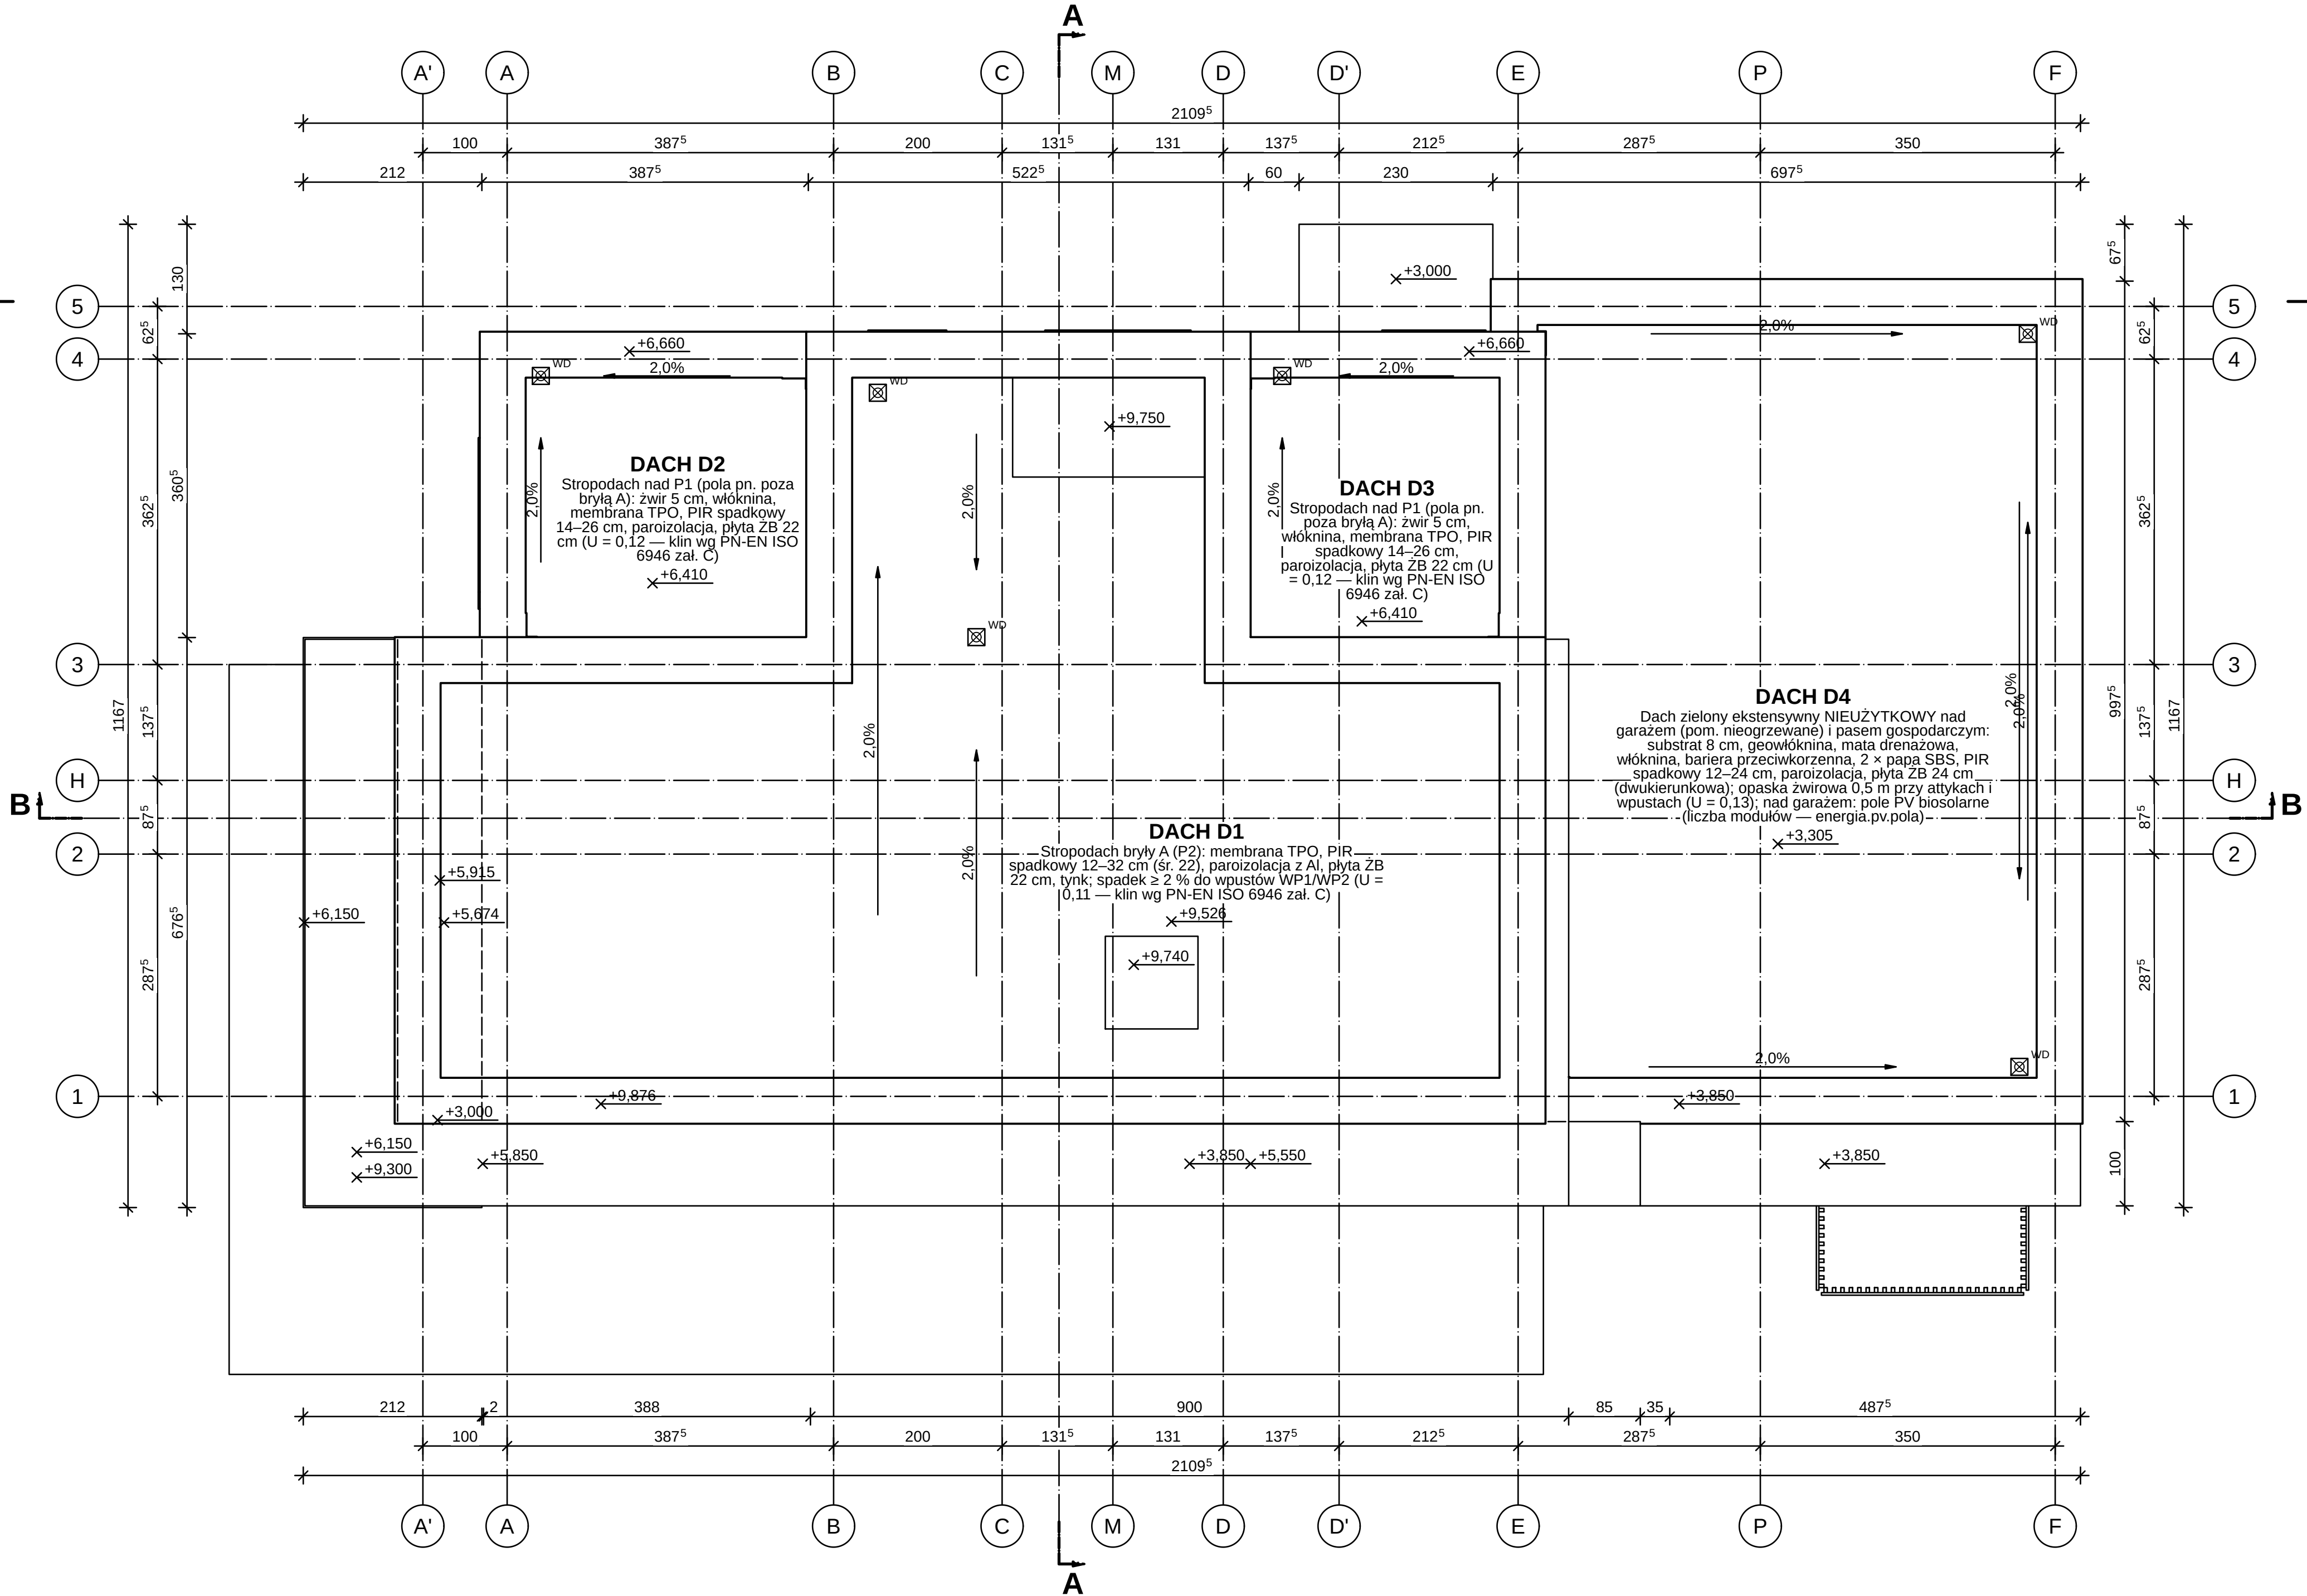

RZUT DACHU 1:50

OZNACZENIA MATERIAŁÓW (PN-B-01030 + przyjęte)

- Włna mineralna 035 (szkielet, docieplenia, ściana dom-garaz);
Włna mineralna fasadowa (elewacja wentylowana bryły A, A1)
--- meander, UUU
Błoczek wapniowo-piaskowy 12 cm, kl. 15 (ścianki działowe, boczny w klatce); Błoczek wapniowo-piaskowy (silikat) 18 cm, kl. 20, gr. 1, na zaprawie cienkowarstwowej — kratka ukośna 45°/135°
Żelbet C25/30, B500SP (stropy, płyta fundamentowa, ściany) — 45° na przemiian cięgie i przerywane
Styropian grafitowy EPS 031 (ETICS, NRO w systemie) — zgrząk, VVV
Membrana fasadowa wiatroizolacyjna UV-stabilna, czarna (sd = 0,02 m)

OBJAŚNIENIA I UWAGI

1. Wymiary w cm (mm w indeksie górnym, np. 24° = 24,5 cm), rzędne w m względem ±0,000 = 101,650 m n.p.m. (PL-EVRF2007-NH).
2. Rzut: płaszczyzna cięcia +1,10 m nad posadzką kondygnacji. Linia krekowa — elementy nad płaszczyzną cięcia (obrysy płyt i wsporników, brył wyższych kondygnacji, otwory w stropie nad, belki); linia ciągła — elementy poniżej (widok).
3. Otwory: licznik — szerokość, mianownik — wysokość w świetle muru, w nawiasie wysokość parapetu; symbol stolarki wg zestawienia stolarki.
4. Numeracja pomieszczeń wg PN-B-01025 / PN-EN ISO 4157-2: <nr> kondygnacji (parter = 1) <nr>; identyfikator w modelu: <kond> <nr> (parter = 0).
5. Dzw: strona otwierania (lewo/prawo) wg modelu — patrz: od strony, w którą otwiera się skrzydło.
6. Rysunek wygenerowany automatycznie z modelu modelBudynek.yamf (wersja 1.0, 2026-09-25) — generatory lamela.views.

1 0 1 2 3 4 5 m
PODZIAŁKA 1:50

ZESTAWIENIE POMIESZCZEŃ

Nr	Nazwa pomieszczenia	Posadzka	Kat.	Wys. [m]	Pow. [m²]
3.02	Sypialnia rodziców	Deska warstwowa dębowa 15 mm, klejona podst.		2,77	21,43
3.05	Gabinet / pokój gościnny okazjonalny	Deska warstwowa dębowa 15 mm, klejona podst.		2,77	16,25
3.03	Garderoba (przedpokój apartamentu)	Deska warstwowa dębowa 15 mm, klejona podst.		2,77	10,49
3.07	Pom. techniczne (centrala rekuperacyjna, wylaz na dach)	Płytki gresowe 60x120 na kleju CZTE \$1 techn.		2,77	5,90
3.01	Hol	Deska warstwowa dębowa 15 mm, klejona podst.		2,77	5,74
3.04	Łazienka rodziców	Płytki gresowe 60x120 na kleju CZTE \$1 techn.		2,77	5,51
3.08	Szacht instalacyjny SI	techn.		2,77	0,45
3.06	Klatka schodowa (wyjście z biegu 2, pustka)	Deska warstwowa dębowa 15 mm, klejona podst.		2,77	0,24
RAZEM powierzchnia netto					66,01
w tym użytkowa (podst. + pomoc.)					53,67

REW.	OPIS ZMIANY	DATA
0	Wydanie — rysunek wygenerowany z modelu	2026-09-25
PRACOWNIA PROJEKTOWA — nazwa do uzupełnienia		STADIUM
ul. Lipowa (fikcyjna), dz. nr ewid. 123/4, obręb 0005 Przykładowo, gm. Przykładowo (fikcyjna)		BRANŻA
INWESTOR (do uzupełnienia)		ARCHITEKTURA (AR)
OBIEKT / NAZWA ZAMIERZENIA BUDOWLANEGO		
Budynek mieszkalny jednorodzinny wolnostojący „Dom LAMELA”		
ADRES / LOKALIZACJA (NR DZIAŁKI, OBRĘB, JEDN. EWIDENCYJNA)		KAT. OBIEKTU
ul. Lipowa (fikcyjna), dz. nr ewid. 123/4, obręb 0005 Przykładowo, gm. Przykładowo (fikcyjna)		I
FUNKCJA	IMIĘ I NAZWISKO	SPECJALNOŚĆ, NR UPRAWNIENI
Projektant		DATA
Projektant (wsp.)		PODPIS
Sprawdzający		
Opracował		
TYTUŁ RYSUNKU		
RZUT II PIĘTRA I RZUT DACHU		
SKALA	FORMAT	DATA WYDANIA
1:50	S90x891	2026-09-25
RODZAJ DOK.	NR RYSUNKU	ARKUSZ
Rzut	PB-AR-03	3/5
REW.		0