



A
B
C
D
E
F

odcięcie kontroli 100 mm (wydruk 1:1)

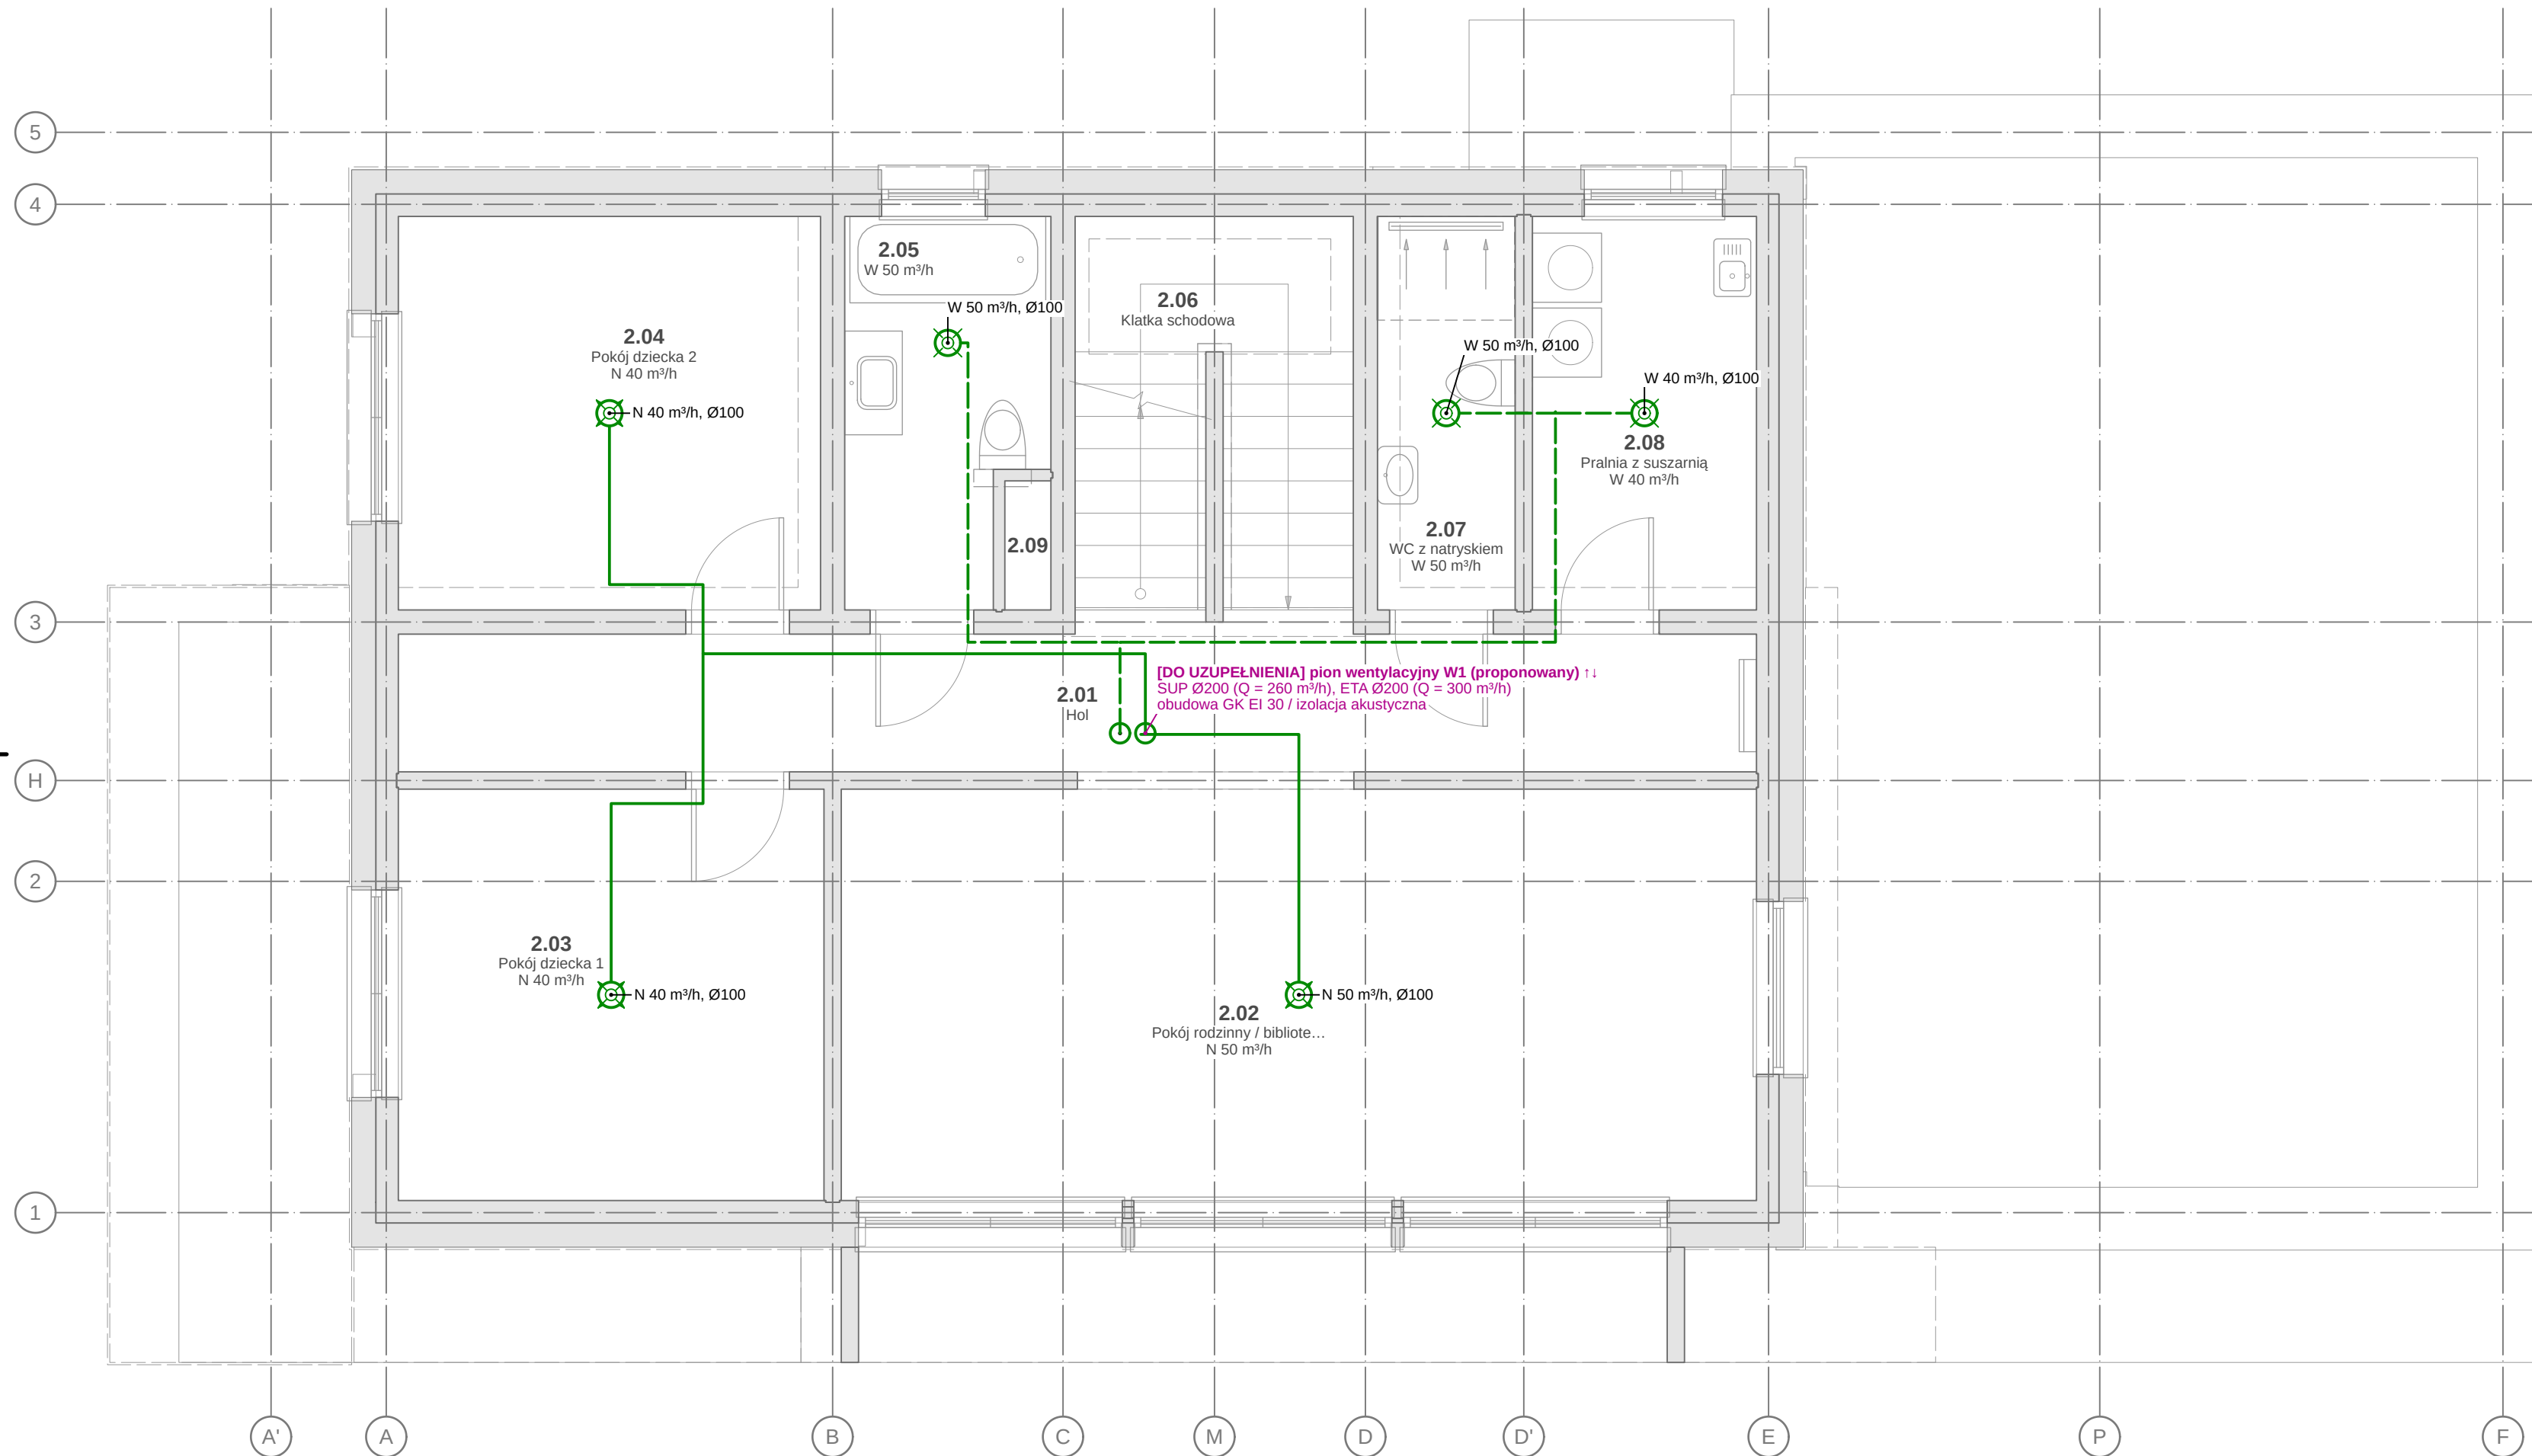

WENTYLACJA MECHANICZNA — RZUT I PIĘTRA 1:50

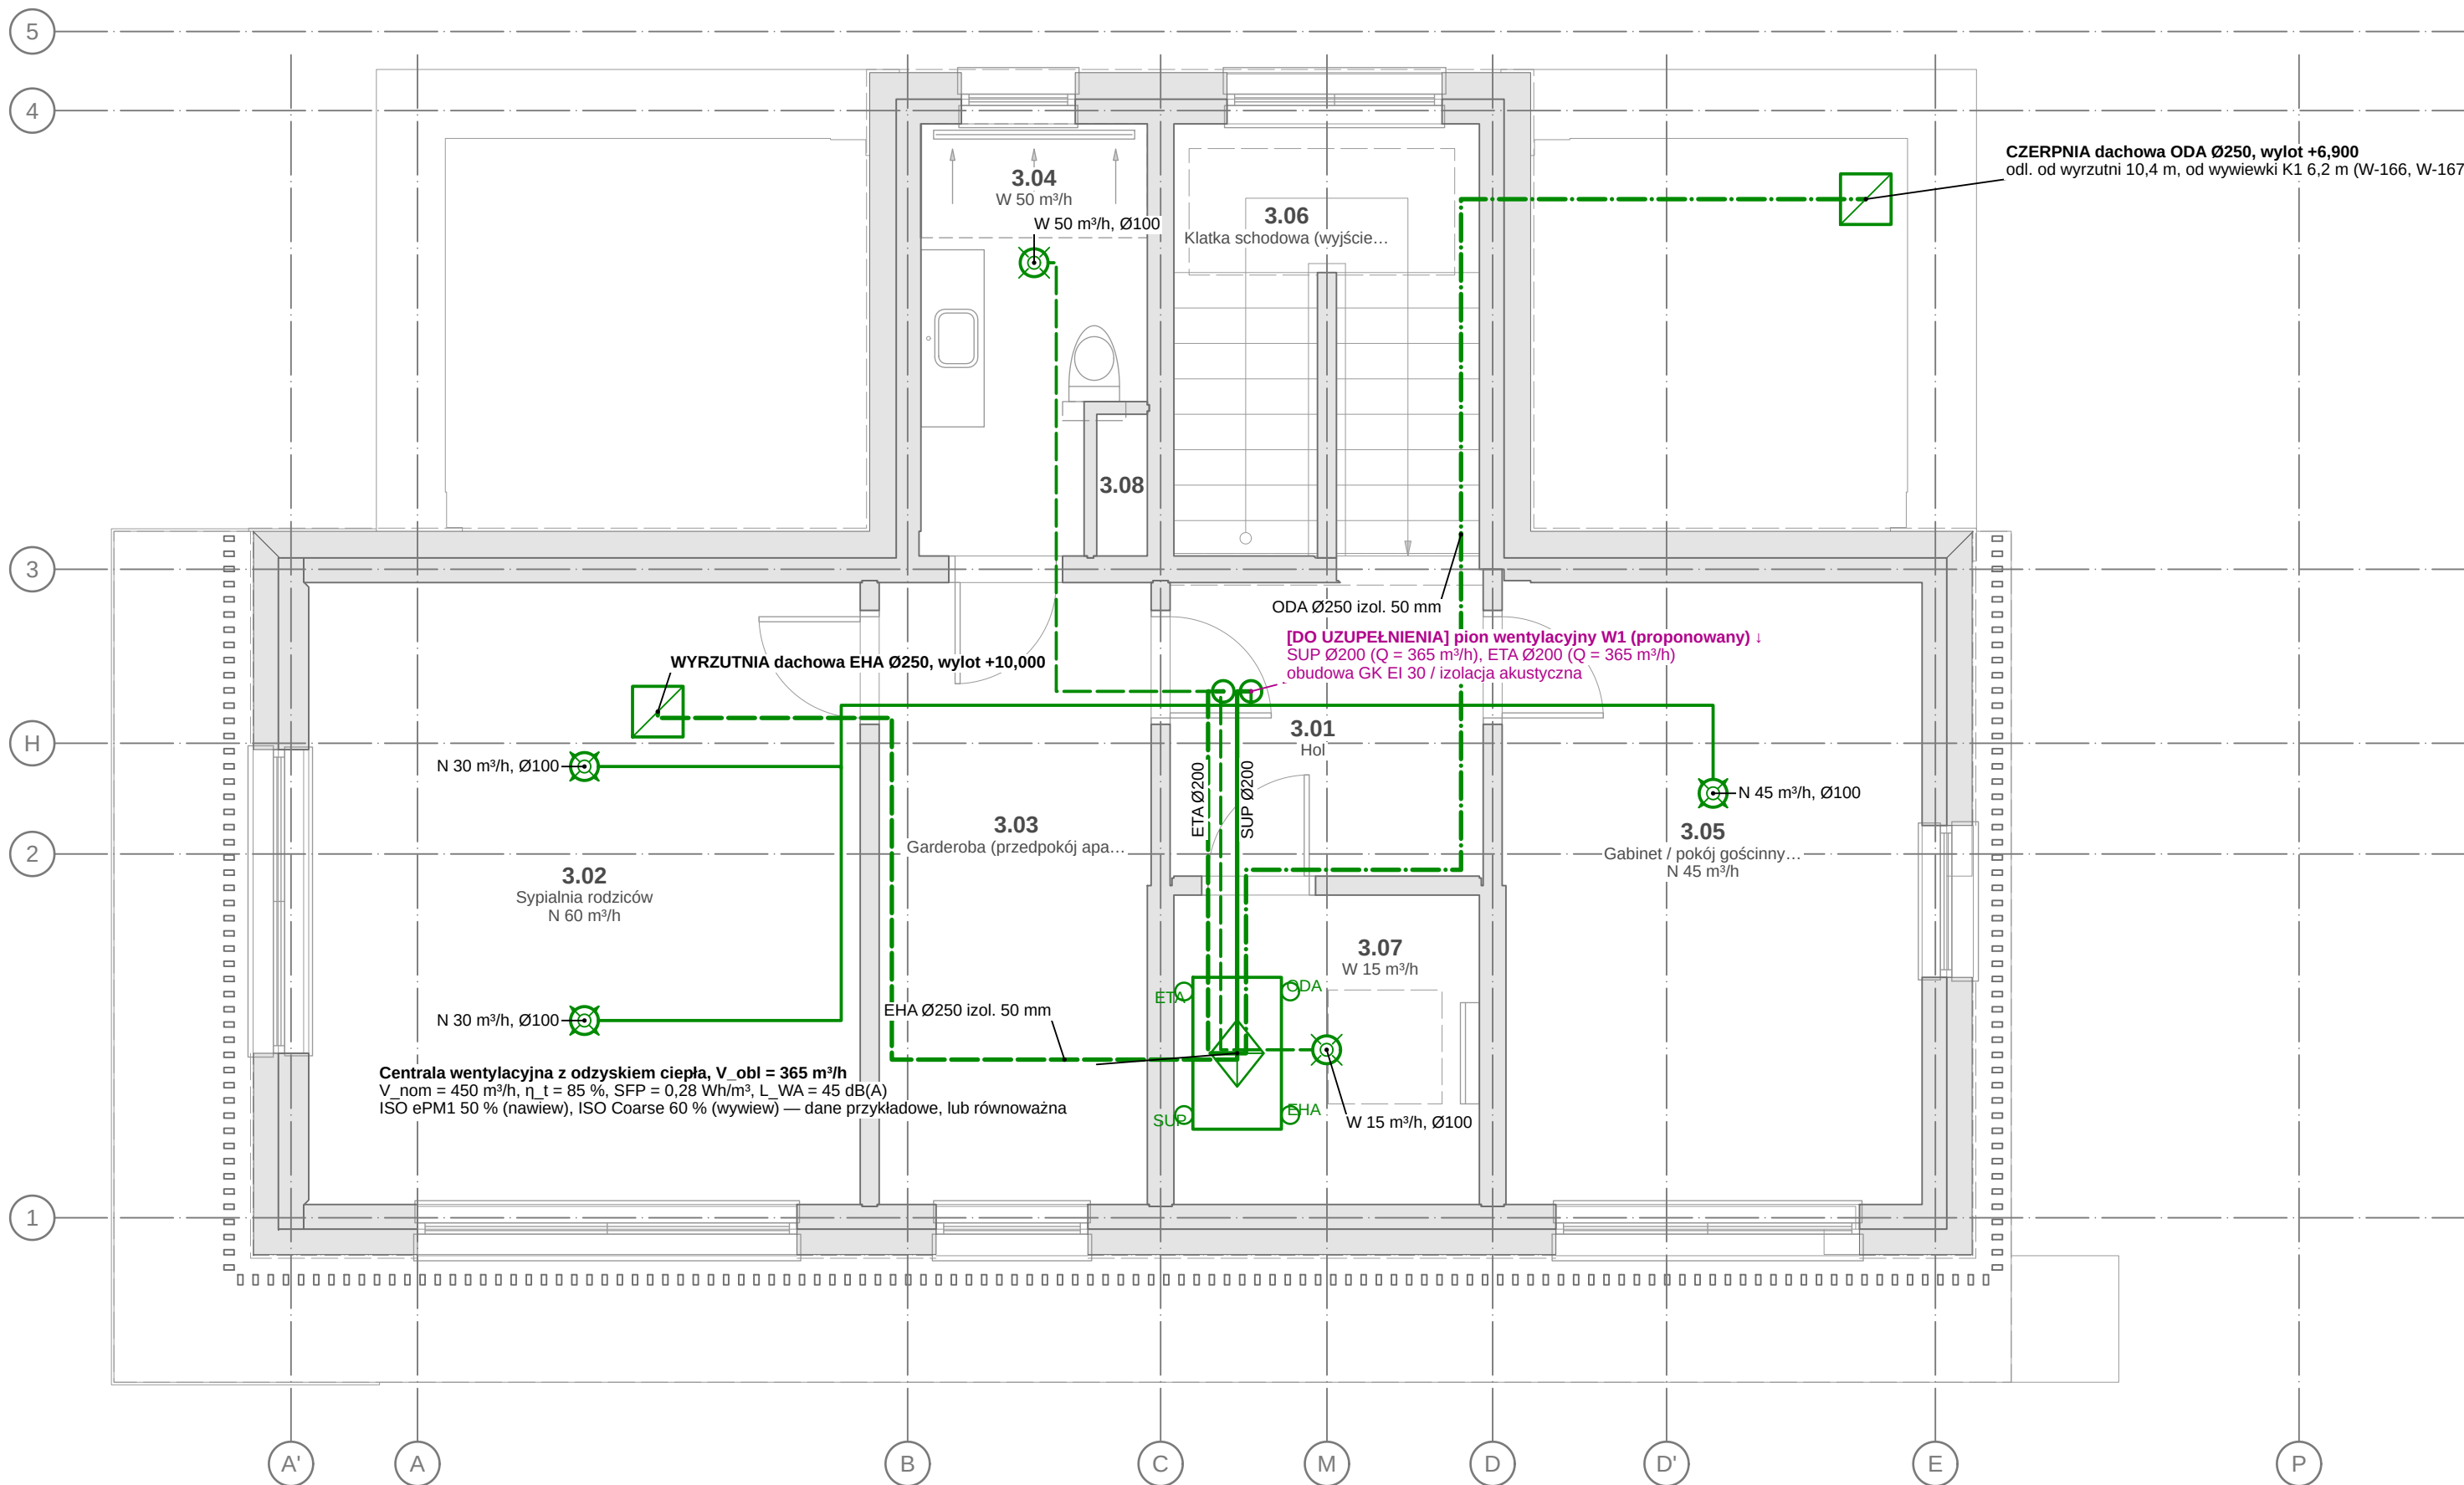

WENTYLACJA MECHANICZNA — RZUT II PIĘTRA 1:50

- OBJAŚNIENIA I UWAGI**
- Średnice przewodów w mm (d, z x s — rury wielowarstwowe, Ø/DN — kanalizacja, kanały wentylacyjne), przekroje żył w mm², odległości i rzędne w m; ±0,000 = 101,650 m n.p.m. (PL-EVRF2007-NH).
 - Rysunki instalacji na podkładzie rzutów architektury (PB-AR); podkład — linie cienkie szare (warstwy I-PODKŁAD*).
 - Wentylacja mechaniczna nawiewno-wywiewna z odzyskiem ciepła wg WT § 147–150 i PN-EN 16798-3 (oznaczenia ODA/SUP/ETA/EHA); strumienie powietrza z bilansu wentylacji (lamela.obliczenia.energia.wentylacja, PN-B-03430/Az3 powołana w WT § 149) — nawiew do pokoi, wywiew z kuchni, łazienek, WC, pralni, spiżarni.
 - Średnice kanałów dobrane dla v ≤ 2,5 m/s (przyłacza) i ≤ 3,5 m/s (pnie); kanały okrągłe stalowe ocynkowane (typu spiro) lub system rozdzielaczy z przewodami elastycznymi (lub równoważne), z tłumikami akustycznymi za centralą; przepływ powietrza między pomieszczeniami przez podcięcia drzwi ≥ 1 cm (przepływ transferowy).
 - Trasy kanałów i lokalizację pionu wyznaczono algorytmicznie (ortogonalnie, w przestrzeni sufitów podwieszanych/stropów) — do koordynacji z konstrukcją i architekturą (sufity SUF_GK).
 - Kanały ODA i EHA w obrębie budynku — izolacja paroszczelna ≥ 50 mm; kanały SUP/ETA w przestrzeniach nieogrzewanych — izolacja ≥ 50 mm. Okap kuchenny — z recyrkulacją (filtr węglowy).
 - Bilans na rysunkach: Σ nawiew = 365 m³/h, Σ wywiew = 365 m³/h — strumienie = max(model, bilans modułu energii); strumienie z modelu (pomieszczenia[.went]) — sprawdzone; minima, bilans ±10 %, 20 m³/h-os.; nastawy regulacyjne nawiewników wyrównać do bilansu zrównoważonego przy rozruchu (PN-EN 12599).
 - Rysunek wygenerowany automatycznie z modelu model/budynek.yaml (wersja 1.0, 2026-09-25) — generatory lamela.views.

OZNACZENIA — LEGENDA SYMBOLI

Oznaczenia instalacji sanitarnych — praktyka branżowa (PN-B-01410, PN-B-01411, PN-B-01430 — normy wycofane, bez następcy); armatura i urządzenia wg PN-EN ISO 10628-2 / PN-EN ISO 14617; rodzaje powietrza wg PN-EN 16798-3 (ODA, SUP, ETA, EHA). Obowiązuje legenda na arkuszu.


— podkład architektoniczny (rzut AR — ściany, przeście, stolarka, wyposażenie) — linie cienkie szare
— SUP — powietrze nawiewane (kanały okrągłe, izolowane w przestrzeniach nieogrzewanych)
— ETA — powietrze wywiewane
— nawiewnik (anemostat/zawór nawiewny) — N, wydatek [m³/h], średnica przyłącza
— wywiewnik (zawór wywiewny) — W, wydatek [m³/h]
— pion wentylacyjny (kanał pionowy SUP/ETA)
— ODA — powietrze zewnętrzne (czerpane), EHA — wyrzutowe; kanały izolowane paroszczelinie
— centrala wentylacyjna z odzyskiem ciepła (króćce ODA / ETA / SUP wg PN-EN 16798-3)

STRUMIENIE POWIETRZA — P1 [m³/h]

Pom.	Nazwa	Nawiew	Wywiew
1.02	Pokój rodzinny / biblioteka (b)	50	—
1.03	Pokój dziecka 1	40	—
1.04	Pokój dziecka 2	40	—
1.05	Łazienka dzieci (wanna)	—	50
1.07	WC z natryskiem	—	50
1.08	Pralnia z suszarnią	—	40

STRUMIENIE POWIETRZA — P2 [m³/h]

Pom.	Nazwa	Nawiew	Wywiew
2.02	Sypialnia rodziców	60	—
2.04	Łazienka rodziców	—	50
2.05	Gabinet / pokój gościnny okaz	45	—
2.07	Pom. techniczne (centrala reku)	—	15

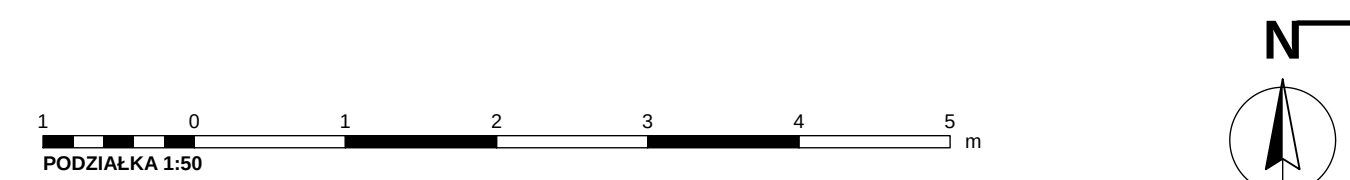

REW.	OPIS ZMIANY			DATA		
0	Wydanie — rysunek wygenerowany z modelu			2026-09-25		
PRACOWNIA PROJEKTOWA PRACOWNIA PROJEKTOWA — nazwa do uzupełnienia adres pracowni do uzupełnienia			STADIUM PT	BRANŻA INSTALACJE SANITARNE (IS)		
INWESTOR (do uzupełnienia)						
OBIEKT / NAZWA ZAMIERZENIA BUDOWLANEGO Budynek mieszkalny jednorodzinny wolnostojący „Dom LAMELA”						
ADRES / LOKALIZACJA (NR DZIAŁKI, OBRĘB, JEDN. EWIDENCYJNA) ul. Lipowa (fikcyjna), dz. nr ewid. 123/4, obręb 0005 Przykładowo, gm. Przykładowo (fikcyjna)				KAT. OBIEKTU I		
FUNKCJA	IMIĘ I NAZWISKO	SPECJALNOŚĆ, NR UPRAWNIENI	DATA	PODPIS		
Projektant	[DO UZUPEŁNIENIA]	[DO UZUPEŁNIENIA]				
Projektant (wsp.)	[DO UZUPEŁNIENIA]	[DO UZUPEŁNIENIA]				
Sprawdzający	nie dotyczy (art. 20 ust. 3 pkt 2 PB)	—				
Opracował	[DO UZUPEŁNIENIA]	[DO UZUPEŁNIENIA]				
TYTUŁ RYSUNKU WENTYLACJA MECHANICZNA — RZUTY I PIĘTRA I II PIĘTRA						
SKALA 1:50	FORMAT 1320×297	DATA WYDANIA 2026-09-25	RODZAJ DOK. rzut instalacji	NR RYSUNKU PT-IS-09	ARKUSZ 9/11	REW. 0