



PRZĘKRÓJ A-A 1:50

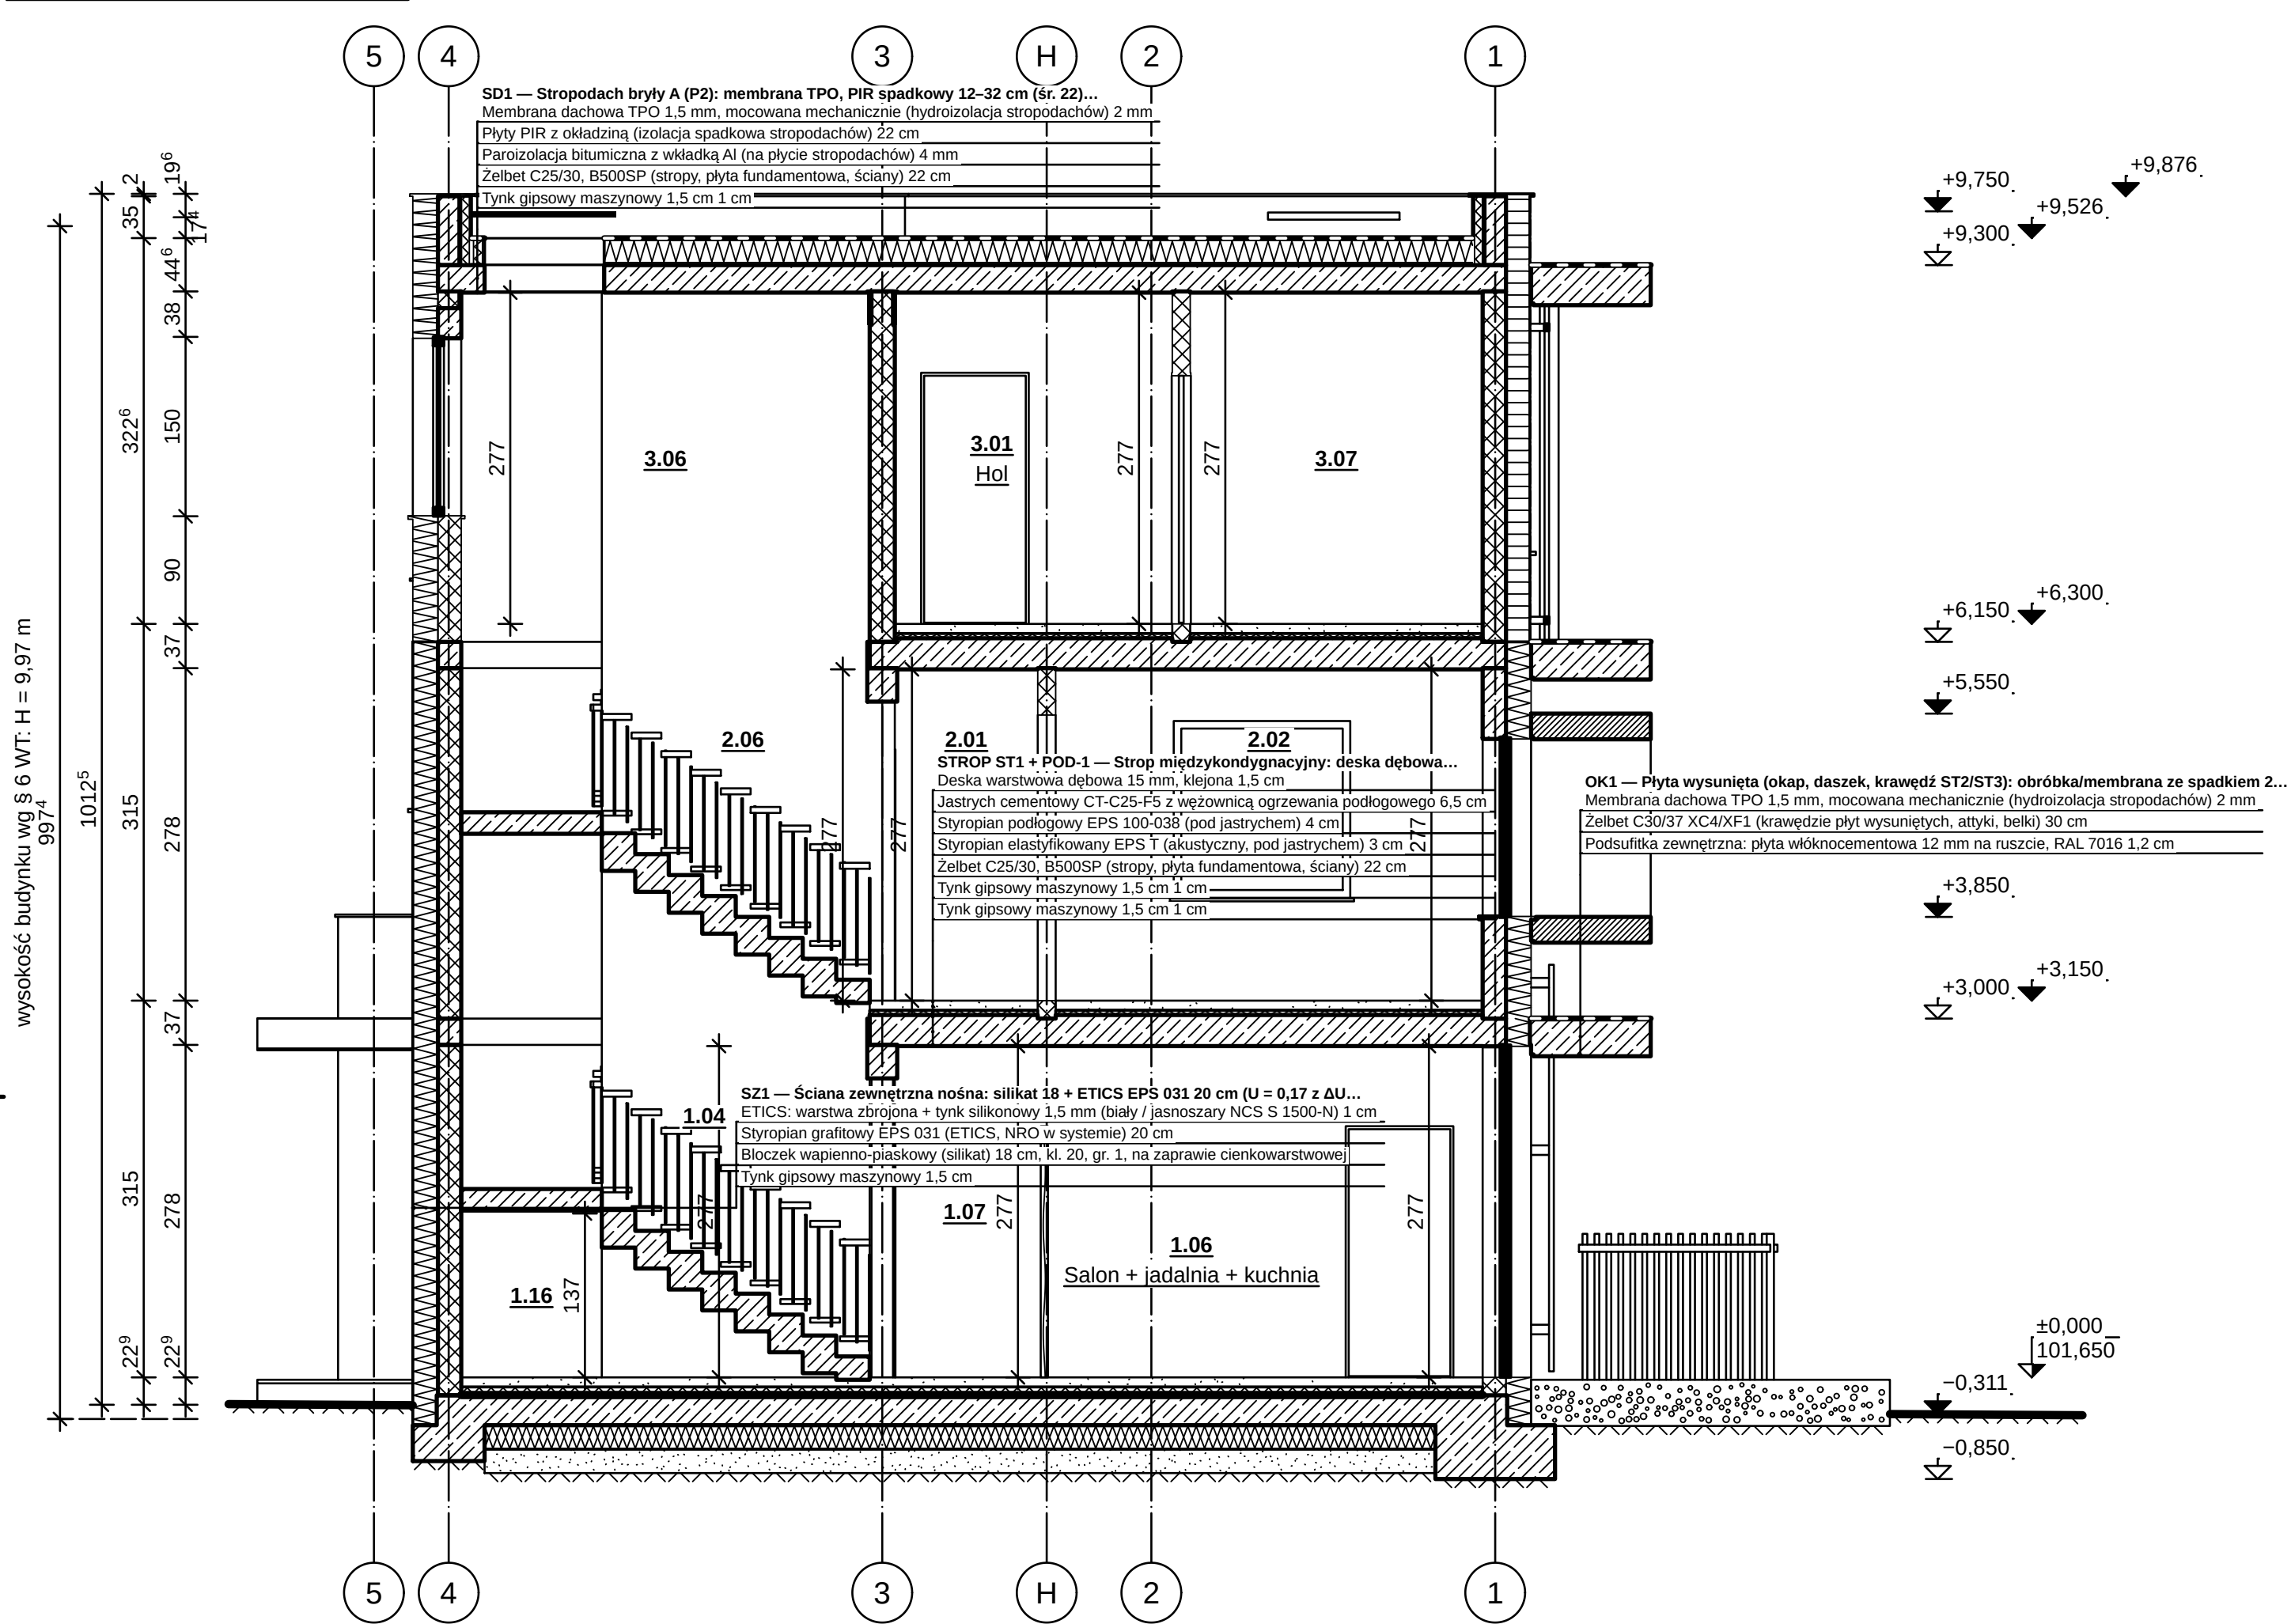

PRZĘKRÓJ B-B 1:50

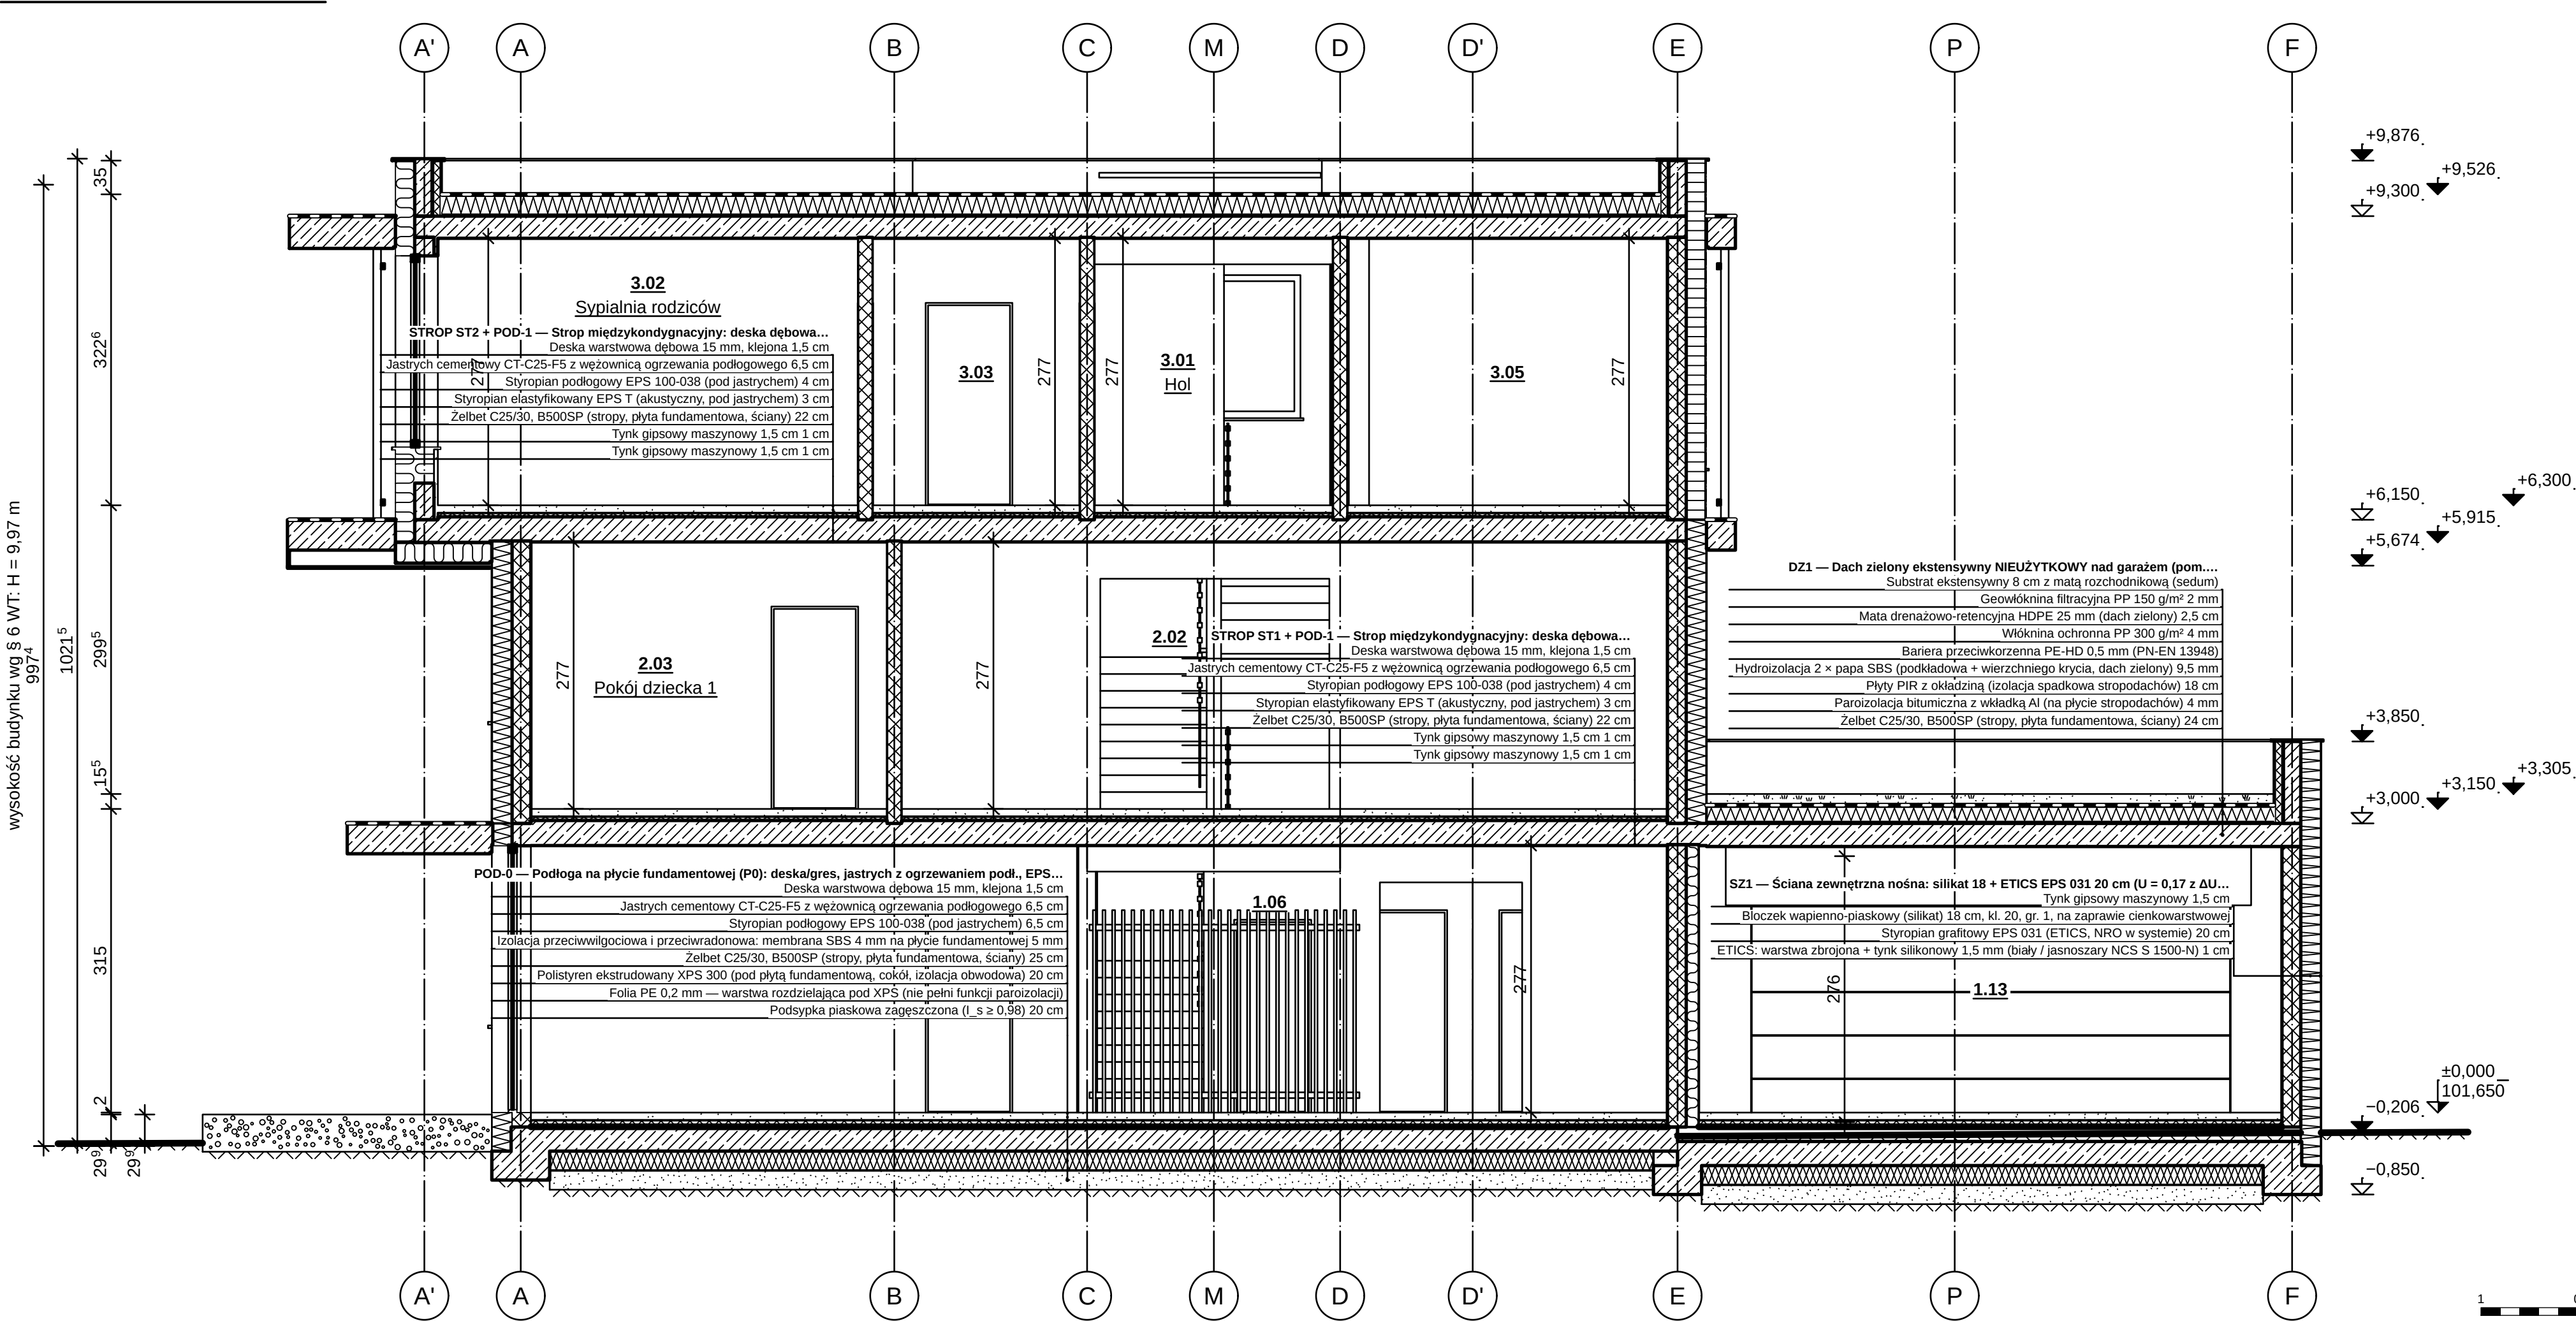

OBJAŚNIENIA I UWAGI

- Wymiary w cm (mm w indeksie górnym, np. 24⁵ = 24,5 cm), rzędne w m względem ±0,000 = 101,650 m n.p.m. (PL-EVRF2007-NH).
- Rzędne: trójkąt zaczerpnięty — poziom wykończenia, niezaczerpnięty — konstrukcji, w polowie zaczerpnięty — poziom ±0,000 z rzędną bezwzględną (PN-B-01025).
- Wysokość budynku wg § 6 WT: od terenu przy najniższej położonym wejściu (-0,348) do wierzchu stropodachu D1 (+9,626) — H = 9,97 m (bez atyki).
- Opisy warstw: kod i nazwa przegrody z modelu, materiały i grubości wg modelu (od góry / od lewej).
- Przekrój A-A: opisy warstw pominięte na rysunku (brak miejsca w podziale 1:50); STROP ST2 + POD-1, SD1, OK1 — układ warstw wg zestawienia przegród w części opisowej / przekroju 1:50.
- Przekrój B-B: opisy warstw pominięte na rysunku (brak miejsca w podziale 1:50); STROP ST2 + POD-1, SD1, OK1 — układ warstw wg zestawienia przegród w części opisowej / przekroju 1:50.
- Rysunek wygenerowany automatycznie z modelu model/budynek.yam1 (wersja 1.0, 2026-09-25) — generatory lamela.views.

ZNACZENIA MATERIAŁÓW (PN-B-01030 + przyjęte)

- Lamele dębowe 30×60 mm (ekran komunikacji P0, h 2,10 m); Deska warstwowa dębowa 15 mm, klejona — przekrój wzdłuż włókna
- grunt rodzimy
- Substrat ekstensywny 8 cm z matą rozchodnikową (sedum)
- Włna mineralna fasadowa (elewacja wentylowana bryły A, A1); Włna mineralna 035 (szkielet, docieplenia, ściana dom-garaz) — neander, JUKUT
- Płyty PIR z okładziną (izolacja spadkowa stropodachów) — zygzak z okładzinami
- Izolacja przeciwwilgociowa i przeciwdrożdżowa: membrana SBS 4 mm na płycie fundamentowej 5 mm; Żelbet C25/30, B500SP (stropy, płyta fundamentowa, ściany) 22 cm; Polistyren ekstrudowany XPS 300 (pod płytą fundamentową, cokół, izolacja obwodowa) 20 cm; Folia PE 0,2 mm — warstwa rozdzielająca pod XPS (nie pełni funkcji paroizolacji); Podsyłka piaskowa zagęszczona (l, s ≥ 0,98) 20 cm
- Membrana dachowa TPO 1,5 mm, mocowana mechanicznie (hydroizolacja stropodachów); Hydroizolacja 2 × papa SBS podkładowa + wierzchniego krycia, dach zielony) — pas czarno-biały
- Styropian gątowny EPS 031 (ETICS, NRO w systemie); Styropian podłogowy EPS 100-038 (pod jaskrychem); Styropian elastyczny EPS T (akustyczny, pod jaskrychem) — zygzak „VVV”
- Polistyren ekstrudowany XPS 300 (pod płytą fundamentową, cokół, izolacja obwodowa) — zygzak podkowy
- Jaskrych cementowy CT-C25-F5 z węzownicą ogrzewania podłogowego — kropki
- Membrana fasadowa wiatroizolacyjna UV-stabilna, czarna (sd = 0,02 m)
- Błoczek wapienno-piaskowy 12 cm, kl. 15 (ścianki działowe, licowy w klatce); Błoczek wapienno-piaskowy (silikat) 18 cm, kl. 20, gr. 1, na zaprawie cienkowarstwowej — kratka ukośna 45°/135°
- Paroizolacja bitumiczna z wkładką Al (na płycie stropodachów) — linia kreskowa cienka 3/1 po ciepłej stronie
- Podsyłka piaskowa zagęszczona (l, s ≥ 0,98)
- Płyta gipsowo-kartonowa 12,5 mm (GKB / GKBi w łazienkach); Podsyłka zewnętrzna: płyta włóknocementowa 12 mm na ruszcie, RAL 7016
- Okładziny blacharskie (blacha powlekana); Staloka — profile aluminiowe, antracyt; Rama boku C: ruszt stalowy ocynkowany w okładzinie z blachy aluminiowej RAL 7016 (pusta w środku); Stal malowana proszkowo (dalsztrady, tygiel) — zaznaczenie
- Szkło (szyby zespolone); Ścianka szklana VSG 2 × 8 mm w ramie aluminiowej (wiatrolap / hol)
- Żelbet C25/30, B500SP (stropy, płyta fundamentowa, ściany); Żelbet C30/37 XC4/XF1 (krawędzie płyt wysuniętych, atyki, belki) — 45° na przemian ciagle i przerywane
- Podbudowa nawierzchni (kruszywo)

REW.		OPIS ZMIANY		DATA	
0		Wydanie — rysunek wygenerowany z modelu		2026-09-25	
PRACOWNIA PROJEKTOWA PRACOWNIA PROJEKTOWA — nazwa do uzupełnienia			STADIUM PB	BRANŻA ARCHITEKTURA (AR)	
adres pracowni do uzupełnienia					
INWESTOR (do uzupełnienia)					
OBIEKT / NAZWA ZAMIERZENIA BUDOWLANEGO Budynek mieszkalny jednorodzinny wolnostojący „Dom LAMELA”					
ADRES / LOKALIZACJA (NR DZIAŁKI, OBRĘB, JEDN. EWIDENCYJNA) ul. Lipowa (fikcyjna), dz. nr ewid. 1234, obręb 0005 Przykładowo, gm. Przykładowo (fikcyjna)				KAT. OBIEKTU	
FUNKCJA	IMIĘ I NAZWISKO	SPECJALNOŚĆ, NR UPRAWNIENI	DATA	PODPIS	
Projektant	[DO UZUPEŁNIENIA]	[DO UZUPEŁNIENIA]			
Projektant (wsp.)	[DO UZUPEŁNIENIA]	[DO UZUPEŁNIENIA]			
Sprawdzający	nie dotyczy (art. 20 ust. 3 pkt 2 PB)	—			
Opracował	[DO UZUPEŁNIENIA]	[DO UZUPEŁNIENIA]			
TYTUŁ RYSUNKU					
PRZĘKROJE A-A I B-B					
SKALA	FORMAT	DATA WYDANIA	RODZAJ DOK.	NR RYSUNKU	
1:50	1130x420	2026-09-25	przekrój	PB-AR-04	
				ARKUSZ	REW.
				4/5	0