


RZUT II PIĘTRA 1:50

OBJAŚNIENIA I UWAGI (cd.)

6. Rysunek projektu technicznego (RPT § 24 pkt 1) wykonany z tego samego stanu modelu co rysunki PB-AR-xx projektu architektoniczno-budowlanego (tom I); stan modelu: SHA-256 98826e2b39ab (budynek, działka, instalacja, wyposażenie).
7. Układ warstw przegrod, stolarka, wykończenia, odwodnienie — część ogólna PT-1-AR; wezły — detale PT-AR-D.
8. Rysunek wygenerowany automatycznie z modelu modelbudynek.yaml (wersja 1.0, 2026-09-25) — generatory lamela.views.

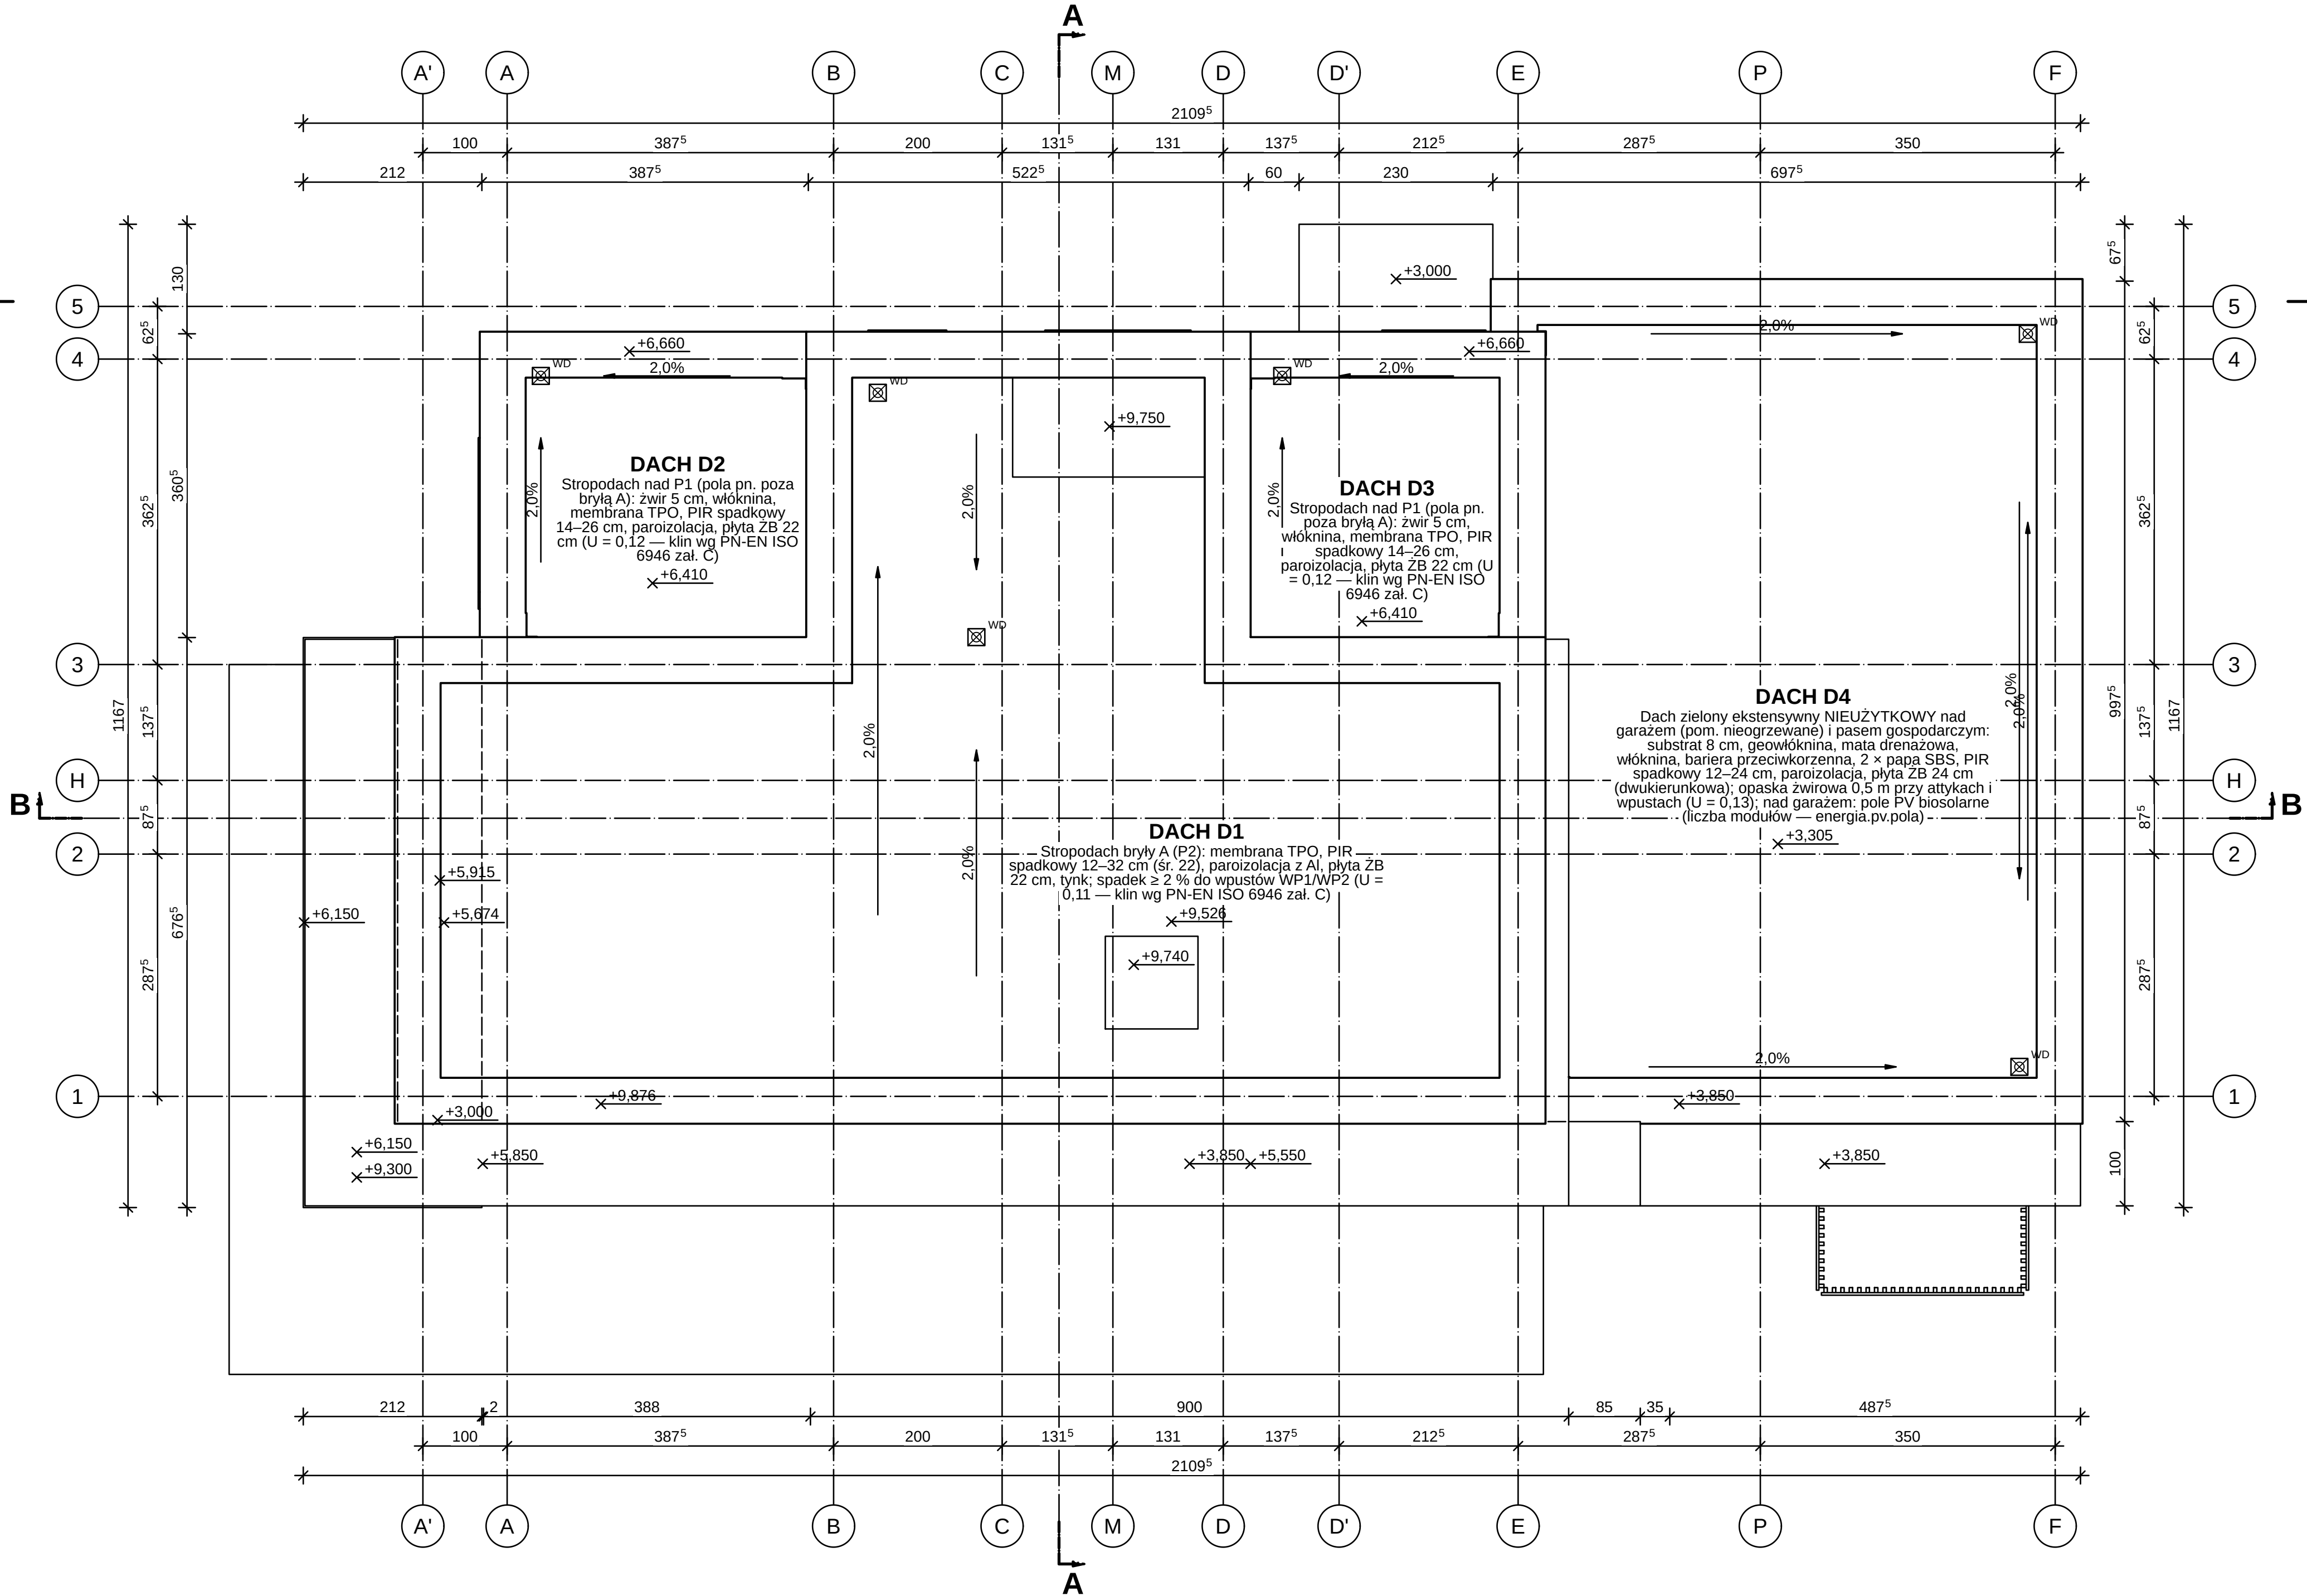

RZUT DACHU 1:50

OZNACZENIA MATERIAŁÓW (PN-B-01030 + przyjęte)

- Włókna mineralna 035 (szkielet, docieplenia, ściana dom-garaż). Włókna mineralna fasadowa (elewacja wentylowana bryły A, A1) — meander „UUU”
Styropian grafitowy EPS 031 (ETICS, NFO w systemie) — zygnak „VVV”
Membrana fasadowa wiatroizolacyjna UV-stabilna, czarna (sd = 0,02 m)
Błoczek wapniowo-piaskowy 12 cm, kl. 15 (ścianki działowe, łocowy w klatce); Błoczek wapniowo-piaskowy (silikat) 18 cm, kl. 20, gr. 1, na zaprawie cienkowarstwowej — kłaska ukośna 45°/135°
Żelbet C25/30, B500SP (stropy, płyta fundamentowa, ściany); Żelbet C30/37 XC4/XF1 (krawędzie płyt wysuniętych, atyki, belki) — 45° na przemian ciagle i przerywane

OZNACZENIA LINII

- elementy nad płaszczyznę cięcia (obrys płyt, wsporników, brył wyższych kondygnacji)
— elementy poniżej płaszczyzny cięcia (widok z góry)
— osie konstrukcyjne; linia punktowa z pogrubionymi końcami — ślad przekroju

OBJAŚNIENIA I UWAGI

1. Wymiary w cm (mm w indeksie górnym, np. 24° = 24,5 cm), rzędne w m względem ±0,000 = 101,650 m n.p.m. (PL-EVPF2007-NH).
2. Rzuty: płaszczyzna cięcia +1,10 m nad posadzką kondygnacji. Linia kreskową — elementy nad płaszczyznę cięcia (obrys płyt i wsporników, brył wyższych kondygnacji), otwory w stropie nad, belki); linią cieniłą — elementy poniżej (widok).
3. Otwory: licznik — szerokość; mianownik — wysokość w świetle muru, w nawiasie wysokość parapetu; symbol stolarki wg zestawienia stolarki.
4. Numeracja pomieszczeń wg PN-B-01025 / PN-EN ISO 4157-2: -nn kondygnacji (parter = 1) <->-nn, identyfikator w modelu: <klond>-<parter> (parter = 0).
5. Drzwi: strona otwierania (lewe/prawe) wg modelu — patrząc od strony, w którą otwiera się skrzydło.

ZESTAWIENIE POMIESZCZEŃ

Nr	Nazwa pomieszczenia	Posadzka	Kat.	Wys. [m]	Pow. [m²]
3.02	Sypialnia rodziców	Deska warstwowa dębowa 15 mm, klejona	podst.	2,77	21,43
3.05	Gabinet / pokój gościnny okazjonalny	Deska warstwowa dębowa 15 mm, klejona	podst.	2,77	16,25
3.03	Garderoba (przedpokój apartamentu)	Deska warstwowa dębowa 15 mm, klejona	pomoc.	2,77	10,49
3.07	Pom. techniczne (centrala rekuperacyjna, wentyl na dach)	Płytki gresowe 60x120 na kleju C2TE S1	techn.	2,77	5,90
3.01	Hol	Deska warstwowa dębowa 15 mm, klejona	ruchu	2,77	5,74
3.04	Łazienka rodziców	Płytki gresowe 60x120 na kleju C2TE S1	pomoc.	2,77	5,51
3.08	Szacht instalacyjny SI		techn.	2,77	0,45
3.06	Klatka schodowa (wyjście z biegu 2, pustaka)	Deska warstwowa dębowa 15 mm, klejona	ruchu	2,77	0,24
RAZEM powierzchnia netto					66,01
w tym podstawowa + pomocnicza					53,67



REW.	OPIS ZMIANY	DATA
0	Wydanie — rysunek wygenerowany z modelu	2026-09-25
PRACOWNIA PROJEKTOWA	PRACOWNIA PROJEKTOWA — nazwa do uzupełnienia	STADIUM
BRANZA	ARCHITEKTURA (AR)	PT
INWESTOR	(do uzupełnienia)	
OBJEKT / NAZWA ZAMIERZENIA BUDOWLANEGO	Budynek mieszkalny jednorodzinny wolnostojący „Dom LAMELA”	
ADRES / LOKALIZACJA (NR DZIAŁKI, OBRĘB, JEDN. EWIDENCYJNA)	ul. Lipowa (fikcyjna), dz. nr ewid. 123/4, obręb 0005 Przykładowo, gm. Przykładowo (fikcyjna)	KAT. OBJEKTU
1		
FUNKCJA	IMIĘ I NAZWISKO	SPECJALNOŚĆ, NR UPRAWNIENI
Projektant	[DO UZUPEŁNIENIA]	[DO UZUPEŁNIENIA]
Projektant (wsp.)	[DO UZUPEŁNIENIA]	[DO UZUPEŁNIENIA]
Sprawdzający	nie dotyczy (art. 20 ust. 3 pkt 2 PB)	—
Opracował	[DO UZUPEŁNIENIA]	[DO UZUPEŁNIENIA]
TYTUŁ RYSUNKU	RZUT II PIĘTRA I RZUT DACHU	
SKALA	1:50	FORMAT
580x891	DATA WYDANIA	2026-09-25
RZUT	RODZAJ DOK.	NR RYSUNKU
PT-AR-03	ARKUSZ	3/5
REW.	0	