



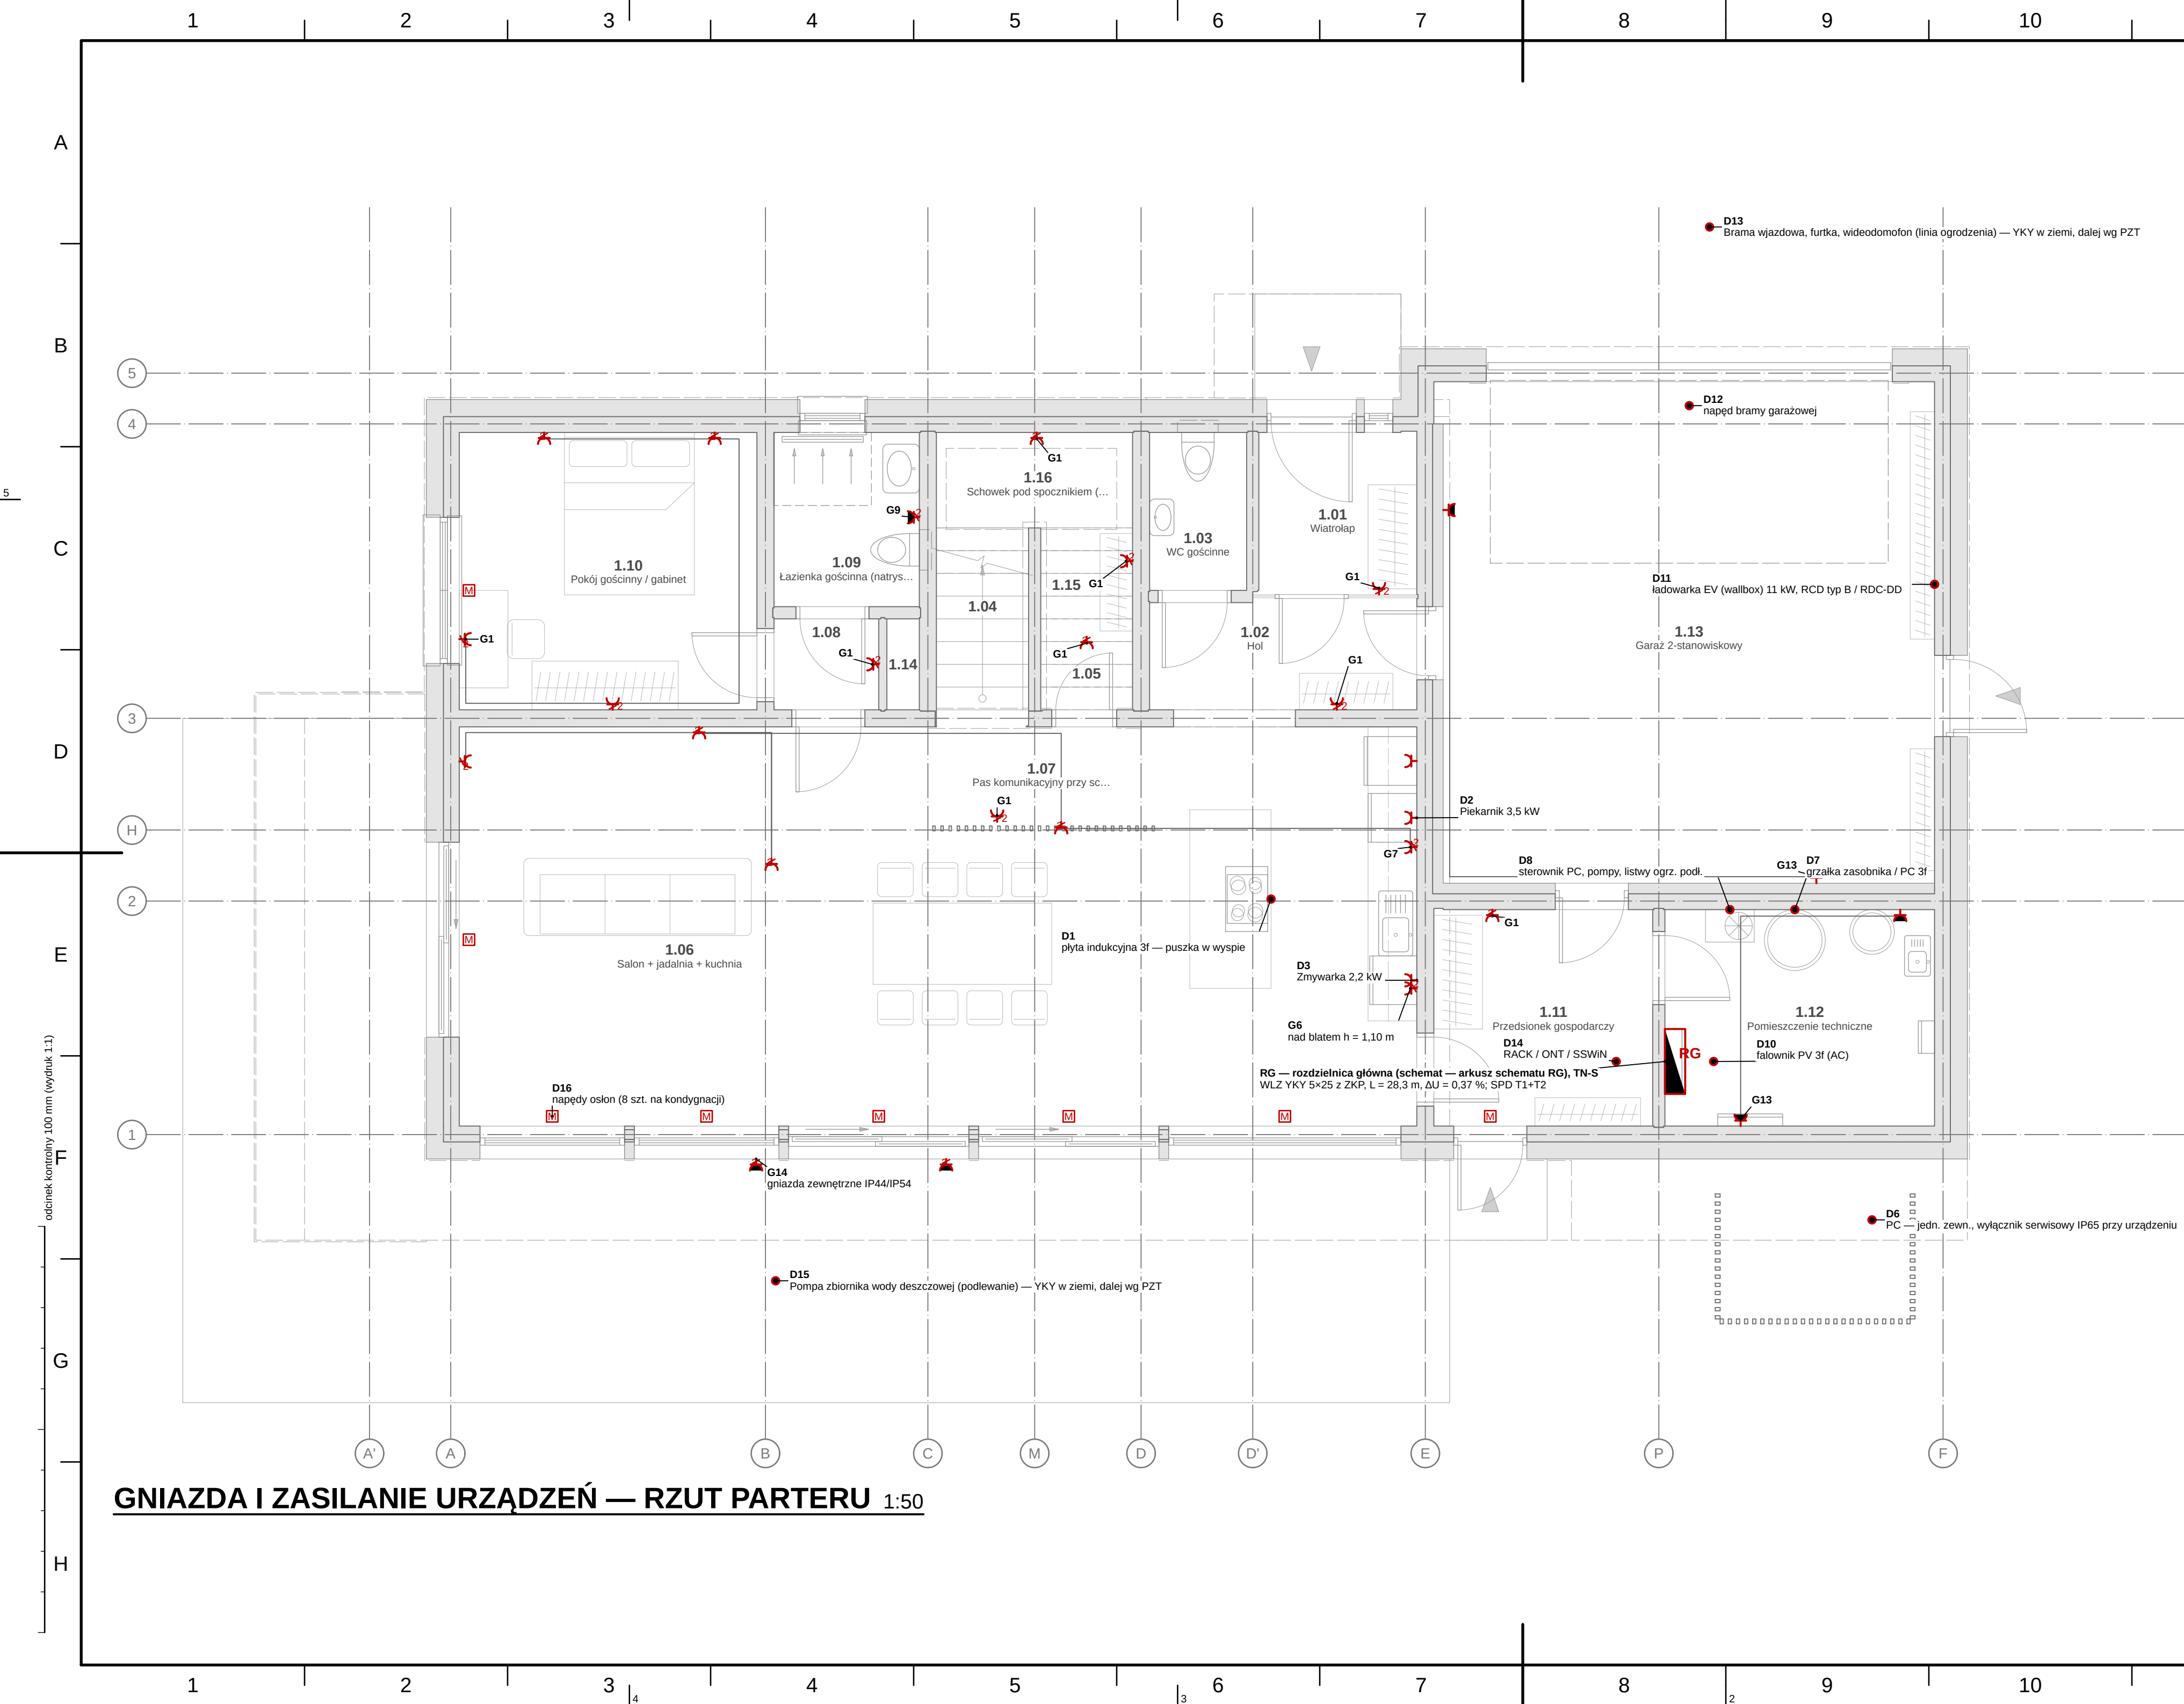

OZNACZENIA — LEGENDA SYMBOLI

Symbolne instalacji elektrycznych wg IEC 60617 (baza IEC; PN-EN 60617 — wycofana, stosowana jako praktyka branżowa) i PN-EN ISO 14617; oznaczenia teletechniczne — praktyka branżowa. Obowiązuje legenda na arkuszu.

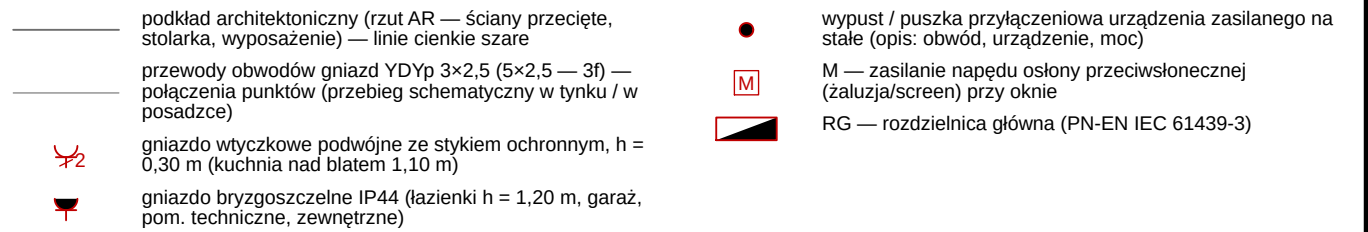


OBWODY NA ARKUSZU (lamela.obliczenia.elektryka.obwody)

Obw.	Odbiorniki	Zab.	Przewód	L [m]	ΔU [%]	Faza	RCD
G1	Gniazda P0: 0,10 Pokój gościnny / gabinet, 0,08 Przedpokój gościnny, 0,14 Szafka instalacyjna S1, 0,04 Kłaska schodowa, 0,16 Schowek pod spóżnikiem (h < 1,40), 0,07 Pas komunikacyjny przy schodach, 0,05 Szpiarnia, 0,15 Schowek pod schodami (h 1,40–2,20), 0,02 Hol, 0,01 Wiatrołap, 0,11 Przedśionek gospodarczy	B16	YDyp 3×2,5	5,6	1,02	L1	RCBO typ A 30 mA
G6	Gniazda kuchenne 1 (0,06 Salon + jadalnia + kuchnia)	B16	YDyp 3×2,5	15,8	2,21	L1	RCBO typ A 30 mA
G7	Gniazda kuchenne 2 (0,06 Salon + jadalnia + kuchnia)	B16	YDyp 3×2,5	15,8	2,21	L3	RCBO typ A 30 mA
G9	Gniazda łazienki (0,09 Łazienka gościnnia (natrysk))	B16	YDyp 3×4	23,2	1,99	L1	RCBO typ A 30 mA
G13	Gniazda garażu / pom. technicznego (IP44)	B16	YDyp 3×2,5	5,5	1,01	L2	RCBO typ A 30 mA
G14	Gniazda zewnętrzne (taras, ogród; IP44/IP54)	B16	YDyp 3×4	27,5	2,30	L3	RCBO typ A 30 mA
D1	Płyta indukcyjna	3P B16	YDyp 5×2,5	11,3	0,80	3f	RCD 4P 40 A/30 mA typ A
D2	Piekarnik	B16	YDyp 3×2,5	15,8	2,11	L2	RCBO typ A 30 mA
D3	Zmywarka	B16	YDyp 3×2,5	8,0	0,90	L3	RCBO typ A 30 mA
D6	Pompa ciepła — jednostka zewnętrzna (PC-R290-07 (przykład))	C16	YDyp 3×2,5	9,4	1,15	L1	RCBO typ F/B 30 mA wg DTR
D7	Grzałka rezerwowa PC / zasobnika c.w.u. (6,0 kW)	3P B10	YDyp 5×2,5	6,6	0,57	3f	RCD 4P 40 A/30 mA typ A
D8	Sterowanie PC, pompy obiegowe, listwy ogrzewania podłogowego	B10	YDyp 3×1,5	6,6	0,47	L3	RCBO typ A 30 mA
D10	Falownik PV 3f (6,0 kW AC)	3P B16	YDyp 5×2,5	3,0	0,46	3f	RCD typ B 30 mA
D11	Ładowarka EV 11 kW (3f) — garaż; przewód na 22 kW	3P C20	YDY 5×6	9,6	0,59	3f	własny RCD typ B 30 mA lub A-EV + RDC-DD 6 mA DC
D12	Naped bramy garażowej	B10	YDyp 3×1,5	13,4	0,57	L3	RCBO typ A 30 mA
D13	Brama wjazdowa, furtka, wideodomofon (linia ogrodzenia)	B16	YKY 3×2,5	23,2	0,70	L3	RCBO typ A 30 mA
D14	Teletechnika: ONT, router, szafka RACK, SSWIN	B16	YDyp 3×2,5	3,0	0,39	L2	RCBO typ A 30 mA
D15	Pompa zbiornicza wody deszczowej (podwlewanie)	B16	YKY 3×2,5	25,7	0,95	L1	RCBO typ A 30 mA
D16	Napedy osion przeciwniosłonecznych (19 szt.)	B10	YDyp 3×1,5	3,0	0,66	L2	RCBO typ A 30 mA

OBJAŚNIENIA I UWAGI

1. Średnice przewody w mm (d_z – średnica wewnętrzna, Ø/DN – kanalizacja, kanały wentylacyjne), przekroje żył w mm², odległości i rzędne w m; z₀ = 100 160,5 m (p.d. – PL-EVRF2007-NH).
2. Rysunki instalacji na podkładzie zrostu architektury (PB-AR), podkład – linie ciemne szare (warstwy I PCD30 KALD).
3. Instalacja gniazd wtyczkowych i zasilania urządzeń w PN-AR 60364-4-41 (samoczynne wyłączenie, ROD 30 mA dla gniazd ≤ 32 A – p. 411.3.3, PN-AR 60364-5-52 (przewody), PN-AR 60364-7-701 (zabezpieczenia), PN-AR 60364-7-726 (dławienie EMI); WT § 180–188 (obwody gniazd oddzielne od obwodów, gniazda ze stykiem ochrannym).
4. Bilans mocy (lamela obliczenia elektryka, bilans): P_{inst} = 71,3 kW, P_{szczyt} z DLM = 24,8 kW, P_z przył = 27 kW, zabezpieczenie przedlicznikowe 40 A.
5. Liczbie i rozmieszczenie gniazd wyznaczono algorytmicznie (praktyka branżowa, DIN 18015-2): przy łóżkach, biurkach, sofach, nad białem kuchennym co ok. 1,1 m, przy wtykiarkach (poza strefami 0 i 2), pozostałe równomiernie wzdłuż ścian bez otworów; urządzenia stałe – wzdłuż instalacji doświetlenia i wentylacji D_z – gniazda w obwodach D_z.
6. Wykonywano montażu (pomocniczo): gniazda 0,30 m; nad białem 1,10 m; łazienki 1,20 m (IP44); garaż, pom. techniczne 1,10 m (IP44); łączniki 1,10 m.
7. Rysunek wygenerowany automatycznie z modelu model/budynki_yam1 (wersja 1.0, 2026-09-25) – generatory lamela views.

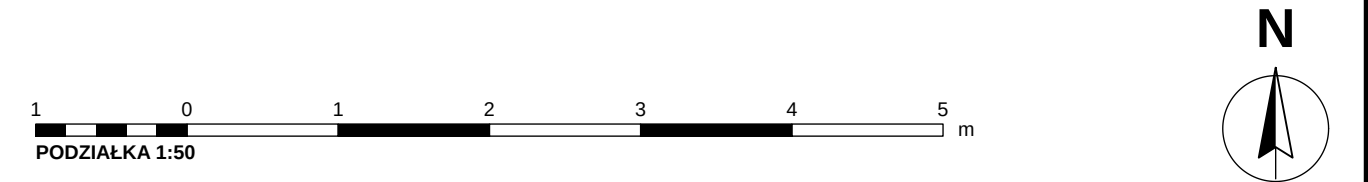

REW.	OPIS ZMIANY				DATA	
0	Wydanie — rysunek wygenerowany z modelu				2026-09-25	
PRACOWNIA PROJEKTOWA PRACOWNIA PROJEKTOWA — nazwa do uzupełnienia adres pracowni do uzupełnienia			STADIUM PT		BRANŻA INSTALACJE ELEKTRYCZNE (IE)	
INWESTOR (do uzupełnienia)						
OBJEKT / NAZWA ZAMIERZENIA BUDOWLANEGO Budynek mieszkalny jednorodzinny wolnostojący „Dom LAMELA”						
ADRES / LOKALIZACJA (NR DZIAŁKI, OBREB, JEDN. EWIDENCYJNA) ul. Lipowa (fikcyjna), dz. nr ewid. 123/4, obręb 0005 Przykładowo, gm. Przykładowo (fikcyjna)					KAT. OBIEKTU I	
FUNKCJA		IMIĘ I NAZWISKO		SPECJALNOŚĆ, NR UPRAWNIENIŃ	DATA	PODPIS
Projektant		[DO UZUPEŁNIENIA]		[DO UZUPEŁNIENIA]		
Projektant (wsp.)		[DO UZUPEŁNIENIA]		[DO UZUPEŁNIENIA]		
Sprawdzający		nie dotyczy (art. 20 ust. 3 pkt 2 PB)		—		
Opracował		[DO UZUPEŁNIENIA]		[DO UZUPEŁNIENIA]		
TYTUŁ RYSUNKU						
GNIAZDA I ZASILANIE URZĄDZEŃ — RZUT PARTERU						
SKALA 1:50	FORMAT 750×420	DATA WYDANIA 2026-09-25	RODZAJ DOK. rzut instalacji	NR RYSUNKU PT-IE-04	ARKUSZ 4/14	REW. 0