




KOLORYSTYKA I MATERIAŁY ELEWACJI

1	ETICS: warstwa zbrojona + tynk silikonowy 1,5 mm (biały / jasnoszary NCS S 1500-N) [TYNK_SIL]	#f5f4f0
2	Szko (szyby zespolone) [SZKLO]	#a9c3cd
3	Membrana fasadowa wiatroizolacyjna UV-stabilna, czarna (sd = 0,02 m) [MEMB_WIATR]	#1d1d1d
4	Lamele elewacyjne 40×80 mm, drewno termojesion (klasa 1 trwałości), olejowane [DREWNO_TERMIO]	#9b6b41
5	Żelbet C30/37 XC4/XF1 (krawędzie płyt wysuniętych, atyki, belki) [ZB_C30]	#b4b1a9
6	Stolarka — profile aluminiowe, antracyt [RAMA_ALU]	#2b2f33
7	Rama boku C: ruszt stalowy ocynkowany w okładzinie z blachy aluminiowej RAL 7016 (pusta w środku) [RAMA_C]	#3b4044
8	Podbudowa nawierzchni (kruszywo) [NAW_PODBUDOWA]	#8d877d
9	Drzwi zewnętrzne, płycina aluminiowa [DRZWI_ZEWN]	#34383c
10	Stal malowana proszkowo (balustrady, rygle) [STAL_BAL]	#2c3034
11	Podsufitka zewnętrzna: płyta włóknocementowa 12 mm na ruszcie, RAL 7016 [PODSUF]	#474b4f
12	Obróbki blacharskie (blacha powlekana) [OBROBKA_BLACH]	#3b3f43
13	Deska tarasowa [NAW_DESKA]	#6d5847

OBJAŚNIENIA I UWAGI

- Wymiary w cm (mm w indeksie górnym, np. 24² = 24,5 cm), rzędne w m względem ±0,000 = 101,650 m n.p.m. (PL-EVRF2007-NH).
- Rzędne: trójkąt zaczerniony — poziom wykończenia, niezaczerniony — konstrukcji, w pokoiwie zaczerniony — poziom ±0,000 z rzędną bezwzględną (PN-B-01025).
- Wysokość budynku wg § 6 WT: od terenu przy najniżej położonym wejściu (−0,267) do wierzchu stropodachu D1 (+9,526) — H = 9,79 m (bez attyk).
- Kolorystyka orientacyjna wg kolorów materiałów w modelu (do potwierdzenia wzornikiem RAL/NCS).
- Rysunek wygenerowany automatycznie z modelu /home/user/aihouse/model/budynek.yaml (wersja 1.0, 2026-09-25) — generatory lamela.views.

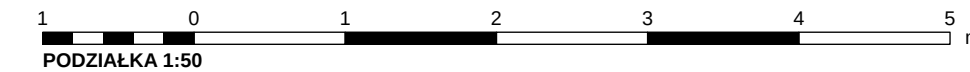

REW.	OPIS ZMIANY				DATA	
0	Wydanie — rysunek wygenerowany z modelu				2026-09-25	
PRACOWNIA PROJEKTOWA PRACOWNIA PROJEKTOWA — nazwa do uzupełnienia adres pracowni do uzupełnienia				STADIUM PB	BRANŻA ARCHITEKTURA (AR)	
INWESTOR (do uzupełnienia)						
OBIEKT / NAZWA ZAMIERZENIA BUDOWLANEGO Budynek mieszkalny jednorodzinny wolnostojący „Dom LAMELA”						
ADRES / LOKALIZACJA (NR DZIAŁKI, OBREB, JEDN. EWIDENCYJNA) ul. Lipowa (fikcyjna), dz. nr ewid. 123/4, obręb 0005 Przykładowo, gm. Przykładowo (fikcyjna)					KAT. OBIEKTU I	
FUNKCJA		IMIĘ I NAZWISKO		SPECJALNOŚĆ, NR UPRAWNIENIEN	DATA	PODPIS
Projektant						
Projektant (wsp.)						
Sprawdzający						
Opracował						
TYTUŁ RYSUNKU ELEWACJA POŁUDNIOWA (OGRODOWA)						
SKALA 1:50	FORMAT A3×3	DATA WYDANIA 2026-09-25	RODZAJ DOK. elewacja	NR RYSUNKU PB-AR-07	ARKUSZ 7/10	REW. 0