


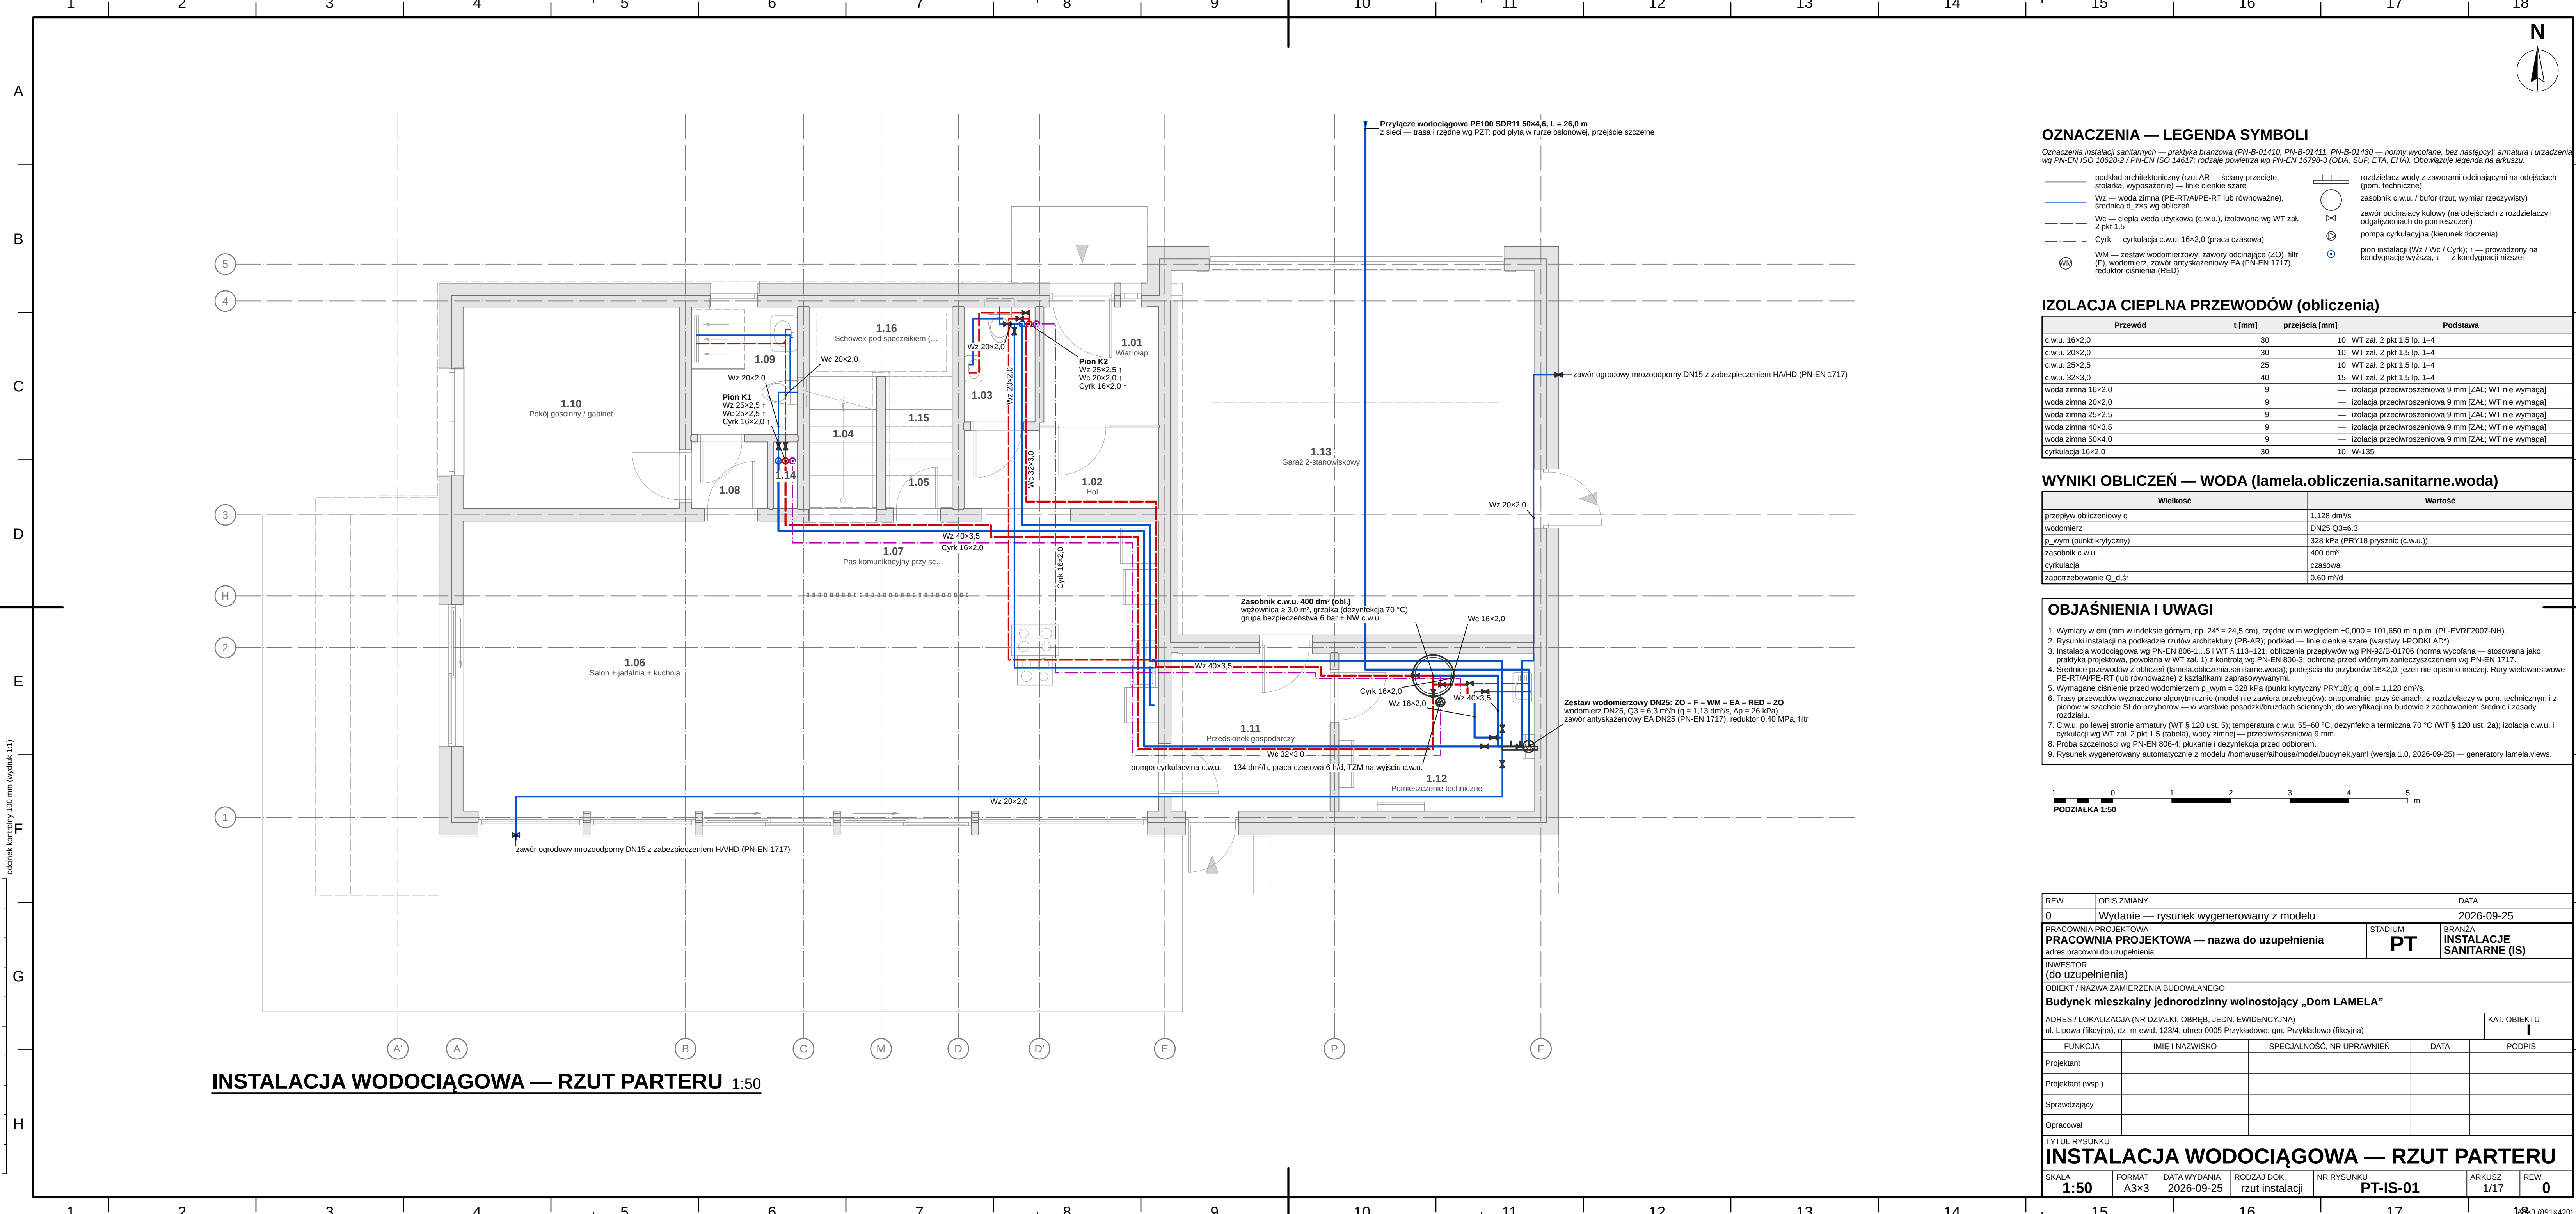

INSTALACJA WODOCIĄGOWA — RZUT PARTERU 1:50

OZNACZENIA — LEGENDA SYMBOLI

Oznaczenia instalacji sanitarnych — praktyka branżowa (PN-B-01410, PN-B-01411, PN-B-01430 — normy wycofane, bez następcy); armatura i urządzenia wg PN-EN ISO 10628-2 / PN-EN ISO 14617; rodzaje powietrza wg PN-EN 16798-3 (ODA, SUP, ETA, EHA). Obowiązuje legenda na arkuszu.

—	podkład architektoniczny (rzut AR — ściany przecięte, stolarka, wyposażenie) — linie cienkie szare	—	rozdzielnice wody z zaworami odcinającymi na odejściach (pom. techniczne)
—	Wz — woda zimna (PE-RT/AlPE-RT lub równoważne), średnica d _z ×s wg obliczeń	—	zasobnik c.w.u. / bufor (rzut, wymiar rzeczywisty)
—	Wc — ciepła woda użytkowa (c.w.u.), izolowana wg WT zał. 2 pkt 1.5	—	zawór odcinający kulowy (na odejściach z rozdzielaczy i odgłęzieniach do pomieszczeń)
—	Cyrk — cyrkulacja c.w.u. 16×2,0 (praca czasowa)	—	pompa cyrkulacyjna (kierunek tłoczenia)
—	WM — zestaw wodomierzowy: zawory odcinające (ZO), filtr (F), wodomierz, zawór antyskażeniowy EA (PN-EN 1717), reduktor ciśnienia (RED)	—	—

IZOLACJA CIEPLNA PRZEWODÓW (obliczenia)


Przewód	t [mm]	przejścia [mm]	Podstawa
c.w.u. 16×2,0	30	10	WT zał. 2 pkt 1.5 lp. 1–4
c.w.u. 20×2,0	30	10	WT zał. 2 pkt 1.5 lp. 1–4
c.w.u. 25×2,5	25	10	WT zał. 2 pkt 1.5 lp. 1–4
c.w.u. 32×3,0	40	15	WT zał. 2 pkt 1.5 lp. 1–4
woda zimna 16×2,0	9	—	izolacja przeciwwoszeniowa 9 mm [ZAL; WT nie wymaga]
woda zimna 20×2,0	9	—	izolacja przeciwwoszeniowa 9 mm [ZAL; WT nie wymaga]
woda zimna 25×2,5	9	—	izolacja przeciwwoszeniowa 9 mm [ZAL; WT nie wymaga]
woda zimna 40×3,5	9	—	izolacja przeciwwoszeniowa 9 mm [ZAL; WT nie wymaga]
woda zimna 50×4,0	9	—	izolacja przeciwwoszeniowa 9 mm [ZAL; WT nie wymaga]
cyrkulacja 16×2,0	30	10	W-135

WYNIKI OBLICZEŃ — WODA (lamela.obliczenia.sanitarne.woda)

Wielkość	Wartość
przepływ obliczeniowy q	1,128 dm³/s
wodomierz	DN25 Q3=6.3
p _{wym} (punkt krytyczny)	328 kPa (PRY18 przysznic (c.w.u.))
zasobnik c.w.u.	400 dm³
cyrkulacja	czasowa
zapotrzebowanie Q _{d,śr}	0,60 m³/d

OBJAŚNIENIA I UWAGI

- Wymiary w cm (mm w indeksie górnym, np. 24^h = 24,5 cm), rzędne w m względem ±0,000 = 101,650 m n.p.m. (PL-EVRF2007-NH).
- Rysunki instalacji na podkładzie rzutów architektury (PB-AR); podkład — linie cienkie szare (warstwy I-PODKLAD).
- Instalacja wodociągowa wg PN-EN 806-1...5 i WT § 113–121; obliczenia przepływów wg PN-92/B-01706 (norma wycofana — stosowana jako praktyka projektowa, powołana w WT zał. 1) z kontrolą wg PN-EN 806-3; ochrona przed wtórnym zanieczyszczeniem wg PN-EN 1717.
- Średnice przewodów z obliczeń (lamela.obliczenia.sanitarne.woda); podejścia do przyborów 16×2,0, jeżeli nie opisano inaczej. Rury wielowarstwowe PE-RT/AlPE-RT (lub równoważne) z kształtkami zaprasowywanymi.
- Wymagane ciśnienie przed wodomierzem p_{wym} = 328 kPa (punkt krytyczny PRY18); q_{obl} = 1,128 dm³/s.
- Trasy przewodów wyznaczono algorytmicznie (model nie zawiera przebiegów); ortogonalnie, przy ścianach, z rozdzielaczami w pom. technicznym i z pionów w szachcie SI do przyborów — w warstwie posadzkibruzdach ściennych; do weryfikacji na budowie z zachowaniem średnic i zasady rozdziału.
- C.w.u. po lewej stronie armatury (WT § 120 ust. 5); temperatura c.w.u. 55–60 °C, dezynfekcja termiczna 70 °C (WT § 120 ust. 2a); izolacja c.w.u. i cyrkulacji wg WT zał. 2 pkt 1.5 (tabela), wody zimnej — przeciwwoszeniowa 9 mm.
- Próba szczelności wg PN-EN 806-4; plukanie i dezynfekcja przed odbiorem.
- Rysunek wygenerowany automatycznie z modelu /home/user/alhouse/model/budynek.yaml (wersja 1.0, 2026-09-25) — generatory lamela.views.

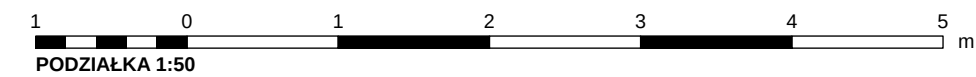

REW.	OPIS ZMIANY	DATA				
0	Wydanie — rysunek wygenerowany z modelu	2026-09-25				
PRACOWNIA PROJEKTOWA PRACOWNIA PROJEKTOWA — nazwa do uzupełnienia adres pracowni do uzupełnienia		STADIUM PT	BRANŻA INSTALACJE SANITARNE (IS)			
INWESTOR (do uzupełnienia)						
OBIEKT / NAZWA ZAMIERZENIA BUDOWLANEGO Budynek mieszkalny jednorodzinny wolnostojący „Dom LAMELA”						
ADRES / LOKALIZACJA (NR DZIAŁKI, OBRĘB, JEDN. EWIDENCYJNA) ul. Lipowa (fikcyjna), dz. nr ewid. 123/4, obręb 0005 Przykładowo, gm. Przykładowo (fikcyjna)			KAT. OBIEKTU I			
FUNKCJA	IMIĘ I NAZWISKO	SPECJALNOŚĆ, NR UPRAWNIENI	DATA	PODPIS		
Projektant						
Projektant (wsp.)						
Sprawdzający						
Opracował						
TYTUŁ RYSUNKU INSTALACJA WODOCIĄGOWA — RZUT PARTERU						
SKALA 1:50	FORMAT A3×3	DATA WYDANIA 2026-09-25	RODZAJ DOK. rzut instalacji	NR RYSUNKU PT-IS-01	ARKUSZ 1/17	REW. 0