


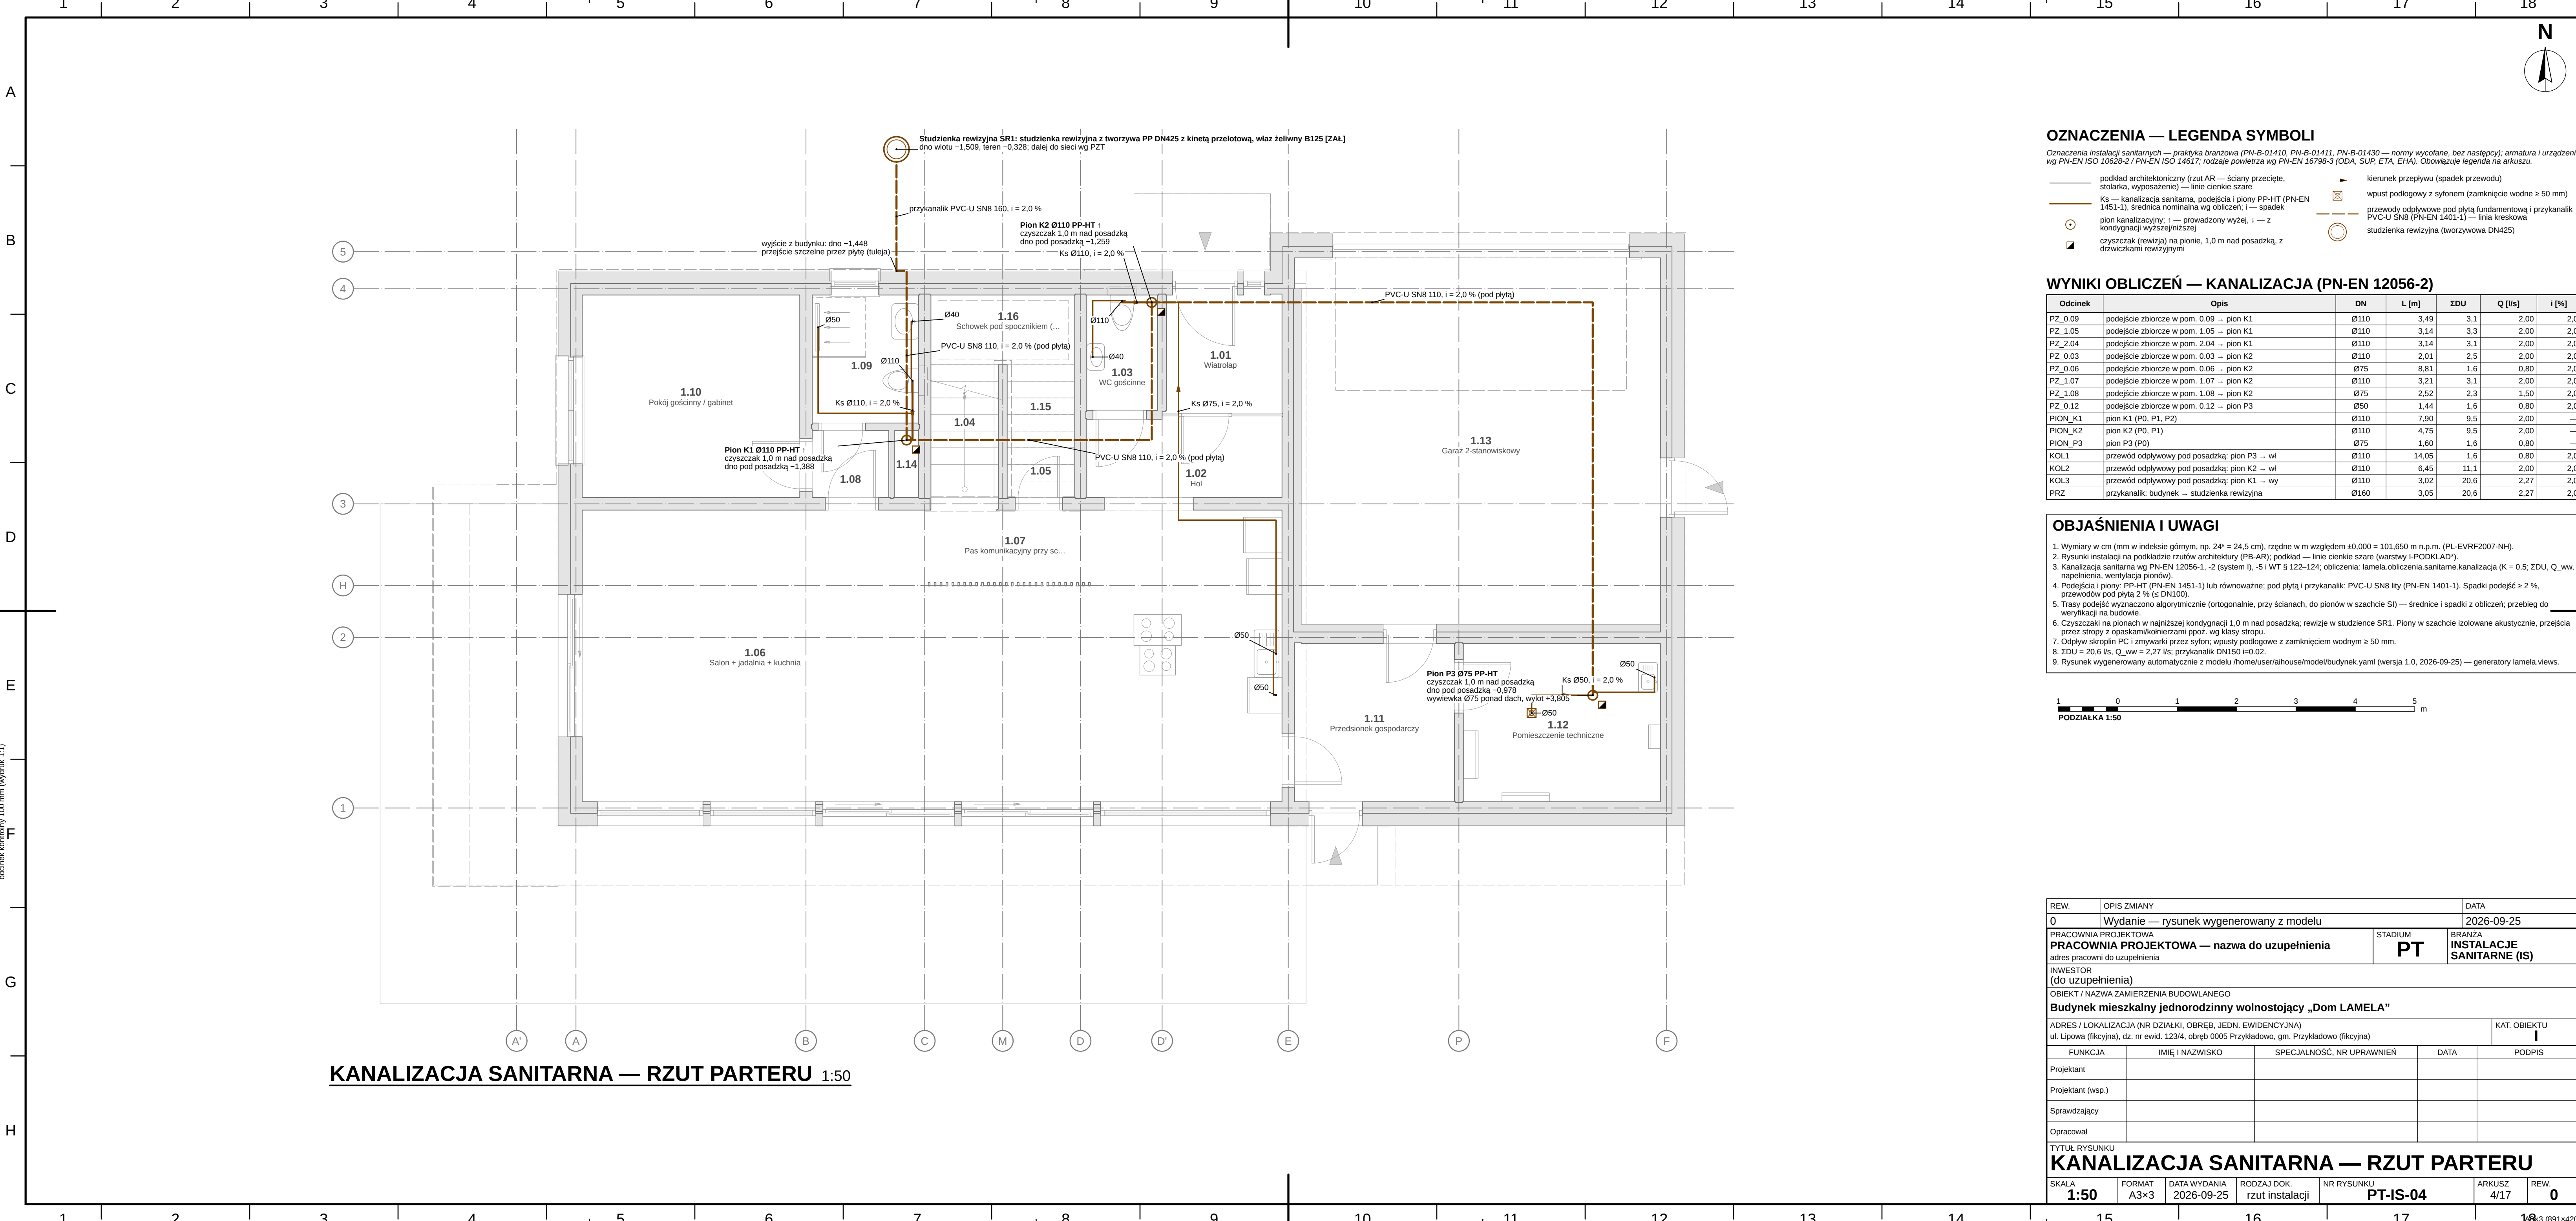

KANALIZACJA SANITARNA — RZUT PARTERU 1:50

OZNACZENIA — LEGENDA SYMBOLI

Oznaczenia instalacji sanitarnych — praktyka brązowa (PN-B-01410, PN-B-01411, PN-B-01430 — normy wycofane, bez następcy); armatura i urządzenia wg PN-EN ISO 10628-2 / PN-EN ISO 14617; rodzaje powietrza wg PN-EN 16798-3 (ODA, SUP, ETA, EHA). Obowiązuje legenda na arkuszu.


	podkład architektoniczny (rzut AR — ściany przecięte, stolarka, wyposażenie) — linie cienkie szare		kierunek przepływu (spadek przewodu)
	Ks — kanalizacja sanitarna, podejście i pion PP-HT (PN-EN 1451-1), średnica nominalna wg obliczeń; i — spadek		wpust podłogowy z syfonem (zamknięcie wodne ≥ 50 mm)
	pion kanalizacyjny; 1 — prowadzony wyżej, i — z kondygnacji wyższej/niższej		przewody odpływowe pod płytą fundamentową i przykanalik PVC-U SN8 (PN-EN 1401-1) — linia kreskowa
	czyszczak (rewizja) na pionie, 1.0 m nad posadzką, z drzwiczkami rewizyjnymi		studzienka rewizyjna (tworzywna DN425)

WYNIKI OBLICZEŃ — KANALIZACJA (PN-EN 12056-2)

Odcinek	Opis	DN	L [m]	ΣDU	Q [l/s]	i [%]
PZ_0.09	podejście zbiorcze w pom. 0.09 → pion K1	Ø110	3,49	3,1	2,00	2,0
PZ_1.05	podejście zbiorcze w pom. 1.05 → pion K1	Ø110	3,14	3,3	2,00	2,0
PZ_2.04	podejście zbiorcze w pom. 2.04 → pion K1	Ø110	3,14	3,1	2,00	2,0
PZ_0.03	podejście zbiorcze w pom. 0.03 → pion K2	Ø110	2,01	2,5	2,00	2,0
PZ_0.06	podejście zbiorcze w pom. 0.06 → pion K2	Ø75	8,81	1,6	0,80	2,0
PZ_1.07	podejście zbiorcze w pom. 1.07 → pion K2	Ø110	3,21	3,1	2,00	2,0
PZ_1.08	podejście zbiorcze w pom. 1.08 → pion K2	Ø75	2,52	2,3	1,50	2,0
PZ_0.12	podejście zbiorcze w pom. 0.12 → pion P3	Ø50	1,44	1,6	0,80	2,0
PION_K1	pion K1 (P0, P1, P2)	Ø110	7,90	9,5	2,00	—
PION_K2	pion K2 (P0, P1)	Ø110	4,75	9,5	2,00	—
PION_P3	pion P3 (P0)	Ø75	1,60	1,6	0,80	—
KOL1	przewód odpływowy pod posadzką; pion P3 → wł	Ø110	14,05	1,6	0,80	2,0
KOL2	przewód odpływowy pod posadzką; pion K2 → wł	Ø110	6,45	11,1	2,00	2,0
KOL3	przewód odpływowy pod posadzką; pion K1 → wy	Ø110	3,02	20,6	2,27	2,0
PRZ	przykanalik: budynek → studzienka rewizyjna	Ø160	3,05	20,6	2,27	2,0

OBJAŚNIENIA I UWAGI

- Wymiary w cm (mm w indeksie górnym, np. 24⁴ = 24,5 cm), rzędne w m względem ±0,000 = 101,650 m n.p.m. (PL-EVRF2007-NH).
- Rysunki instalacji na podkładzie rzutów architektury (PB-AR); podkład — linie cienkie szare (warstwy I-PODKŁAD).
- Kanalizacja sanitarna wg PN-EN 12056-1, -2 (system I), -5 i WT § 122–124; obliczenia: lamela.obliczenia.sanitarne.kanalizacja (K = 0,5; ΣDU, Q_{ww}, napełnienia, wentylacja pionów).
- Podejścia i pion: PP-HT (PN-EN 1451-1) lub równoważne; pod płytą i przykanalik: PVC-U SN8 lity (PN-EN 1401-1). Spadki podejść ≥ 2 ‰, przewodów pod płytą 2 ‰ (≤ DN100).
- Trasy podejść wyznaczono algorytmicznie (ortogonalnie, przy ścianach, do pionów w szachcie SI) — średnice i spadki z obliczeń; przebieg do weryfikacji na budowie.
- Czyszczaki na pionach w najwyższej kondygnacji 1.0 m nad posadzką; rewizje w studziennce SR1. Piony w szachcie izolowane akustycznie, przejścia przez stropy z opaskami/kolierzami ppo, wg klasy stropu.
- Odpływ skroplin PC i zmywarki przez syfon; wpusty podłogowe z zamknięciem wodnym ≥ 50 mm.
- ΣDU = 20,6 l/s, Q_{ww} = 2,27 l/s; przykanalik DN150 i=0.02.
- Rysunek wygenerowany automatycznie z modelu /home/user/aihouse/model/budynek.yaml (wersja 1.0, 2026-09-25) — generatory lamela.views.

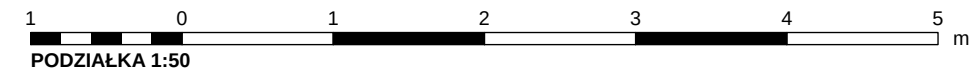

REW.		OPIS ZMIANY		DATA		
0		Wydanie — rysunek wygenerowany z modelu			2026-09-25	
PRACOWNIA PROJEKTOWA PRACOWNIA PROJEKTOWA — nazwa do uzupełnienia				STADIUM PT	BRANZA INSTALACJE SANITARNE (IS)	
adres pracowni do uzupełnienia						
INWESTOR (do uzupełnienia)						
OBIEKT / NAZWA ZAMIERZENIA BUDOWLANEGO						
Budynek mieszkalny jednorodzinny wolnostojący „Dom LAMELA”						
ADRES / LOKALIZACJA (NR DZIAŁKI, OBRĘB, JEDN. EWIDENCYJNA) ul. Lipowa (fikcyjna), dz. nr ewid. 123/4, obręb 0005 Przykładowo, gm. Przykładowo (fikcyjna)					KAT. OBIEKTU I	
FUNKCJA		IMIĘ I NAZWISKO		SPECJALNOŚĆ, NR UPRAWNIEŃ	DATA	PODPIS
Projektant						
Projektant (wsp.)						
Sprawdzający						
Opracował						
TYTUŁ RYSUNKU						
KANALIZACJA SANITARNA — RZUT PARTERU						
SKALA 1:50	FORMAT A3×3	DATA WYDANIA 2026-09-25	RODZAJ DOK. rzut instalacji	NR RYSUNKU PT-IS-04	ARKUSZ 4/17	REW. 0