


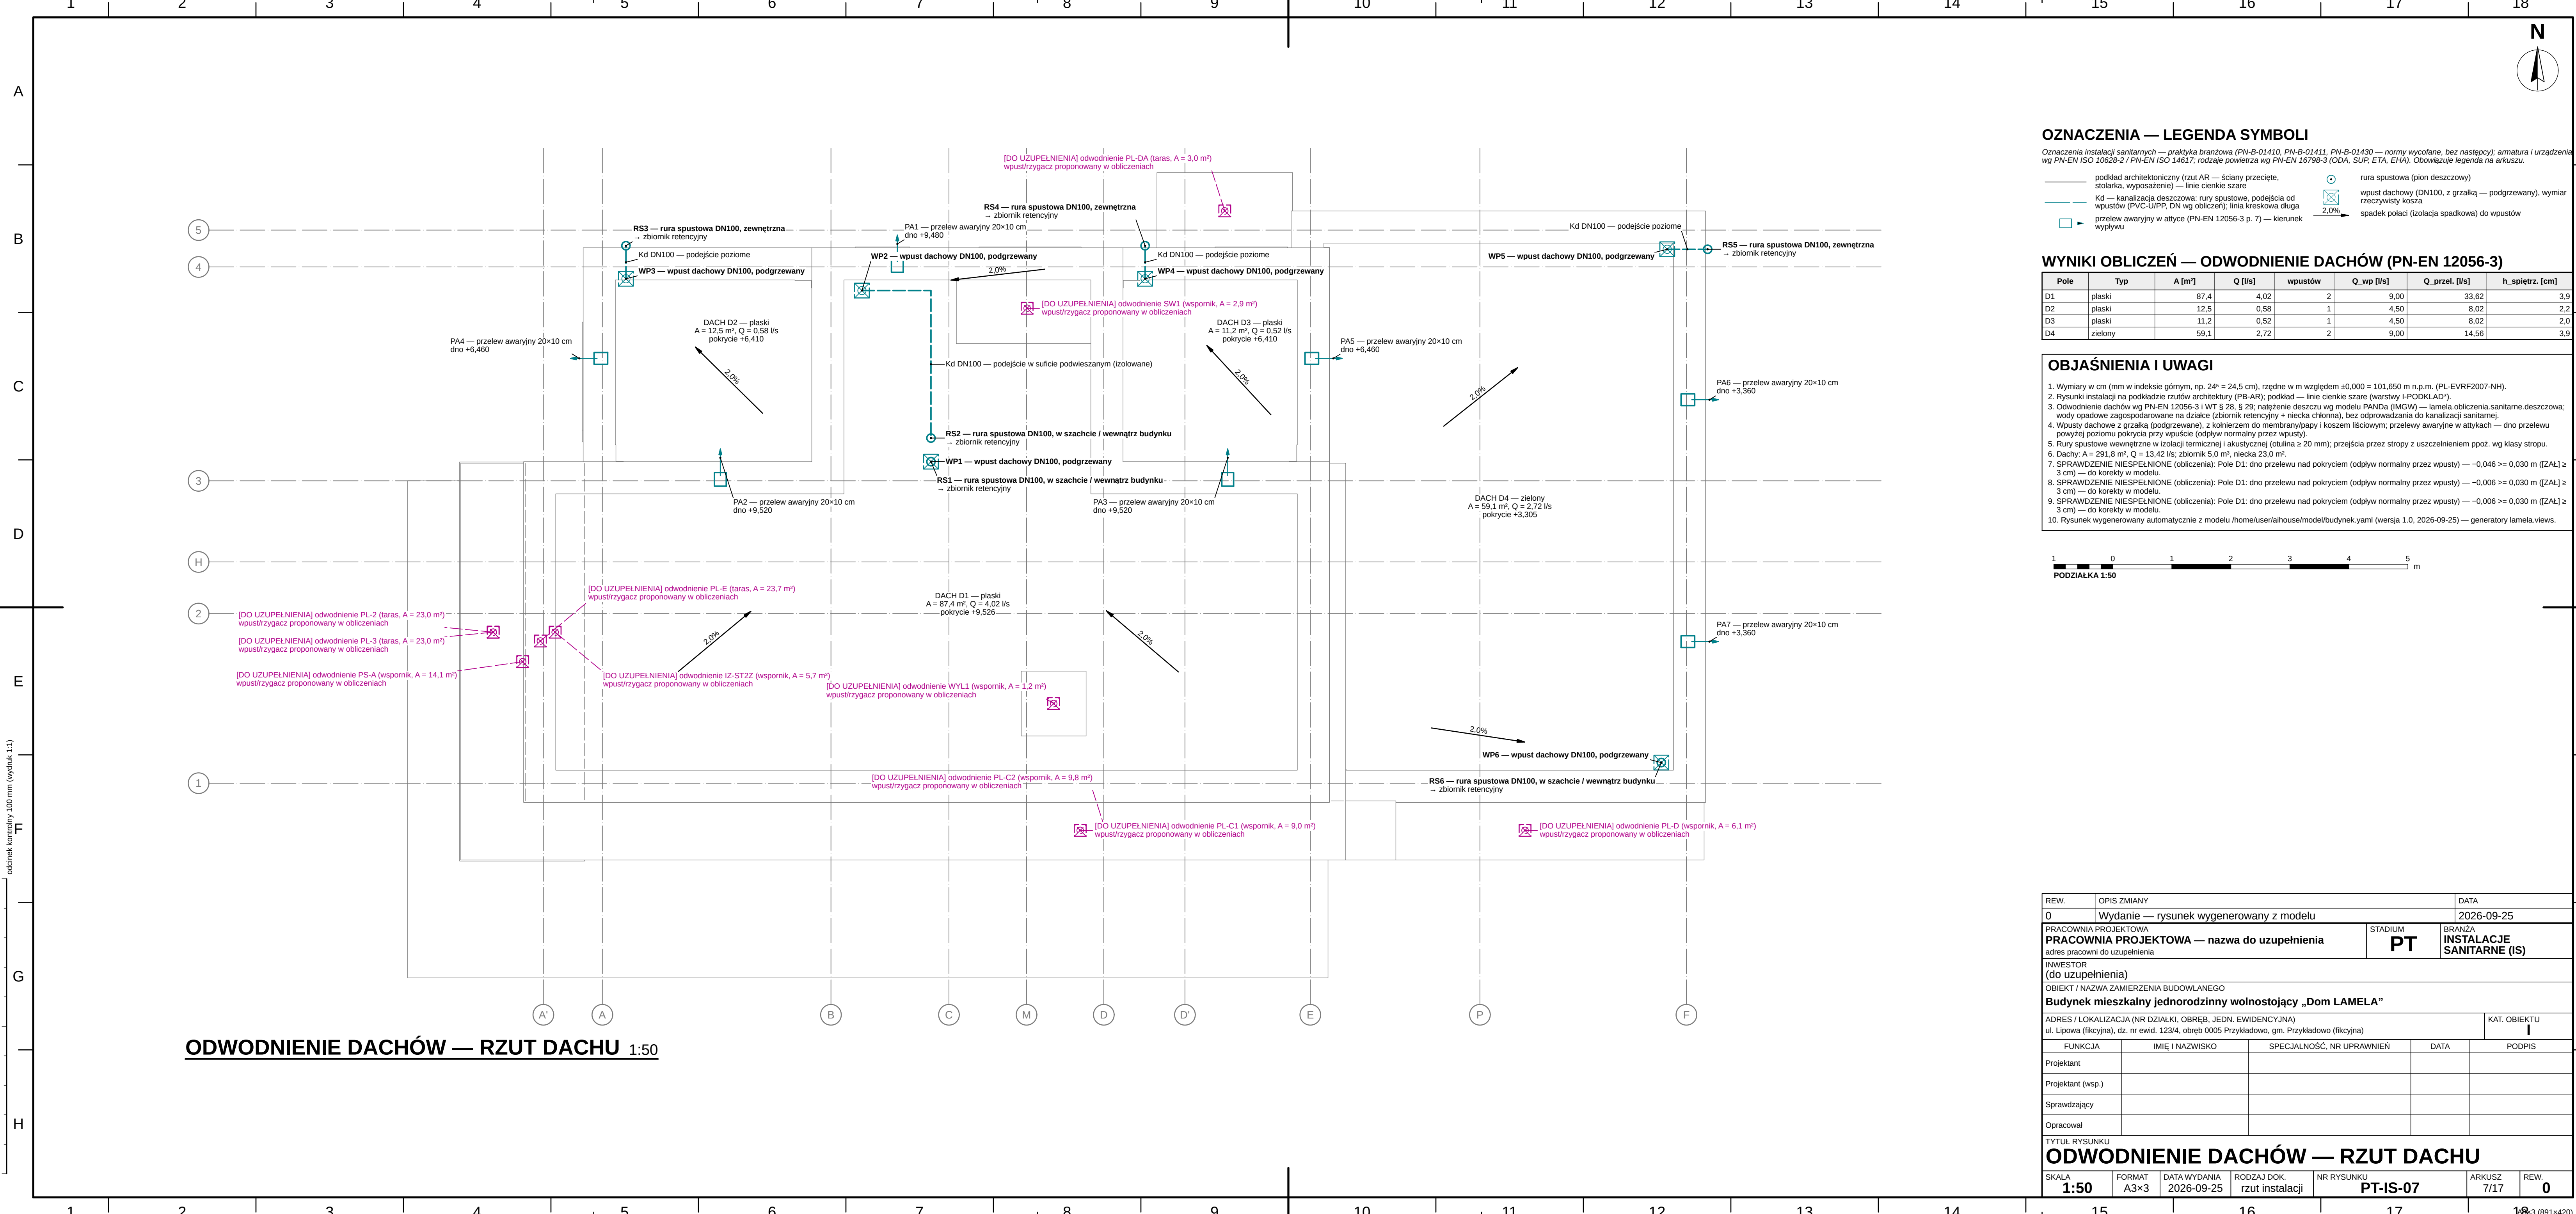

ODWODNIENIE DACHÓW — RZUT DACHU 1:50

OZNACZENIA — LEGENDA SYMBOLI

Oznaczenia instalacji sanitarnych — praktyka branżowa (PN-B-01410, PN-B-01411, PN-B-01430 — normy wycofane, bez następcy); armatura i urządzenia wg PN-EN ISO 10628-2 / PN-EN ISO 14617; rodzaje powietrza wg PN-EN 16798-3 (ODA, SUP, ETA, EHA). Obowiązuje legenda na arkuszu.


	podkład architektoniczny (rzut AR — ściany przecięte, stolarka, wyposażenie) — linie cienkie szare		rura spustowa (pion deszczowy)
	Kd — kanalizacja deszczowa: rury spustowe, podejścia od wpustów (PVC-U/PP, DN wg obliczeń); linia kreskowa długa		wpust dachowy (DN100, z grzałką — podgrzewany), wymiar rzeczywisty kosza
	przelew awaryjny w attyce (PN-EN 12056-3 p. 7) — kierunek wypływu		spadek pola (izolacja spadkowa) do wpustów

WYNIKI OBLICZEŃ — ODWODNIENIE DACHÓW (PN-EN 12056-3)

Pole	Typ	A [m²]	Q [l/s]	wpustów	Q_wp [l/s]	Q_przel. [l/s]	h_spiętrz. [cm]
D1	plaski	87,4	4,02	2	9,00	33,62	3,9
D2	plaski	12,5	0,58	1	4,50	8,02	2,2
D3	plaski	11,2	0,52	1	4,50	8,02	2,0
D4	zielony	59,1	2,72	2	9,00	14,56	3,9

OBJAŚNIENIA I UWAGI

- Wymiary w cm (mm w indeksie górnym, np. 24" = 24,5 cm), rzędne w m względem ±0,000 = 101,650 m n.p.m. (PL-EVRF2007-NH).
- Rysunki instalacji na podkładzie rzutów architektury (PB-AR); podkład — linie cienkie szare (warstwy I-PODKŁAD).
- Odwodnienie dachów wg PN-EN 12056-3 i WT § 28, § 29; natężenie deszczu wg modelu PANDA (IMGW) — lamela obliczenia sanitarne deszczowa; wody opadowe zagospodarowane na działce (zbiornik retencyjny + niekaa chłonna), bez odprowadzania do kanalizacji sanitarnej.
- Wpusty dachowe z grzałką (podgrzewane), z kolnierzem do membrany/papy i koszem liściowym; przelewy awaryjne w attykach — dno przelewu powyżej poziomu pokrycia przy wpuscie (odpływ normalny przez wpusty).
- Rury spustowe wewnętrzne w izolacji termicznej i akustycznej (średnica ≥ 20 mm); przejścia przez stropy z uszczelnieniem ppoż. wg klasy stropu.
- Dachy: A = 291,8 m², Q = 13,42 l/s; zbiornik 5,0 m³, niekaa 23,0 m³.
- SPRAWDZENIE NIESPEŁNIŁO (obliczenia): Pole D1: dno przelewu nad pokryciem (odpływ normalny przez wpusty) — -0,046 >= 0,030 m ([ZAL] ≥ 3 cm) — do korekty w modelu.
- SPRAWDZENIE NIESPEŁNIŁO (obliczenia): Pole D1: dno przelewu nad pokryciem (odpływ normalny przez wpusty) — -0,006 >= 0,030 m ([ZAL] ≥ 3 cm) — do korekty w modelu.
- SPRAWDZENIE NIESPEŁNIŁO (obliczenia): Pole D1: dno przelewu nad pokryciem (odpływ normalny przez wpusty) — -0,006 >= 0,030 m ([ZAL] ≥ 3 cm) — do korekty w modelu.
- Rysunek wygenerowany automatycznie z modelu /home/user/aihouse/model/budynek.yaml (wersja 1.0, 2026-09-25) — generatory lamela.views.

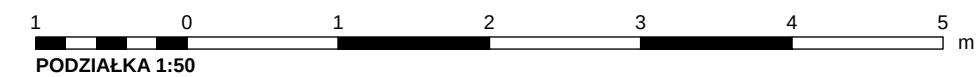

REW.	OPIS ZMIANY			DATA		
0	Wydanie — rysunek wygenerowany z modelu			2026-09-25		
PRACOWNIA PROJEKTOWA PRACOWNIA PROJEKTOWA — nazwa do uzupełnienia adres pracowni do uzupełnienia				STADIUM PT	BRANŻA INSTALACJE SANITARNE (IS)	
INWESTOR (do uzupełnienia)						
OBIEKT / NAZWA ZAMIERZENIA BUDOWLANEGO						
Budynek mieszkalny jednorodzinny wolnostojący „Dom LAMELA”						
ADRES / LOKALIZACJA (NR DZIAŁKI, OBRĘB, JEDN. EWIDENCYJNA) ul. Lipowa (fikcyjna), dz. nr ewid. 123/4, obręb 0005 Przykładowo, gm. Przykładowo (fikcyjna)						
KAT. OBIEKTU I						
FUNKCJA	IMIĘ I NAZWISKO	SPECJALNOŚĆ, NR UPRAWNIENI	DATA			PODPIS
Projektant						
Projektant (wsp.)						
Sprawdzający						
Opracował						
TYTUŁ RYSUNKU						
ODWODNIENIE DACHÓW — RZUT DACHU						
SKALA 1:50	FORMAT A3×3	DATA WYDANIA 2026-09-25	RODZAJ DOK. rzut instalacji	NR RYSUNKU PT-IS-07	ARKUSZ 7/17	
					REW. 0	