


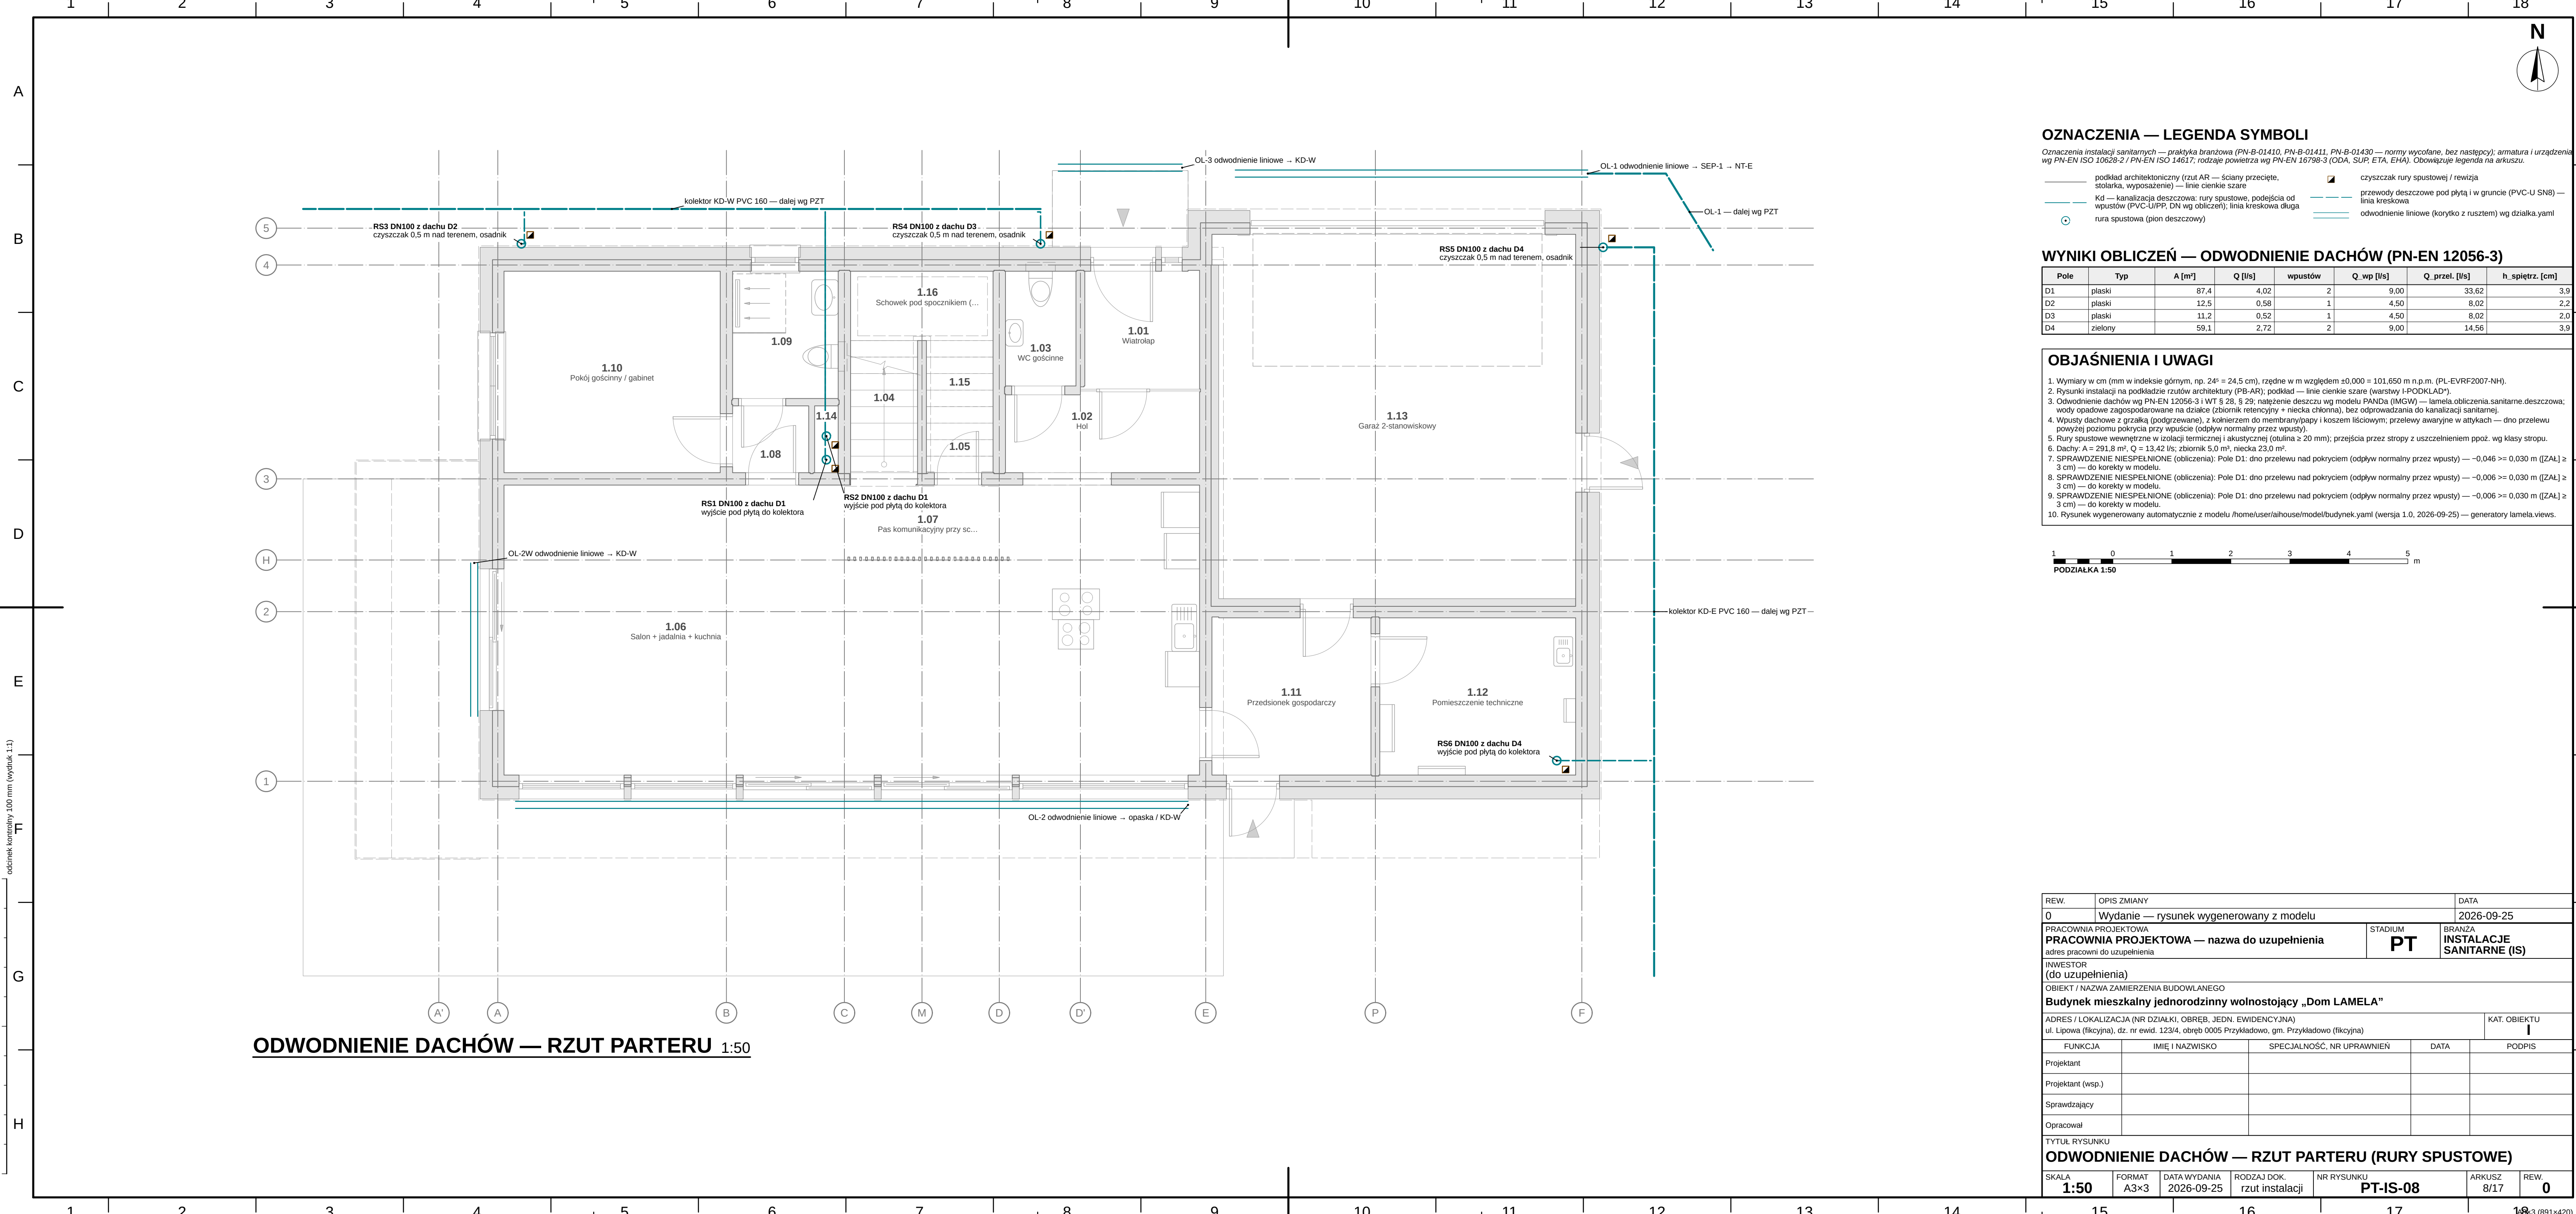

ODWODNIENIE DACHÓW — RZUT PARTERU 1:50

OZNACZENIA — LEGENDA SYMBOLI

Oznaczenia instalacji sanitarnych — praktyka branżowa (PN-B-01410, PN-B-01411, PN-B-01430 — normy wycofane, bez następcy); armatura i urządzenia wg PN-EN ISO 10628-2 / PN-EN ISO 14617; rodzaje powietrza wg PN-EN 16798-3 (ODA, SUP, ETA, EHA). Obowiązuje legenda na arkuszu.

	podkład architektoniczny (rzut AR — ściany przecięte, stolarka, wyposażenie) — linie cienkie szare		czyszczak rury spustowej / rewizja
	Kd — kanalizacja deszczowa: rury spustowe, podejścia od wpustów (PVC-U/PP, DN wg obliczeń); linia kreskowa długa		przewody deszczowe pod płytą i w gruncie (PVC-U SN8) — linia kreskowa
	rura spustowa (pion deszczowy)		odwodnienie liniowe (korytko z rusztem) wg działka.yaml

WYNIKI OBLICZEŃ — ODWODNIENIE DACHÓW (PN-EN 12056-3)

Pole	Typ	A [m²]	Q [l/s]	wpustów	Q_wp [l/s]	Q_przel. [l/s]	h_spiętrz. [cm]
D1	plaski	87.4	4.02	2	9.00	33.62	3.9
D2	plaski	12.5	0.58	1	4.50	8.02	2.2
D3	plaski	11.2	0.52	1	4.50	8.02	2.0
D4	zielony	59.1	2.72	2	9.00	14.56	3.9

OBJAŚNIENIA I UWAGI

- Wymiary w cm (mm w indeksie górnym, np. 24^ø = 24,5 cm), rzędne w m względem ±0,000 = 101,650 m n.p.m. (PL-EVRF2007-NH).
- Rysunki instalacji na podkładzie rzutów architektury (PB-AR); podkład — linie cienkie szare (warstwy I-PODKLAD²).
- Odwodnienie dachów wg PN-EN 12056-3 i WT § 28, § 29; natężenie deszczu wg modelu PANDA (IMGW) — lamela.obliczenia.sanitarne.deszczowa; wody opadowe zagospodarowane na działce (zbiornik retencyjny + niecka chłonna), bez odprowadzania do kanalizacji sanitarnej.
- Wpusty dachowe z grzałką (podgrzewane), z kolierzem do membrany/papy i koszem liściowym; przelewy awaryjne w atykach — dno przelewu powyżej poziomu pokrycia przy wpuscie (odpływ normalny przez wpusty).
- Rury spustowe wewnętrzne w izolacji termicznej i akustycznej (otulina ≥ 20 mm); przejścia przez stropy z uszczelnieniem ppoż. wg klasy stropu.
- Dachy: A = 291,8 m², Q = 13,42 l/s; zbiornik 5,0 m³, niecka 23,0 m³.
- SPRAWDZENIE NIESPEŁNIONE (obliczenia): Pole D1: dno przelewu nad pokryciem (odpływ normalny przez wpusty) — -0,046 >= 0,030 m ([ZAL] ≥ 3 cm) — do korekty w modelu.
- SPRAWDZENIE NIESPEŁNIONE (obliczenia): Pole D1: dno przelewu nad pokryciem (odpływ normalny przez wpusty) — -0,006 >= 0,030 m ([ZAL] ≥ 3 cm) — do korekty w modelu.
- SPRAWDZENIE NIESPEŁNIONE (obliczenia): Pole D1: dno przelewu nad pokryciem (odpływ normalny przez wpusty) — -0,006 >= 0,030 m ([ZAL] ≥ 3 cm) — do korekty w modelu.
- Rysunek wygenerowany automatycznie z modelu /home/user/aihouse/model/budynek.yaml (wersja 1.0, 2026-09-25) — generatory lamela.views.

1 0 1 2 3 4 5 m
PODZIAŁKA 1:50

REW.	OPIS ZMIANY	DATA
0	Wydanie — rysunek wygenerowany z modelu	2026-09-25
PRACOWNIA PROJEKTOWA PRACOWNIA PROJEKTOWA — nazwa do uzupełnienia adres pracowni do uzupełnienia	STADIUM PT	BRANŻA INSTALACJE SANITARNE (IS)
INWESTOR (do uzupełnienia)	OBIEKT / NAZWA ZAMIERZENIA BUDOWLANEGO Budynek mieszkalny jednorodzinny wolnostojący „Dom LAMELA”	
ADRES / LOKALIZACJA (NR DZIAŁKI, OBRĘB, JEDN. EWIDENCYJNA) ul. Lipowa (fikcyjna), dz. nr ewid. 123/4, obręb 0005 Przykładowo, gm. Przykładowo (fikcyjna)		KAT. OBIEKTU I
FUNKCJA	IMIĘ I NAZWISKO	SPECJALNOŚĆ, NR UPRAWNIEN
Projektant		DATA
Projektant (wsp.)		PODPIS
Sprawdzający		
Opracował		
TYTUŁ RYSUNKU ODWODNIENIE DACHÓW — RZUT PARTERU (RURY SPUSTOWE)		
SKALA 1:50	FORMAT A3×3	DATA WYDANIA 2026-09-25
RODZAJ DOK. rzut instalacji	NR RYSUNKU PT-IS-08	ARKUSZ 8/17
REW. 0		