


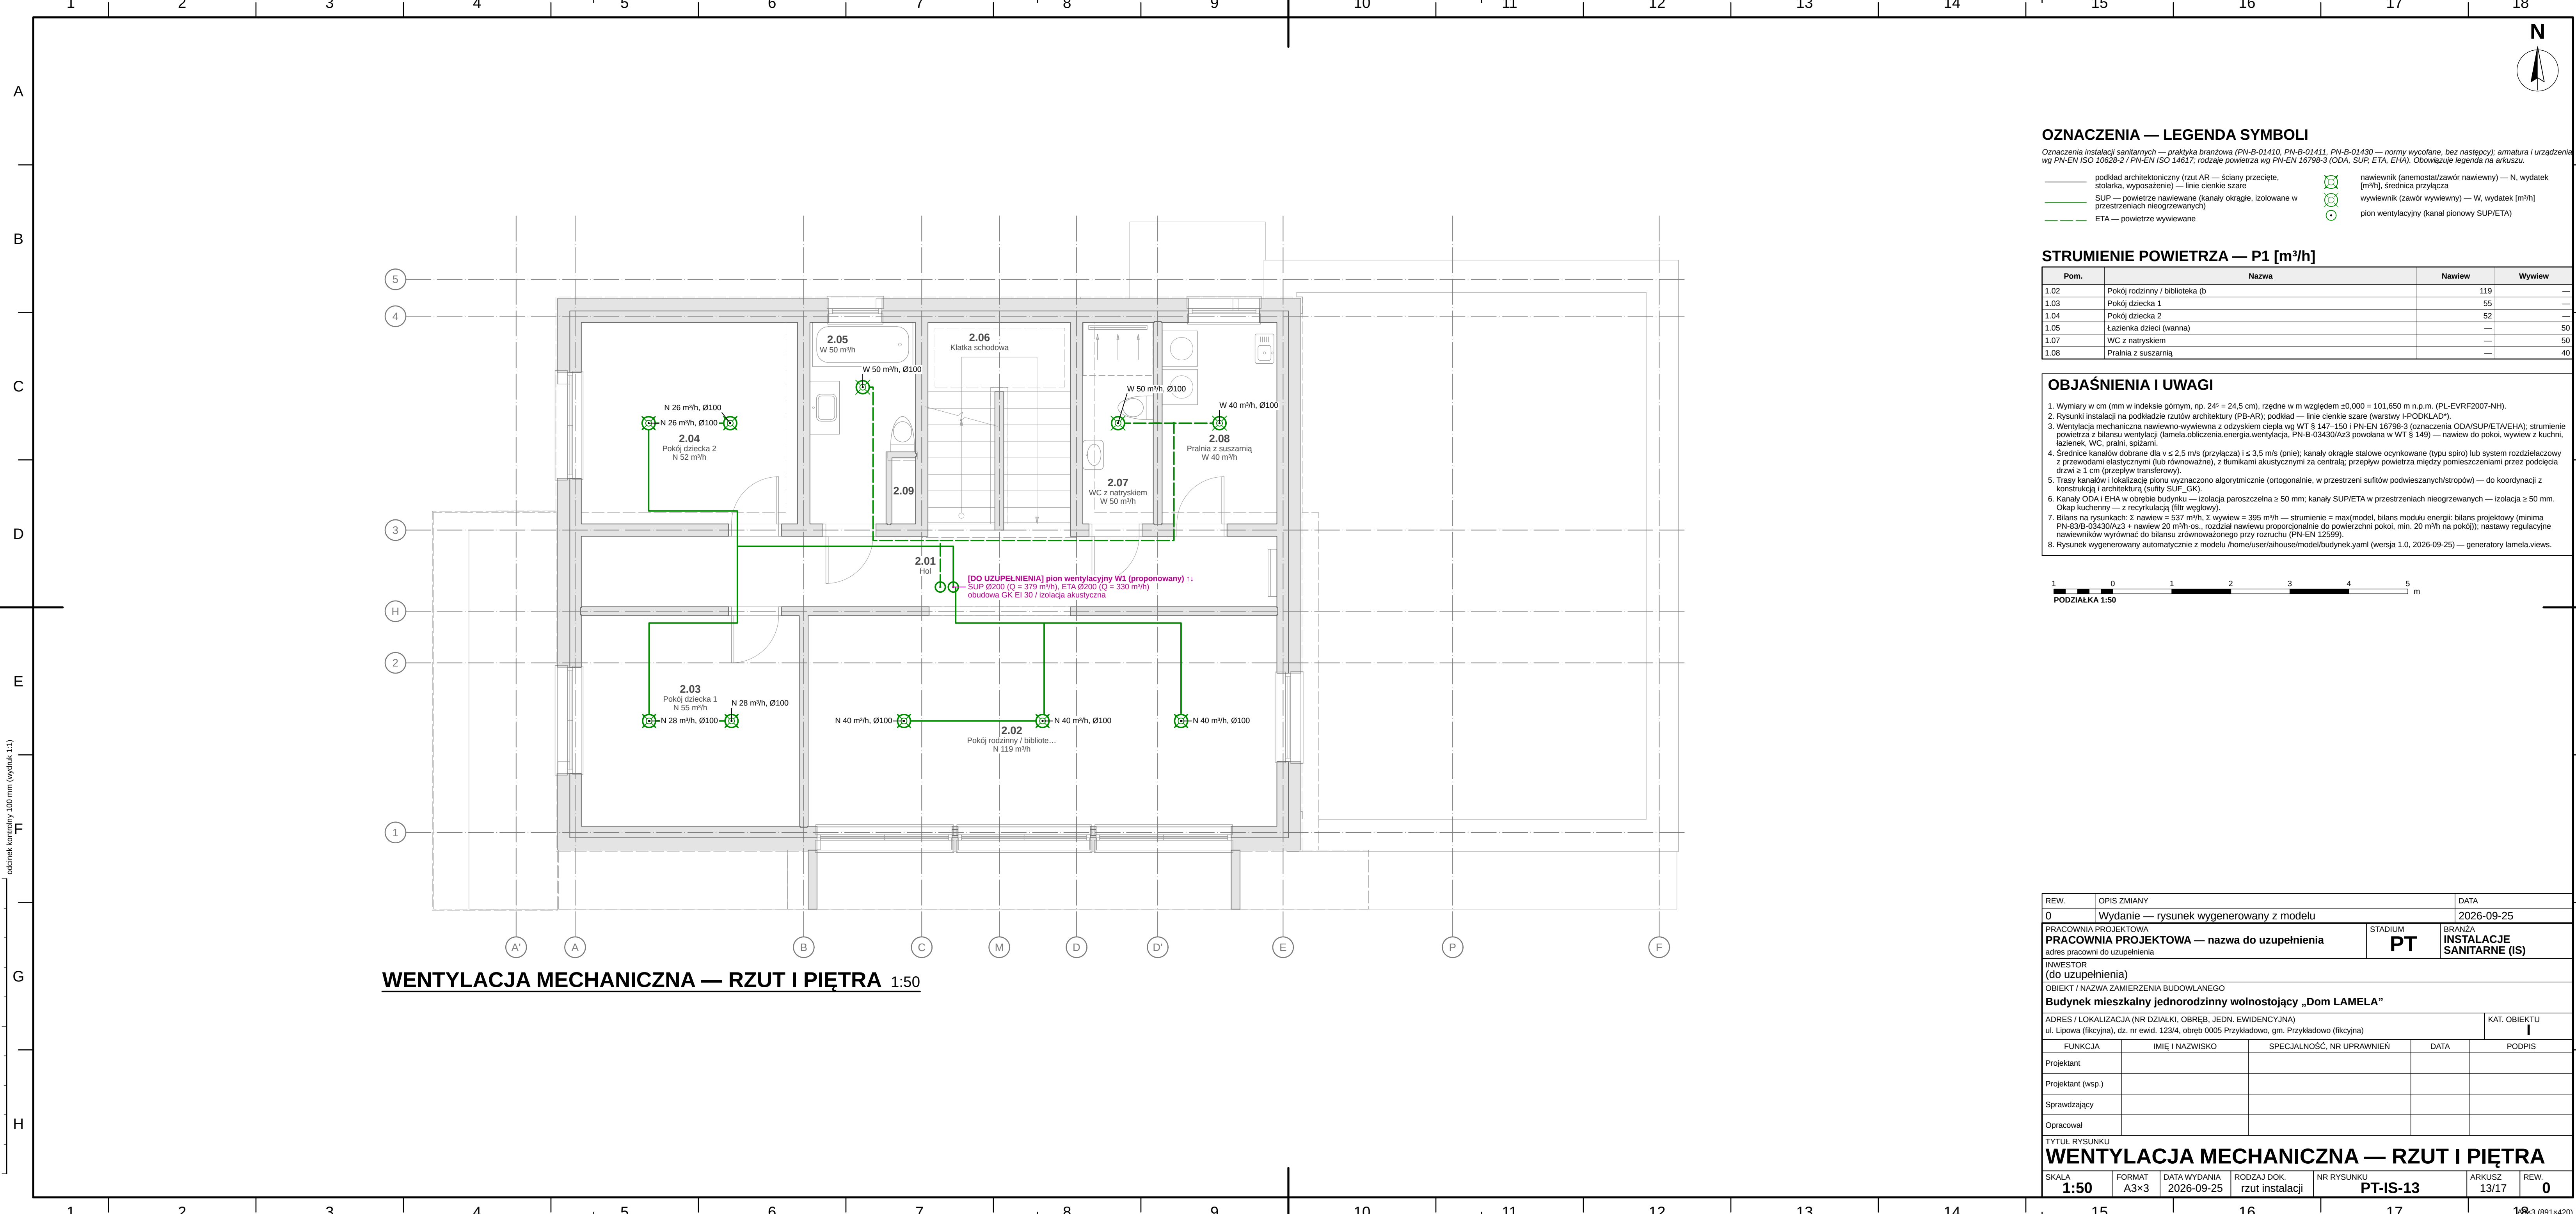

WENTYLACJA MECHANICZNA — RZUT I PIĘTRA 1:50

OZNACZENIA — LEGENDA SYMBOLI

Oznaczenia instalacji sanitarnych — praktyka branżowa (PN-B-01410, PN-B-01411, PN-B-01430 — normy wycofane, bez następcy); armatura i urządzenia wg PN-EN ISO 10628-2 / PN-EN ISO 14617; rodzaje powietrza wg PN-EN 16798-3 (ODA, SUP, ETA, EHA). Obowiązuje legenda na arkuszu.


—	podkład architektoniczny (rzut AR — ściany przecięte, stolarka, wyposażenie) — linie cienkie szare	⊗	nawiewnik (anemostat/zawór nawiewny) — N, wydatek (m³/h), średnica przyłącza
—	SUP — powietrze nawiewane (kanały okrągłe, izolowane w przestrzeniach nieogrzewanych)	⊙	wywiewnik (zawór wywiewny) — W, wydatek (m³/h)
—	ETA — powietrze wywiewane	⊖	pion wentylacyjny (kanał pionowy SUP/ETA)

STRUMIENIE POWIETRZA — P1 [m³/h]

Pom.	Nazwa	Nawiew	Wywiew
1.02	Pokój rodzinny / biblioteka (b)	119	—
1.03	Pokój dziecka 1	55	—
1.04	Pokój dziecka 2	52	—
1.05	Łazienka dzieci (wanna)	—	50
1.07	WC z natryskiem	—	50
1.08	Pralnia z suszarnią	—	40

OBJAŚNIENIA I UWAGI

- Wymiary w cm (mm w indeksie górnym, np. 24⁴ = 24,5 cm), rzędne w m względem ±0,000 = 101,650 m n.p.m. (PL-EVRF2007-NH).
- Rysunki instalacji na podkładzie rzutów architektury (PB-AR); podkład — linie cienkie szare (warstwy I-PODKŁAD).
- Wentylacja mechaniczna nawiewno-wywiewna z odzyskiem ciepła wg WT § 147–150 i PN-EN 16798-3 (oznaczenia ODA/SUP/ETA/EHA); strumienie powietrza z bilansu wentylacji (lamela.obliczenia.energia.wentylacja, PN-B-03430/Az3 powołana w WT § 149) — nawiew do pokoi, wywiew z kuchni, łazienek, WC, pralni, sypialni.
- Średnice kanałów dobrane dla $v \leq 2,5$ m/s (przyłącza) i $v \leq 3,5$ m/s (pnie); kanały okrągłe stalowe ocynkowane (typu spiro) lub system rozdzielaczy z przewodami elastycznymi (lub równoważne), z tłumikami akustycznymi za centralą; przepływ powietrza między pomieszczeniami przez podcięcia drzwi ≥ 1 cm (przepływ transferowy).
- Trasy kanałów i lokalizację pionu wyznaczono algorytmicznie (ortogonalnie, w przestrzeni sufitów podwieszanych/stropów) — do koordynacji z konstrukcją i architekturą (suffity SUP, GK).
- Kanały ODA i EHA w obrębie budynku — izolacja paroszczelna ≥ 50 mm; kanały SUP/ETA w przestrzeniach nieogrzewanych — izolacja ≥ 50 mm. Okap kuchenny — z recyrkulacją (filtr węglowy).
- Bilans na rysunkach: Σ nawiew = 537 m³/h, Σ wywiew = 395 m³/h — strumienie = max(model, bilans modułu energii; bilans projektowy (minima PN-B3/B-03430/Az3 + nawiew 20 m³/h os., rozdział nawiewu proporcjonalnie do powierzchni pokoi, min. 20 m³/h na pokój)); nastawy regulacyjne nawiewników wyrownać do bilansu zrównoważonego przy rozruchu (PN-EN 12599).
- Rysunek wygenerowany automatycznie z modelu /home/user/aihouse/model/budynek.yaml (wersja 1.0, 2026-09-25) — generatory lamela.views.

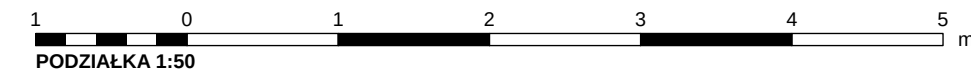

REW.	OPIS ZMIANY	DATA
0	Wydanie — rysunek wygenerowany z modelu	2026-09-25
PRACOWNIA PROJEKTOWA PRACOWNIA PROJEKTOWA — nazwa do uzupełnienia	STADIUM PT	BRANZA INSTALACJE SANITARNE (IS)
INWESTOR (do uzupełnienia)	OBIEKT / NAZWA ZAMIERZENIA BUDOWLANEGO Budynek mieszkalny jednorodzinny wolnostojący „Dom LAMELA”	
ADRES / LOKALIZACJA (NR DZIAŁKI, OBRĘB, JEDN. EWIDENCYJNA) ul. Lipowa (fikcyjna), dz. nr ewid. 123/4, obręb 0005 Przykładowo, gm. Przykładowo (fikcyjna)	KAT. OBIEKTU I	
FUNKCJA	IMIĘ I NAZWISKO	SPECJALNOŚĆ, NR UPRAWNIEN
Projektant		DATA
Projektant (wsp.)		PODPIS
Sprawdzający		
Opracował		
TYTUŁ RYSUNKU WENTYLACJA MECHANICZNA — RZUT I PIĘTRA		
SKALA 1:50	FORMAT A3×3	DATA WYDANIA 2026-09-25
RODZAJ DOK. rzut instalacji	NR RYSUNKU PT-IS-13	ARKUSZ 13/17
REW. 0		