


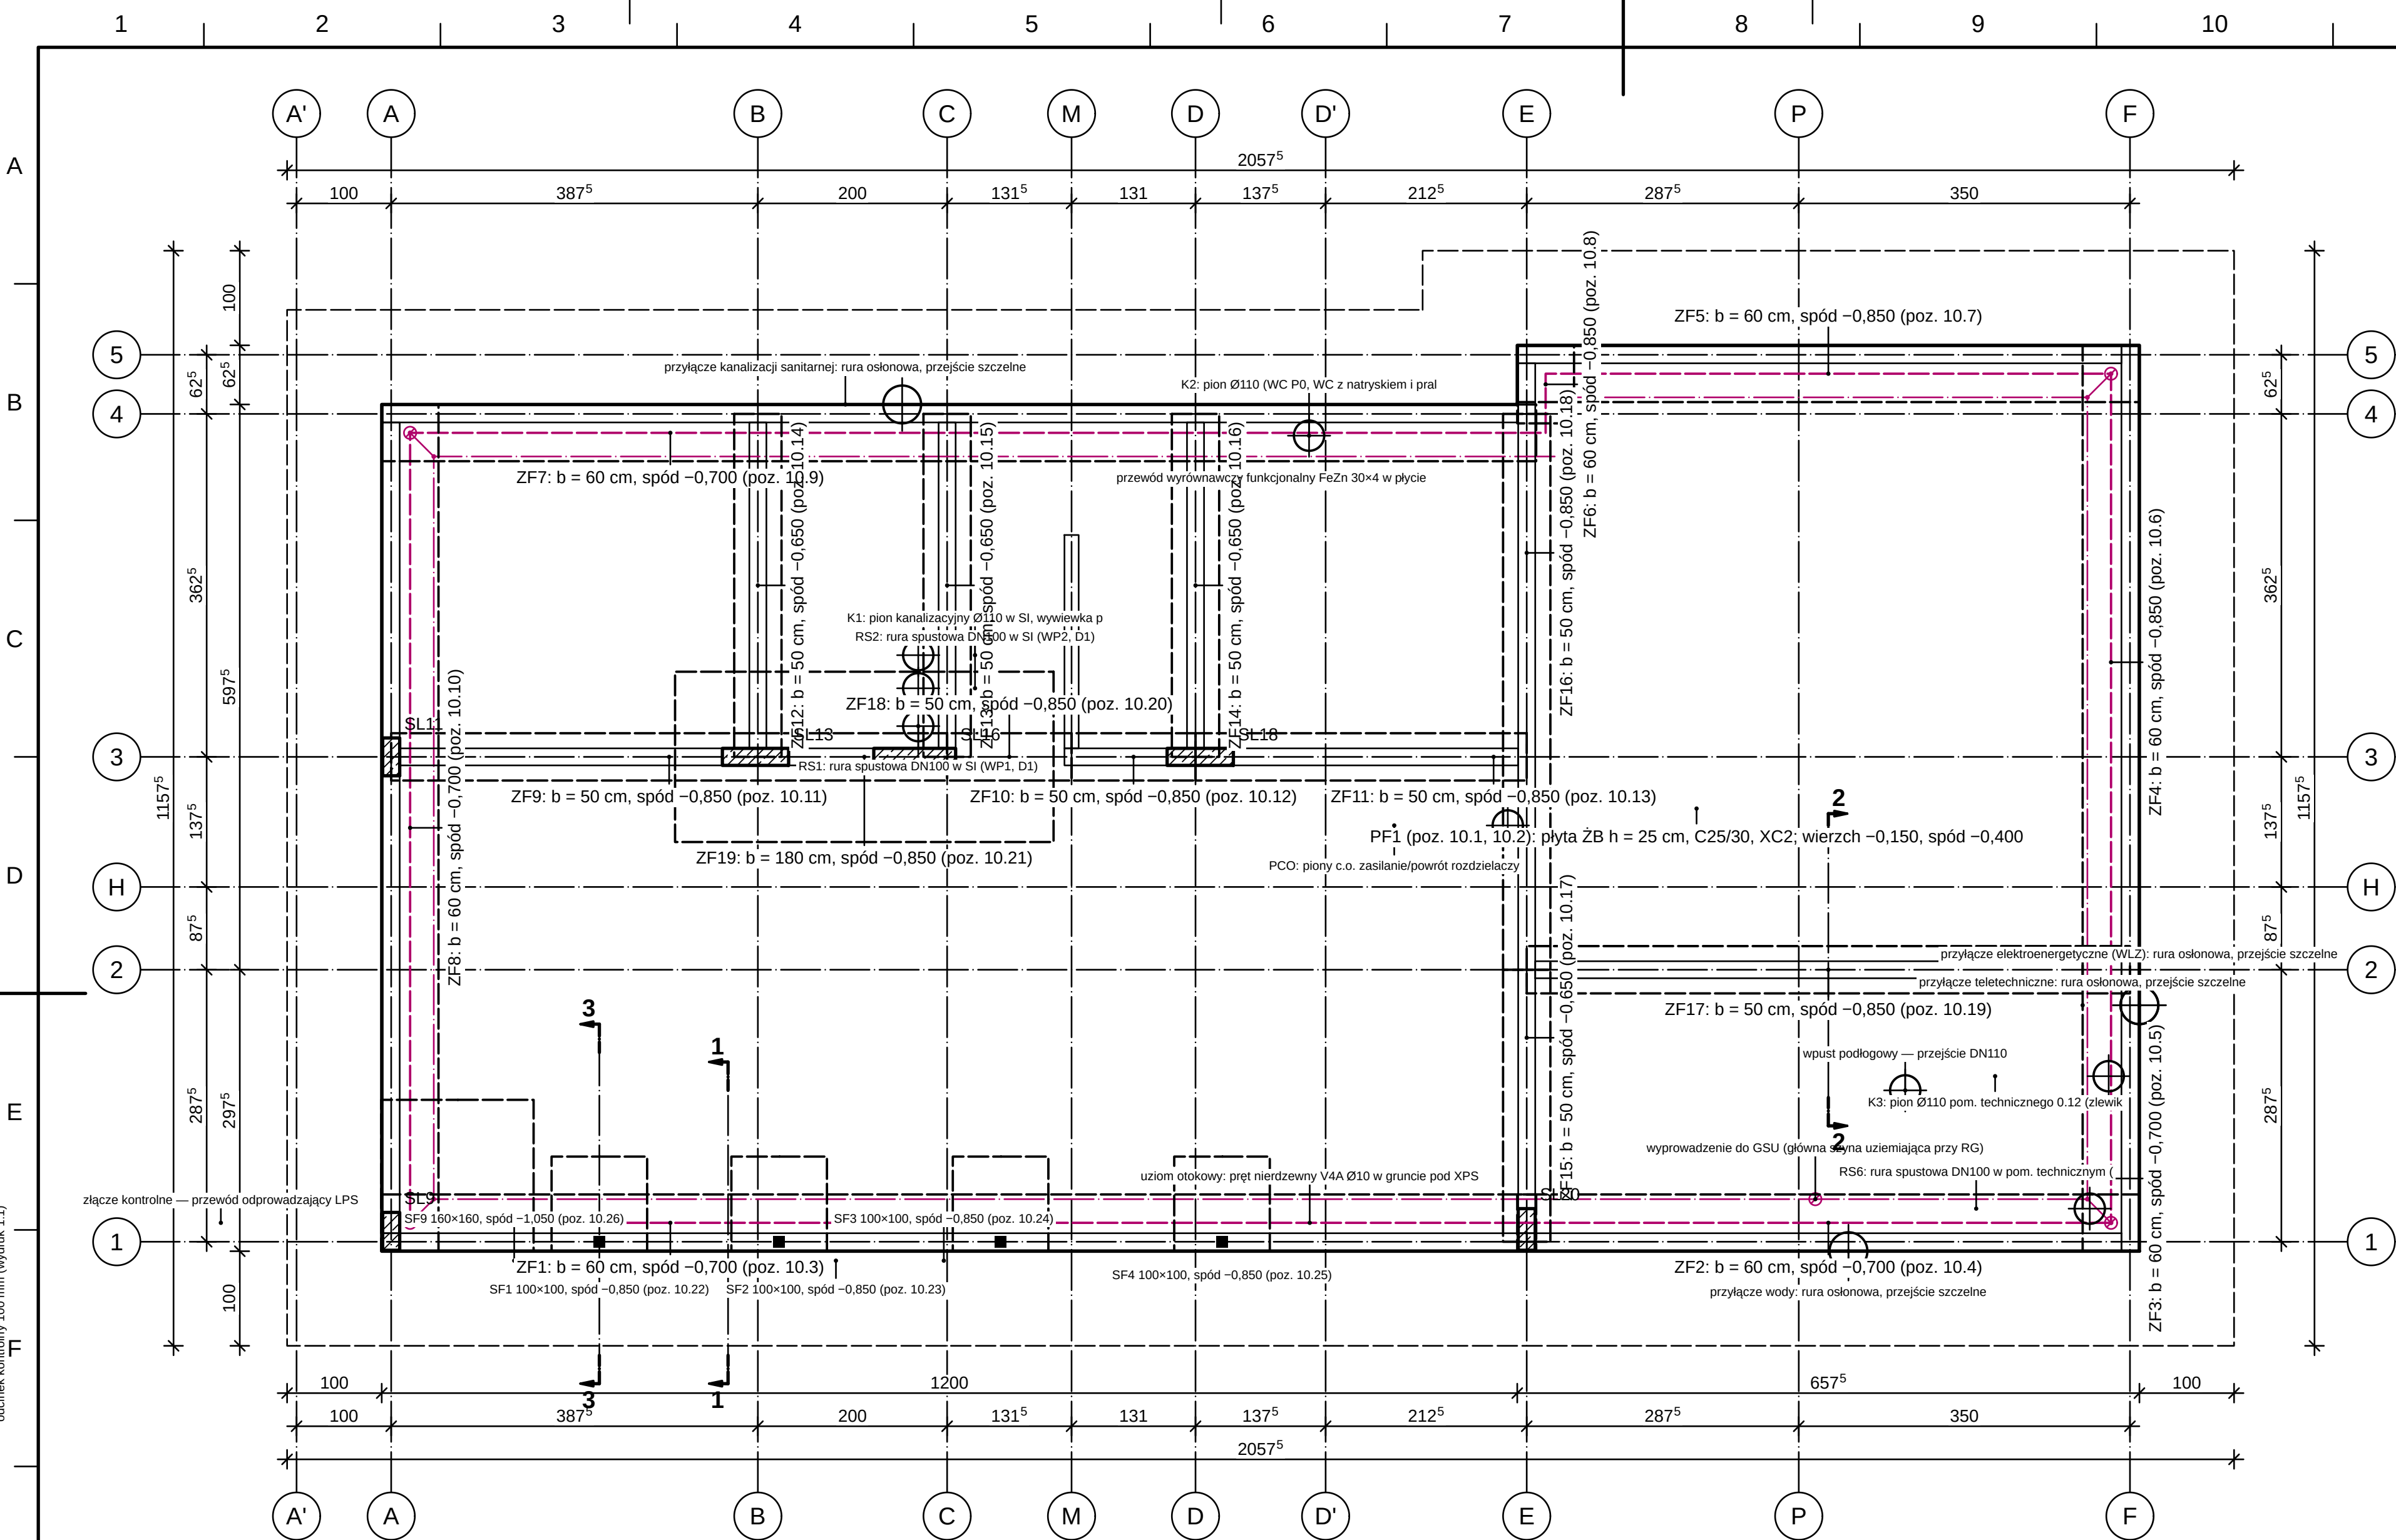

OBJAŚNIENIA I UWAGI

- Wymiary w cm (mm w indeksie górnym, np. 24⁵ = 24,5 cm), rzędne w m względem ±0,000 = 101,650 m n.p.m. (PL-EVRF2007-NH).
- Uziom fundamentowy (PN-HD 60364-5-54 p. 542.2.3, PN-EN 62305-3 p. 5.4.2.2 i E.5.4.3.2; praktyka DIN 18014): płyta na XPS jest odizolowana od gruntu — uziom otokowy ze stali nierdzewnej V4A (1.4571) Ø10 mm lub 30x3,5 mm ułożyć w gruncie POD warstwą XPS wzdłuż zeber obwodowych (obwód ≈ 53,9 m); w płycie przewód wyrównawczy funkcjonalny FeZn 30x4 (lub Ø10) połączony ze zbrojeniem co ≤ 2 m (zaciski), oczka ≤ 20 × 20 mm; połączenia otoku z przewodem wyrównawczym (stal nierdzewna przez izolację, szczelnie) w 4 narożach (odstęp po obwodzie ≤ 20 mm); wyprowadzenia (V4A, min. 1,5 m zapasu) do GSU i złączy kontrolnych LPS (jeżeli LPS wymagały wg analizy ryzyka PN-EN 62305-2). Połączenia — zaciski wg PN-EN 62561-1; pomiar ciągłości i rezystancji przed betonowaniem (protokół). Trasa i wyprowadzenia do uzgodnienia z branżą E.
- Posadowienie bezpośrednie — posadowienie bezpośrednie na piaskach średnich (I_D = 0,6), niewysadzinowych; ZWG = 3,8 m p.p.t. — drenaż opaskowy zbędny (W-285); zdjęcie humusu 0,4 m, podsypka zagęszczona; uziom otokowy w gruncie pod XPS (W-286/W-187) Kategoria geotechniczna II; grunt: piasek średni (MSA), średniozagęszczony, ϕ' = 33°, γ = 18,5 kN/m³, M₀ = 80000 kPa; ZWG ~3,800, h_z = 0,8 m (PN-EN 1997-1 + NA; dane wg modelu — do potwierdzenia dokumentacją badań podłoża).



OBJAŚNIENIA I UWAGI (cd.)

- Beton fundamentu: C25/30 XC2 c_{nom} 35 mm (50 mm od gruntu); otulina: wierzch 35 mm, spód i czola (na XPS/podsypce) 50 mm (PN-EN 1992-1-1 4.4.1.3(4) + NA). Stal B500SP. Zbrojenie — arkusz zbrojenia płyty fundamentowej.
- Izolacja obwodowa przeciwprzemarzaniowa: izolacja przeciwprzemarzaniowa XPS 10 cm × 1,00 m (garaż 1,20 m) wokół płyty, spadek 2 % od budynku — typ pozioma, szerokość D = 1,00 m, grubość d_n = 10 cm (XPS300), głębokość 0,45 m p.p.t. — PN-EN ISO 13793 (zastępuje wymaganie posadowienia poniżej h_z; uzasadnienie — obliczenia wg normy dla strefy klimatycznej lokalizacji).
- Przebiegi instalacyjne (12) wykonać w tulejach ochronnych (rury osłonowe PVC/PE osadzone przed betonowaniem), szczelnie w warstwie przeciwwilgociowej/przeciwradonowej (kolnierze systemowe), położenie wg projektów branż S i E — koordynacja przed betonowaniem.
- Rysunek wygenerowany automatycznie z modelu model/budynek.yaml (wersja 1.0, 2026-09-25) — generatory lamela.views.

RZUT FUNDAMENTÓW 1:50

OZNACZENIA NA RYSUNKU

- — — żebra / pogrubienia płyty (pod płytą — widok zasłonięty)
- - - - - zasieg izolacji obwodowej przeciwprzemarzaniowej XPS (PN-EN ISO 13793)
- — — uziom otokowy — w gruncie pod warstwą XPS
- — — przewód wyrównawczy funkcjonalny w płycie (połączony ze zbrojeniem)
- ⊗ wyprowadzenie uziomu / złącze kontrolne (punkt stały uziemienia)
- ⊕ przejście instalacyjne przez płytę (tuleja ochronna, szczelne)
- słup stalowy (baza na pogrubieniu płyty)

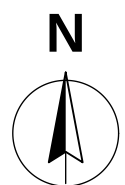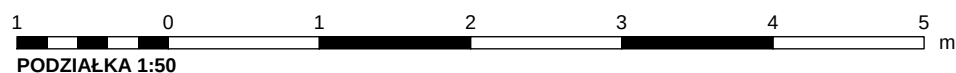

REW.	OPIS ZMIANY		DATA			
0	Wydanie — rysunek wygenerowany z modelu		2026-09-25			
PRACOWNIA PROJEKTOWA PRACOWNIA PROJEKTOWA — nazwa do uzupełnienia adres pracowni do uzupełnienia		STADIUM PT	BRANŻA KONSTRUKCJA (BO)			
INWESTOR (do uzupełnienia)						
OBIEKT / NAZWA ZAMIERZENIA BUDOWLANEGO Budynek mieszkalny jednorodzinny wolnostojący „Dom LAMELA”						
ADRES / LOKALIZACJA (NR DZIAŁKI, OBRĘB, JEDN. EWIDENCYJNA) ul. Lipowa (fikcyjna), dz. nr ewid. 123/4, obręb 0005 Przykładowo, gm. Przykładowo (fikcyjna)			KAT. OBIEKTU I			
FUNKCJA	IMIĘ I NAZWISKO	SPECJALNOŚĆ, NR UPRAWNIEN	DATA	PODPIS		
Projektant	[DO UZUPEŁNIENIA]	[DO UZUPEŁNIENIA]				
Projektant (wsp.)	[DO UZUPEŁNIENIA]	[DO UZUPEŁNIENIA]				
Sprawdzający	nie dotyczy (art. 20 ust. 3 pkt 2 PB)	—				
Opracował	[DO UZUPEŁNIENIA]	[DO UZUPEŁNIENIA]				
TYTUŁ RYSUNKU RZUT FUNDAMENTÓW						
SKALA 1:50	FORMAT 710×420	DATA WYDANIA 2026-09-25	RODZAJ DOK. rzut fundamentów	NR RYSUNKU PT-BO-01	ARKUSZ 1/27	REW. 0