


OZNACZENIA — LEGENDA SYMBOLI

Symbole instalacji elektrycznych wg IEC 60617 (baza IEC; PN-EN 60617 — wycofana, stosowana jako praktyka branżowa) i PN-EN ISO 14617; oznaczenia teletechniczne — praktyka branżowa. Obowiązuje legenda na arkuszu.

- podkład architektoniczny (rzut AR — ściany przecięte, stolarka, wyposażenie) — linie cienkie szare
- okablowanie strukturalne: skrętka kat. 6A U/FTP (LAN), koncentryk (TV/SAT), przewody SSWIN i wideodomofonu — w rurach osłonowych, gwiazdziście od RACK


OBJAŚNIENIA I UWAGI

- Średnice przewodów w mm (d_zxs — rury wielowarstwowe, Ø/DN — kanalizacja, kanały wentylacyjne), przekroje żył w mm², odległości i rzędne w m; ±0,000 = 101,650 m n.p.m. (PL-EVRF2007-NH).
- Rysunki instalacji na podkładzie rzutów architektury (PB-AR); podkład — linie cienkie szare (warstwy I-PODKŁAD*).
- Instalacje telekomunikacyjne wg WT § 192a–192c (instalacja telekomunikacyjna budynku, przyłącze światłowodowe — art. 10 ustawy o wspieraniu rozwoju usług i sieci telekomunikacyjnych), PN-EN 50173-4 (okablowanie strukturalne w domach), PN-EN 50174-2 (instalowanie), SSWIN wg PN-EN 50131-1 (stopień 2).
- Punkty teleinformatyczne rozmieszczono algorytmicznie: przy biurkach 2×RJ45, na ścianie naprzeciw łóżek i sofy (TV + RJ45), AP Wi-Fi w komunikacji każdej kondygnacji; czujki ruchu w pomieszczeniach parteru z oknami/drzwiami zewnętrznymi. Okablowanie gwiazdźiste do RACK — trasy schematyczne.
- Przewody teletechniczne prowadzić w odległości ≥ 0,1 m od przewodów elektroenergetycznych (lub z przegrodą), w rurach osłonowych Ø20–Ø32, ekranowanie wg PN-EN 50174-2.
- Rysunek wygenerowany automatycznie z modelu model/budynek.yaml (wersja 1.0, 2026-09-25) — generatory lamela.views.

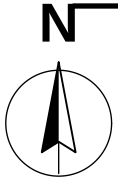

REW.	OPIS ZMIANY			DATA	
0	Wydanie — rysunek wygenerowany z modelu			2026-09-25	
PRACOWNIA PROJEKTOWA PRACOWNIA PROJEKTOWA — nazwa do uzupełnienia adres pracowni do uzupełnienia			STADIUM PT	BRANŻA INSTALACJE ELEKTRYCZNE (IE)	
INWESTOR (do uzupełnienia)					
OBIEKT / NAZWA ZAMIERZENIA BUDOWLANEGO Budynek mieszkalny jednorodzinny wolnostojący „Dom LAMELA”					
ADRES / LOKALIZACJA (NR DZIAŁKI, OBRĘB, JEDN. EWIDENCYJNA) ul. Lipowa (fikcyjna), dz. nr ewid. 123/4, obręb 0005 Przykładowo, gm. Przykładowo (fikcyjna)				KAT. OBIEKTU I	
FUNKCJA	IMIĘ I NAZWISKO	SPECJALNOŚĆ, NR UPRAWNIEŃ	DATA	PODPIS	
Projektant	[DO UZUPEŁNIENIA]	[DO UZUPEŁNIENIA]			
Projektant (wsp.)	[DO UZUPEŁNIENIA]	[DO UZUPEŁNIENIA]			
Sprawdzający	nie dotyczy (art. 20 ust. 3 pkt 2 PB)	—			
Opracował	[DO UZUPEŁNIENIA]	[DO UZUPEŁNIENIA]			
TYTUŁ RYSUNKU TELETECHNIKA — RZUT II PIĘTRA					
SKALA 1:50	FORMAT 570×297	DATA WYDANIA 2026-09-25	RODZAJ DOK. rzut instalacji	NR RYSUNKU PT-IE-09	ARKUSZ 9/14
					REW. 0

odcinek kontrolny 100 mm (wydruk 1:1)

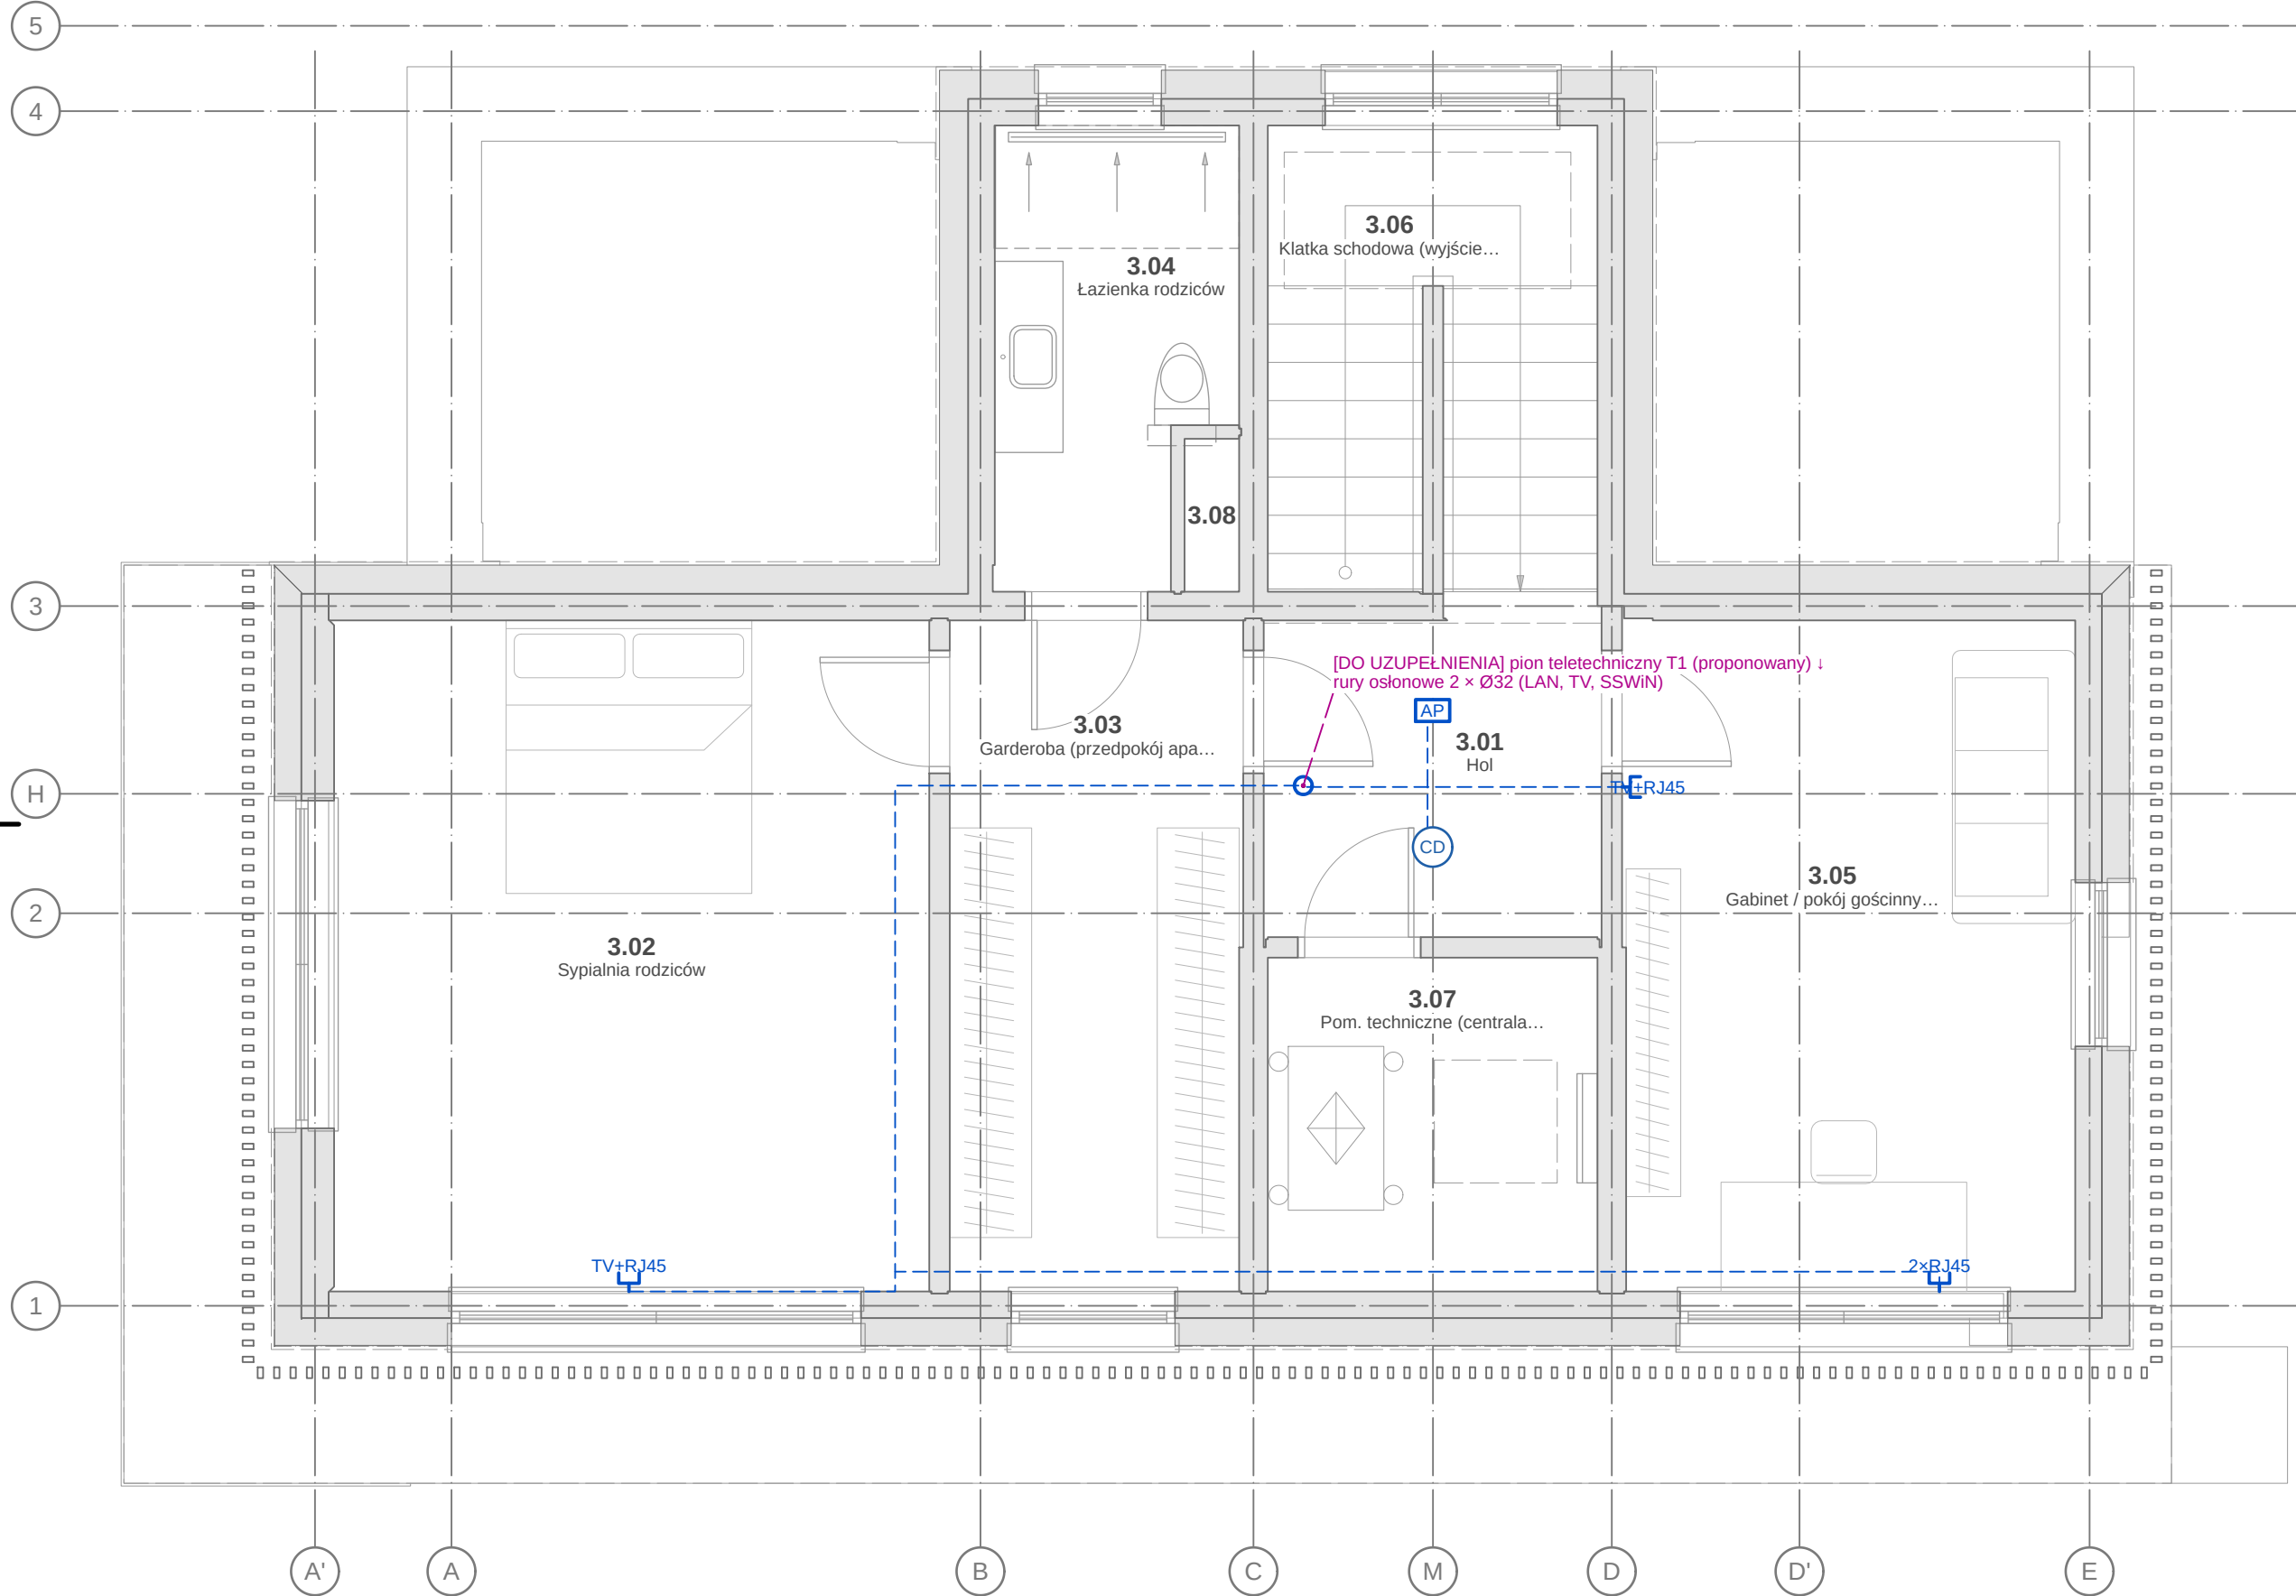

TELETECHNIKA — RZUT II PIĘTRA 1:50