

RZUT PARTERU 1:50

ZESTAWIENIE POMIESZCZEŃ

Nr	Nazwa pomieszczenia	Posadzka	Kat.	Wys. [m]	Pow. [m²]
1.06	Salon + jadalnia + kuchnia	Deska warstwowa dębowa 15 mm, klejona	podst.	2,77	54,44
1.13	Garaż 2-stanowiskowy	Posadzka żywiczna epoksydowa antypoślizgowa R11 (garaż)	pomoc.	2,76	37,42
1.10	Pokój gościnny / gabinet	Deska warstwowa dębowa 15 mm, klejona	podst.	2,77	12,52
1.12	Pomieszczenie techniczne	Płytki gresowe 60×120 na kleju C2TE S1	techn.	2,76	8,85
1.11	Przedśionek gospodarczy	Płytki gresowe 60×120 na kleju C2TE S1	ruchu	2,76	7,18
1.02	Hol	Płytki gresowe 60×120 na kleju C2TE S1	ruchu	2,77	4,44
1.01	Wiatrołap	Płytki gresowe 60×120 na kleju C2TE S1	ruchu	2,77	3,89
1.09	Łazienka gościnna (natrysk)	Płytki gresowe 60×120 na kleju C2TE S1	pomoc.	2,77	3,84
1.07	Pas komunikacyjny przy schodach	Deska warstwowa dębowa 15 mm, klejona	ruchu	2,77	3,51
1.16	Schowek pod spocznikiem (h < 1,40)	Płytki gresowe 60×120 na kleju C2TE S1	pomoc.	1,37	2,91
1.04	Klatka schodowa	Deska warstwowa dębowa 15 mm, klejona	ruchu	2,77	2,78
1.03	WC gościnne	Płytki gresowe 60×120 na kleju C2TE S1	pomoc.	2,77	2,32
1.15	Schowek pod schodami (h 1,40–2,20)	Płytki gresowe 60×120 na kleju C2TE S1	pomoc.	1,80	1,45
1.08	Przedpokój gościnny	Deska warstwowa dębowa 15 mm, klejona	ruchu	2,77	1,44
1.05	Spizarnia	Płytki gresowe 60×120 na kleju C2TE S1	pomoc.	2,77	1,02
1.14	Szacht instalacyjny SI		techn.	2,77	0,45
RAZEM powierzchnia netto					148,45
w tym podstawowa + pomocnicza					115,91

OZNACZENIA MATERIAŁÓW (PN-B-01030 + przyjęte)



	Wełna mineralna 035 (szkielet, docieplenia, ściana dom–garaż) — meander „UUU”		Stal konstrukcyjna S355 (słupy RK, rama boksu C), cynkowana ogniowo + malowana proszkowo RAL 7016 — zaczemienie
	Styropian grafitowy EPS 031 (ETICS, NRO w systemie) — sygnak „VVV”		Szklanka szklana VSG 2 × 8 mm w ramie aluminiowej (wiatrołap / hol)
	Płyta gipsowa 12 cm, kl. 15 (ścianki działowe, łcowy w klatce); Błoczek wapienno-piaskowy (silikat) 18 cm, kl. 20, gr. 1, na zaprawie cienkowarstwowej — kratka ukośna 45°/135°		Żelbet C25/30, B500SP (stropy, płyta fundamentowa, ściany); Żelbet C30/37 XC4/XF1 (krawędzie płyt wysuniętych, attyki, belki) — 45° na przemian ciągle i przerywane

OZNACZENIA LINII

—	elementy nad płaszczyzną cięcia (obrys płyt, wsporników, brył wyższych kondygnacji)
—	elementy poniżej płaszczyzny cięcia (widok z góry)
- -	osie konstrukcyjne; linia punktowa z pogrubionymi końcami — ślad przekroju

OBJAŚNIENIA I UWAGI

- Wymiary w cm (mm w indeksie górnym, np. 24” = 24,5 cm), rzędne w m względem ±0,000 = 101,650 m n.p.m. (PL-EVRF2007-NH).
- Rzuty: płaszczyzna cięcia +1,10 m nad posadzką kondygnacji. Linia kreskowa — elementy nad płaszczyzną cięcia (obrys płyt i wsporników, brył wyższych kondygnacji, otwory w stropie nad, belki); linia cieniła — elementy poniżej (widok).
- Otwory, licznik — szerokość, mianownik — wysokość w świetle muru, w nawiasie wysokość parapetu; symbol stolarki wg zestawienia stolarki.
- Numeracja pomieszczeń wg PN-B-01025 / PN-EN ISO 4157-2: <nr kondygnacji (parter = 1)><nr>; identyfikator w modelu: <kond>-<nr> (parter = 0).
- Drzwi: strona otwierania (lewej/prawej) wg modelu — patrząc od strony, w którą otwiera się skrzydło.
- Rysunek wygenerowany automatycznie z modelu model/budynk.yam (wersja 1.0, 2026-09-25) — generatory lamela.views.

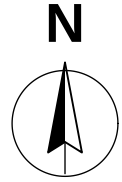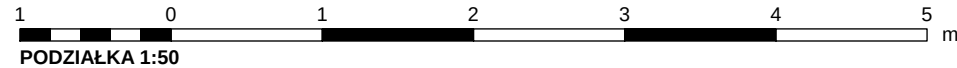

REW.	OPIS ZMIANY			DATA
0	Wydanie — rysunek wygenerowany z modelu			2026-09-25
PRACOWNIA PROJEKTOWA PRACOWNIA PROJEKTOWA — nazwa do uzupełnienia adres pracowni do uzupełnienia		STADIUM PB	BRANZA ARCHITEKTURA (AR)	
INWESTOR (do uzupełnienia)				
OBJEKT / NAZWA ZAMIERZENIA BUDOWLANEGO Budynek mieszkalny jednorodzinny wolnostojący „Dom LAMELA”				
ADRES / LOKALIZACJA (NR DZIAŁKI, OBREB, JEDN. EWIDENCYJNA) ul. Lipowa (fikcyjna), dz. nr ewid. 123/4, obręb 0005 Przykładowo, gm. Przykładowo (fikcyjna)				KAT. OBJEKTU I
FUNKCJA	IMIĘ I NAZWISKO	SPECJALNOŚĆ, NR UPRAWNIENI	DATA	PODPIS
Projektant	[DO UZUPEŁNIENIA]	[DO UZUPEŁNIENIA]		
Projektant (wsp.)	[DO UZUPEŁNIENIA]	[DO UZUPEŁNIENIA]		
Sprawdzający	nie dotyczy (art. 20 ust. 3 pkt 2 PB)	—		
Opracował	[DO UZUPEŁNIENIA]	[DO UZUPEŁNIENIA]		
TYTUŁ RYSUNKU RZUT PARTERU				
SKALA 1:50	FORMAT 620×594	DATA WYDANIA 2026-09-25	RODZAJ DOK. rzut	NR RYSUNKU PB-AR-01
ARKUSZ 1/5		REW. 0		