



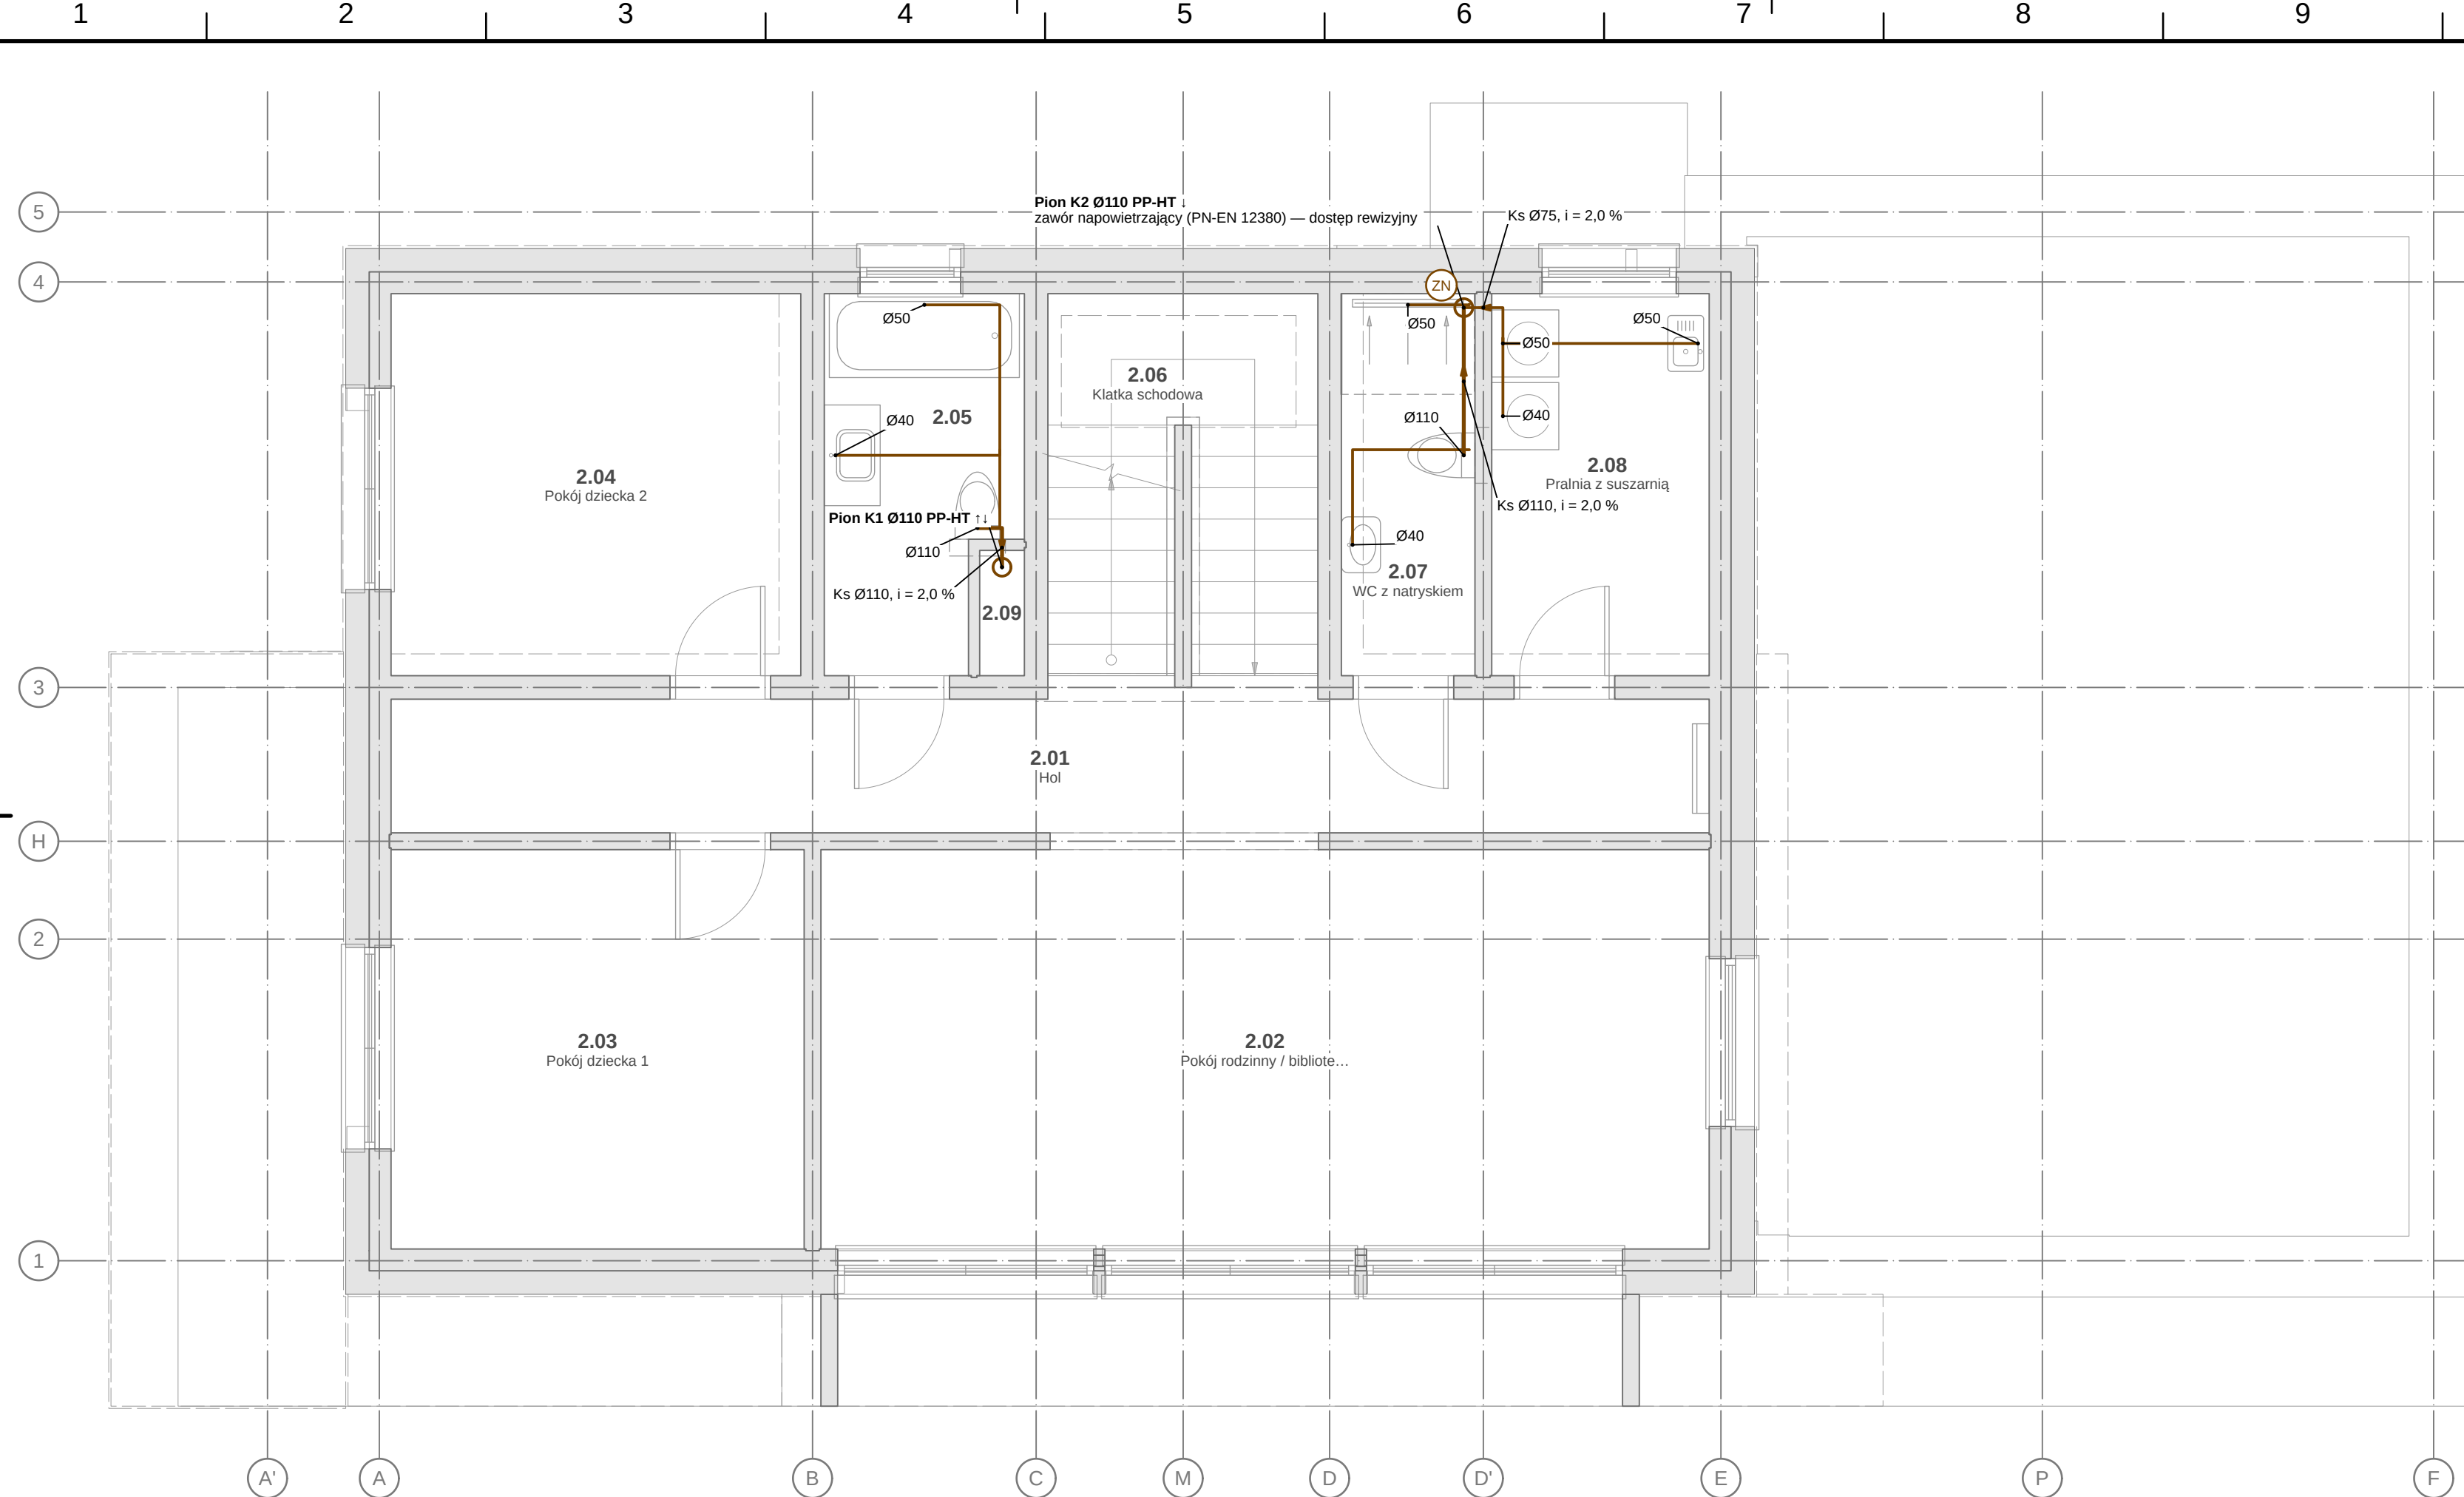

KANALIZACJA SANITARNA — RZUT I PIĘTRA 1:50

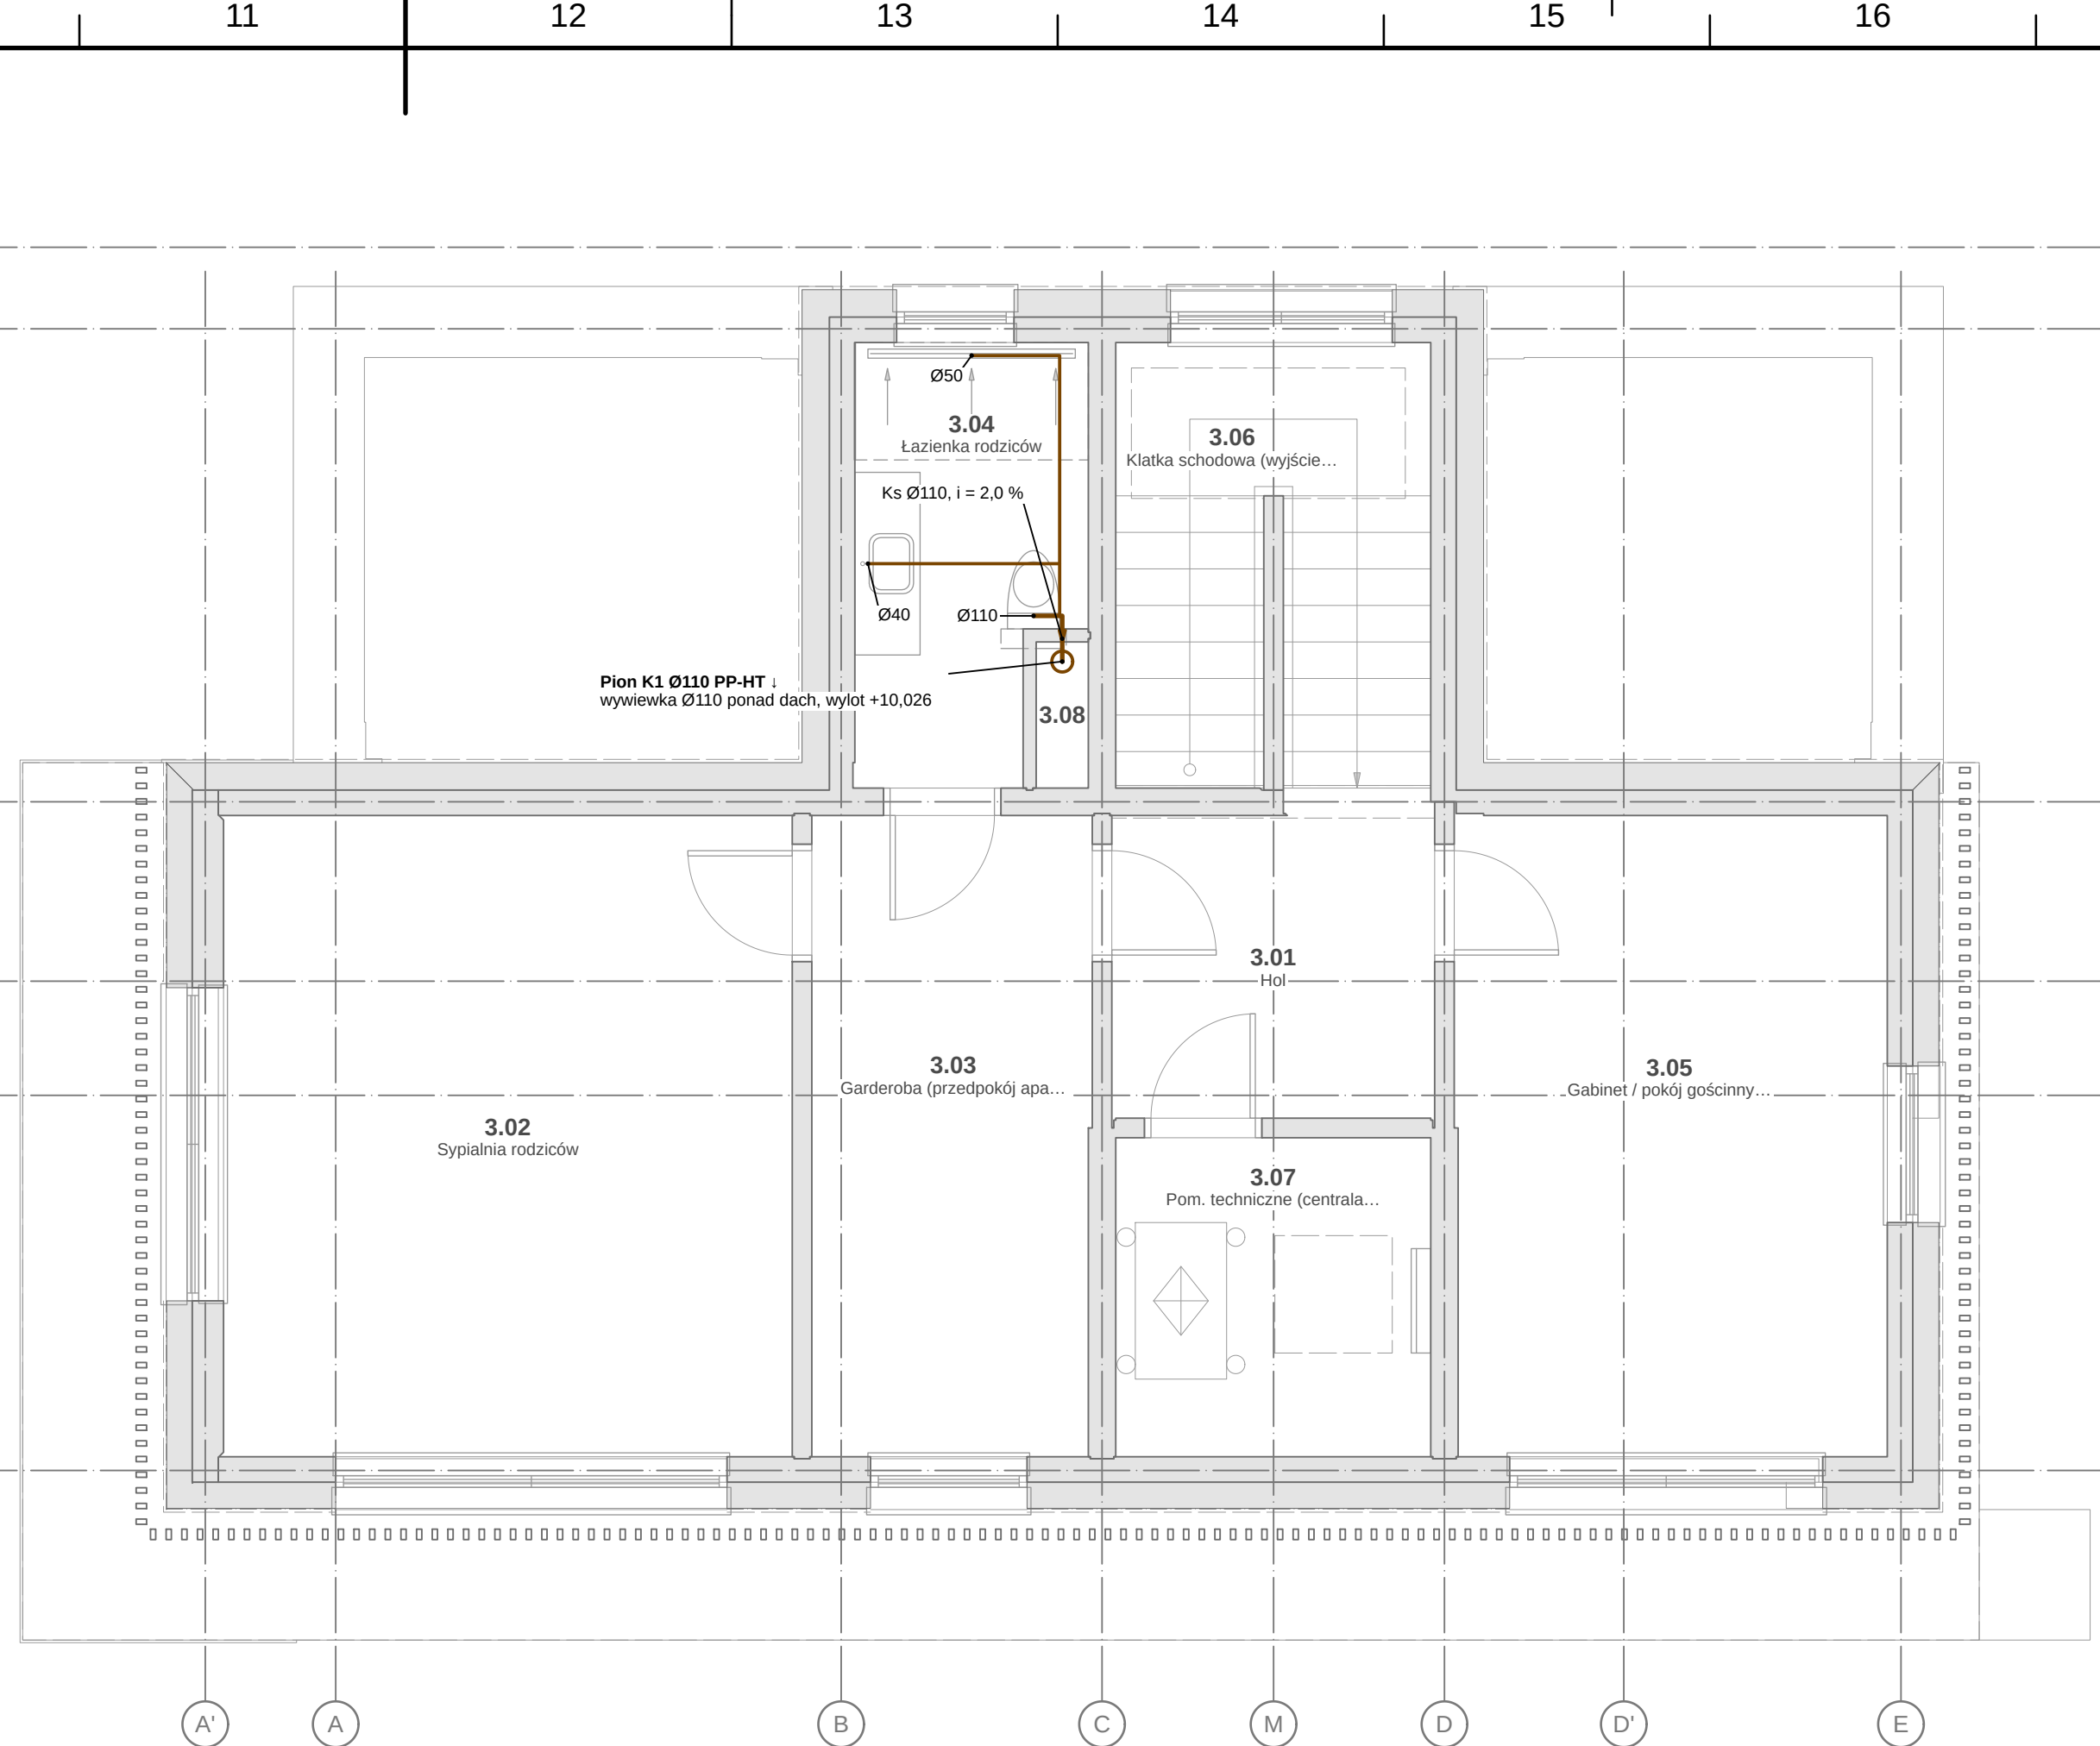

KANALIZACJA SANITARNA — RZUT II PIĘTRA 1:50


OZNACZENIA — LEGENDA SYMBOLI

Oznaczenia instalacji sanitarnych — praktyka branżowa (PN-B-01410, PN-B-01411, PN-B-01430 — normy wycofane, bez następcy); armatura i urządzenia wg PN-EN ISO 10628-2 / PN-EN ISO 14617; rodzaje powietrza wg PN-EN 16798-3 (ODA, SUP, ETA, EHA). Obowiązuje legenda na arkuszu.

- podkład architektoniczny (rzut AR) — ściany przecięte, stolarka, wyposażenie — linie cienie szare
- Ks — kanalizacja sanitarna, podejścia i piony PP-HT (PN-EN 1451-1), średnica nominalna wg obliczeń; i — spadek
- ZN — zawór napowietrzający pionu (PN-EN 12380, montaż ponad podejściami)
- pion kanalizacyjny; 1 — prowadzony wyżej, i — z kondygnacji wyższej/niższej
- kierunek przepływu (spadek przewodu)

OBJAŚNIENIA I UWAGI

- Średnice przewodów w mm (d, z x s — rury wielowarstwowe, Ø/DN — kanalizacja, kanały wentylacyjne), przekroje żył w mm², odległości i rzędne w m; ±0.000 = 101.650 m n.p.m. (PL-EVRF2007-14H).
- Rysunek instalacji na podkładzie rzutów architektury (PB-AR); podkład — linie cienie szare (warstwy I-PODKŁAD*).
- Kanalizacja sanitarna wg PN-EN 12056-1, -2 (system I), -5 i WT § 122-124; obliczenia: lamela.obliczenia.sanitarne.kanalizacja (K = 0,5; ZDU, Q_w, napełnienia, wentylacja pionów).
- Podejścia i piony: PP-HT (PN-EN 1451-1) lub równoważne; pod płytą i przykanalik: PVC-U SN8 lity (PN-EN 1401-1). Spadki podejść ≥ 2 %, przewodów pod płytą 2 % (≤ DN100).
- Trasy podejść wyznaczono algorytmicznie (ortogonalnie, przy ścianach, do pionów w szachcie SI) — średnice i spadki z obliczeń; przebieg do weryfikacji na budowie.
- Czyszczarki na pionach w najniższej kondygnacji 1,0 m nad posadzką; rewizje w studziennic SR1. Piony w szachcie izolowane akustycznie, przejścia przez stropy z opaskami/kolnierzami ppoz. wg klasy stropu.
- Odpiływ skroplin PC i zmywarki przez syfon; wpusty podłogowe z zamknięciem wodnym ≥ 50 mm.
- Rysunek wygenerowany automatycznie z modelu model/budynki.yam (wersja 1.0, 2026-09-25) — generatory lamela.views.

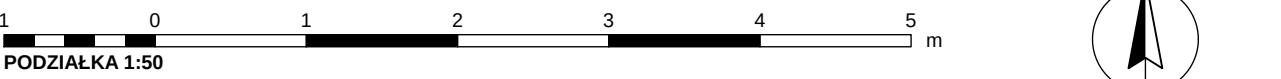

REW.			OPIS ZMIANY			DATA		
			Wydanie — rysunek wygenerowany z modelu			2026-09-25		
PRACOWNIA PROJEKTOWA			STADIUM			BRANŻA		
PRACOWNIA PROJEKTOWA — nazwa do uzupełnienia			PT			INSTALACJE SANITARNE (IS)		
INWESTOR								
do uzupełnienia)								
OBIEKT / NAZWA ZAMIERZENIA BUDOWLANEGO								
Budynek mieszkalny jednorodzinny wolnostojący „Dom LAMELA”								
ADRES / LOKALIZACJA (NR DZIAŁKI, OBRĘB, JEDN. EWIDENCYJNA)						KAT. OBIEKTU		
Lipowa (fikcyjna), dz. nr ewid. 123/4, obręb 0005 Przykładowo, gm. Przykładowo (fikcyjna)						I		
FUNKCJA		IMIĘ I NAZWISKO		SPECJALNOŚĆ, NR UPRAWNIENI		DATA		PODPIS
projektant		[DO UZUPEŁNIENIA]		[DO UZUPEŁNIENIA]				
projektant (wsp.)		[DO UZUPEŁNIENIA]		[DO UZUPEŁNIENIA]				
sprawdzający		nie dotyczy (art. 20 ust. 3 pkt 2 PB)		—				
opracował		[DO UZUPEŁNIENIA]		[DO UZUPEŁNIENIA]				
TYTUŁ RYSUNKU								
KANALIZACJA SANITARNA — RZUTY I PIĘTRA I II PIĘTRA								
SKALA		FORMAT	DATA WYDANIA	RODZAJ DOK.	NR RYSUNKU		ARKUSZ	REW.
1:50		1130×297	2026-09-25	rzut instalacji	PT-IS-04		4/11	0