

WENTYLACJA MECHANICZNA — RZUT PARTERU 1:50

OZNACZENIA — LEGENDA SYMBOLI

Oznaczenia instalacji sanitarnych — praktyka branżowa (PN-B-01410, PN-B-01411, PN-B-01430 — normy wycofane, bez następcy); armatura i urządzenia wg PN-EN ISO 10628-2 / PN-EN ISO 14617; rodzaje powietrza wg PN-EN 16798-3 (ODA, SUP, ETA, EHA). Obowiązuje legenda na arkuszu.


	podkład architektoniczny (rzut AR — ściany przecięte, stolarka, wyposażenie) — linie cienie szare		nawiewnik (anemostat/zawór nawiewny) — N, wydatek [m³/h], średnica przyłącza
	SUP — powietrze nawiewane (kanały okrągłe, izolowane w przestrzeniach nieogrzewanych)		wywiewnik (zawór wywiewny) — W, wydatek [m³/h]
	ETA — powietrze wywiewane		pion wentylacyjny (kanał pionowy SUP/ETA)

STRUMIENIE POWIETRZA — P0 [m³/h]

Pom.	Nazwa	Nawiew	Wywiew
0.03	WC gościnne	—	30
0.05	Spiżarnia	—	15
0.06	Salon + jadalnia + kuchnia	90	50
0.09	Łazienka gościnna (natrysk)	—	50
0.10	Pokój gościnny / gabinet	40	—
0.12	Pomieszczenie techniczne	—	15

OBJAŚNIENIA I UWAGI

- Średnice przewodów w mm (d. z'x's — rury wielowarstwowe, Ø/DN — kanalizacja, kanały wentylacyjne), przekroje żył w mm², odległości i rzędne w m; ±0.000 = 101.650 m n.p.m. (PL-EVRF-2007-NH).
- Rysunki instalacji na podkładzie rzutów architektury (PB-AR); podkład — linie cienie szare (warstwy I-PODKŁAD*).
- Wentylacja mechaniczna nawiewno-wywiewna z odzyskiem ciepła wg WT § 147–150 i PN-EN 16798-3 (oznaczenia ODA/SUP/ETA/EHA); strumienie powietrza z bilansu wentylacji (lamela.obliczenia.energia.wentylacja, PN-B-03430/Az3 powołana w WT § 149) — nawiew do pokoi, wywiew z kuchni, łazienek, WC, pralni, spiżarni.
- Średnice kanałów dobrane dla $v \leq 2,5$ m/s (przyłacza) i $\leq 3,5$ m/s (pnie); kanały okrągłe stalowe ocynkowane (typu spiro) lub system rozdzielaczy z przewodami elastycznymi (lub równoważne), z tłumikami akustycznymi za centralą; przepływ powietrza między pomieszczeniami przez podcięcie drzwi ≥ 1 cm (przepływ transferowy).
- Trasy kanałów i lokalizację pionu wyznaczono algorytmicznie (ortogonalnie, w przestrzeni sufitów podwieszanych/stropów) — do koordynacji z konstrukcją i architekturą (sufity SUF_GK).
- Kanały ODA i EHA w obrębie budynku — izolacja paroszczelna ≥ 50 mm; kanały SUP/ETA w przestrzeniach nieogrzewanych — izolacja ≥ 50 mm. Okap kuchenny — z recyrkulacją (filtr węglowy).
- Bilans na rysunkach: Σ nawiew = 365 m³/h, Σ wywiew = 365 m³/h — strumienie = max(model, bilans modułu energii: strumienie z modelu ("pomieszczenia[].went") — sprawdzone: minima, bilans ± 10 %, 20 m³/h-os.); nastawy regulacyjne nawiewników wyrównać do bilansu zrównoważonego przy rozruchu (PN-EN 12599).
- Rysunek wygenerowany automatycznie z modelu model/budynek.yaml (wersja 1.0, 2026-09-25) — generatory lamela.views.

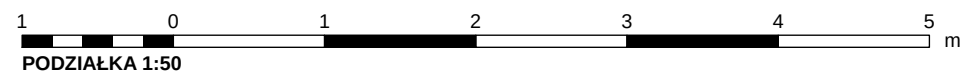

REW.	OPIS ZMIANY		DATA			
0	Wydanie — rysunek wygenerowany z modelu		2026-09-25			
PRACOWNIA PROJEKTOWA PRACOWNIA PROJEKTOWA — nazwa do uzupełnienia adres pracowni do uzupełnienia		STADIUM PT	BRANŻA INSTALACJE SANITARNE (IS)			
INWESTOR (do uzupełnienia)						
OBIEKT / NAZWA ZAMIERZENIA BUDOWLANEGO Budynek mieszkalny jednorodzinny wolnostojący „Dom LAMELA”						
ADRES / LOKALIZACJA (NR DZIAŁKI, OBRĘB, JEDN. EWIDENCYJNA) ul. Lipowa (fikcyjna), dz. nr ewid. 123/4, obręb 0005 Przykładowo, gm. Przykładowo (fikcyjna)			KAT. OBIEKTU I			
FUNKCJA	IMIĘ I NAZWISKO	SPECJALNOŚĆ, NR UPRAWNIENI	DATA	PODPIS		
Projektant	[DO UZUPEŁNIENIA]	[DO UZUPEŁNIENIA]				
Projektant (wsp.)	[DO UZUPEŁNIENIA]	[DO UZUPEŁNIENIA]				
Sprawdzający	nie dotyczy (art. 20 ust. 3 pkt 2 PB)	—				
Opracował	[DO UZUPEŁNIENIA]	[DO UZUPEŁNIENIA]				
TYTUŁ RYSUNKU WENTYLACJA MECHANICZNA — RZUT PARTERU						
SKALA 1:50	FORMAT 594x450	DATA WYDANIA 2026-09-25	RODZAJ DOK. rzut instalacji	NR RYSUNKU PT-IS-08	ARKUSZ 8/11	REW. 0