



odcinek kontroli 100 mm (rysunek 1.1)

A
B
C
D
E
F

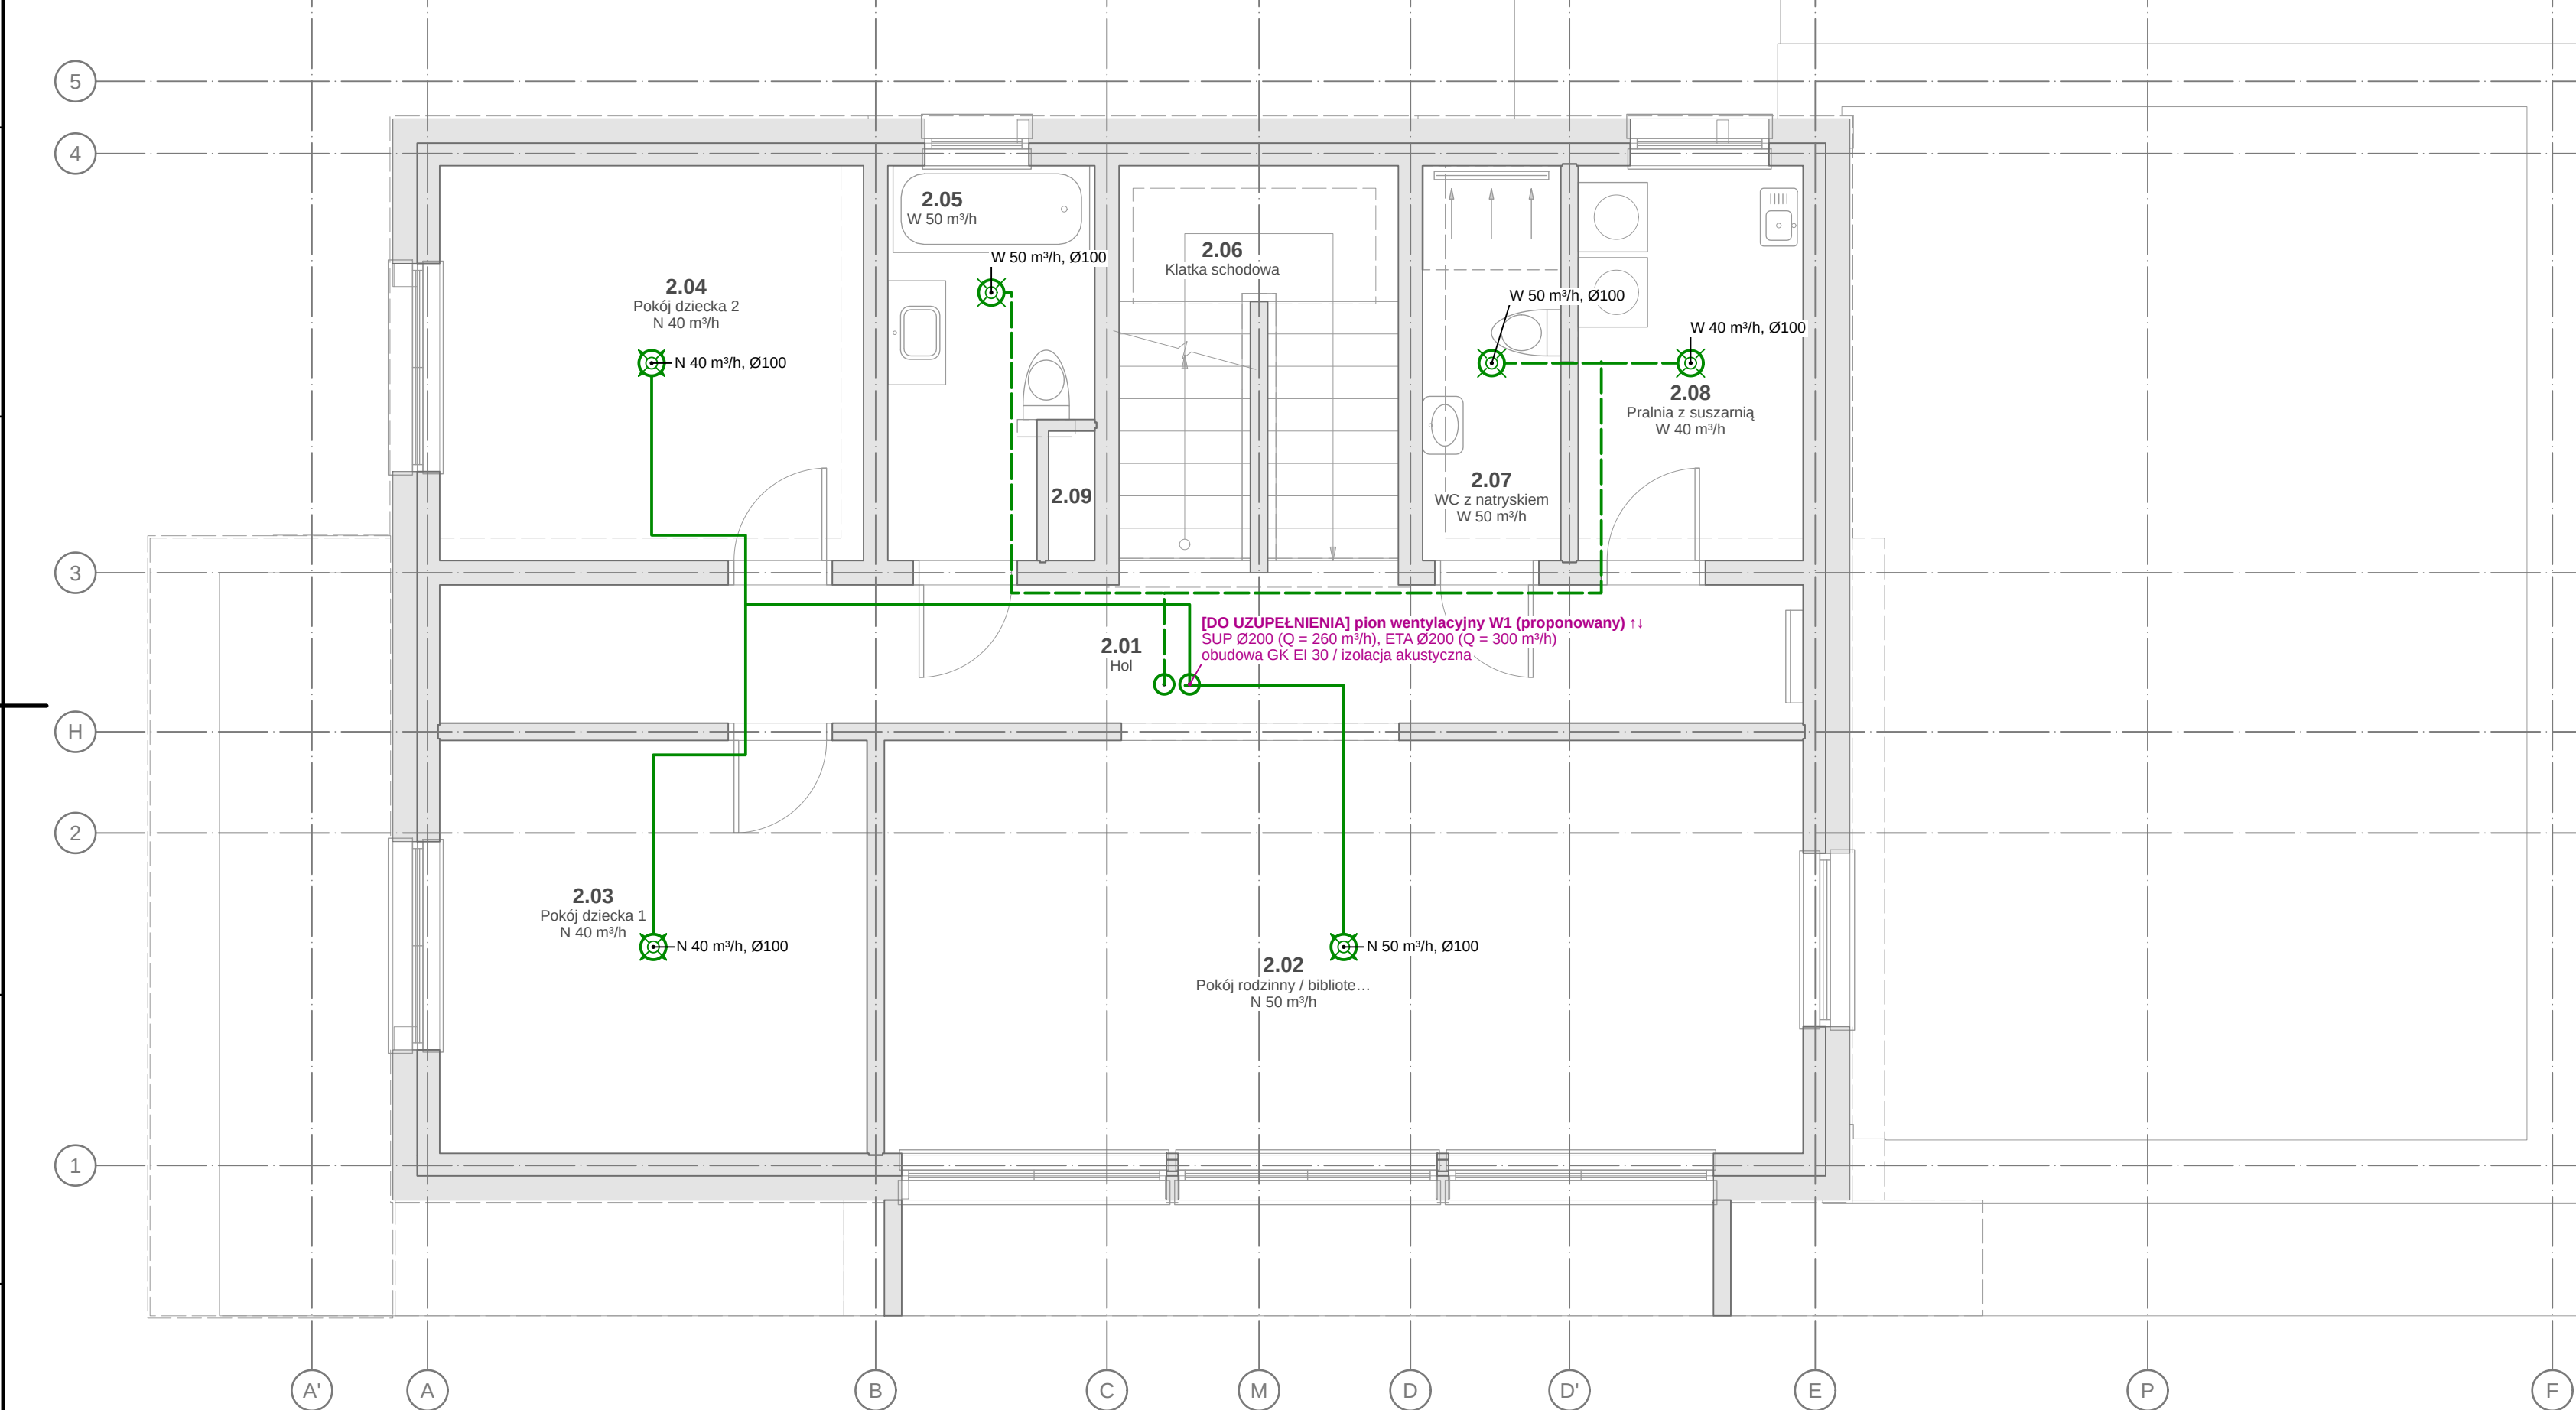

WENTYLACJA MECHANICZNA — RZUT I PIĘTRA 1:50

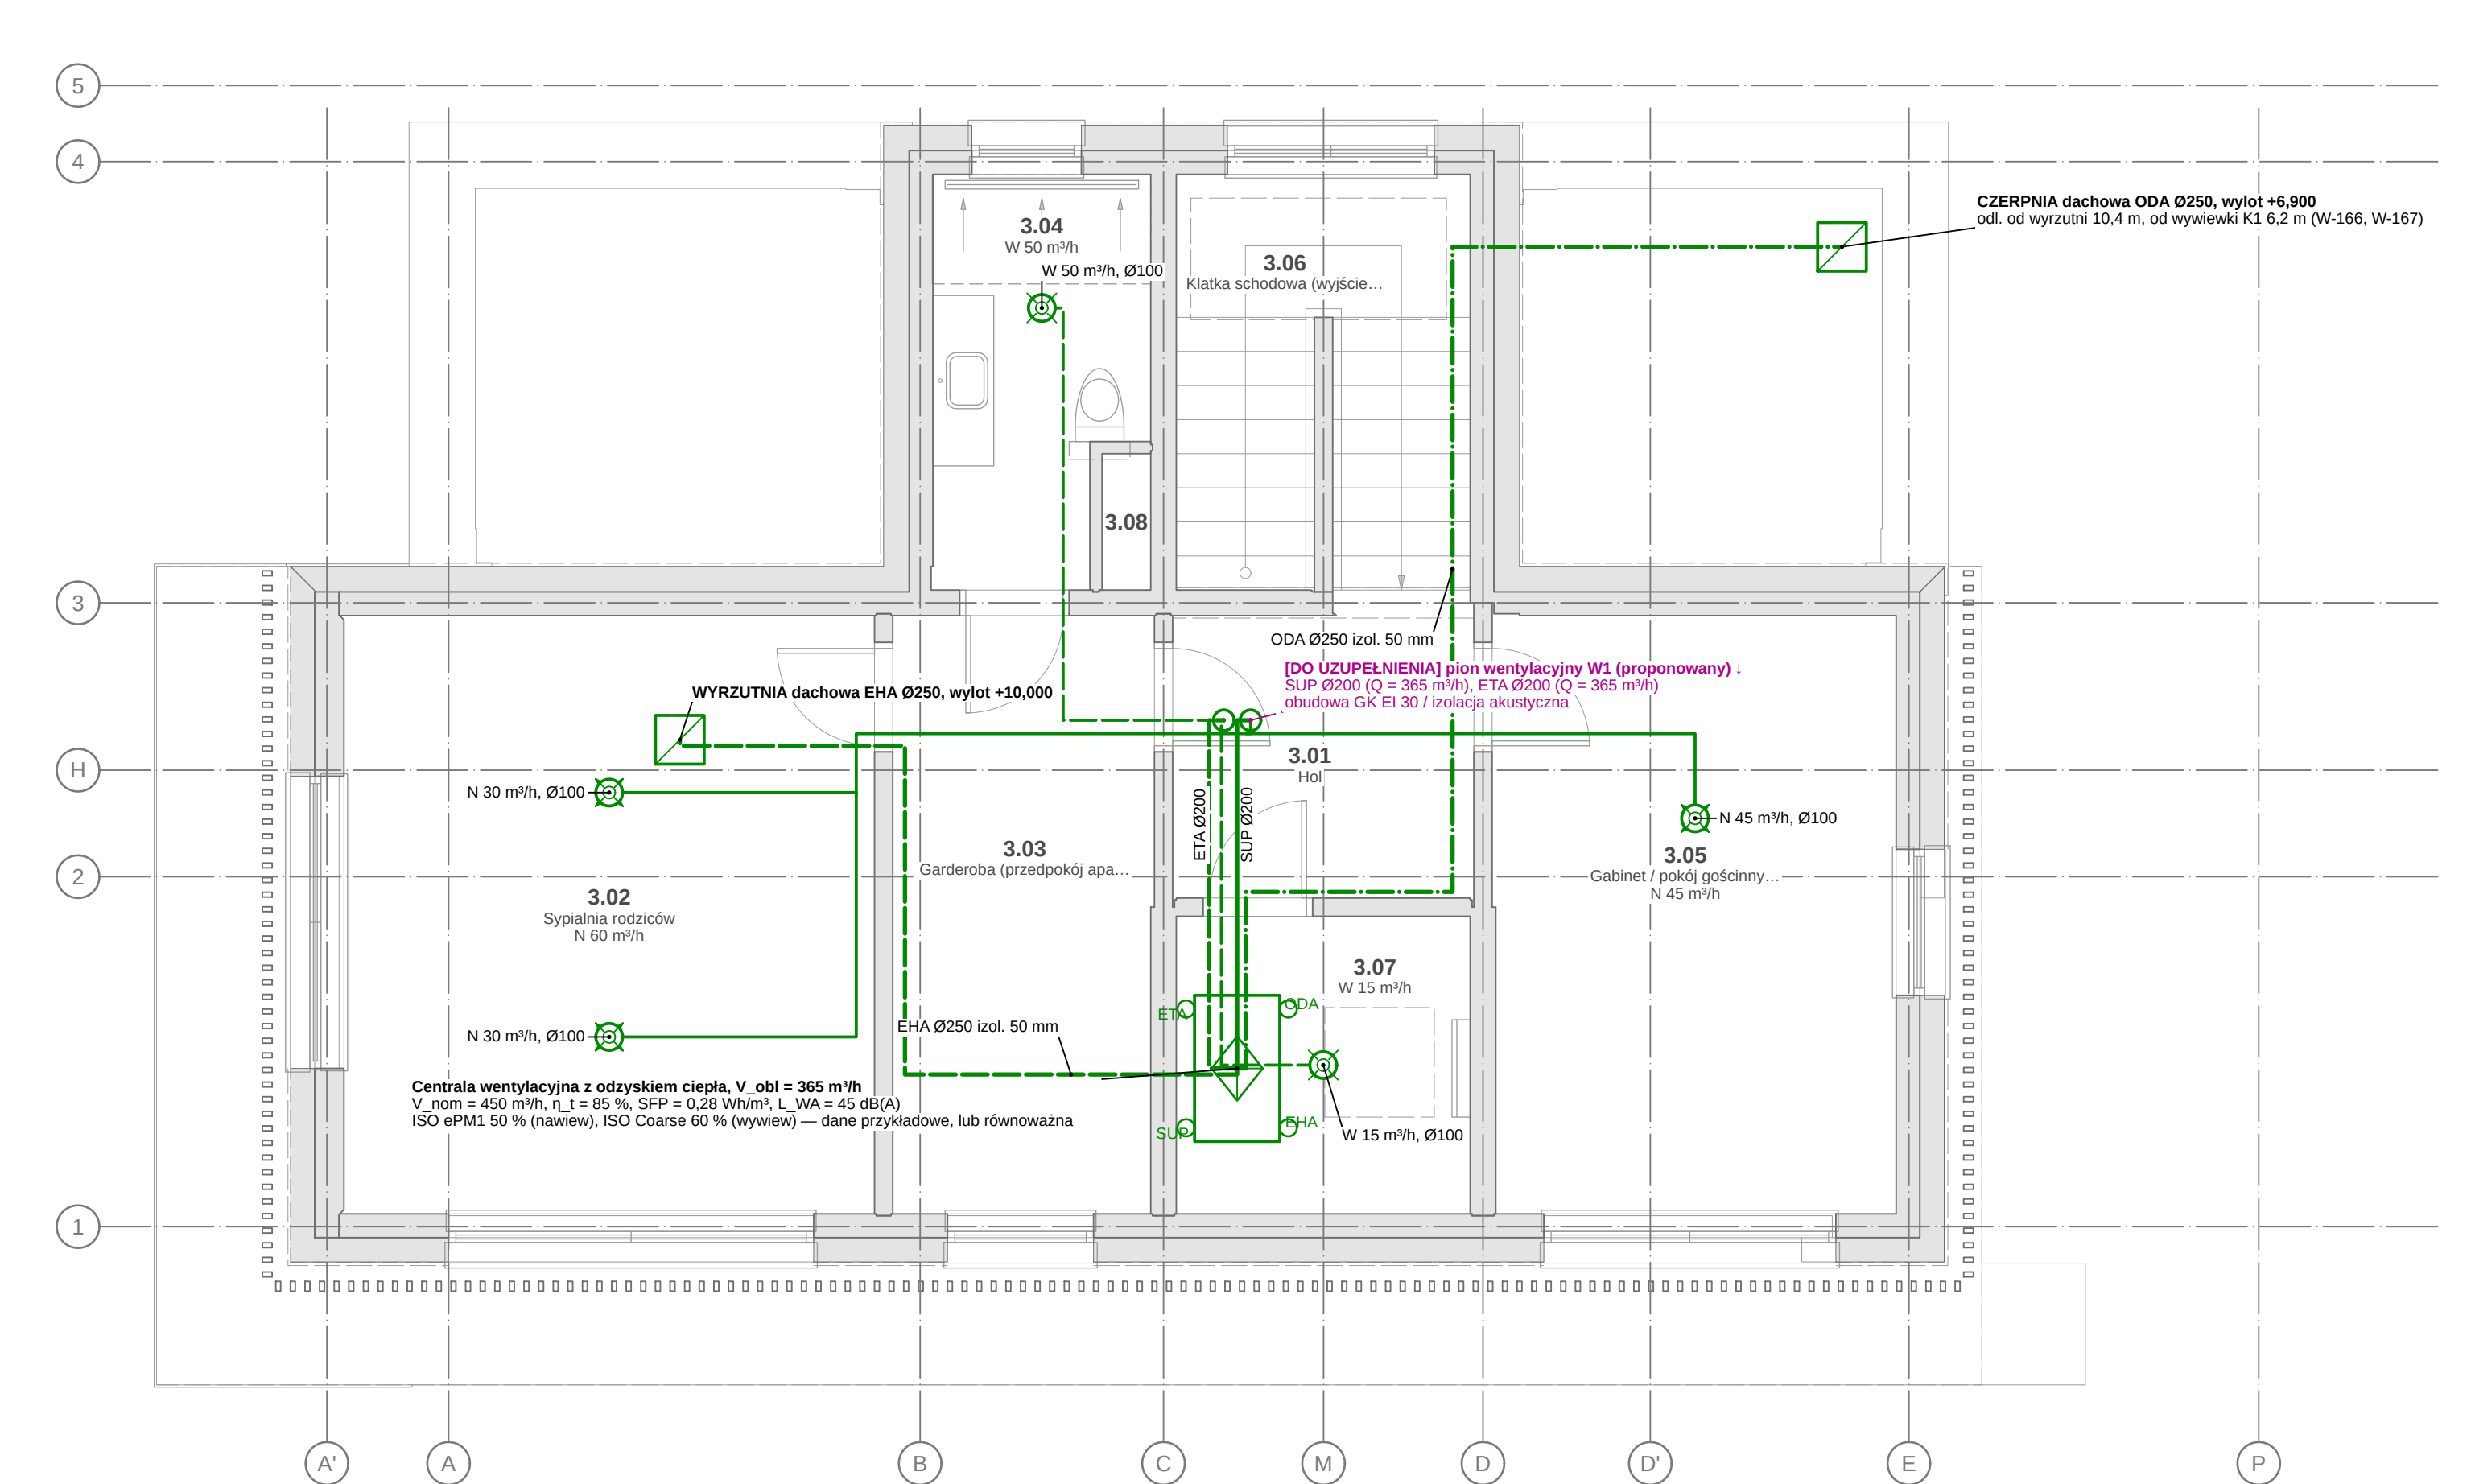

WENTYLACJA MECHANICZNA — RZUT II PIĘTRA 1:50

OZNACZENIA — LEGENDA SYMBOLI

- Oznaczenia instalacji sanitarnych — praktyka branżowa (PN-B-01410, PN-B-01411, PN-B-01430 — normy wycofane, bez następcy); armatura i urządzenia wg PN-EN ISO 10628-2 / PN-EN ISO 14617; rodzaje powietrza wg PN-EN 16798-3 (ODA, SUP, ETA, EHA). Obowiązuje legenda na arkuszu.
- podkład architektoniczny (rzut AR — ściany przecięte, stolarka, wyposażenie) — linie cienie szare
 - SUP — powietrze nawiewane (kanały okrągłe, izolowane w przestrzeniach nieogrzewanych)
 - ETA — powietrze wywiewane
 - nawiewnik (anemostat/zawór nawiewny) — N, wydatek [m³/h], średnica przyłącza
 - wywiewnik (zawór wywiewny) — W, wydatek [m³/h] pion wentylacyjny (kanał pionowy SUP/ETA)
 - ODA — powietrze zewnętrzne (czerpane), EHA — wyrzutowe; kanały izolowane paroszczelnie
 - centrała wentylacyjna z odzyskiem ciepła (króćce ODA / EHA / ETA / SUP wg PN-EN 16798-3)

STRUMIENIE POWIETRZA — P1 [m³/h]



Pom.	Nazwa	Nawiew	Wywiew
1.02	Pokój rodzinny / biblioteka (b)	50	—
1.03	Pokój dziecka 1	40	—
1.04	Pokój dziecka 2	40	—
1.05	Łazienka dzieci (wanna)	—	50
1.07	WC z natryskiem	—	50
1.08	Pralnia z suszarnią	—	40

STRUMIENIE POWIETRZA — P2 [m³/h]

Pom.	Nazwa	Nawiew	Wywiew
2.02	Sypialnia rodziców	60	—
2.04	Łazienka rodziców	—	50
2.05	Gabinet / pokój gościnny okazj	45	—
2.07	Pom. techniczne (centrała reku)	—	15

OBJAŚNIENIA I UWAGI

- Średnice przewodów w mm (d, z x s — rury wielowarstwowe, Ø/DN — kanalizacja, kanały wentylacyjne), przekroje żył w mm², odległości i rzędne w m; ±0,000 = 101,650 m n.p.m. (PL-EVRF2007-NH).
- Rysunki instalacji na podkładzie rzutów architektury (PB-AR); podkład — linie cienie szare (warstwy I-PODKŁAD*).
- Wentylacja mechaniczna nawiewno-wywiewna z odzyskiem ciepła wg WT § 147–150 i PN-EN 16798-3 (oznaczenia ODA/SUP/ETA/EHA); strumienie powietrza z bilansu wentylacji (lamela obliczenia energia wentylacja, PN-B-03430/AZ3 powołana w WT § 149) — nawiew do pokoi, wywiew z kuchni, łazienek, WC, pralni, sypialni.
- Średnice kanałów dobrane dla $v \leq 2,5$ m/s (przyłącza) i $\leq 3,5$ m/s (pnie); kanały okrągłe stalowe ocynkowane (typu spiro) lub system rozdzielaczy z przewodami elastycznymi (lub równoważne), z tłumikami akustycznymi za centralą; przepływ powietrza między pomieszczeniami przez podcięcie drzwi ≥ 1 cm (przepływ transferowy).
- Trasy kanałów i lokalizację pionu wyznaczono algorytmicznie (ortogonalnie, w przestrzeni sufitów podwieszanych/stropów) — do koordynacji z konstrukcją i architekturą (sufity SUF_GK).
- Kanały ODA i EHA w obrebie budynku — izolacja paroszczelna ≥ 50 mm; kanały SUP/ETA w przestrzeniach nieogrzewanych — izolacja ≥ 50 mm. Okap kuchenny — z recykulacją (filtr węglowy).
- Bilans na rysunkach: z nawiewu = 365 m³/h, z wywiewu = 365 m³/h — strumienie = max(model, bilans modułu energii; strumienie z modelu (pomieszczenia) went) — sprawdzone: minima, bilans ± 10 %, 20 m³/h-os.; nastawy regulacyjne nawiewników wyrównać do bilansu zrównoważonego przy rozruchu (PN-EN 12599).
- Rysunek wygenerowany automatycznie z modelu model/budynki.yam (wersja 1.0, 2026-09-25) — generatory lamela.views.

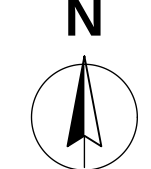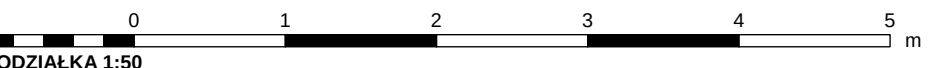

OPIS ZMIANY			DATA	
Wydanie — rysunek wygenerowany z modelu			2026-09-25	
COWNIA PROJEKTOWA ACOWNIA PROJEKTOWA — nazwa do uzupełnienia		STADIUM PT	BRANŻA INSTALACJE SANITARNE (IS)	
s pracowni do uzupełnienia				
ESTOR uzupełnienia)				
EKT / NAZWA ZAMIERZENIA BUDOWLANEGO				
dynek mieszkalny jednorodzinny wolnostojący „Dom LAMELA”				
RES / LOKALIZACJA (NR DZIAŁKI, OBRĘB, JEDN. EWIDENCYJNA)				KAT. OBIEKTU
ipowa (fikcyjna), dz. nr ewid. 123/4, obręb 0005 Przykładowo, gm. Przykładowo (fikcyjna)				I
FUNKCJA	IMIĘ I NAZWISKO	SPECJALNOŚĆ, NR UPRAWNIEN	DATA	PODPIS
ektant	[DO UZUPEŁNIENIA]	[DO UZUPEŁNIENIA]		
ektant (wsp.)	[DO UZUPEŁNIENIA]	[DO UZUPEŁNIENIA]		
wdzający	nie dotyczy (art. 20 ust. 3 pkt 2 PB)	—		
acował	[DO UZUPEŁNIENIA]	[DO UZUPEŁNIENIA]		
UL RYSUNKU				
ENTYLACJA MECHANICZNA — RZUTY I PIĘTRA I II PIĘTRA				
LA	FORMAT	DATA WYDANIA	RODZAJ DOK.	NR RYSUNKU
1:50	1310×297	2026-09-25	rzut instalacji	PT-IS-09
ARKUSZ	REW.			
9/11	0			