

Gniazda i zasilanie urządzeń — rzut parteru 1:50

Obwody na arkuszu (lamela.obliczenia.elektryka.obwody)

Obw.	Odbiorniki	Zab.	Przewód	L [m]	ΔU [%]	Faza	RCD
G1	Gniazda P0: 0.10 Pokój gościnny / gabinet, 0.08 Przedpokój gościnny, 0.14 Szacht instalacyjny SI, 0.04 Klatka schodowa, 0.16 Schowek pod spocznikiem (h < 1,40), 0.07 Pas komunikacyjny przy schodach, 0.05 Szpiarnia, 0.15 Schowek pod schodami (h 1,40–2,20), 0.02 Hol, 0.01 Wiatrołap, 0.11 Przedsiónek gospodarczy	B16	YDYp 3×2,5	5,6	1,02	L1	RCBO typ A 30 mA
G6	Gniazda kuchenne 1 (0.06 Salon + jadalnia + kuchnia)	B16	YDYp 3×2,5	15,8	2,21	L1	RCBO typ A 30 mA
G7	Gniazda kuchenne 2 (0.06 Salon + jadalnia + kuchnia)	B16	YDYp 3×2,5	15,8	2,21	L3	RCBO typ A 30 mA
G9	Gniazda łazienki (0.09 Łazienka gościnna (natrysk))	B16	YDYp 3×4	23,2	1,99	L1	RCBO typ A 30 mA
G13	Gniazda garażu / pom. technicznego (IP44)	B16	YDYp 3×2,5	5,5	1,01	L2	RCBO typ A 30 mA
G14	Gniazda zewnętrzne (taras, ogród; IP44/IP54)	B16	YDYp 3×4	27,5	2,30	L3	RCBO typ A 30 mA
D1	Płyta indukcyjna	3P B16	YDYp 5×2,5	11,3	0,80	3f	RCD 4P 40 A/30 mA typ A
D2	Piekarnik	B16	YDYp 3×2,5	15,8	2,11	L2	RCBO typ A 30 mA
D3	Zmywarka	B16	YDYp 3×2,5	8,0	0,90	L3	RCBO typ A 30 mA
D6	Pompa ciepła — jednostka zewnętrzna (PC-R290-07 (przykład))	C16	YDYp 3×2,5	9,4	1,15	L1	RCD typ F/B 30 mA wg DTR
D7	Grzałka rezerwowa PC / zasobnika c.w.u. (6,0 kW)	3P B10	YDYp 5×2,5	6,6	0,57	3f	RCD 4P 40 A/30 mA typ A
D8	Sterowanie PC, pompy obiegowe, listwy ogrzewania podłogowego	B10	YDYp 3×1,5	6,6	0,47	L3	RCBO typ A 30 mA
D10	Falownik PV 3f (6,0 kW AC)	3P B16	YDYp 5×2,5	3,0	0,46	3f	RCD typ B 30 mA
D11	Ładowarka EV 11 kW (3f) — garaż; przewód na 22 kW	3P C20	YDY 5×6	9,6	0,59	3f	własny RCD typ B 30 mA lub A-EV + RDC-DD 6 mA DC
D12	Napęd bramy garażowej	B10	YDYp 3×1,5	13,4	0,57	L3	RCBO typ A 30 mA
D13	Brama wjazdowa, furtka, wideodomofon (linia ogrodzenia)	B16	YKY 3×2,5	23,2	0,70	L3	RCBO typ A 30 mA
D14	Teletechnika: ONT, router, szafka RACK, SSWiN	B16	YDYp 3×2,5	3,0	0,39	L2	RCBO typ A 30 mA
D15	Pompa zbiornika wody deszczowej (podlewanie)	B16	YKY 3×2,5	25,7	0,95	L1	RCBO typ A 30 mA
D16	Napędy osłon przeciwslonecznych (19 szt.)	B10	YDYp 3×1,5	3,0	0,66	L2	RCBO typ A 30 mA

Oznaczenia — Legenda symboli

Symbol instalacji elektrycznych wg IEC 60617 (baza IEC; PN-EN 60617 — wycofana, stosowana jako praktyka branżowa) i PN-EN ISO 14617; oznaczenia teletechniczne — praktyka branżowa. Obowiązuje legenda na arkuszu.

- podkład architektoniczny (rzut AR — ściany przecięte, stolarka, wyposażenie) — linie cienkie szare

—

przewody obwodów gniazd YDYp 3×2,5 (5×2,5 — 3f) — połączenia punktów (przebieg schematyczny w tynku / w posadzce)



gniazdo wtyczkowe podwójne ze stykiem ochronnym, h = 0,30 m (kuchnia nad blatem 1,10 m)

gniazdo brygoszczelne IP44 (łazienki h = 1,20 m, garaż, pom. techniczne, zewnętrzne)
- wypust / puszka przyłączeniowa urządzenia zasilanego na stałe (opis: obwód, urządzenie, moc)
- M

M — zasilanie napędu osłony przeciwslonecznej (żaluzja/screen) przy oknie
- RG — rozdzielnica główna (PN-EN IEC 61439-3)

Objaśnienia i uwagi

- Srednice przewodów w mm (d, z×s — rury wielowarstwowe, Ø/DN — kanalizacja, kanały wentylacyjne), przekroje żył w mm², odległości i rzędne w m; ±0,000 = 101,650 m n.p.m. (PL-EVRF2007-NH).
- Rysunki instalacji na podkładzie rzutów architektury (PB-AR); podkład — linie cienkie szare (warstwy I-Podkład).
- Instalacja gniazd wtyczkowych i zasilania urządzeń wg PN-HD 60364-4-41 (samoczynne wyłączenie, RCD 30 mA dla gniazd ≤ 32 A — p. 411.3.3), PN-HD 60364-5-52 (przewody), PN-HD 60364-7-701 (łazienki), PN-HD 60364-7-722 (ładowanie EV); WT § 180–188 (obwody gniazd oddzielne od oświetlenia, gniazda ze stykiem ochronnym).
- Bilans mocy (lamela.obliczenia.elektryka.bilans): P_inst = 71,3 kW, P_szczyt z DLM = 24,8 kW ≤ P_przył = 27 kW, zabezpieczenie przedlicznikowe 40 A.
- Liczbę i rozmieszczenie gniazd wyznaczono algorytmicznie (praktyka branżowa, DIN 18015-2): przy łóżkach, biurkach, sofach, nad blatem kuchennym co ok. 1,1 m, przy umywalkach (poza strefami 0–2), pozostałe równomiernie wzdłuż ścian bez otworów; urządzenia stałe — wypusty/gniazda dedykowane wg obwodów D.
- Wysokości montażu (od posadzki): gniazda 0,30 m; nad blatem 1,10 m; łazienki 1,20 m (IP44); garaż, pom. techniczne 1,10 m (IP44); łączniki 1,10 m.
- Rysunek wygenerowany automatycznie z modelu model/budynke.yaml (wersja 1.0, 2026-09-25) — generatory lamela.views.

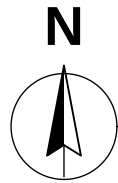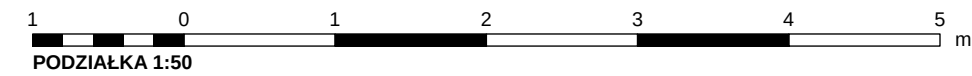

REW.	OPIS ZMIANY			DATA		
0	Wydanie — rysunek wygenerowany z modelu			2026-09-25		
PRACOWNIA PROJEKTOWA PRACOWNIA PROJEKTOWA — nazwa do uzupełnienia adres pracowni do uzupełnienia			STADIUM PT	BRANŻA INSTALACJE ELEKTRYCZNE (IE)		
INWESTOR (do uzupełnienia)						
OBIEKT / NAZWA ZAMIERZENIA BUDOWLANEGO Budynek mieszkalny jednorodzinny wolnostojący „Dom LAMELA”						
ADRES / LOKALIZACJA (NR DZIAŁKI, OBRĘB, JEDN. EWIDENCYJNA) ul. Lipowa (fikcyjna), dz. nr ewid. 123/4, obręb 0005 Przykładowo, gm. Przykładowo (fikcyjna)				KAT. OBIEKTU I		
FUNKCJA	IMIĘ I NAZWISKO		SPECJALNOŚĆ, NR UPRAWNIENI		DATA	PODPIS
Projektant	[DO UZUPEŁNIENIA]		[DO UZUPEŁNIENIA]			
Projektant (wsp.)	[DO UZUPEŁNIENIA]		[DO UZUPEŁNIENIA]			
Sprawdzający	nie dotyczy (art. 20 ust. 3 pkt 2 PB)		—			
Opracował	[DO UZUPEŁNIENIA]		[DO UZUPEŁNIENIA]			
TYTUŁ RYSUNKU GNIAZDA I ZASILANIE URZĄDZEŃ — RZUT PARTERU						
SKALA 1:50	FORMAT 594x500	DATA WYDANIA 2026-09-25	RODZAJ DOK. rzut instalacji	NR RYSUNKU PT-IE-04	ARKUSZ 4/14	REW. 0